


NOTE :
1. DOOR HINGES : GEZE MAKE.
2. DOOR CLOSER : GEZE MAKE.
3. DOOR PANIC BAR : YELE MAKE.

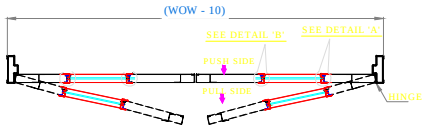

TOP VIEW

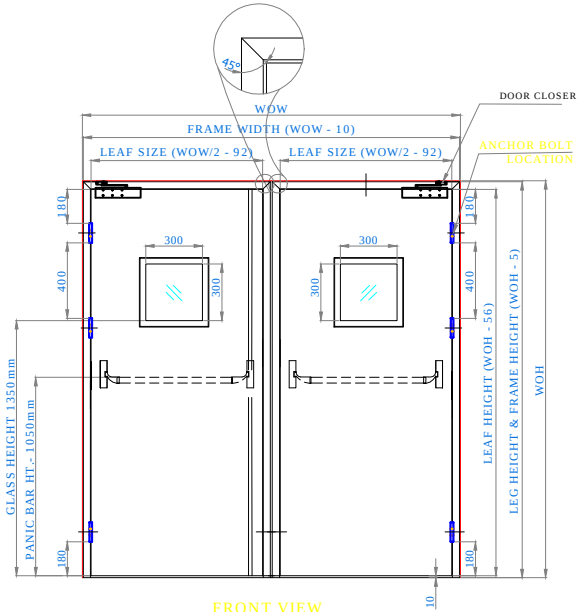


FRONT VIEW

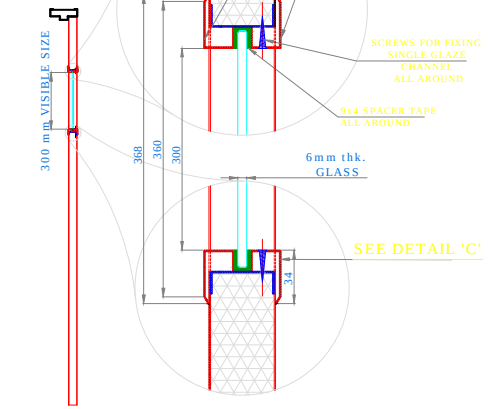

SIDE VIEW SECTION A-A'


SEE DETAIL 'C'

SINGLE GLAZE FIXING DETAIL

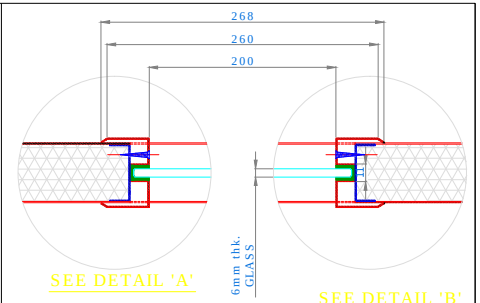



SEE DETAIL 'A'

SEE DETAIL 'B'

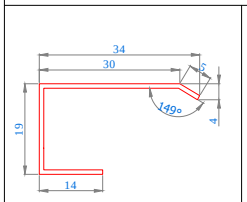


SEE DETAIL 'C'

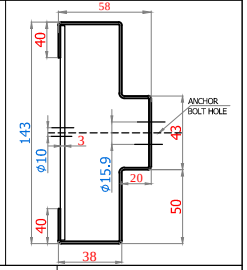

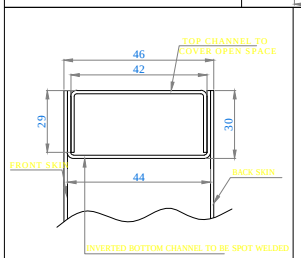

DOOR TOP SECTION DETAIL

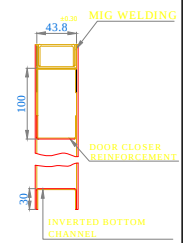

DOOR BOTTOM & TOP DETAIL

NOTE :
1. Up to 2 hours fire resistance in accordance with BS 476 part 22, UL 10B & UL 10C dependent on construction.
2. CORES : Honeycomb Paper.

SR. NO	WALL OPENING WIDTH	WALL OPENING HEIGHT	QTY	RAL	HARDWARE
01	1800	2400	02	9002	Double leaf metal door with glass vision panel , Panic bar inside , pull handle outside

TOLERANCE - ±05mm

This drawing & design is the property of NIHVA TECHNOLOGIES. Not to be sold or copied to any other concern.

TITLE: DOUBLE LEAF FIRERATED STEEL DOOR

NIHVA TECHNOLOGIES PVT. LTD. PUNE
Tel : 020 66304033
Email:- info@nihva.com
Website:- www.nihva.com

	NAME	SIGN	DATE
DRAWN	P.V.A		25.03.2019
CHECK	V.M.T		25.03.2019
APPRD.			

CLIENT - UNITED ARCHITECT
PROJECT - A RAYMOND
SITE LOCATION - CHAKAN, PUNE.
If any queries contact : design@nihva.com
DWG. NO. : NIHVA/18-19/0311 REV- 0
ALL DIMENSION ARE IN mm
SCALE: NTS WT: SHEET: 01 OF 01