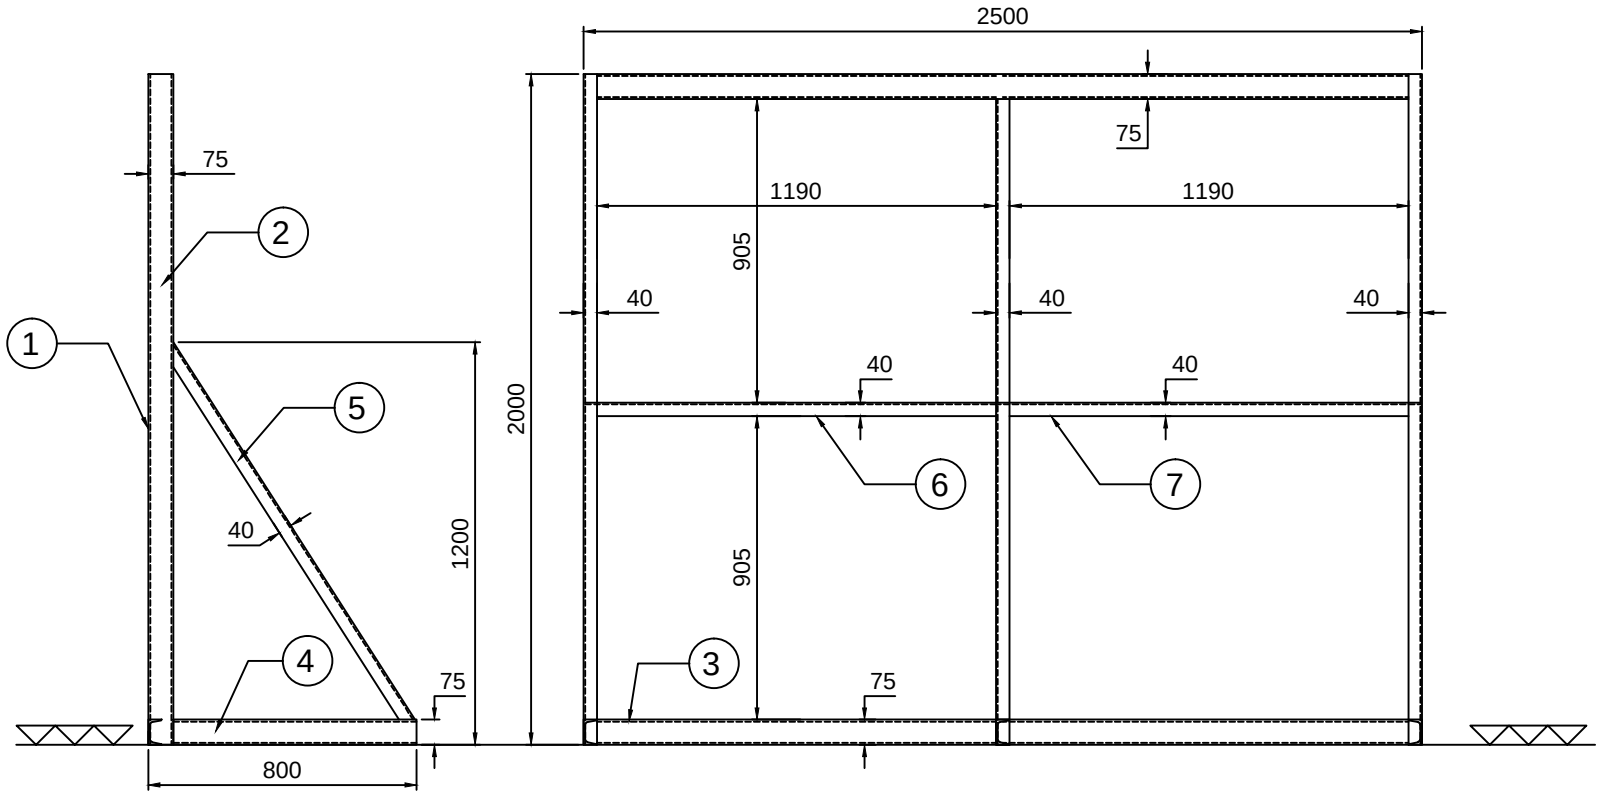

BARRICADE QTY : 300 NOS

SR. NO	SECTION	DESCRIPTION	QTY
07	ISA	40 X 40 X 5 X 1260L	1 NO
06	ISA	40 X 40 X 5 X 1225L	1 NO
05	ISA	40 X 40 X 5 X 1335L	3 NOS
04	ISMC	75 X 40 X 725L	3 NOS
03	ISMC	75 X 40 X 2500L	2 NOS
02	ISMC	75 X 40 X 1925L	3 NOS
01	PLAIN SHEET	2000 X 1.2 THK X 2500L	1 NO

This drawing & design is the property of NIHVA TECHNOLOGIES. Not to be sold or copied to any other concern.

TITLE: BARRICADE

NIHVA TECHNOLOGIES PVT. LTD.

NIHVA TECHNOLOGIES PVT. LTD. PUNE
Tel : 020 66304033
Email:- info@nihva.com
Website:- www.nihva.com

	NAME	SIGN	DATE
DRAWN	P.A		23.01.19
CHECK	A.K		23.01.19
APPRD.			

CLIENT -

PROJECT -

SITE LOCATION -

If any queries contact : design@nihva.com

DWG. NO. : NIHVA/18-19/VDR/364

ALL DIMENSION ARE IN mm

SCALE: NTS | WT: | REV- 00