


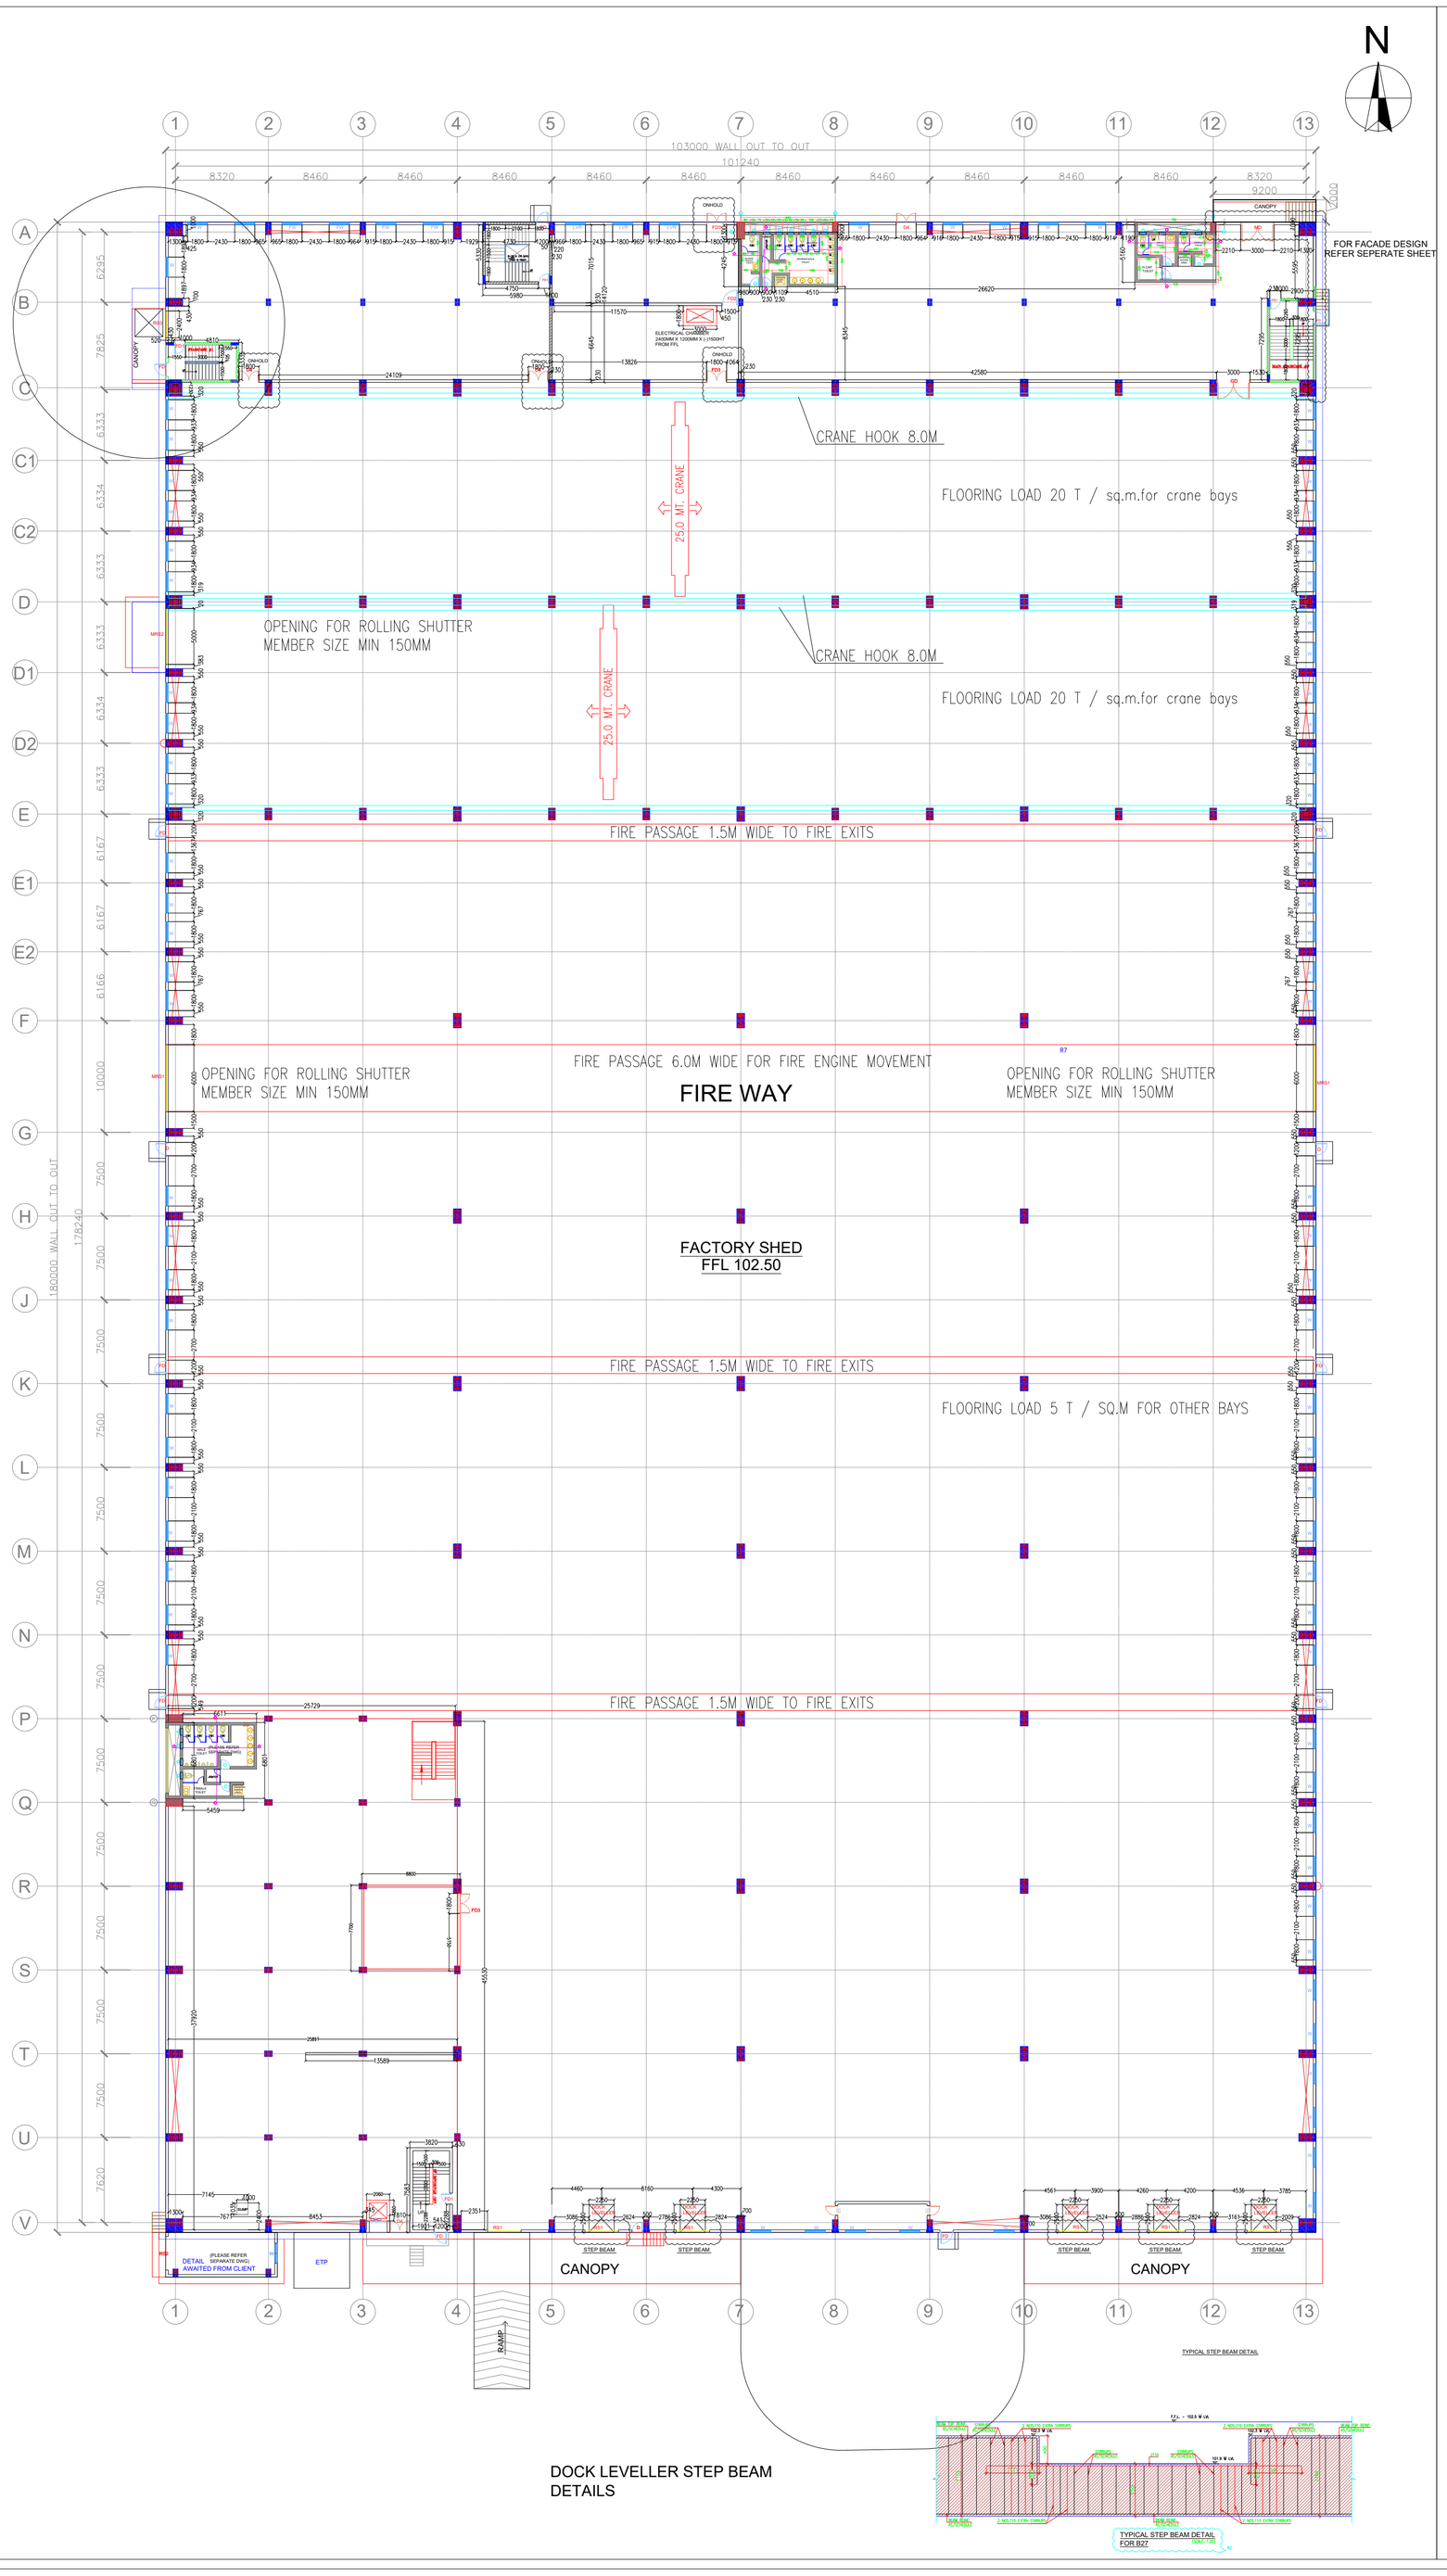

DOCK LEVELLER STEP BEAM DETAILS

NOTES:

- DO NOT SCALE THE DRAWING
- ONLY WRITTEN DIMENSIONS TO BE FOLLOWED
- ALL DIMENSIONS ARE IN MILLIMETERS
- ANY DISCREPANCY IS TO BE BOUGHT TO THE NOTICE OF OUR OFFICE
- THIS DRAWING IS TO BE READ IN CONJUNCTION WITH OTHER RELEVANT DRAWINGS
- IF IN DOUBT PLEASE ASK

OPENING SCHEDULE

FACTORY BUILDING

NAME	DESCRIPTION	SIZE
MRS1	ROLLING SHUTTER FOR FIREWAY	6000W X 6000H
MRS2	ROLLING SHUTTER FOR MACHINE ENTRY	5000W X 5000H
RS1	MANUALLY GEAR OPERATED ROLLING SHUTTER	3000W X 3500H
RS2	ROLLING SHUTTER FOR SYNC PANEL ROOM ENTRY MANUALLY GEAR OPERATED ROLLING SHUTTER	3000W X 3000H
RS3	ROLLING SHUTTER FOR SYNC RESIN ROOM ENTRY MANUALLY GEAR OPERATED ROLLING SHUTTER	2400W X 3000H
W	2 TRACK ALUMINIUM POWDERED SLIDING WINDOW COATED WHITE COLOURED	1800W X 1800H
FW	2 TRACK ALUMINIUM POWDERED FIXED WINDOW COATED WHITE COLOURED	1800W X 1800H
LVR	LOUVERS	1800W X 1800H
FD	SINGLE LEAF 2HR FIRE RATED DOOR WITH VISION PANEL, PANIC BAR FROM INSIDE	1200W X 2150H
FD1	SINGLE LEAF 2HR FIRE RATED DOOR WITH VISION PANEL, TRIM HANDLE FROM BOTH SIDES WITH LOCK	1000W X 2150H
FD2	SINGLE LEAF 2HR FIRE RATED DOOR WITH VISION PANEL, LEVELLER HANDLE FROM BOTH SIDES WITH LOCK	1500W X 2400H
FD3	DOUBLE LEAF 2HR FIRE RATED DOOR WITH PANIC BAR FROM INSIDE	1800W X 2150H
MD	DOUBLE LEAF GLASS DOOR WITH GLASS FACADE	3000W X 2400H
D	MS SINGLE LEAF DOOR WITH LOCK FROM OUTSIDE AND LEVELLER HANDLE FROM BOTH SIDES	1200W X 2150H
D1	FLUSH DOOR WITH LAMINATE FINISH	750W X 2150H
D2	FLUSH DOOR WITH LAMINATE FINISH	900W X 2150H
D3	FLUSH DOOR WITH LAMINATE FINISH	1100W X 2150H
D4	MS DOUBLE LEAF DOOR WITH LOCK FROM OUTSIDE AND LEVELLER HANDLE FROM BOTH SIDES	1800W X 2400H

