


Revision		Date	By
A	Side fastening was with side jamb	2021-11-11	KMÖ
B	Surface treatment for anchor bolt & note for hand crank	2021-11-17	KMÖ
C	Power supply was 400V/50Hz	2021-11-24	KMÖ

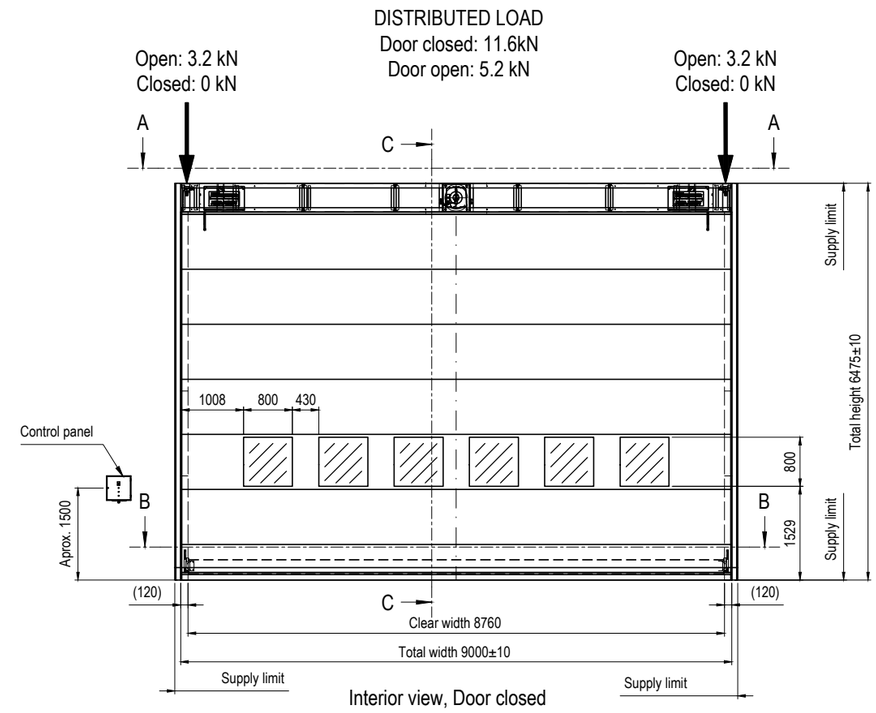

Interior view, Door closed

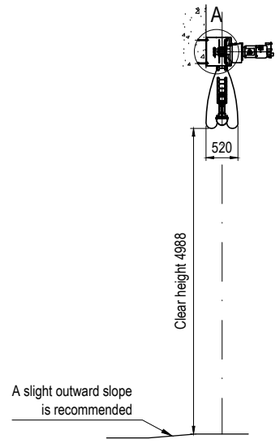

SECTION C-C
Open door
Scale 1:50

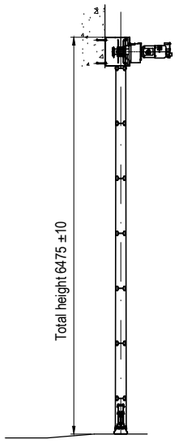

SECTION C-C
Closed door
Scale 1:50

NOT INCLUDED IN DOOR SUPPLY:

1. Design and supply of all door supporting structural components.
2. Design and supply of all closure between door and adjacent steel.
3. Door jambs adjustable for overall door width and true to plumb.
4. Paint job after completed door installation.
5. Any frameworks being provided by ASSA ABLOY will be clearly indicated as "by ASSA ABLOY".

REQUIREMENTS ON BUILDING:

6. Door head support must be straight within 1/600 of span in the in/out direction and free from protrusions of any kind.
7. For a single door leaf, door head support should be horizontal and straight within 1/600 of span at distributed full door load.
8. Door side jambs must be smooth, straight and parallel, out of plumb must not exceed 2mm/m (total deviation at full length 5 mm) in any direction.
9. Any footings at bottom of jamb columns must not interfere with installation of guide rails at floor level.
10. At time of installation, finished floor, free from obstructions, out to a distance of 2 m on each side of door centreline must be available.
11. Header box must be accessible from both sides during installation.


DOOR PROPERTIES:

12. The door is designed to withstand a differential pressure of 1.15kPa.
13. Guide rails, top- and intermediate beams in extruded aluminium with natural finish.
14. Color of header box: BLACK (NCS 9000-N. RAL 9005)
15. Color of door fabric: GREY (NCS 3500, RAL 7004)
16. Metal trim: motor side
17. Hand crank for manual operation


ELECTRICAL:

18. One main control panel provided of PLC type.
19. Audible and visual alarm
20. Back-up power switch
21. Safety edge
22. Approx. size of main control panel: WxHxD (500mm x 600mmx250 mm)
23. Power supply: 415V /50Hz
24. Power: 2.7kW
25. Nom. current: 6.2A
26. (max. allowed voltage drop at start: 5%)


BELT HOIST UNITS:
SK 873.1-100L/4 Z dual brake

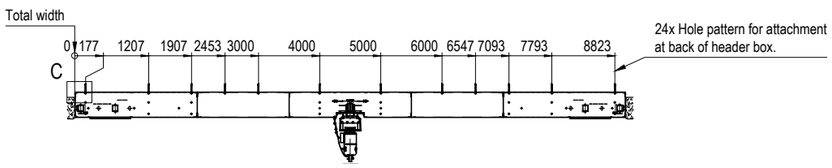


SECTION A-A
Scale 1:50

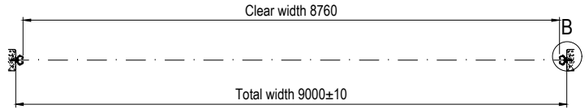


SECTION B-B
Door leaf is not shown for clarification
Scale 1:50

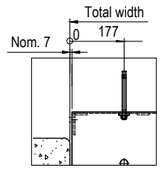


DETAIL C, SCALE (1:10)

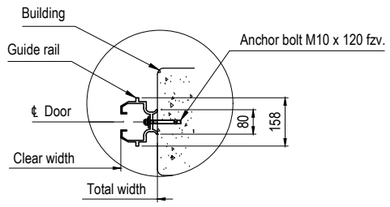


DETAIL B, SCALE (1:10)

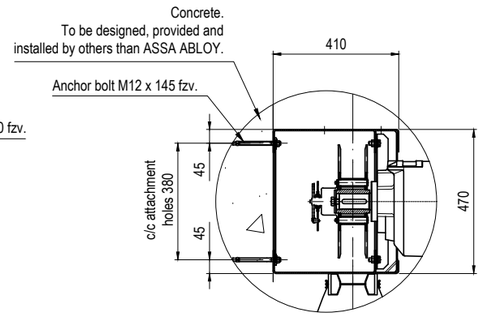

DETAIL A, SCALE (1:10)

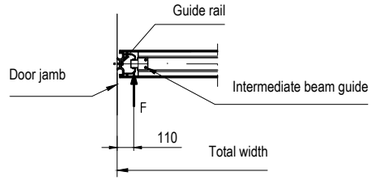

Force by differential pressure
transferred to guide rail at
each intermediate position.
F=4.7 kN

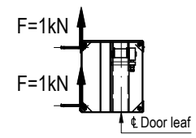

Load on header box attachment
(each screw), due to wind load
and door weight

Building: ARFF5

DESIGNED: KMÖ		SIZE: A1	SCALE: 1:50
CODE: 22240-22241	ITEM NO	If not otherwise stated: Tolerances ISO 2768-m EN ISO 13920-B	
DATE: 2021-07-22		Cutting class ISO 9013-442	
ASSA ABLOY		Weld class ISO 5817-C	
		Surface finish Smooth raw surface	

Delhi Fire Station
India
Megadoor 8760 x 4988
Sales interface

DRAWING NO: 74414
REVISION: C
PLOT DATE

This document is the property of ASSA ABLOY Entrance Systems AB and shall not be reproduced or handed over to a third party or used for any other unauthorized purpose.