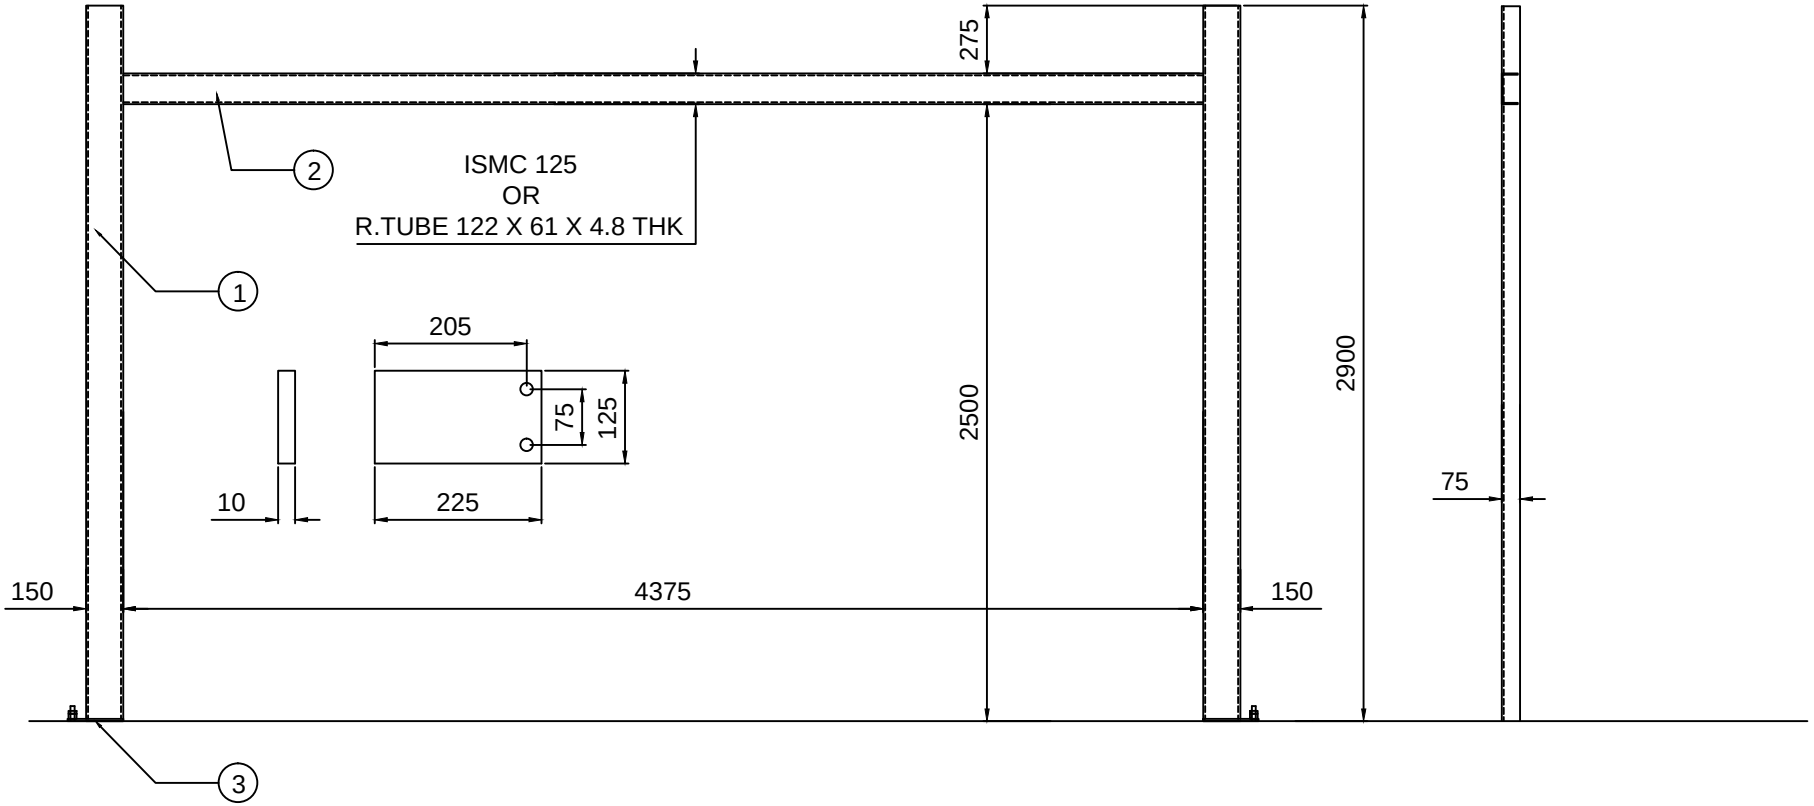

COLOR : SAME AS PER ROLLING SHUTTER

SR.NO	DESCRIPTION	SPECIFICATION	QTY
3	FLAT	150 X 10 X 225L	2 NOS
2	ISMC	125 X 65 X 4375L	1 NO
1	ISMC	150 X 75 X 2890L	2 NOS

This drawing & design is the property of NIHVA TECHNOLOGIES. Not to be sold or copied to any other concern.

TITLE
MOTORIZED GRILLED
ROLLING SHUTTER STRUCTURE

NIHVA
NIHVA TECHNOLOGIES PVT. LTD.

NIHVA TECHNOLOGIES
PVT. LTD. PUNE
Tel : 020 66304033
Email:- info@nihva.com
Website:- www.nihva.com

	NAME	SIGN	DATE
DRAWN	P.A		29.02.2020
CHECK	G.J		29.02.2020
APPRD.			

CLIENT -
PROJECT -
SITE LOCATION -
If any queries contact : design@nihva.com
DWG. NO. : NIHVA/19-20/VDR/355
REV- R00
ALL DIMENSION ARE IN mm
SCALE: NTS
WT:
SHEET: