



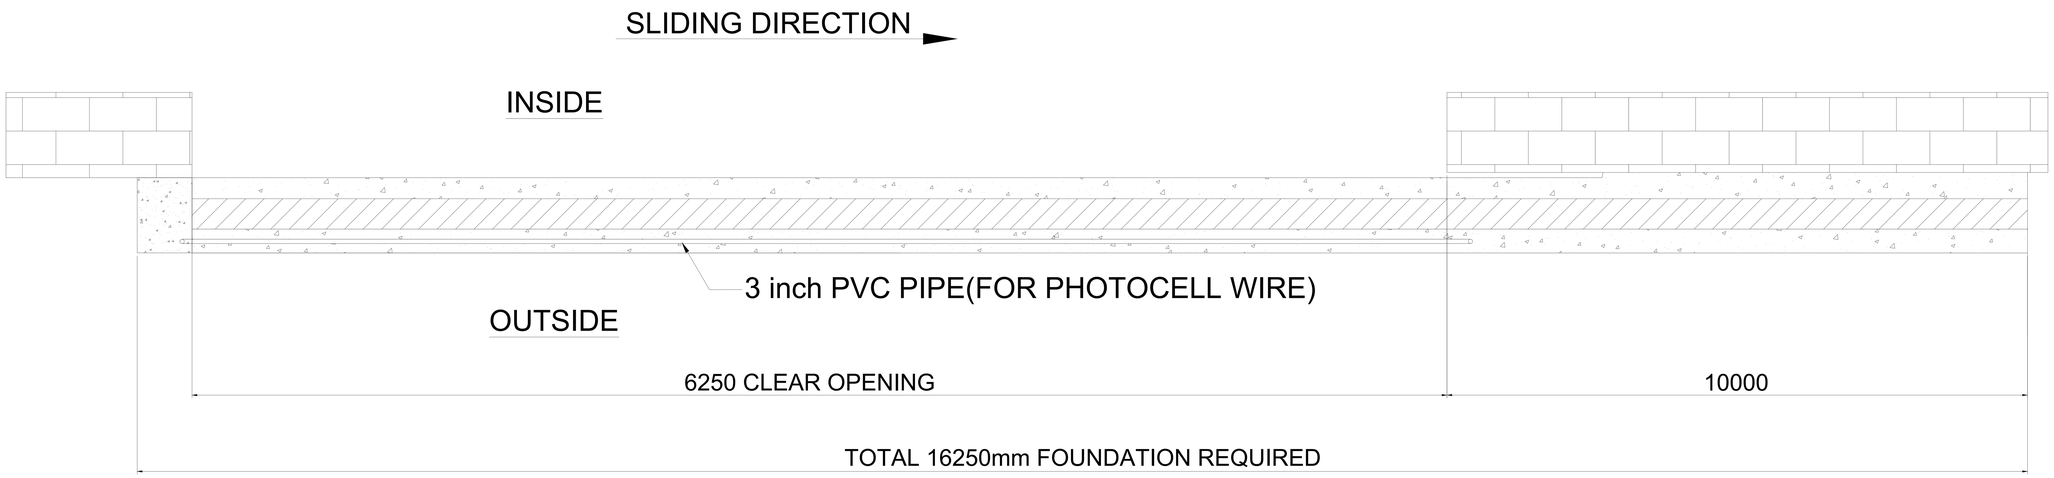

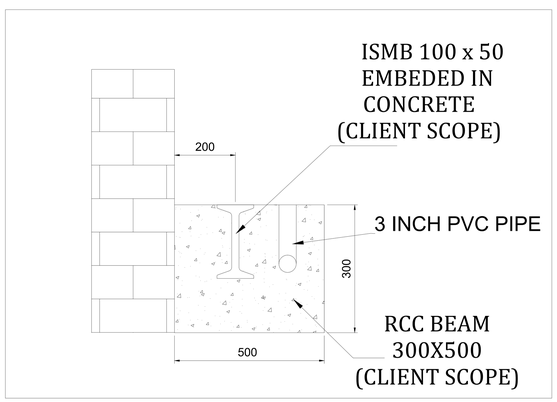

This drawing & designing is the property of NIHVA TECHNOLOGIES. Not to be sold or copied to any other concern.

TITLE
SLIDING GATE FOUNDATION DRAWING

	NAME	SIGN	DATE
DRAWN	P.V.A		31.07.19
CHECK	V.M.T		31.07.19
APPROVAL			

If any queries contact : design@nihva.com

ALL DIMENSION ARE IN mm

NIHVA
NIHVA TECHNOLOGIES PVT. LTD.
NIHVA TECHNOLOGIES PVT. LTD. PUNE
Tel : 020 66304033
Website:- www.nihva.com
Email:- info@nihva.com

CLIENT - OC SPECILITIES PVT LTD

PROJECT -

SITE LOCATION -

DWG. NO. : NIHVA/19-20/0068 REV.:- 0

SCALE: NTS WT: SHEET: 01 OF 01