
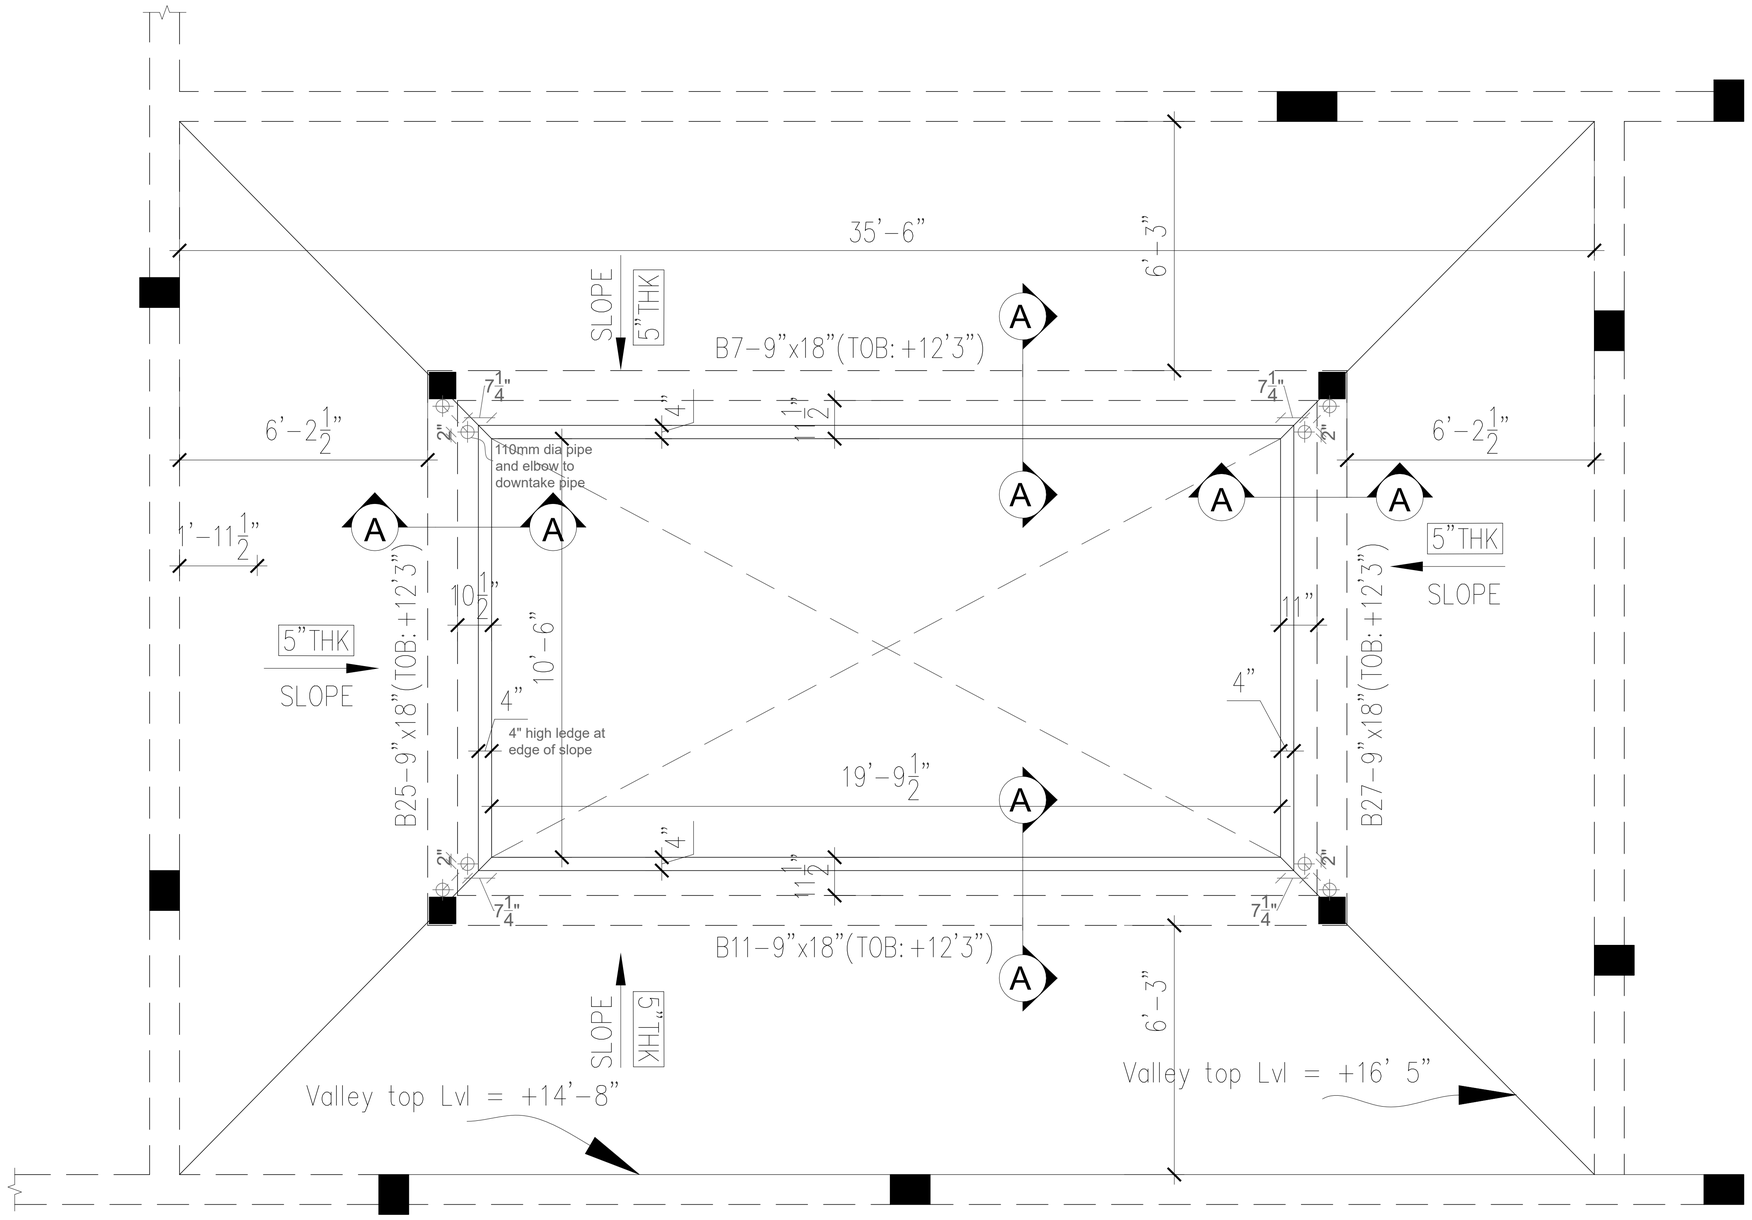


CENTER COURTYARD ROOF PLAN

(SCALE 1:50)

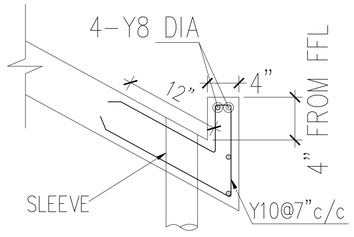

SECTON A-A

SCALE 1:33

BUILDING DIRECTION:

NOTES:

1. STRUCTURAL DRAWINGS SHALL BE READ IN CONJUNCTION WITH RELEVANT ARCHITECTURAL AND SERVICES DRAWINGS.
2. DO NOT SCALE THE DRAWING, FOLLOW WRITTEN DIMENSIONS ONLY.
3. ALL DIMENSIONS ARE IN Feet & inch. UNLESS OTHERWISE SPECIFIED.
4. ALL LEVEL SHOULD BE AS PER ARCHITECTURAL REQUIREMENT.
5. CLEAR COVER
   a) SLAB = 20mm d) BEAM = 25mm
   b) COLUMN = 40mm
6. CONCRETE MIX
   a) SLAB = M25 d) BEAM = M25
   b) COLUMN = M25
7. REINFORCEMENT :REINF. STEEL SHALL BE TMT BARS OF GRADE Fe500 CONFIRMING TO IS 1786-2008.
8. DETAILING OF REINFORCEMENT SHALL BE ACCORDING TO SP-34:1987 & IS-456:2000.
9. LAPPING & ANCHORAGE LENGTH TO BE CONSIDERED AS 50ø FOR FOOTINGS, COLUMNS, BEAMS & SLABS.
10. ANY DISCREPANCY FOUND IN THE DRAWING SHALL BE BROUGHT TO THE NOTICE OF THE ENGINEER/ARCHITECT BEFORE EXECUTION OF THE WORK.
11. THE BUILDING HAS BEEN DESIGNED FOR G.F ONLY
12. SBC OF SOIL IS 250 KN/M² @ 6 Feet FROM N.G.L

GOOD FOR CONSTRUCTION

Sign ..... Date .....

For EDECONS CONSULTANTS PVT. LTD.

NO.	DESCRIPTION	DATE	SIGN.
R0	FOR APPROVAL	26.10.2021	RAHUL

ISSUALS

NO.	DESCRIPTION	DATE	SIGN.
R0	-	26.10.2021	RAHUL

REVISION

PROJECT TITLE :

HIBA RESIDENCE
AT MANGALORE

PRINCIPAL ARCHITECTS:

design harmony
Sustainable Architecture I Interiors I Landscape
Lake View Farm
Siddhapura, Bengaluru - 560066
+919686669602 jaya@designharmony.in

STRUCTURAL CONSULTANTS :

EDECONS CONSULTANTS PVT LTD
(Engineering Designers Consortium)
690-T, 16th Main Road, 4th 'T' Block,
Jayanagar, Bangalore 560 041,
PH: 080 41121685
Email: edeconsc@gmail.com

FOR APPROVAL

DRAWING TITLE:

CENTER COURTYARD GUTTER DETAILS

DESIGN	RAHUL	CHECKED	SVS	SHEET SIZE: A4
DRAWN	RM	DATE	26.10.2021	
APPROVED	RS	SCALE	-	

DRAWING NO : ECPL-OI-DH-ST-07A

REV NO: R0