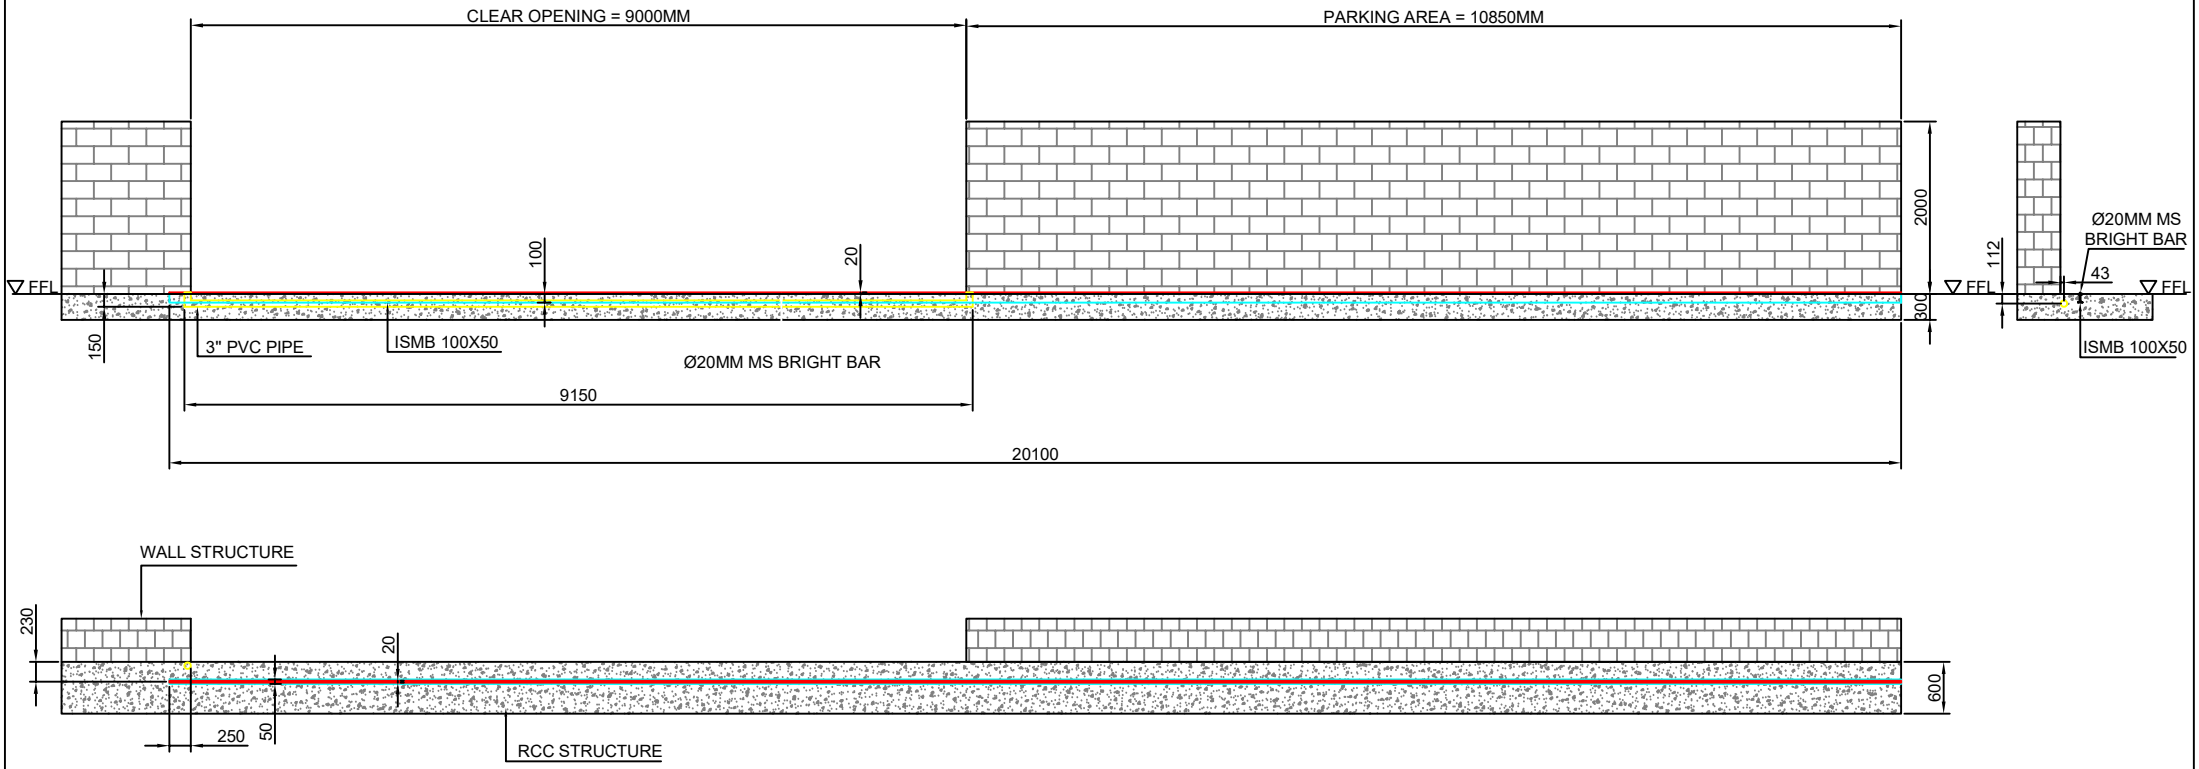


Technical Specs of Motorized Sliding Gate

1. Parking length required -10750+100mm
2. Bottom Rail - Bright bar Ø20mm
3. Total leaf weight ≈ Approx.1134kg
4. ISMB 100 X 50 positioned in the foundation.

Note-

1. All dimension are in mm.
2. All civil work is under client scope.
3. 3" PVC pipe in the foundation to be provided by client.
4. Power supply single phase 230v, 50hz. is in client scope.
5. Cable for power supply 2.5 sqmm 3 core
6. Cable for photocell - 1.5 sqmm 4 core

This drawing & design is the property of NIHVA TECHNOLOGIES. Not to be sold or copied to any other concern.

TITLE:- Foundation Drawing for Sliding Gate

	NAME	DATE	SIGN
DRAWN	SUJATA.B	22/10/2021	
CHECK	G.PATIL	22/10/2021	
APPRD.	A.KURHADE	22/10/2021	

If any queries contact : design@nihva.com

ALL DIMENSION ARE IN mm

NIHVA TECHNOLOGIES PVT. LTD.
NIHVA TECHNOLOGIES PVT. LTD. PUNE
Tel : 020 66304033
Email:- info@nihva.com
Website:- www.nihva.com

CLIENT - SCON PROJECTS


LOCATION -


PRODUCT - SLIDING GATE QTY:-

DWG NO:-NIHVA\21-22\0250 REV- 0

SCALE: NTS SCALE:-- 1:1 SHEET: 01 OF 01

Rev No.	Revision	Date	Revised By

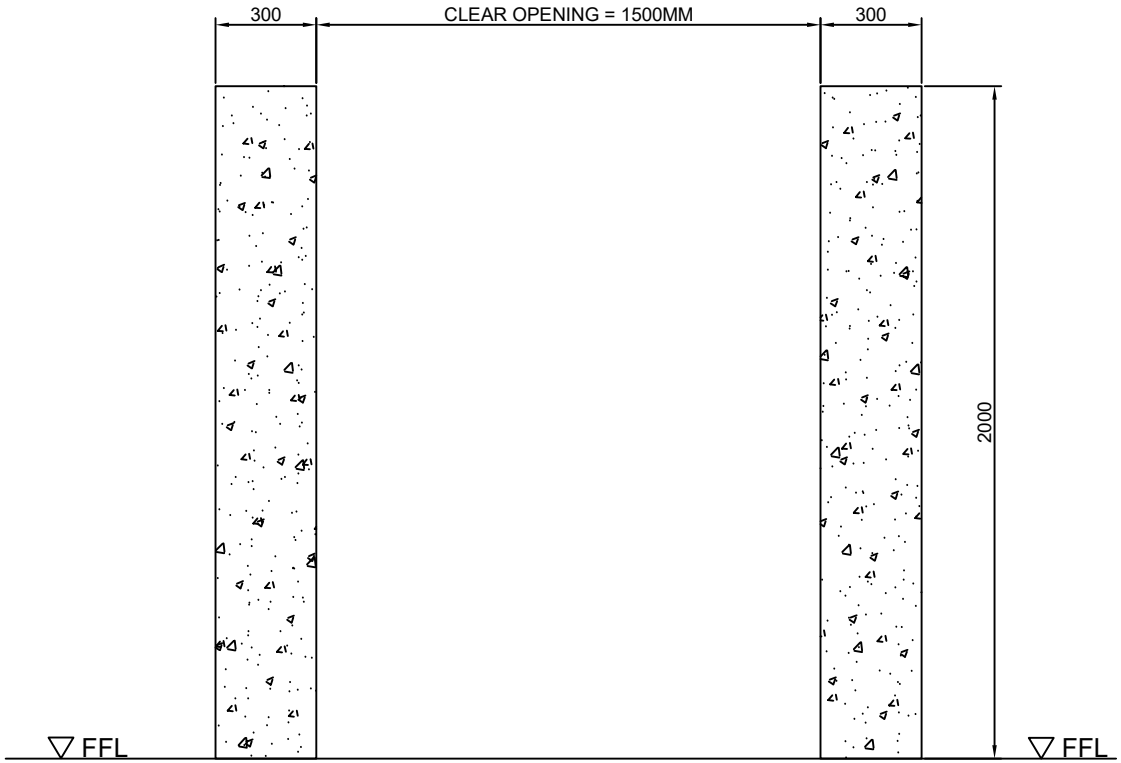

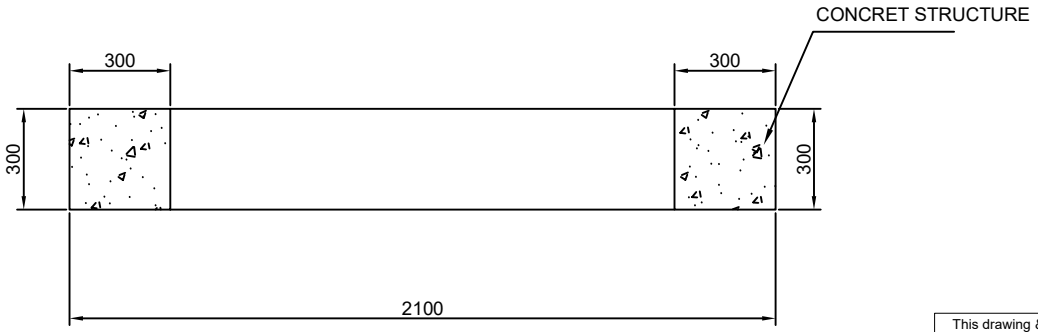

Technical Specs of Swing Gate

1. Total leaf weight ≈ Approx.196Kg

Note-

1. All dimension are in mm.
2. All civil work is under client scope.

This drawing & design is the property of NIHVA TECHNOLOGIES. Not to be sold or copied to any other concern.

TITLE:- WICKET GATE FOUNDATION DRAWING

NIHVA TECHNOLOGIES PVT. LTD.
NIHVA TECHNOLOGIES PVT. LTD. PUNE
Tel : 020 66304033
Email:- info@nihva.com
Website:- www.nihva.com

	NAME	DATE	SIGN
DRAWN	SUJATA.B	22/10/2021	
CHECK	G.PATIL	22/10/2021	
APPRD.	A.KURHADE	22/10/2021	

If any queries contact : design@nihva.com

ALL DIMENSION ARE IN mm

CLIENT - SCON PROJECT

LOCATION -

PRODUCT - WICKET GATE

DWG NO:-NIHVA\21-22\0251 | REV- 0

SCALE: NTS | SCALE:-- 1:1 | SHEET: 01 OF 01

Rev No.	Revision	Date	Revised By