


RETRACTABLE ROOF

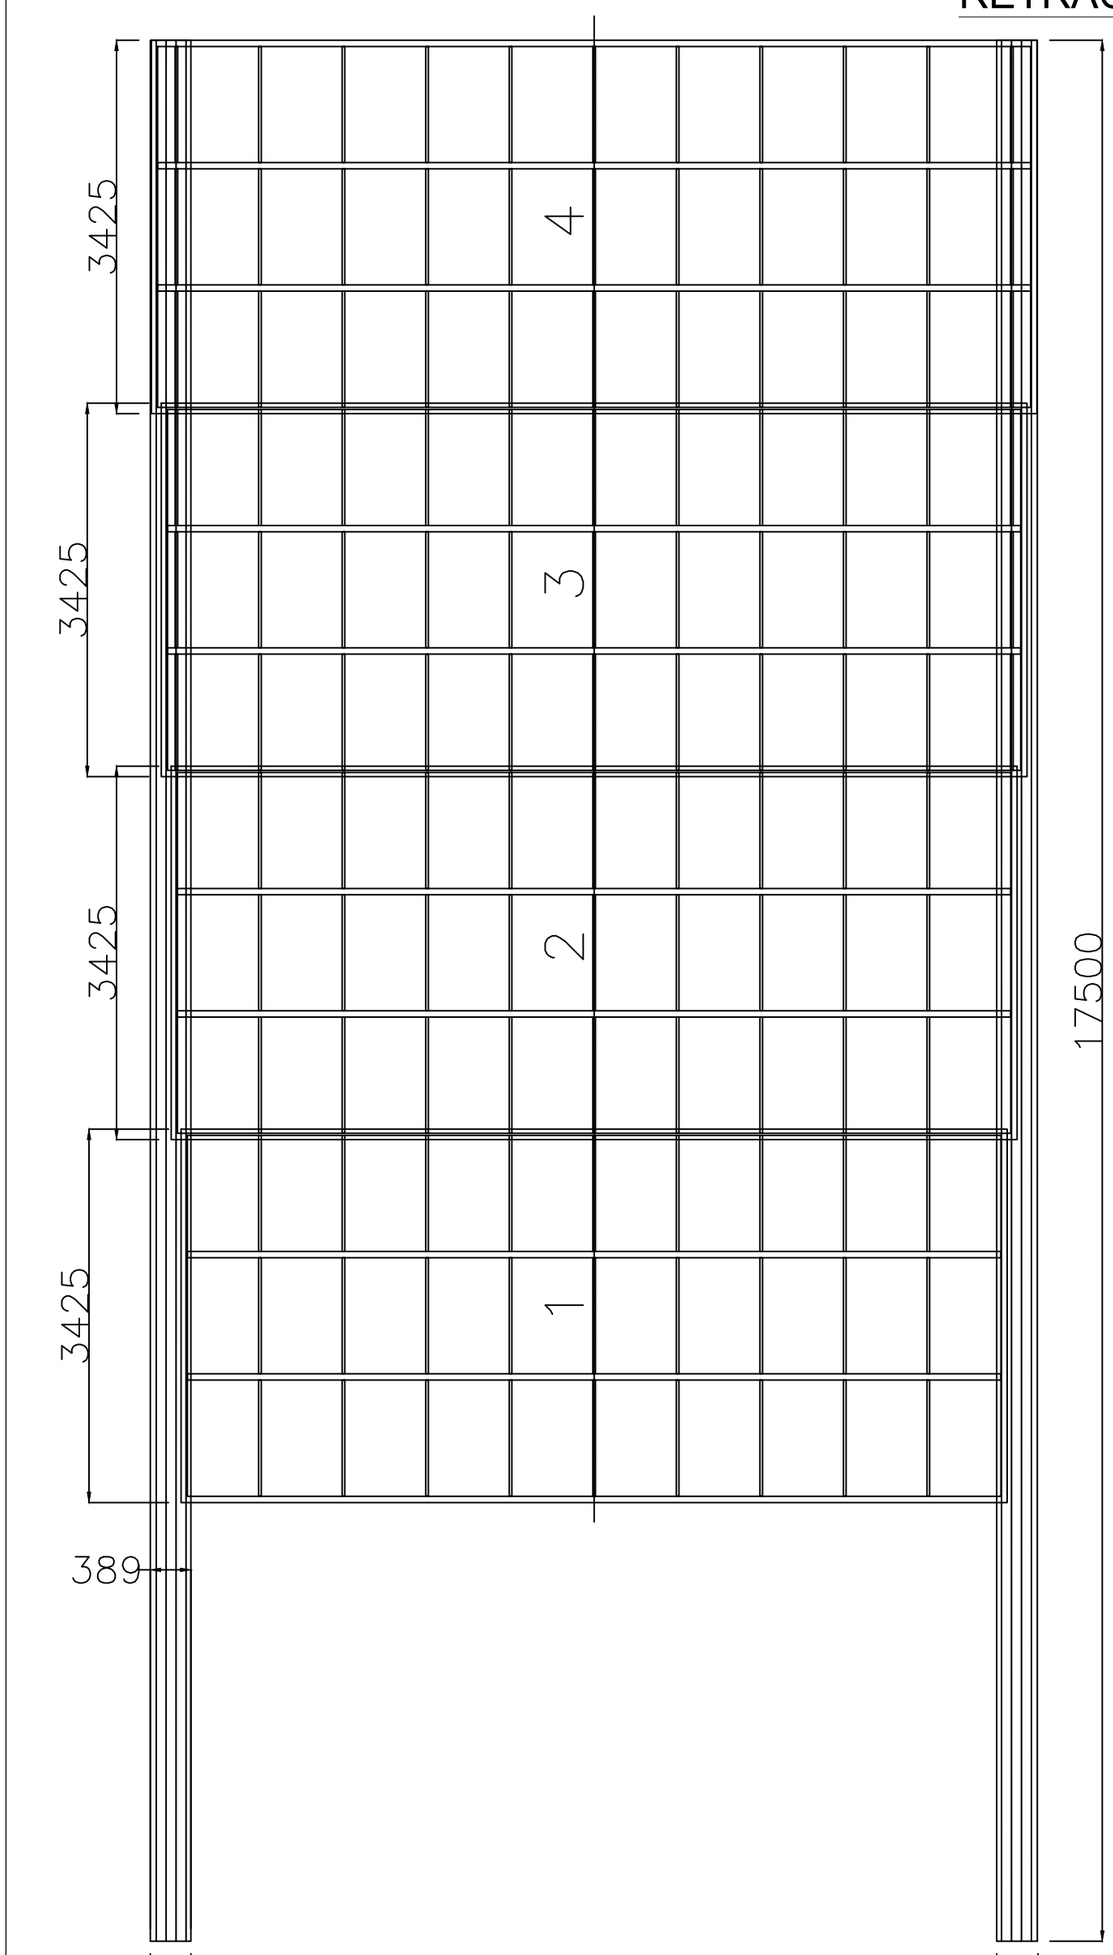

ENCLOSED PLAN

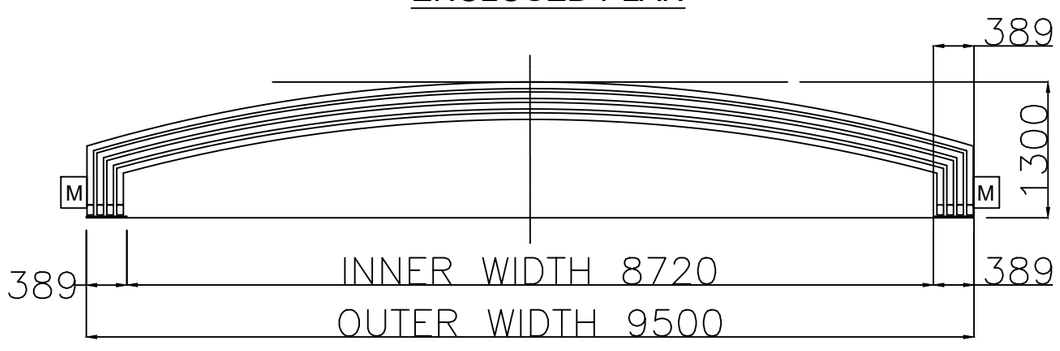

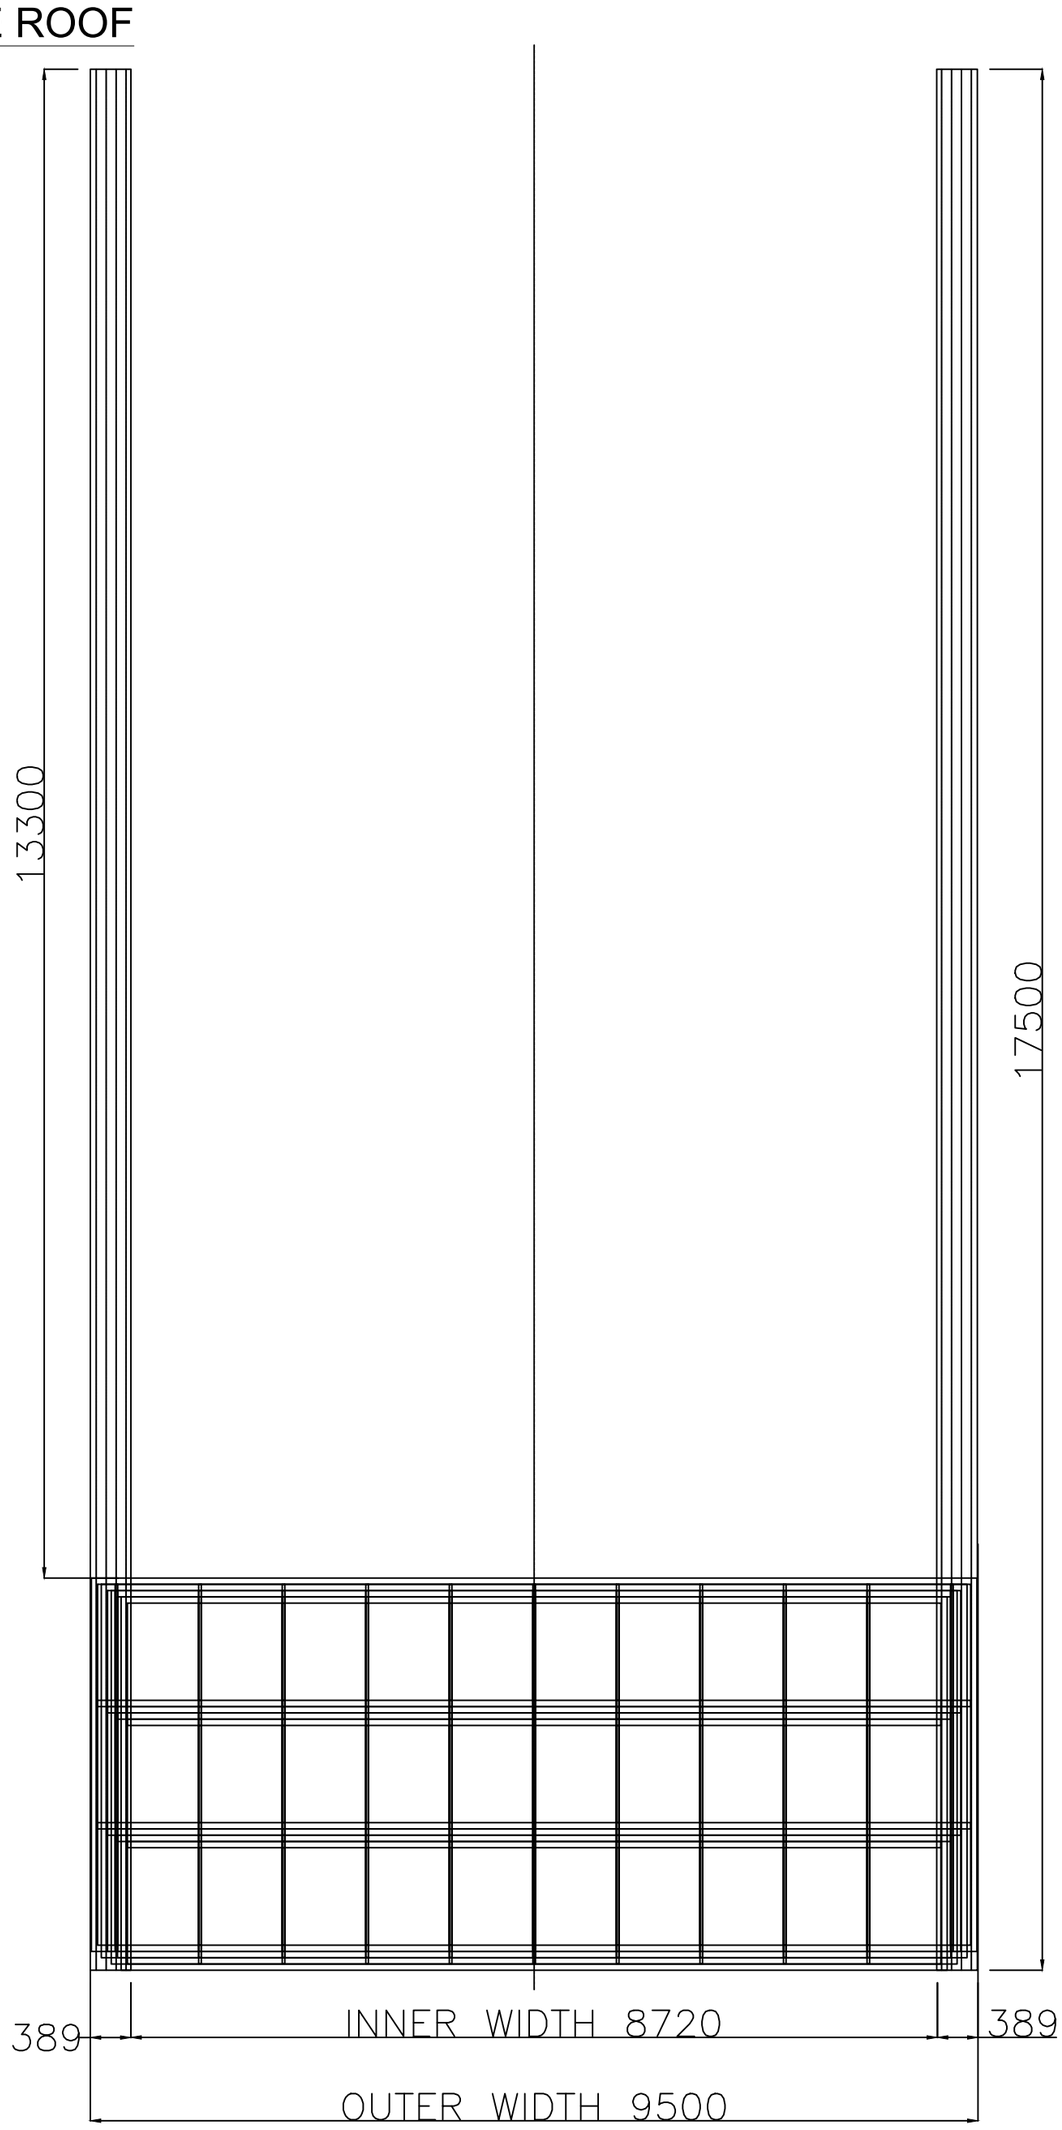

STACKED PLAN

REV.	DESCRIPTION.	REVISED BY	SIGN	DATE
002	REVISED GA DRAWING PER SINGLE SIDE OUT OF CLEAR OPENING	MAHESH S.		08.10.22
001	REVISED GA DRAWING PER BI-PARTING WITHIN CLEAR OPENING	MAHESH S.		06.10.22
000	RELEASED GA DWG FOR APPROVAL	GAURAV J.		20.08.22

This drawing & design is the property of NIHVA TECHNOLOGIES. Not to be sold or copied to any other concern.

TITLE
ROOF LAYOUT

NIHVA TECHNOLOGIES PVT. LTD.

	NAME	SIGN	DATE
DRAWN	MAHESH S.		08.10.22
CHECK	MAHESH S.		08.10.22
APPRD.	VIJAY T.		08.10.22

If any queries contact : projectsautomation@nihva.com

ALL DIMENSION ARE IN mm

CLIENT - MR. PRANAV

LOCATION - NOIDA_IN

PRODUCT - RETRACTABLE ROOF

NIHVA\22-23\02XX | REV- 0

SCALE: NTS | SHEET: 01 OF 01