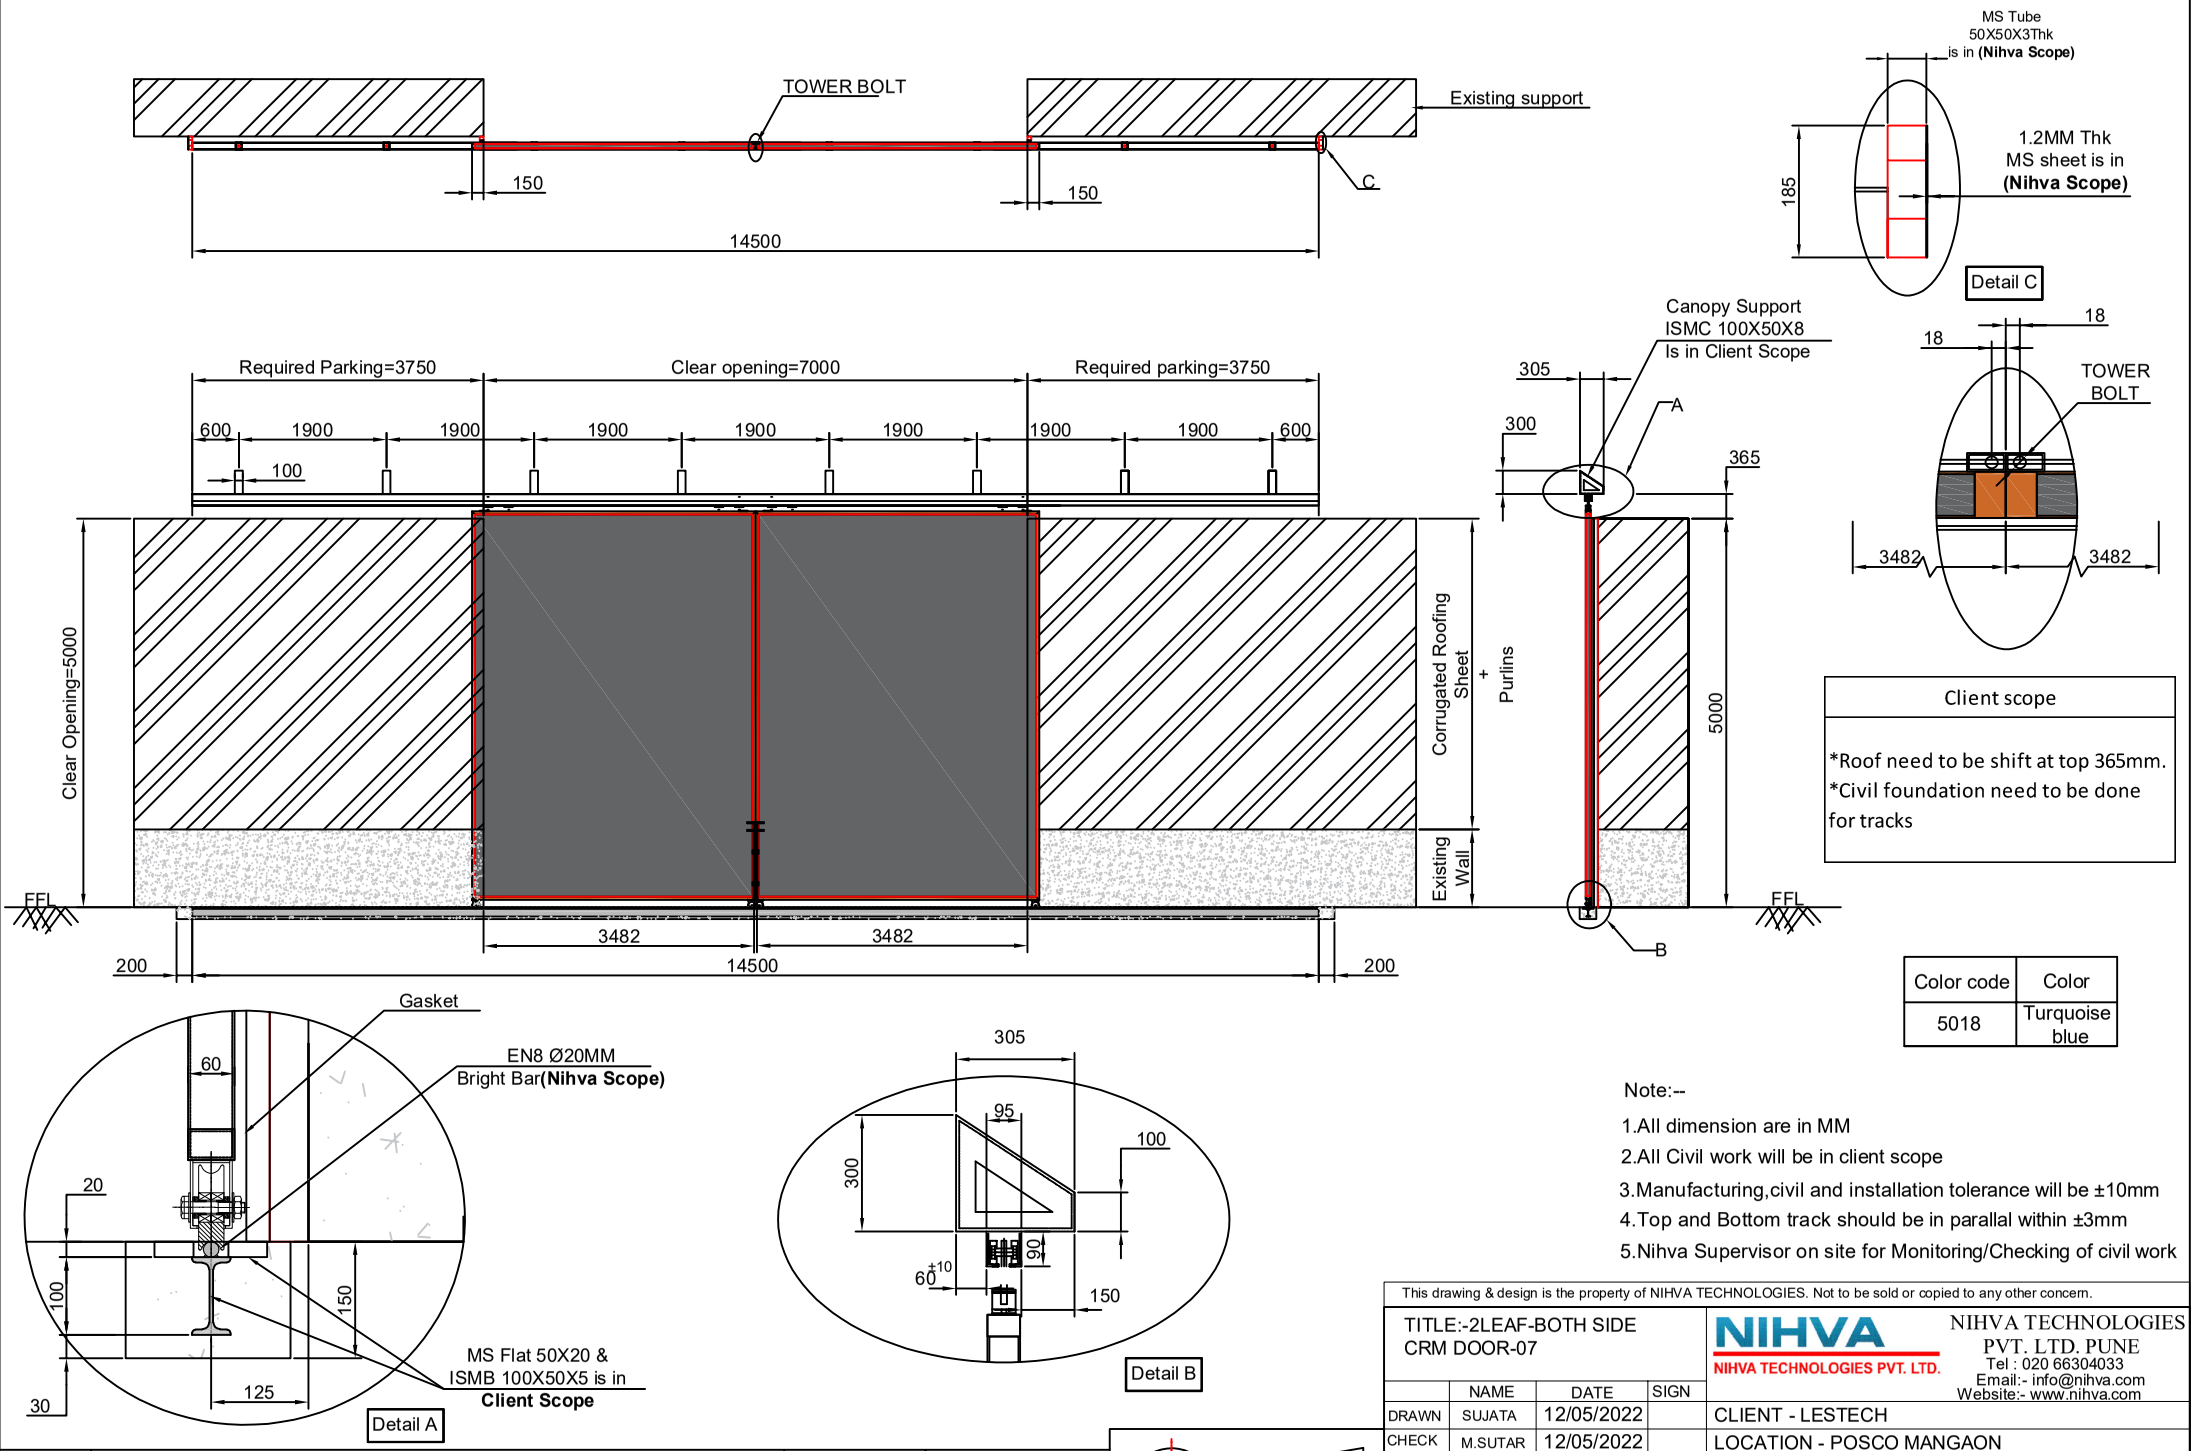



| Client scope |
|---|
| *Roof need to be shift at top 365mm.<br>*Civil foundation need to be done for tracks |

| Color code | Color |
|---|---|
| 5018 | Turquoise blue |

Note:--

1.All dimension are in MM

2.All Civil work will be in client scope

3.Manufacturing,civil and installation tolerance will be ±10mm

4.Top and Bottom track should be in parallal within ±3mm

5.Nihva Supervisor on site for Monitoring/Checking of civil work

This drawing & design is the property of NIHVA TECHNOLOGIES. Not to be sold or copied to any other concern.

TITLE:-2LEAF-BOTH SIDE CRM DOOR-07

NIHVA TECHNOLOGIES PVT. LTD.
NIHVA TECHNOLOGIES PVT. LTD. PUNE
Tel : 020 66304033
Email:- info@nihva.com
Website:- www.nihva.com

| | NAME | DATE | SIGN |
|---|---|---|---|
| DRAWN | SUJATA | 12/05/2022 | |
| CHECK | M.SUTAR | 12/05/2022 | |
| APPRD. | V.TARAK | 12/05/2022 | |

If any queries contact : design@nihva.com

ALL DIMENSION ARE IN mm

CLIENT - LESTECH

LOCATION - POSCO MANGAON

PRODUCT - SLIDING DOOR

DWG NO:-NIHVA/22-23/CLT/0034 | REV- 0

SCALE: NTS | SCALE:-- 1:1 | SHEET: 01 OF 01

| | Revision | Date | Revised By |
|---|---|---|---|
| | | | |