

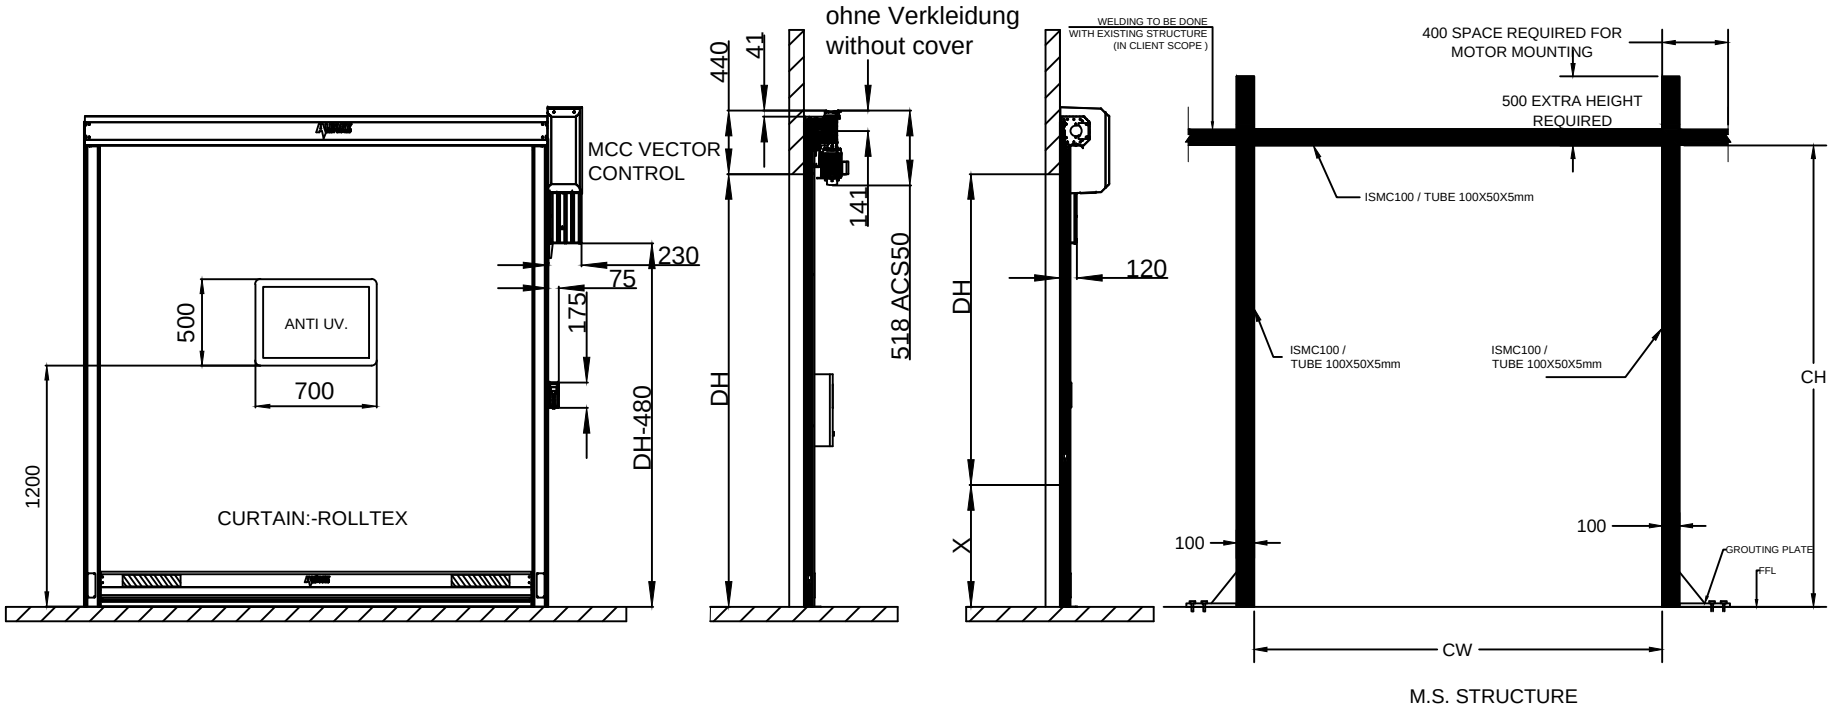


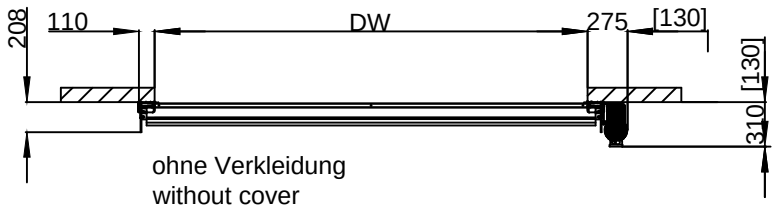

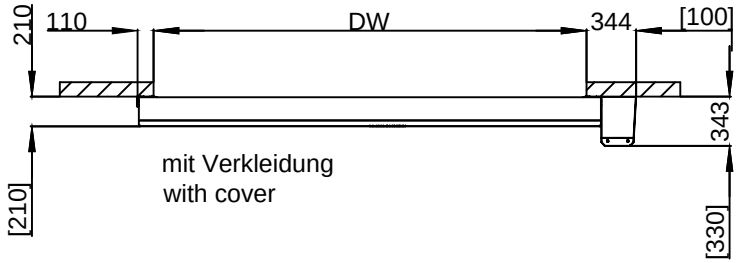

Tolerance ±3 mm (for all dimensions)
Dimensions in [ ] ==> clearance for installation

NOTE : REQUIRED M.S. STRUCTURE , FITTING & ALL CIVIL WORK IN CLIENT SCOPE.

1800mm	2000mm	01 NO	RAL : 5002 BLUE CURTAIN:- ROLLTEX +
CLEAR WIDTH (DW)	CLEAR HEIGHT (DH)	QTY	RAL CODE

This drawing & design is the property of NIHVA TECHNOLOGIES. Not to be sold or copied to any other concern.

TITLE	HIGH SPEED DOOR RP300 & STRUCTURE		
	NAME	SIGN	DATE
DRAWN	S.M.S.		8.12.20
CHECK	A.P.		8.12.20
APPV'ED			

NIHVA TECHNOLOGIES PVT. LTD.
NIHVA TECHNOLOGIES PVT. LTD. PUNE
Tel : 020 66304033
Email:- info@nihva.com
Website:- www.nihva.com

CLIENT :- TENNECO CLEAN AIR (I) PVT LTD.	
PROJECT :- G6 PHASE 3, CHAKAN	
LOCATION :- CHAKAN	
If any queries contact : projectsupport@nihva.com	DWG. NO. :- NIHVA/20-21/0104 REV:-R00
ALL DIMENSION ARE IN mm	SCALE: NTS WT: SHEET: 01 OF 01