


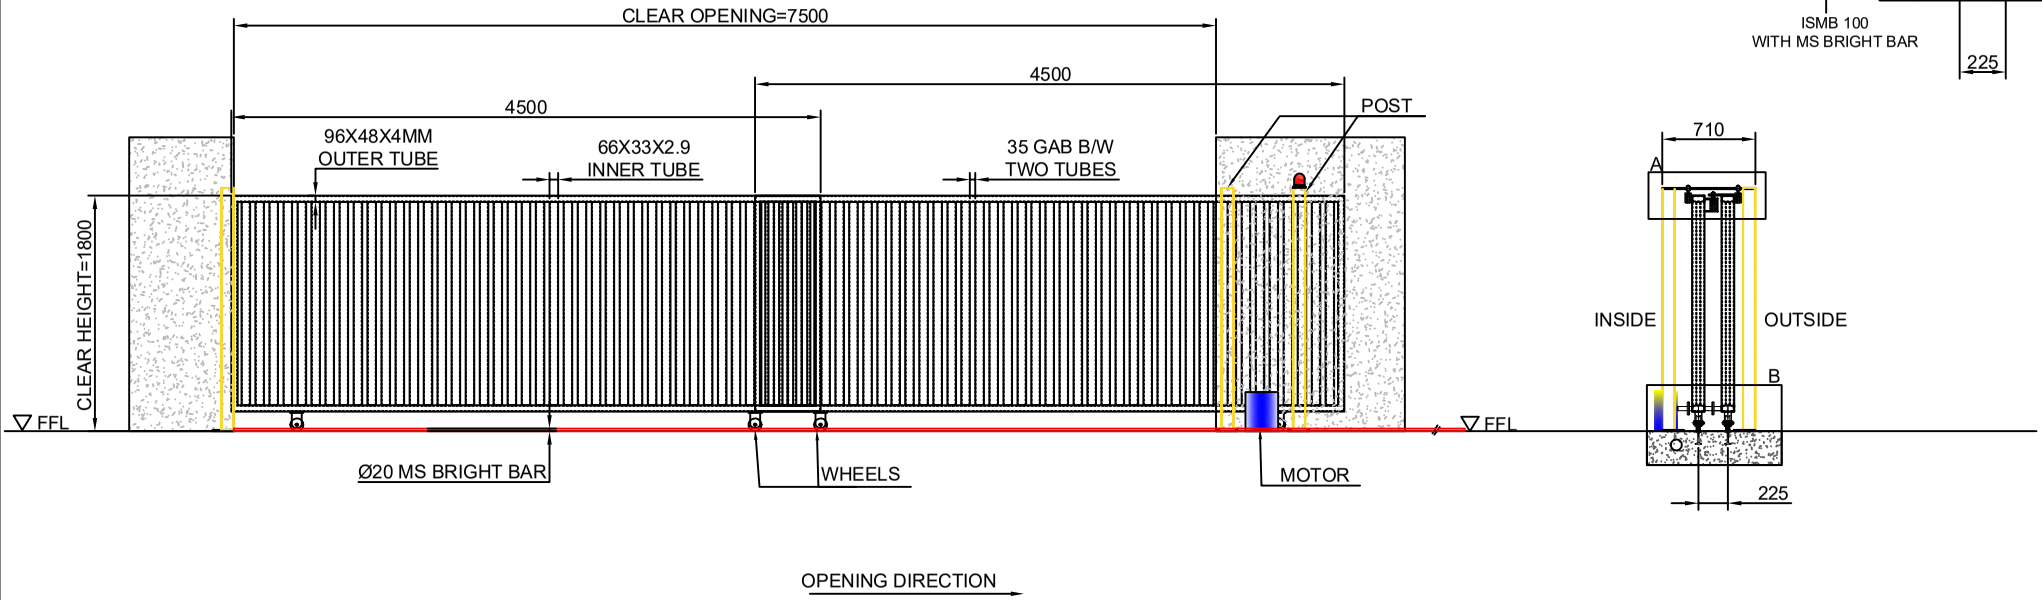

NOTE:-

1.ALL DIMENSION ARE IN MM

2.FIBRICATION TOLERANCE WILL BE ±10MM

3.REQUIRED ALL CIVIL WORK WILL BE IN CLIENT SCOPE

4.REQUIRED PARKING WILL BE 4600MM

This drawing & design is the property of NIHVA TECHNOLOGIES. Not to be sold or copied to any other concern.

TITLE:- Two Leaf for tel.sliding gate				NIHVA TECHNOLOGIES PVT. LTD. PUNE Tel : 020 66304033 Email:- info@nihva.com Website:- www.nihva.com	
	NAME	DATE	SIGN		
DRAWN	SUJATA	02/03/2022		CLIENT - Kunal Structure Ind. Pvt. Ltd	
CHECK	G.PATIL	02/03/2022		LOCATION - Gujrat (Diyodar)	
APPRD.	P.J	02/03/2022		PRODUCT - Tel.sliding gate	QTY-
If any queries contact : design@nihva.com				DWG NO:- NIHVA/21-22/CLT/0357	REV- 1
ALL DIMENSION ARE IN mm				SCALE: NTS	SCALE:-- 1:1 SHEET: 01 OF 01

Rev No.	Revision	Date	Revised By
1.	Revision made as per client remark(Gab b/w two tubes and post CD)	04/03/2022	Sujata