


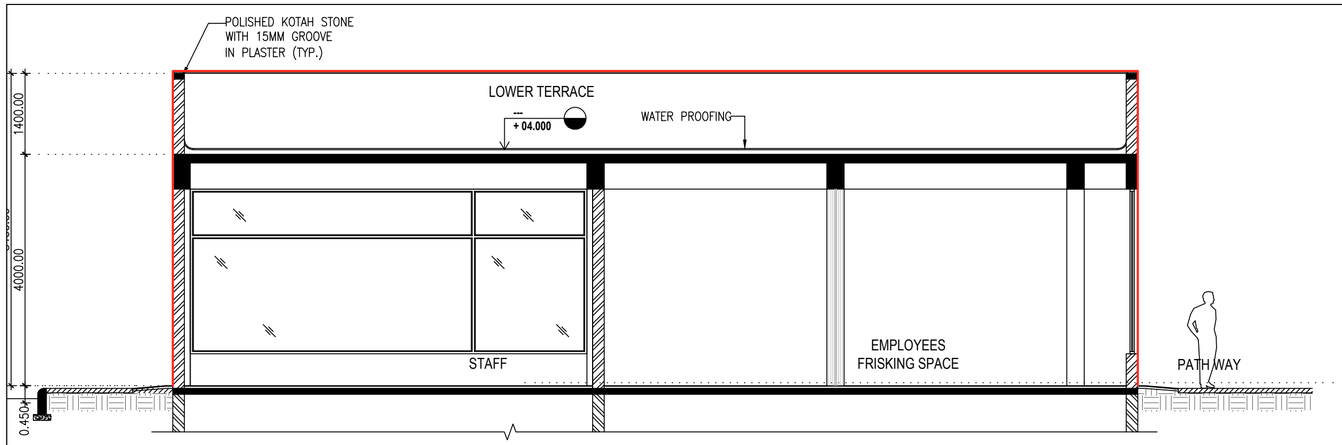


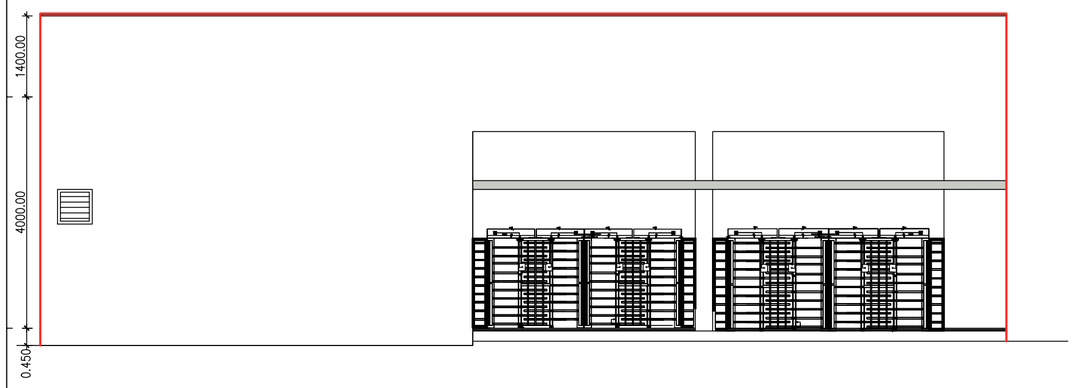


ELEVATION-1

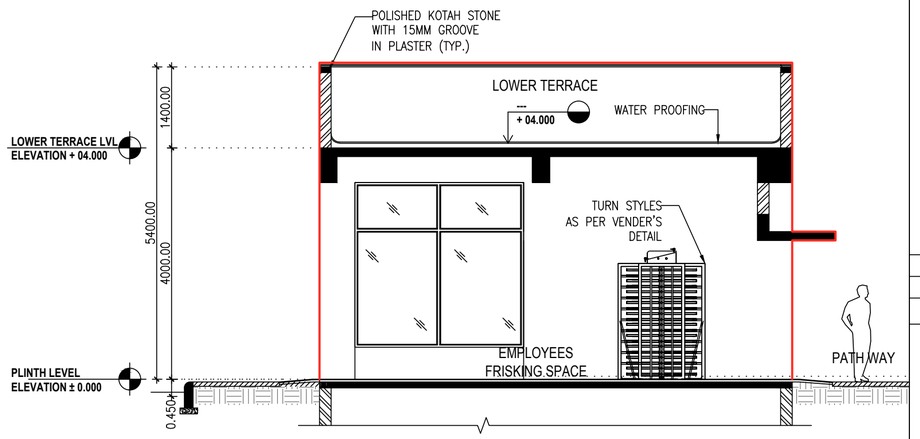

SECTION-2

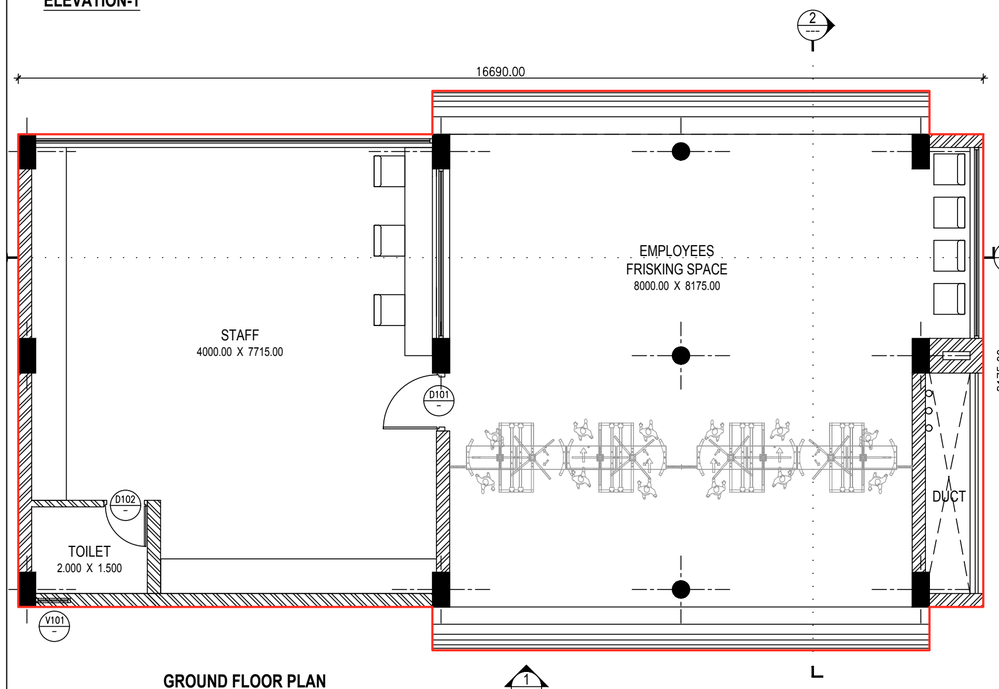

GROUND FLOOR PLAN

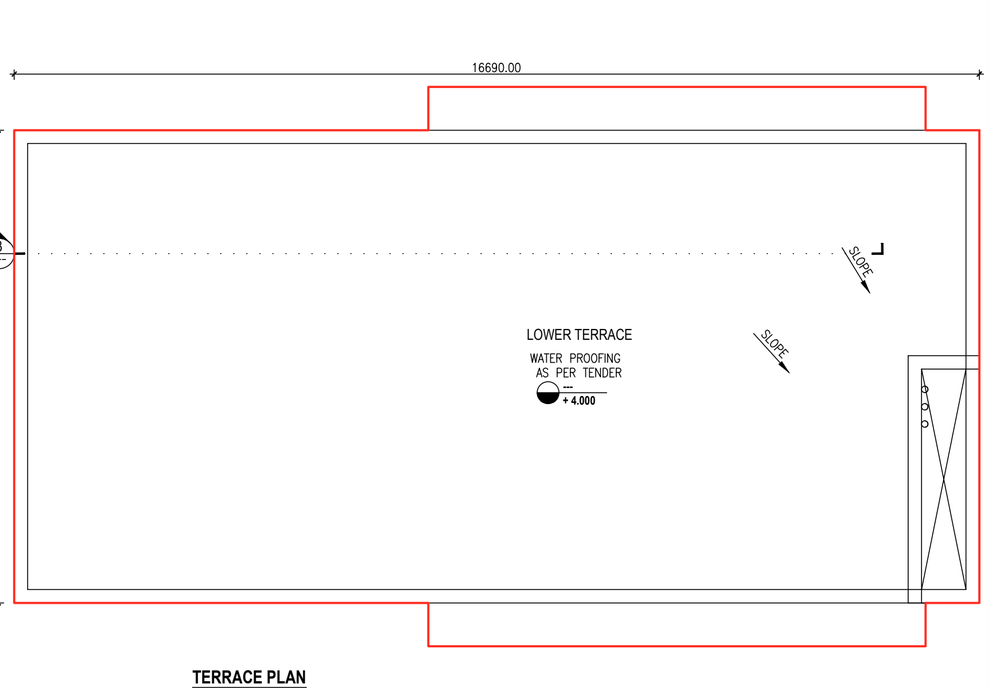

TERRACE PLAN

THIS DRAWING & DESIGN IS THE SOLE PROPERTY OF VMS & SHALL NOT BE COPIED, TRACED OR REPRODUCED BY ANY MEANS WITHOUT PRIOR WRITTEN CONSENT OF THE FIRM.

GENERAL NOTES :

1. ALL THE DIMENSIONS ARE UNFINISHED DIMENSIONS.
2. ALL DIMENSIONS ARE IN MM AND LEVELS ARE IN MT, UNLESS OTHERWISE MENTIONED.
3. ALL THE DIMENSIONS SHALL BE READ & NOT TO BE MEASURED.
4. IN CASE OF ANY DISCREPANCY, BRING IT TO THE NOTICE OF THE ARCHITECT IMMEDIATELY.
5. DETAIL DRAWING PRECEDES THE GENERAL DRAWING

SCHEDULE OF OPENINGS:


MKD.	SIZE	SILL HT.	LINTEL HT.	REMARKS
D101	1200x2400	----	2400	–
D102	750x2400	----	2400	–
D103	750x2100	----	2400	–
V101	600x600	1500	2100	–

FOR TENDER

NO.	DATE	DESCRIPTION	DRN BY	CHK BY

REVISION HISTORY

KEY PLAN
SCALE : N.T.S.

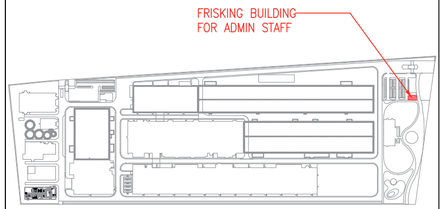

REFERENCE DRAWINGS :

01. ARCHITECTURAL :	-
02. STRUCTURAL :	-
03. HVAC :	-
04. ELECTRICAL :	-
05. UTILITIES :	-

PLAN, ELEVATION & SECTIONS

FRISKING FOR ADMIN STAFF

PROJECT NAME : TIPL AT SANAND

PROJECT NO.	SCALE :	DRAWN : ASHISH C.
3824		CHECKED: BHAKTI B.
	DATE : 03-12-2024	APPROVED : DARSH D.
		CO. CHECKED: DARSH D.

VMS ENGINEERING & DESIGN SERVICES (P) LTD.
CHITRAKOOT FLATS, BEHIND TIMES OF INDIA, OFF ASHRAM ROAD,
AHMEDABAD-380 009. PHONE: +91 (079) 2658-8829/4488, 40236236
FAX : +91 (079) 2658 3596 WWW.VMSCONSULTANTS.COM

SHEET SIZE	DRAWING NO.	TENDER	REVISION:
A2	T.A.7a.101	T	R0