WORKERS FACILITY DESCRIPTION


S.NO	DESCRIPTION	TOTAL NO
1.	MALE TOILET (M)	14
2.	MALE REST ROOM (M)	08
3.	LOCKER ROOM (M 500 NOS)	01
4.	CHANGE ROOM (M)	05
5.	WASHING BATHING (M)	04
6.	DRINKING WATER COOLER	05
7.	CANTEEN LUNCH	01
8.	AMBULANCE ROOM	01

FIRE FIGHTING ARRANGEMENTS

SYMBOL	DESCRIPTION	TOTAL NO.
	FIRE EXTINGUISHER	55
	DRINKING WATER FACILITY	05
	SAND BUCKET	00
	FIRE HYDRANT POINT	05
	FIRE ALARM CALL POINT	00
EMERGENCY EXIT	EMERGENCY EXIT (available on each floo	
	ASSEMBLY AREA	

DOOR WINDOW SCHEDULE

	DW	SILL LVL	LINTEL LVL
WINDOW	W	3'-0"	8'-0"
DOOR	D	---	8'-0"
VENTILATION	V	5'-6"	8'-0"
ROLLING SHUTTER	RS	---	10'-0"

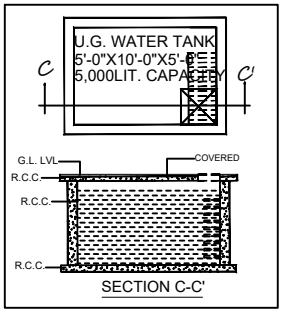

SECTION C-C'


Area To Be Approved
Area Already Approved

Reference:- Previous Registration Number - RJ-31525
Previous Approved Drawing Number - P-45746CIFB2020
Previous Approved Drawing Date - 18082020

Factory Premises Industrial Land
Water Hydrant Pipe Line Shown Like This

ROAD 30.00 Mt WIDE

ROAD 30.00 Mt WIDE

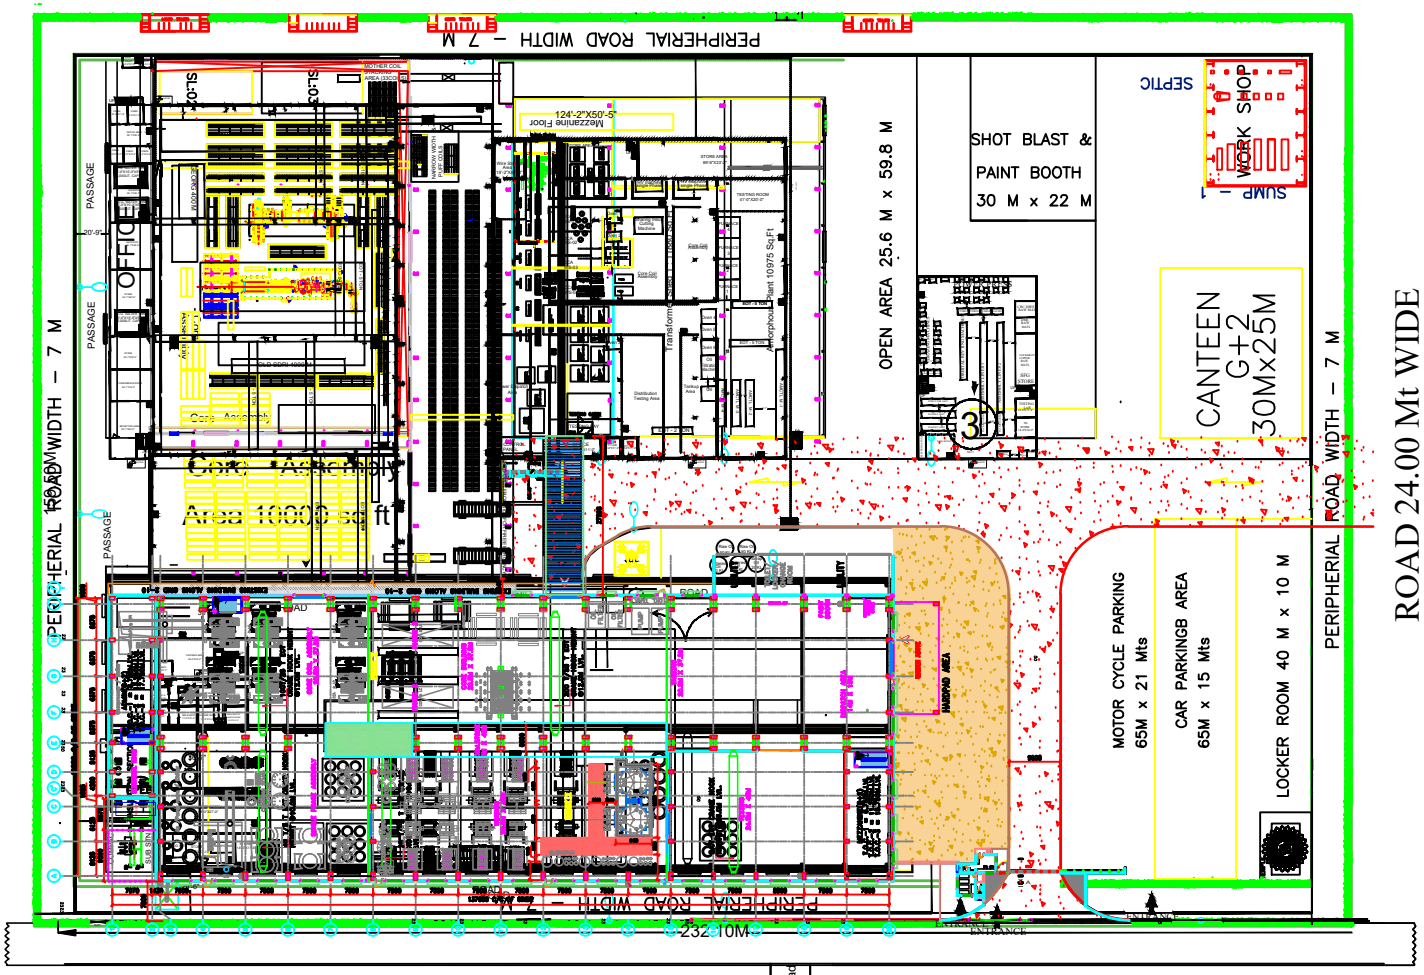

ROAD 30.00 Mt WIDE

ROAD 24.00 Mt WIDE

ROAD 18.00 Mt WIDE

Main Road

SITE PLAN

CLIENT DETAILS: -

M/S MANGAL ELECTRICAL INDUSTRIES LTD.
Plot No. E-40 & 46 (A), Shree Khatu Shyam Ji Ind. Area Reengus, Sri Madhopur, Reengus,Sikar (Raj.) 332404

Layout Scale = N.T.S.
Factory Area : 37008.40 Sq. M.

Drawing Title:

Site Plan

Signature:

GENERAL NOTES: -

1. ALL DIMENSION ARE IN FEET UNLESS OTHERWISE SPECIFIED.
2. DRAWING MUST BE READ IN CONJUNCTION WITH STRUCTURAL DRAWING.
3. THE SIZE OF ALL THE STRUCTURAL MEMBERS TO BE REFER FROM DRAWING OF STRUCTURAL CONSULTANT.
4. DRAWING NOT TO BE SCALED. ONLY WRITTEN DIMENSIONS ARE TO BE FOLLOWED.
5. CONTRACTOR TO STUDY DRAWING & REVERT BACK IN CASE OF ANY DISCREPANCIES BEFORE EXECUTION.
6. ALL CENTER LINE DIMENSIONS ARE WITH REFERENCE TO (0, 0).
7. THE LEVELS SPECIFIED IN ALL THE DRAWINGS ARE FINISHED FLOOR LEVELS UNLESS OTHERWISE SPECIFIED.
8. ALL DIMENSION ARE FROM UNFINISHED TO UNFINISHED SURFACE UNLESS OTHERWISE SPECIFIED.

NOTE:

Direction: N

LEGEND: -

- 230MM. THICK BRICK
- 115MM. THICK BRICK WALL
- R.C.C ROOF SLAB
- MACHINES
- HYDRANT POINT
- FIRST AID KIT
- CO2 FIRE EXTINGUISHERS
- WATER HYDRANT PIPELINE
- FACTORY AREA
- SAND BUCKET

Revision Table

Revision Number	Date	Description