

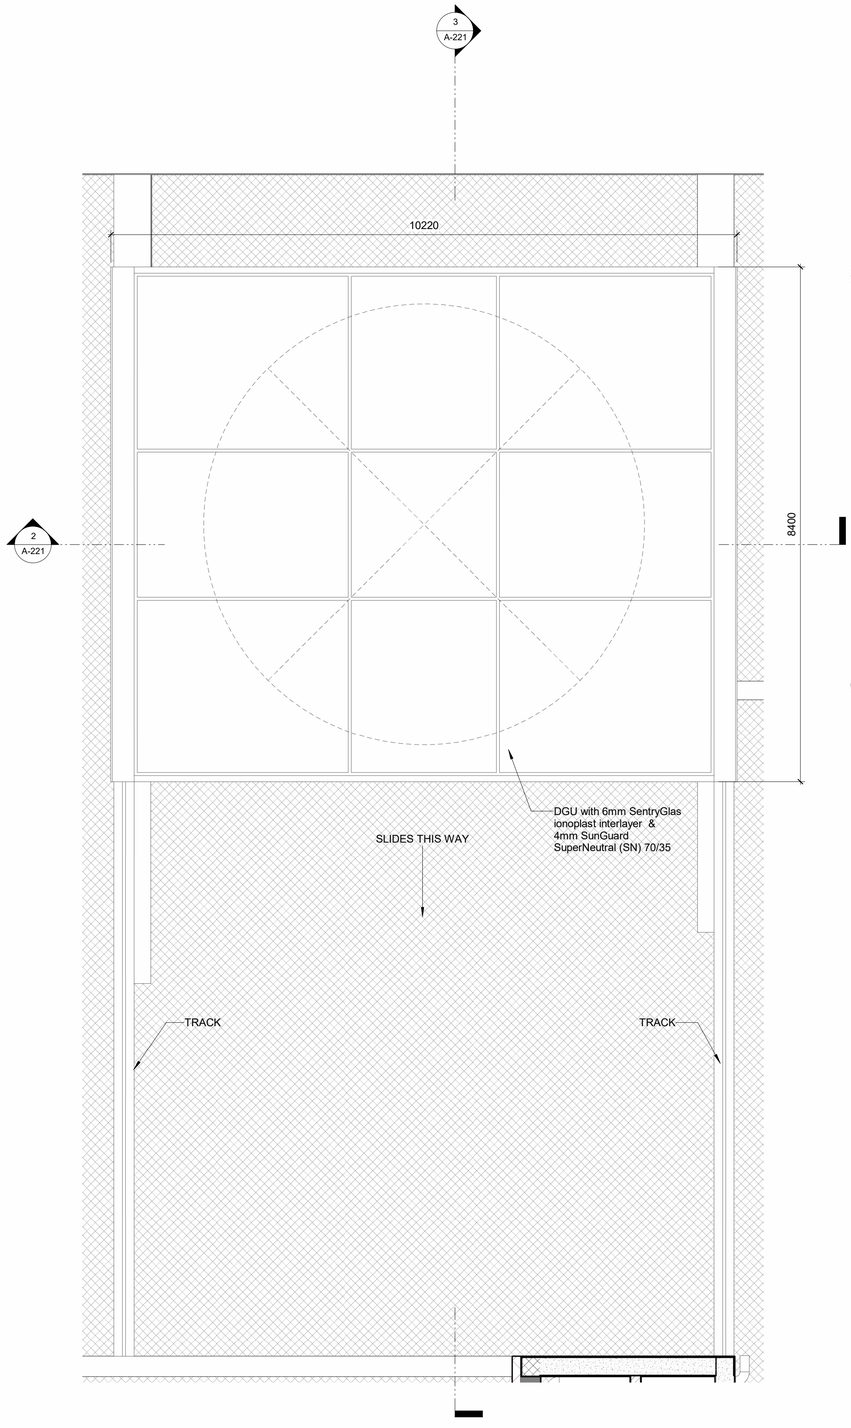


1 Central Courtyard Skylight
1 : 50

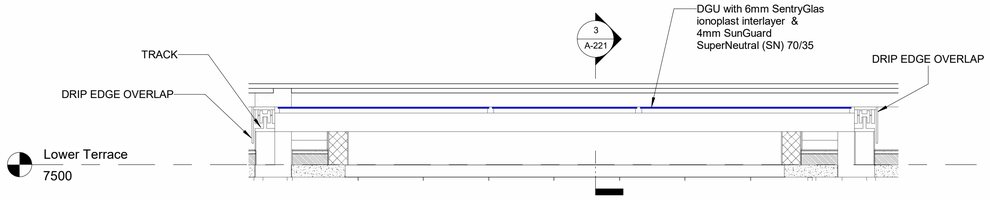

2 Central Courtyard Skylight Section 1
1 : 50

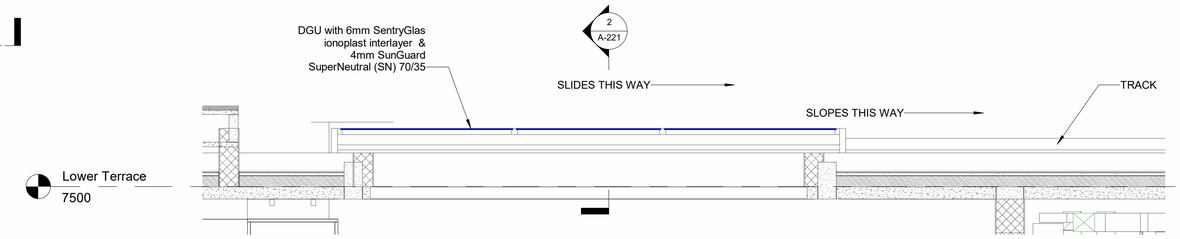

3 Central Courtyard Skylight Section 2
1 : 50

KRISHNAN PARVEZ architects
SHOP NO.5, KRISHNA BLDG., ST. ANTHONY STREET, KALINA JN., SANTACRUZ (E), MUMBAI 400 098. MAHARASHTRA, INDIA.
tel : + 91 22 6702 4521 fax : + 91 22 6702 4522
ww.kpa.in projects@kpa.in

PROJECT TEAM:

STRUCTURAL ENGINEER
GTWCSE
2nd Floor, Krishnakunj, 383-403
RSC-36-37, Gorai - 2,
Borivali (West), Mumbai - 400 092
+91 8655077873

HVAC CONSULTANT
ENOVA
1402 Remi Commercio, 14 Shah Industrial Estate
Andheri (W), Mumbai 400 053
+91 9820100524

PLUMBING CONSULTANT
HYDRO MECH. CONSULTANTS
B-107, Blue Bell Apartment, 1st Floor, Dr. C.G.Road, Sai Dham Lane
Chembur East, Mumbai - 400074
+91 65710407

ELECTRICAL CONSULTANT
K.S.CHANDAVAR & ASSOCIATES
No. 41, Juhu Shangrila Apts, Samarth Ramdas Marg,
Mumbai-400049
+91 9322820502

PROJECT:

VILLA AT LA MISERE

La Misere Road, Mahe, Seychelles

APPROVAL STAMP

© KRISHNAN PARVEZ ARCHITECTS
31/05/2024

REVISIONS:

SCALE	**1 : 50**
DATE ISSUED	**31/05/2024**
PROJECT NO	**AR-114/22/LM**
DRAWN BY	**Author**
CHECKED BY	**Checker**

DRAWING TITLE:

Skylight Drawing

A-221