

DRAWING

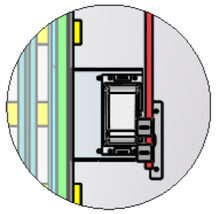


DETAIL B
SCALE 1 : 18

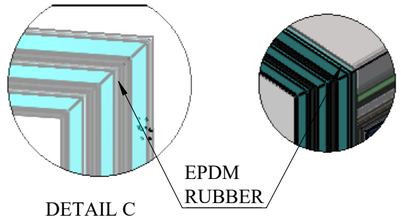


DETAIL C
SCALE 1 : 18


DETAIL F
SCALE 1 : 20

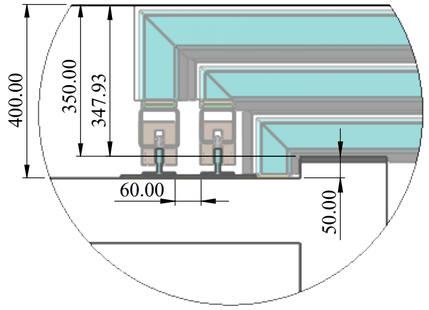


DETAIL E
SCALE 1 : 10

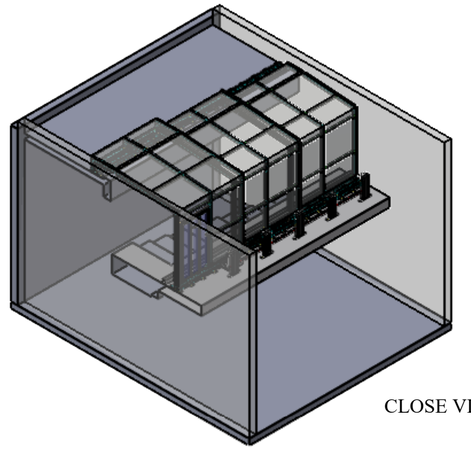


CLOSE VIEW

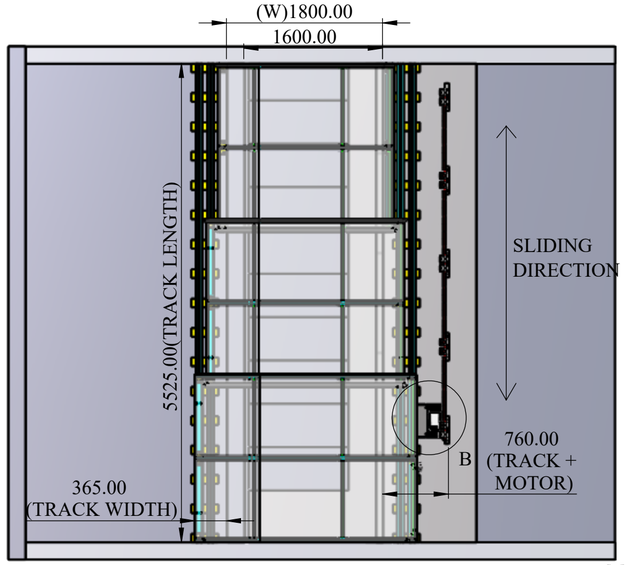


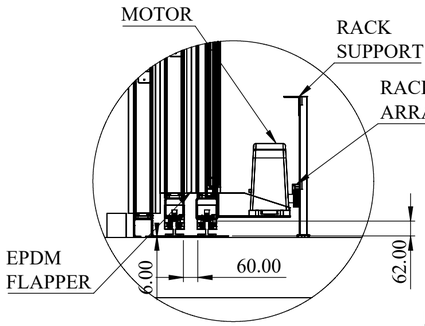


DETAIL A
SCALE 1 : 18

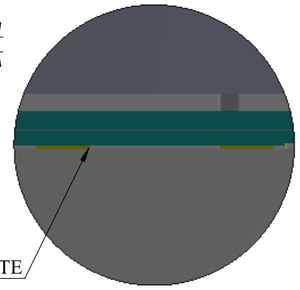



DETAIL H
SCALE 1 : 8

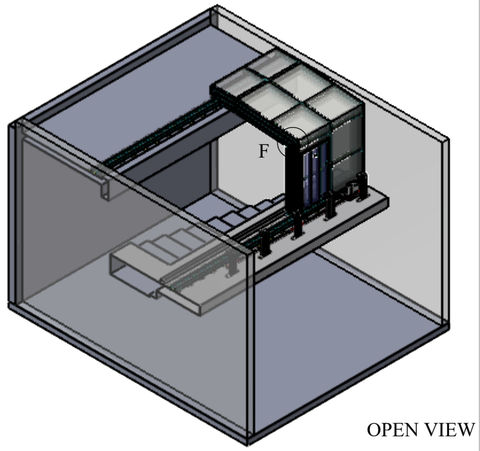

OPEN VIEW

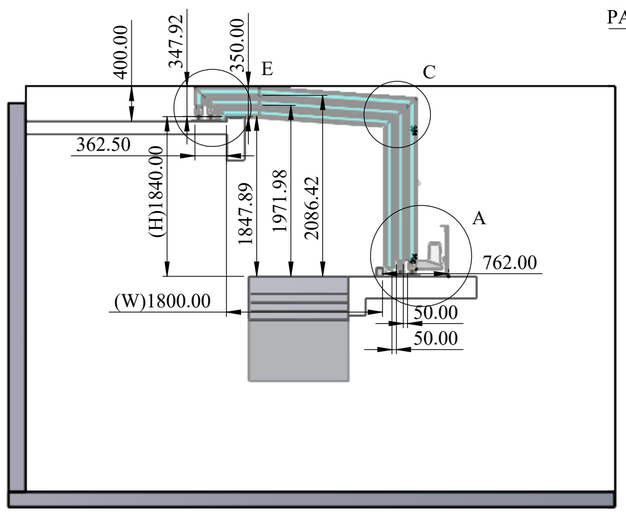

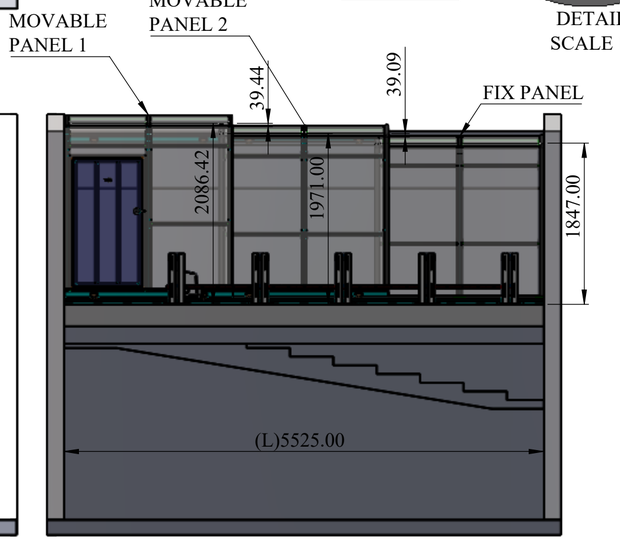

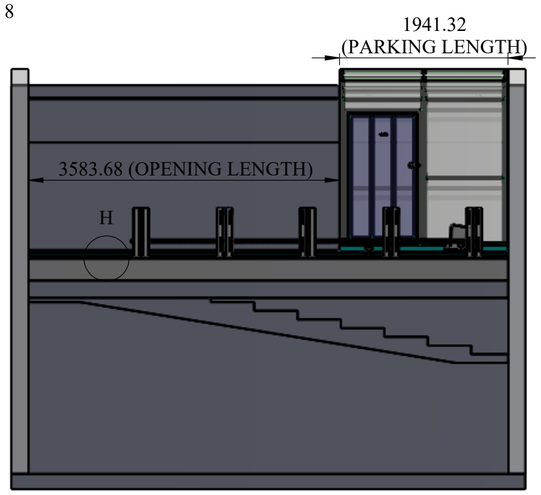

REV DESCRIPTION	DATE	REV NO
	24-07-2026	REV 00
1.		

NOTE :

THIS DRAWING IS FOR CLIENT APPROVAL
BASE STRUCTURE IN CLIENT SCOPE
EPDM RUBBER FLAPPER PROVIDED FOR AIR WATER SEAL.

SPECIAL INSTRUCTION'S :

This drawing & design is the property of NIHVA TECHONOLOGIES PVT. LTD. Not to be sold or copied to any other concern

TITLE - L SHAPE ENCLOSURE

DWG NO - NTPL-000

NIHVA TECHNOLOGIES PVT.LTD.PUNE
Website - www.nihva.com

	NAME	SIGNATURE	DATE
DRAWN	V.W.		24-07-2026
CHK'D	S.P.		25-07-2026
APPV'D	V.T.		25-07-2026

PRODUCT - L SHAPE ENCLOSURE.
CLIENT NAME - LODHA GROUP.
SITE LOCATION - MUMBAI (VERSOVA).
MATRIAL -
QTY - 1
If any queries contact - info@nihva.com
ALL DIMENSION ARE IN mm
A2
PROJECTION METHOD:
SCALE :
SHEET 1 OF 1