


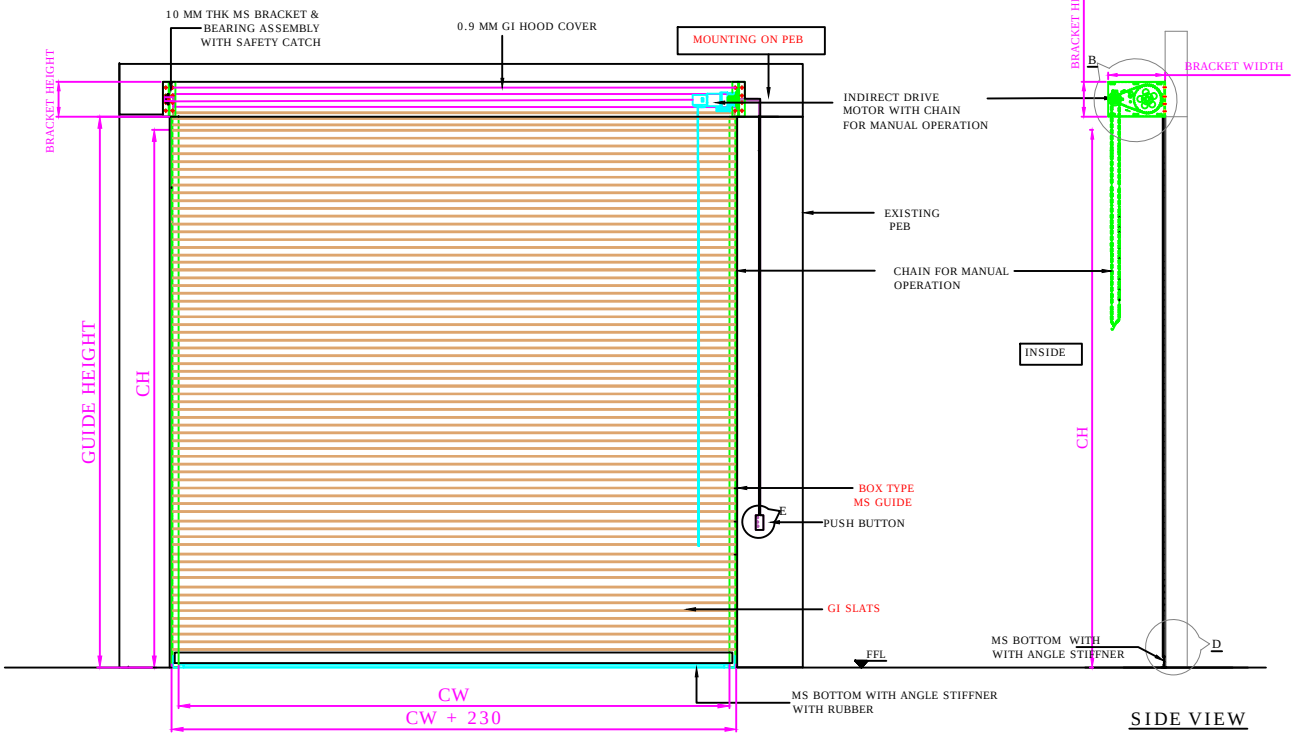


ELEVATION

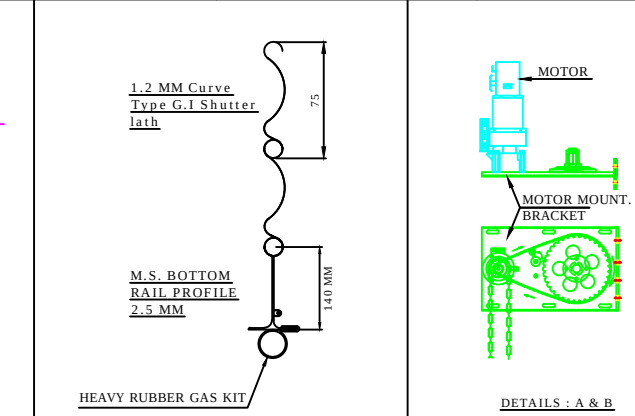


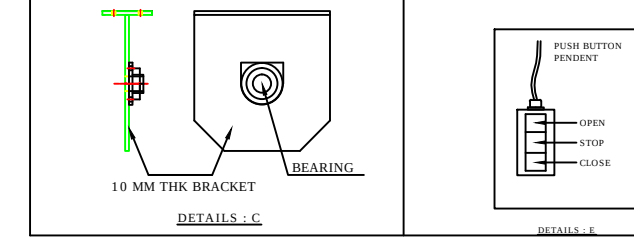

SIDE VIEW

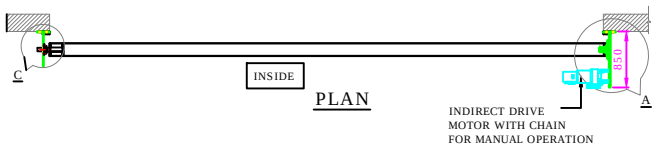

PLAN

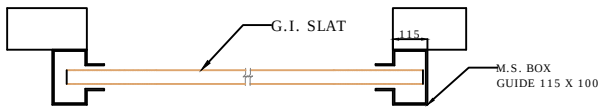

SR NO	CLEAR WIDTH(CW)	CLEAR HEIGHT(CH)	QTY	LOCATION	MOTOR POSITION (SEEN FROM INSIDE)
6	6000	5850	1	A-GRADE SHUTTER	RH
5	6000	5850	1	G-GRADE SHUTTER	RH
4	6070	8000	1	F-19	RH
3	6070	8000	1	B-19	LH
2	6070	8000	1	F-1	LH
1	6070	8000	1	B-1	RH

KINDLY NOTE THAT MOTORISED ROLLING SHUTTER & ALL COMPONENTS USED FOR MOTORISED ROLLING SHUTTER SHOULD WITHSTAND WIND LOAD FOR 140KMPH .

KINDLY REFER TABLE FOR MOTOR POSITIONS AS SEEN FROM INSIDE.

RAL CODE FOR POWDER COATING	SHADE	COLOUR
RAL 7035	LIGHT GREY	

This drawing & design is the property of NIHVA TECHNOLOGIES. Not to be sold or copied to any other concern.

TITLE- GI SLAT MOTORIZED ROLLING SHUTTER

NIHVA TECHNOLOGIES PVT. LTD.

NIHVA TECHNOLOGIES PVT. LTD. PUNE
Tel : 020 66304033
Email:- info@nihva.com
Website:- www.nihva.com

	NAME	SIGN	DATE
DRAWN	SIDDHESHWAR		29.12.2020
CHECK	A.K.		29.12.2020
APPRD.			

CLIENT -

PROJECT -

SITE LOCATION -

If any queries contact : projectsupport@nihva.com

DWG. NO. : NIHVA/20-21/VDR/0091 REV- R00

ALL DIMENSION ARE IN mm

SCALE: NTS WT: SHEET: