



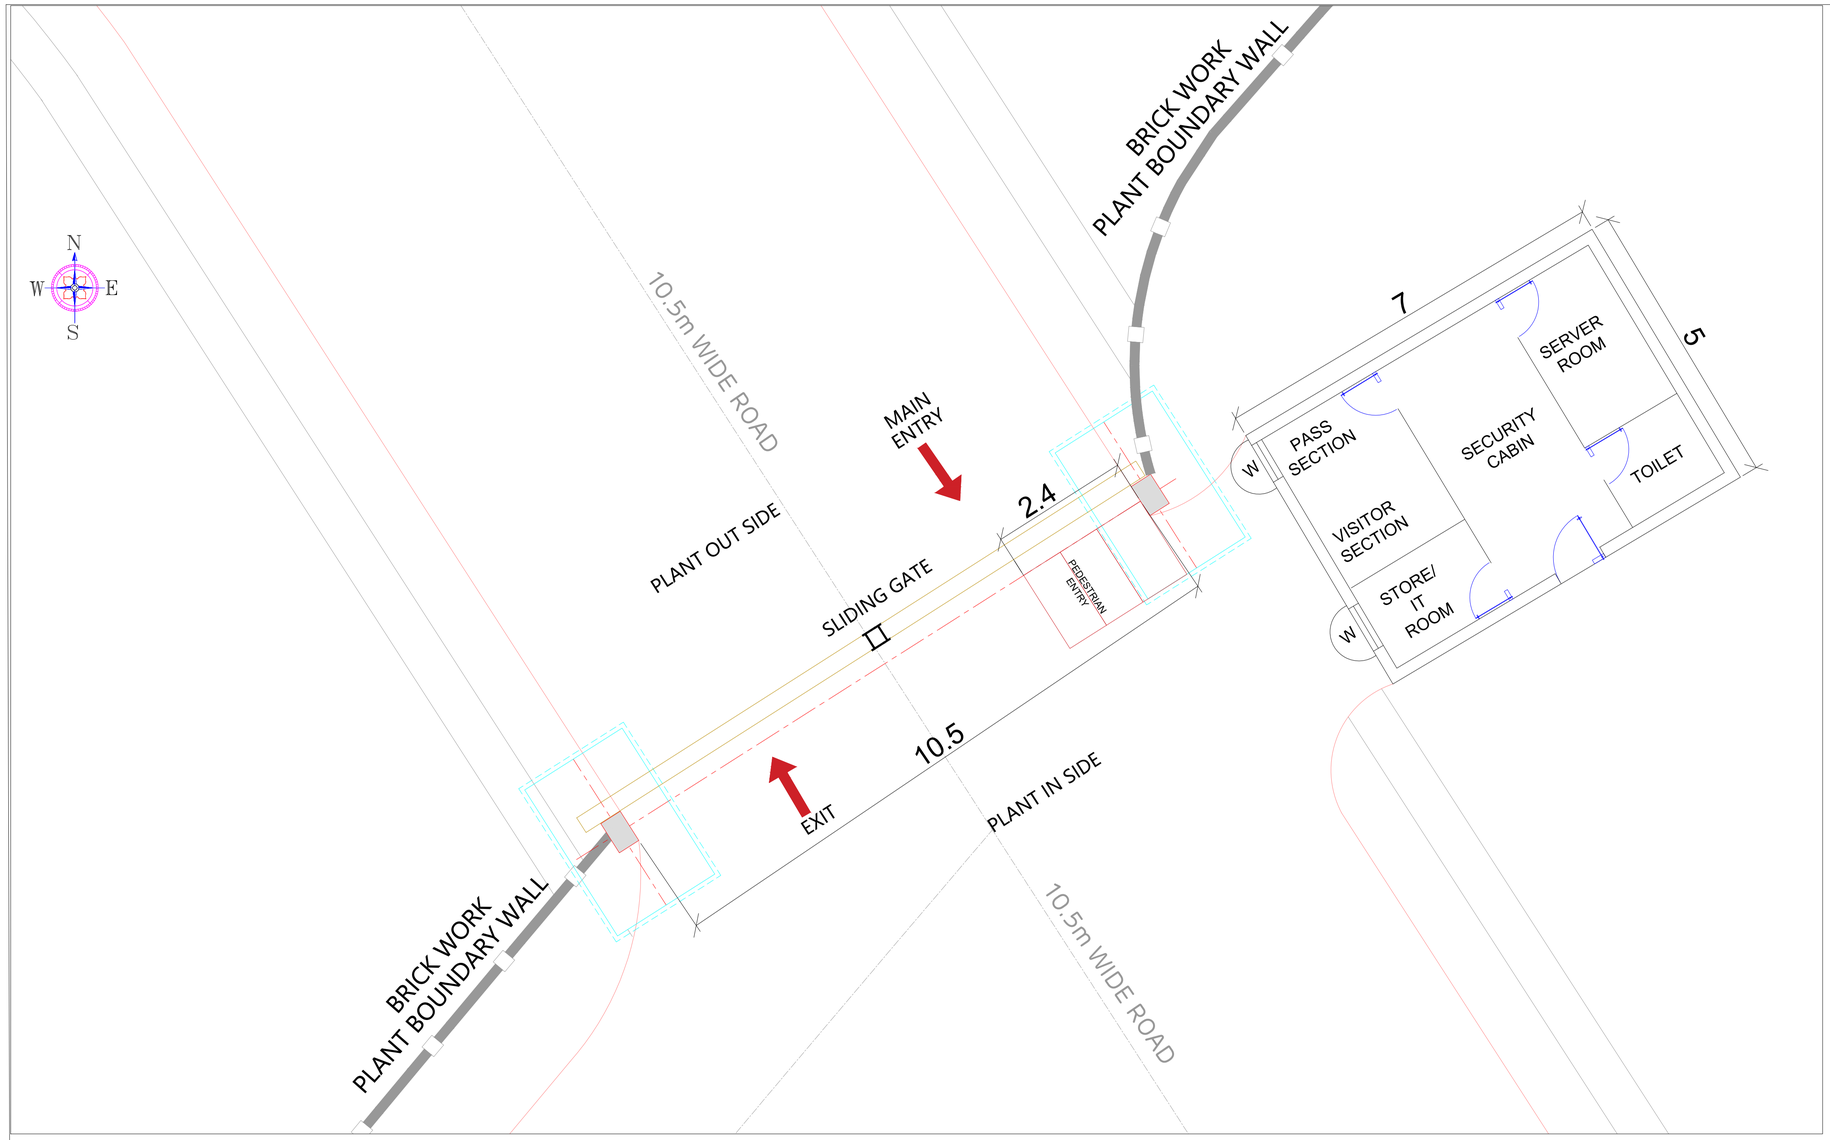

NOTES

ALL DIMENSIONS ARE TO BE READ AND NOT MEASURED
ALL DIMENSIONS ARE IN M.
ALL LEVELS ARE IN METRES
REFER DETAIL DRAWINGS WHEREVER RELEVANT
R.W.P. INDICATES RAIN WATER PIPE
IN CASE THERE IS ANY DISCREPANCY BETWEEN ARCHITECTURAL DRAWINGS AND OTHER DRAWINGS, ARCHITECTURAL DRAWINGS TO BE FOLLOWED. THE DISCREPANCY TO BE BROUGHT TO THE NOTICE OF THE ARCHITECT BEFORE COMMENCEMENT OF THE WORK.

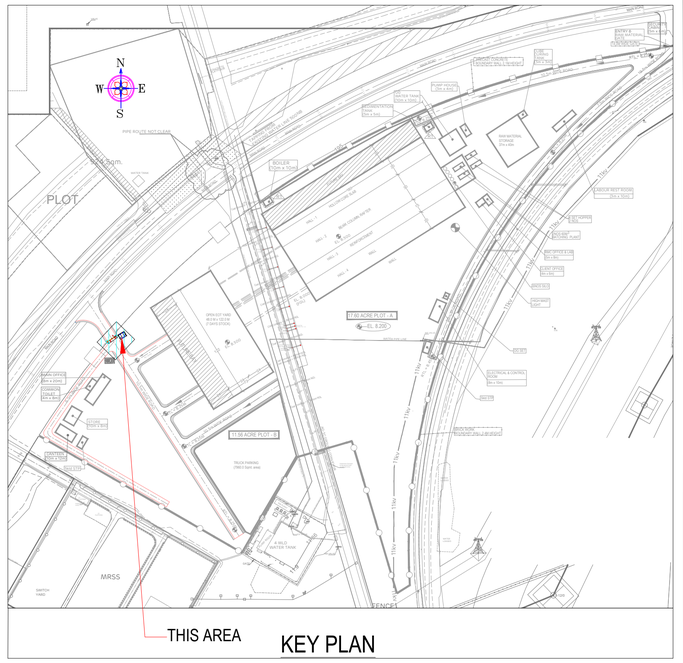

FRONT ELEVATION FROM GATE ENTRY SIDE

Drawing / Document Review & Clearance				
DE		Drawing submitted to all disciplines as input for subsequent engineering.		
DL				
Dept	Civil	Electrical	Mechnical	Layout
Date				

RELESED FOR CONSTRUCTION

REV.	DATE	DESCRIPTION	PREP.	CHECK.	APPROV.
R1	11.09.2024	CONCEPT DRAWING, REVISED AS MARKED ⚠ SLIDING GATE HEIGHT INCREASED TO 2.4M FROM 1.8M	D.S	S.M	S.S.G
R0	30.08.2024	CONCEPT DRAWING	D.S	S.M	S.S.G

	NAME	SIGN	DATE
PREP.	D.S		30.08.2024
DESIG.	S.M		30.08.2024
CHECK.	S.M		30.08.2024
DEPT.HEAD	S.S.G		30.08.2024
PROJ.MGR.	-------		

TITLE:

GATE COMPLEX ARCHITECTURAL PLAN
(10.5M WIDE)

RELEASED FOR			SCALE - AS SHOWN	SHEET: 1	SIZE :A1
	PRELIMINARY				
	TENDER		DWG.NO.		REV.
	ENGINEERING	✓	59AA-E-CIV-OTH-DC-G-I-0001		R1
	INVESTIGATION				