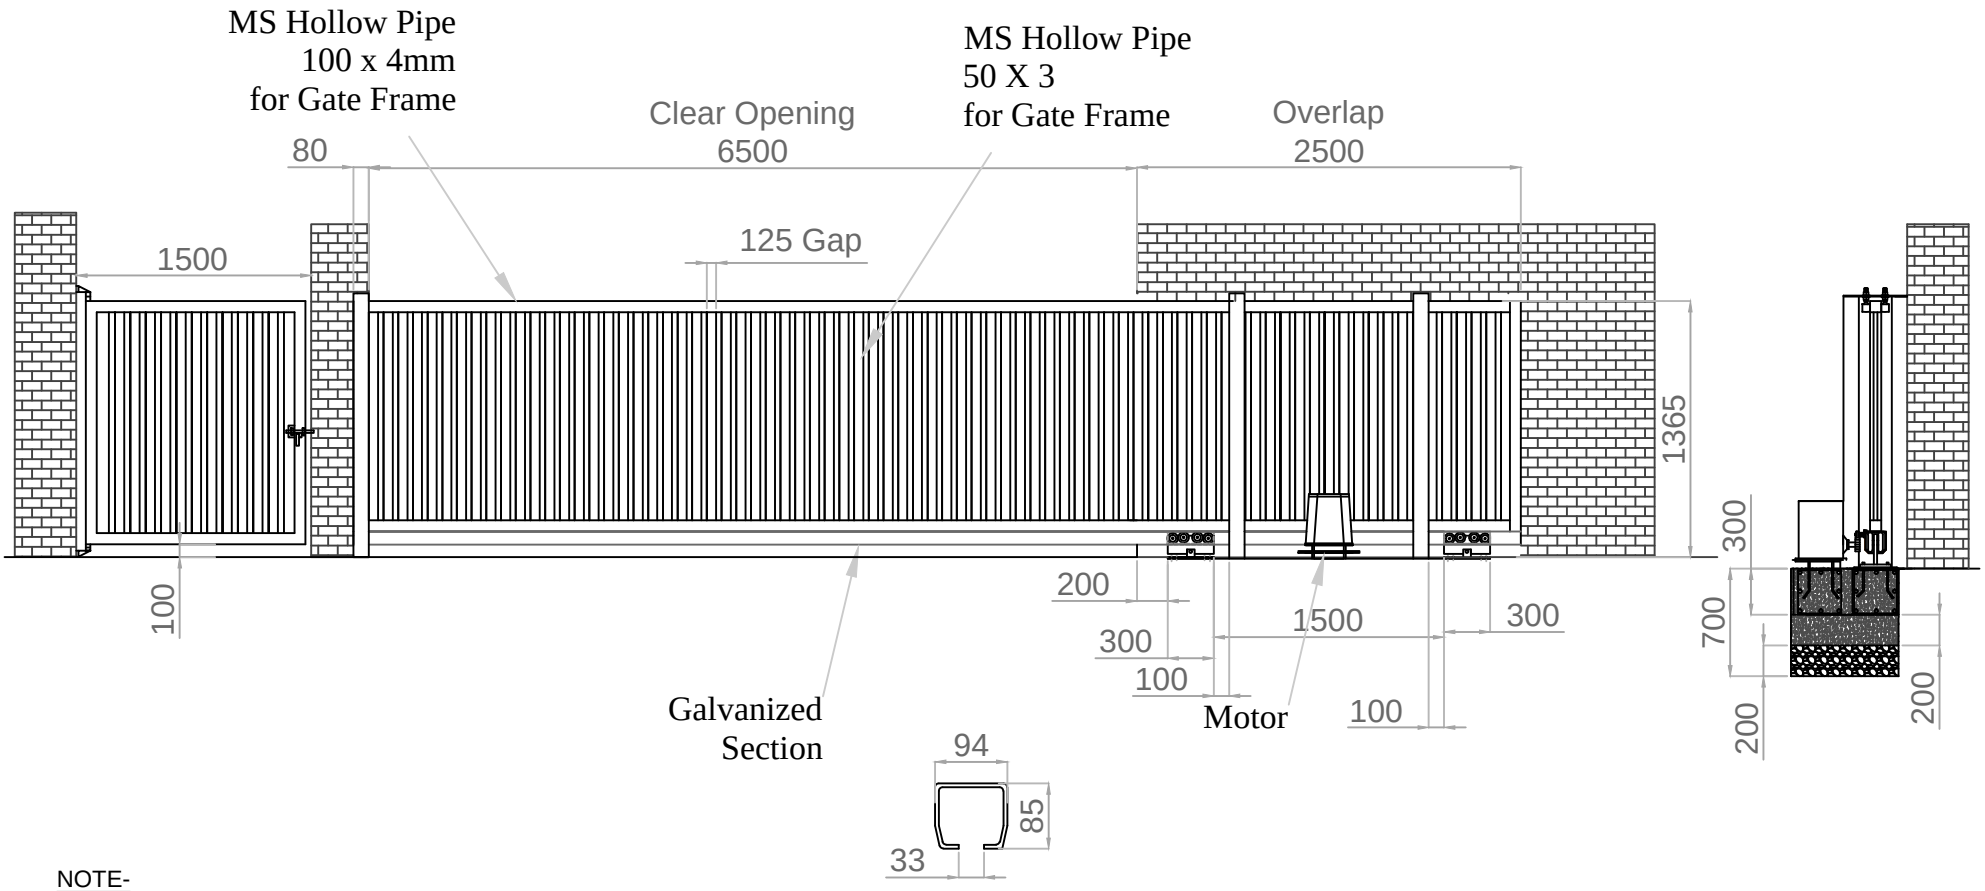


NOTE-

1. ALL REQUIRED CIVIL WORK WILL BE IN CLIENTS SCOPE.
2. GATE LEAF WILL BE IN TWO PARTS FOR TRANSPORTATION & WILL BE WELD TOGETHER ON SITE.
3. FLASHING LIGHT WITH ALARM.
4. VERTICAL ELE. SAFETY EDGE SENSOR(PHOTOCELL).
5. EXTRA PUSH BUTTON.
6. REMOTE CONTROL WITH RECEIVER.
7. EXTRA REMOTE UNIT.
8. KEY SWITCH.

This drawing & designing is the property of NIHVA TECHNOLOGIES. Not be sold or copy to any other concern.

TITLE:- CANTILEVER GATE

	NAME	SIGN	DATE
DRAWN	P.V.A		18.07.19
CHECK	V.M.T		18.07.19
REV.			

CLIENT APPROVAL

ALL DIMENSION ARE IN mm

NIHVA TECHNOLOGIES PVT. LTD.

NIHVA TECHNOLOGY PVT. LTD. PUNE
Tel : 020 66304033
Email:- info@nihva.com
Website:- www.nihva.com

CLIENT - LM WIND POWER BLADES

PROJECT -

SITE - DABASPETH, BANGLORE

DWG. NO. - NIHVA/19-20/0060

SCALE: NTS | Ref. No. | SHEET: 01

If any queries contact : projects@nihva.com