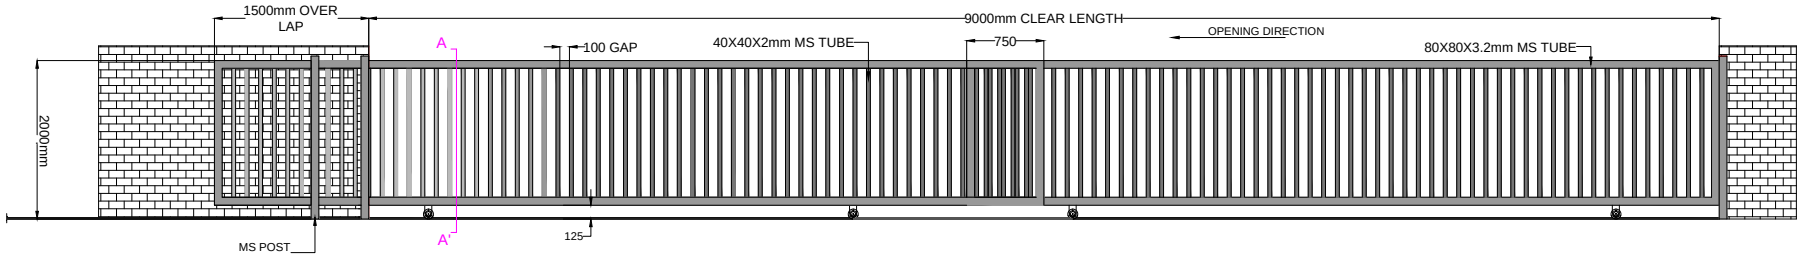
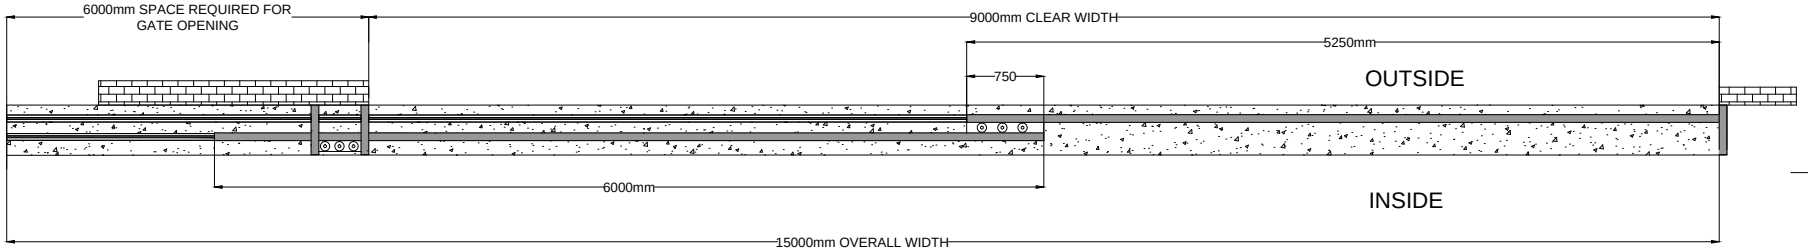


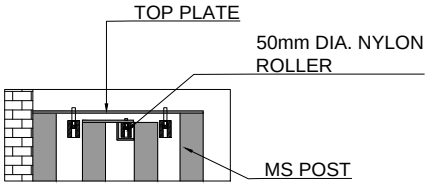

SECTION A-A'



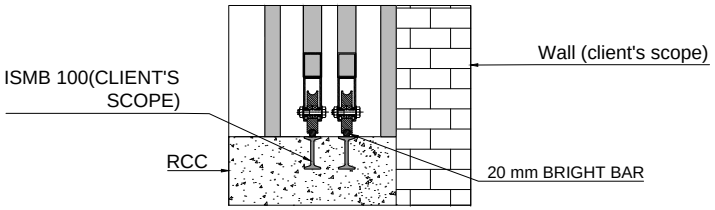

INSIDE ELEVATION




PLAN




DETAIL VIEW OF B




DETAIL VIEW OF A

TOLERANCE - ±10mm

NOTE:-
1.ALL REQUIRED CIVIL WORK BE IN CLIENTS SCOPE.
2.ONE COAT OF RED OXIDE & TWO COAT OF APPROVED RAL SHADE WILL BE GIVEN TO THE GATE.

| CLEAR WIDTH | CLEAR HEIGHT | QUANTITY. |
|---|---|---|
| 9000mm | 2000mm | 01 NOS |

This drawing & design is the property of NIHVA TECHNOLOGIES. Not to be sold or copied to any other concern.

TITLE: TELESCOPIC 2 LEAF SLIDING GATE

| | NAME | SIGN | DATE |
|---|---|---|---|
| DRAWN | SURAJ | | 14-11-2018 |
| CHECK | PRADEEP | | 14-11-2018 |
| APPRD. | R.D | | 14-11-2018 |

NIHVA TECHNOLOGIES PVT. LTD.
NIHVA TECHNOLOGIES PVT. LTD. PUNE
Tel : 020 66304033
Email:- info@nihva.com
Website:- www.nihva.com

CLIENT -SHILPA MEDICARE

PROJECT -

SITE LOCATION -DHARWAD.

If any queries contact : design@nihva.com

DWG. NO. : NIHVA/18-19/0178 | REV- 0

ALL DIMENSION ARE IN mm | SCALE: NTS | WT: | SHEET: 01 OF 01