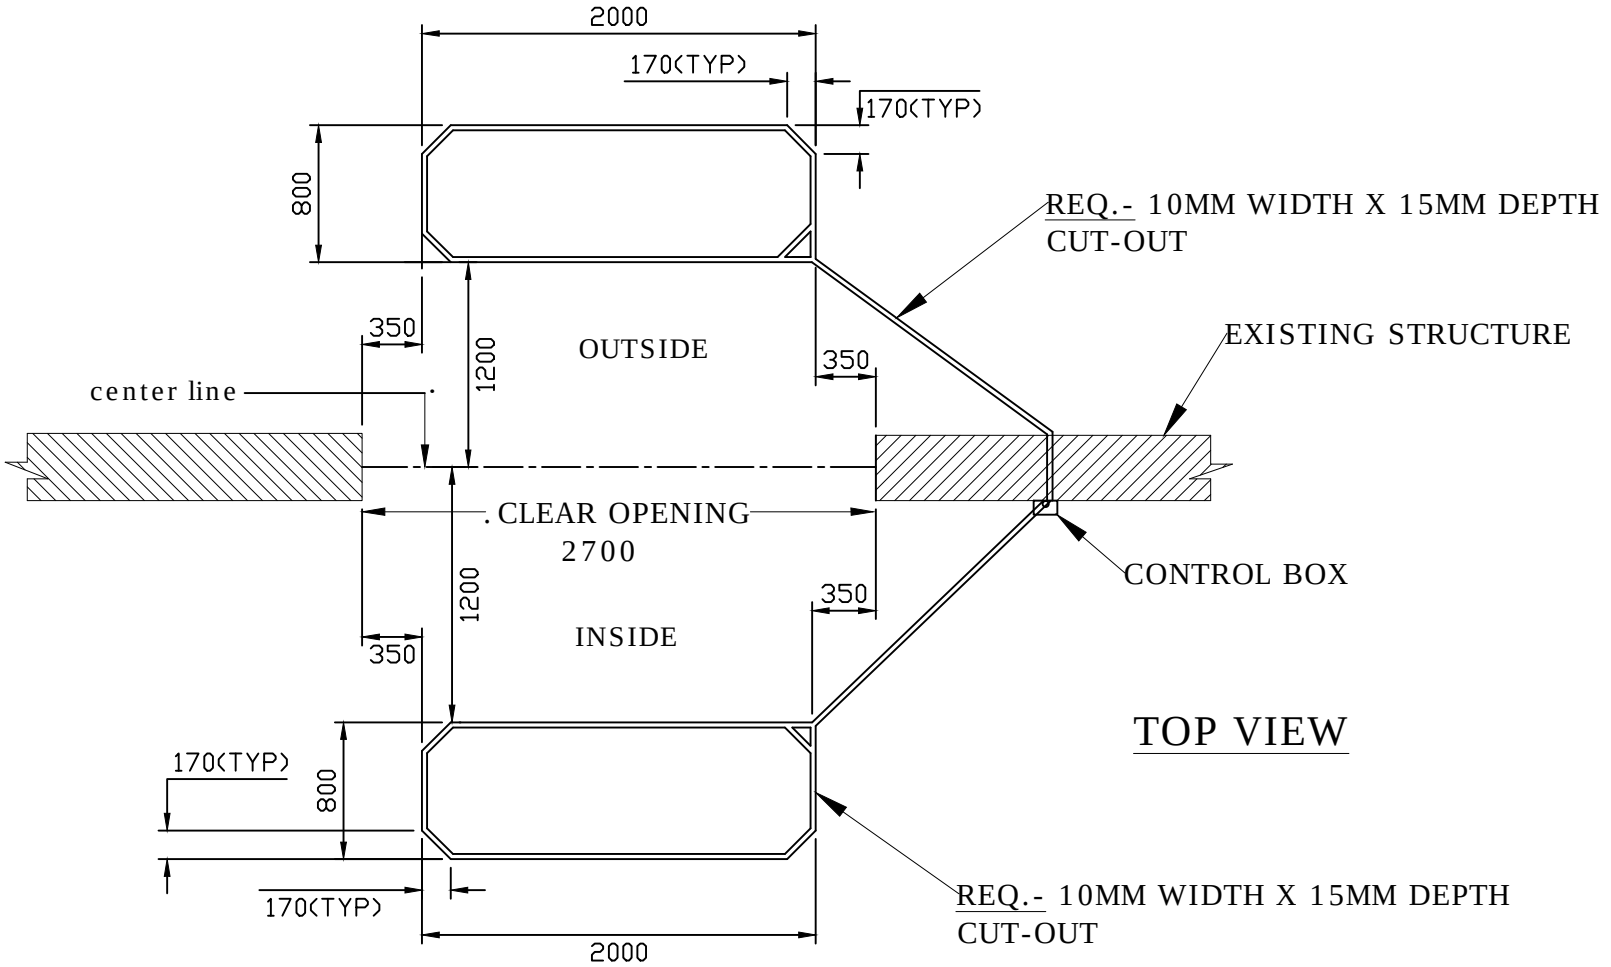


CLEAR WIDTH (CW)	CLEAR HEIGHT (CH)	QUANTITY
2700mm	3200mm	2 NOS

This drawing & designing is the property of NIHVA TECHNOLOGIES. Not be sold or copy to any other concern.

TITLE

FLOOR CUT-OUT FOR LOOP DETECTOR FOR SECTIONAL DOOR

CLIENT APPROVAL

ALL DIMENSION ARE IN mm

	NAME	SIGN	DATE
DRAWN	SURAJ		20/01/18
CHECK	SHEKHAR		20/01/18
APPRD.	SHEKHAR		20/01/18
ENG			
MFG			
Ref. No.			

NIHVA TECHNOLOGIES PVT. LTD.

NIHVA TECHNOLOGY PVT. LTD. PUNE
Tel : 020 66304033
Email:- info@nihva.com
Website:- www.nihva.com

CLIENT - FERRERO INDIA PVT. LTD

PROJECT- FERRERO INDIA PVT. LTD

SITE -BARAMATI

DWG. NO. - NIHVA/16-17/0337 | REV. :- 0

SCALE: NTS. | WT: | SHEET: 01

If any queries contact : design@nihva.com