

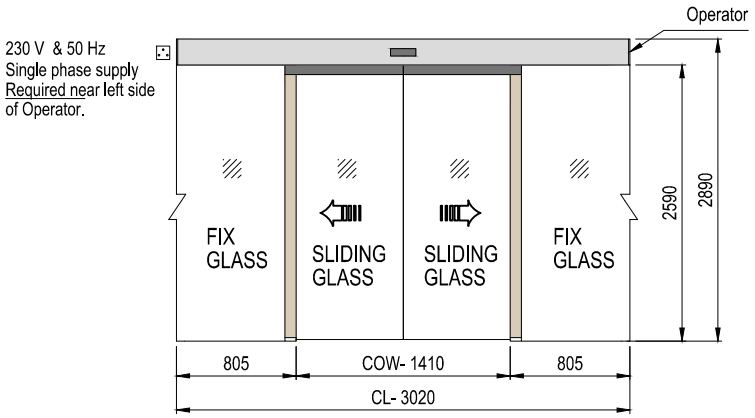



Inside Elevation

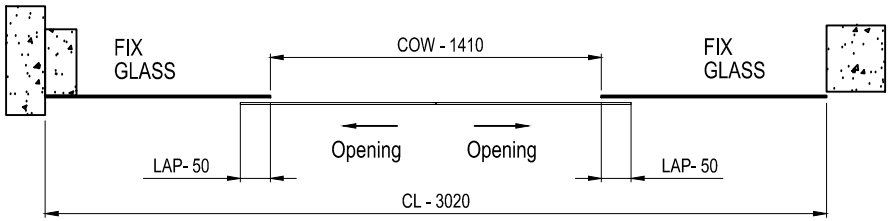

Closed Condition

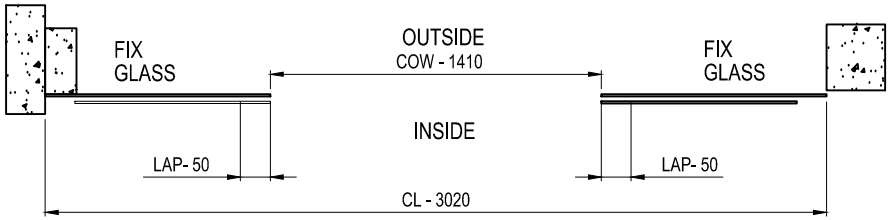

Open Condition

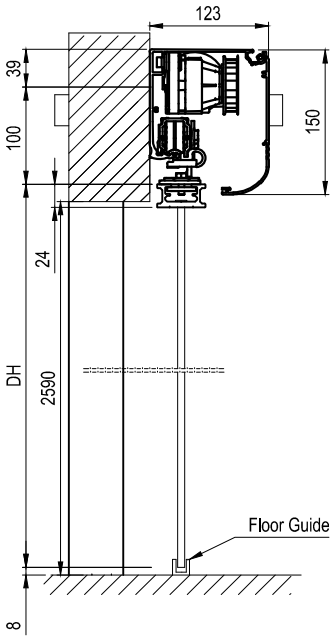

Door Size			
Sr. No.	Clear Open Width	Clear Open Height	Quantity
1	1410	2590	1

Glass Type- 10mm Toughened

REV NO	DATE	DRAWN	REMARK
R01	02.03.20	P.A	1. SIZES CHANGE

NOTE-
1. ALL REQUIRED CIVIL WORK WILL BE IN CLIENTS SCOPE.

TOLERANCE:- ± 05mm

NIHVA TECHNOLOGIES PVT. LTD.
NIHVA TECHNOLOGIES PVT. LTD. PUNE
Website:- www.nihva.com
Email:- info@nihva.com
TEL :020 66304033

TITLE:

AUTOMATIC SLIDING GLASS

CLIENT'S APPROVAL :

CLIENT - SAWANT GROUP OF INDUSTRIES

PROJECT -

SITE LOCATION - CHAKAN

DWG. NO. : NIHVA/19-20/0092			REV. : R01
SCALE: NTS	WT:		SHEET:1 OF 1
DRAWN	P.A		17.09.2019
CHECK	G.J		17.09.2019
APPROVED			

IF ANY QUERIES CONTACT:- design@nihva.com

NOTE: ALL DIMENSIONS ARE IN mm

THIS DRAWING & DESIGN IS THE PROPERTY OF NIHVA TECHNOLOGIES. NOT TO BE SOLD OR COPIED TO ANY OTHER CONCERN.