SECTION A-A

SECTION B-B

Face of steel/℄ Mullion 16457
℄ Mullion/℄ Mullion 16582
(℄ Mullion/℄ Mullion 16582)
℄ Mullion/℄ Mullion 16582
℄ Mullion/℄ Mullion 16582
℄ Mullion/Face of steel 16457
E
F
Clear width 99000

SECTION C-C

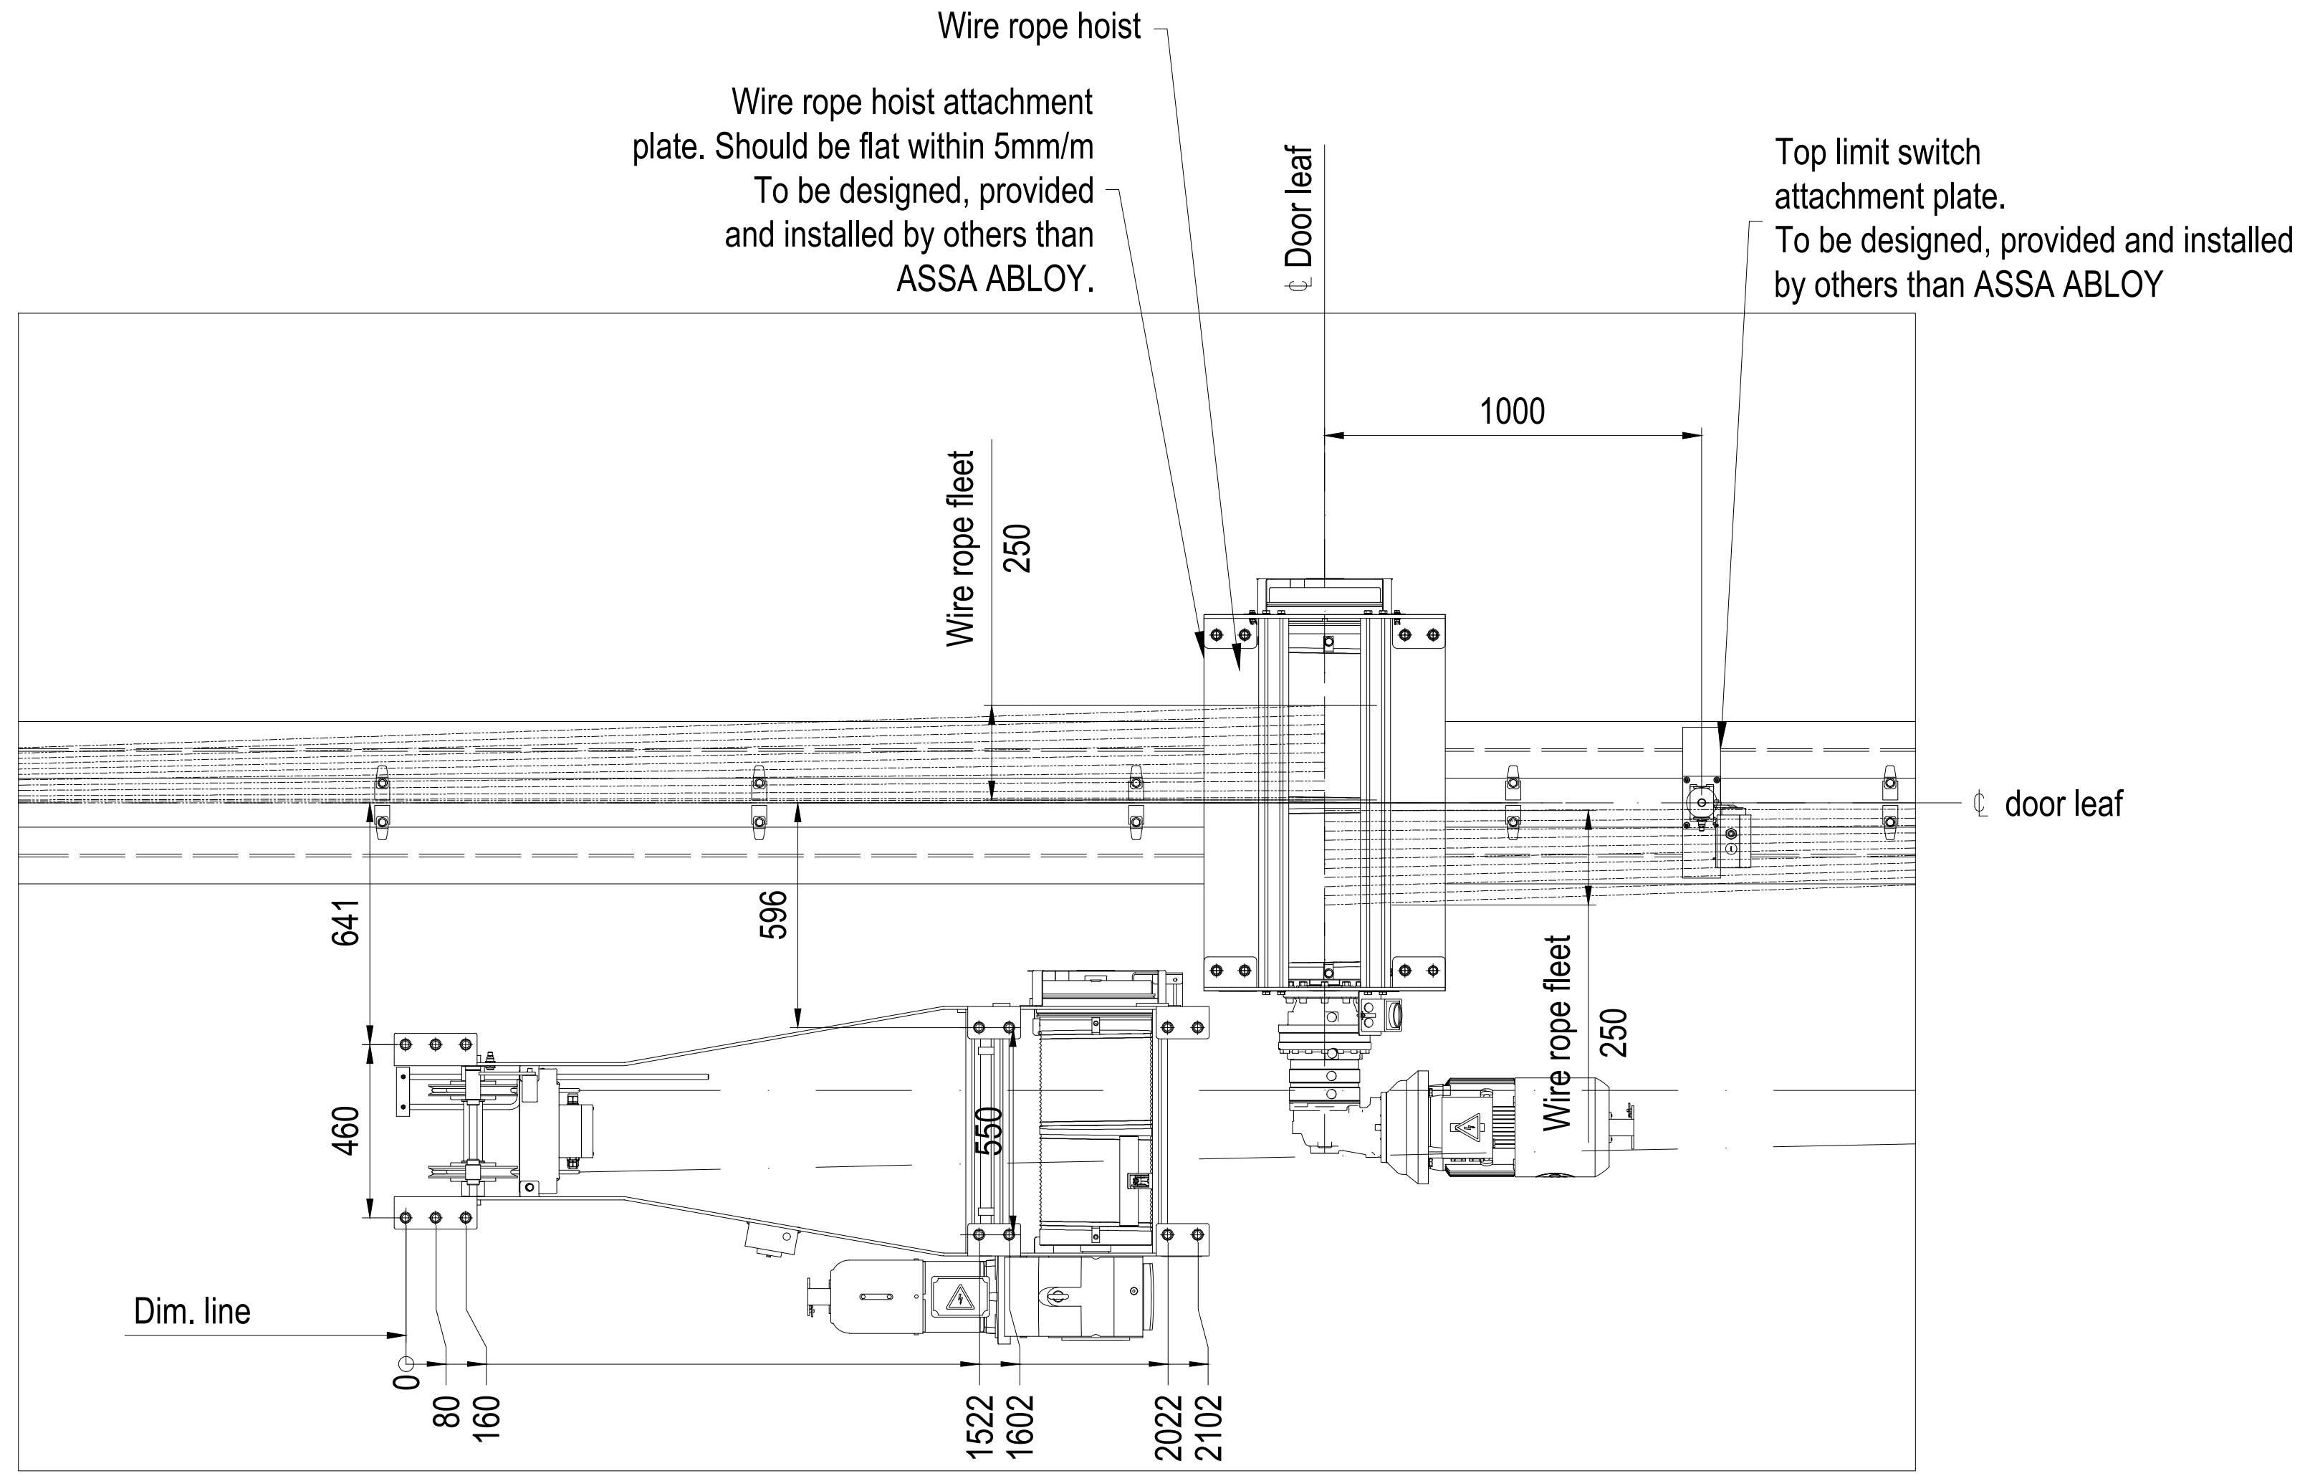

DETAIL B, SCALE (1:20)

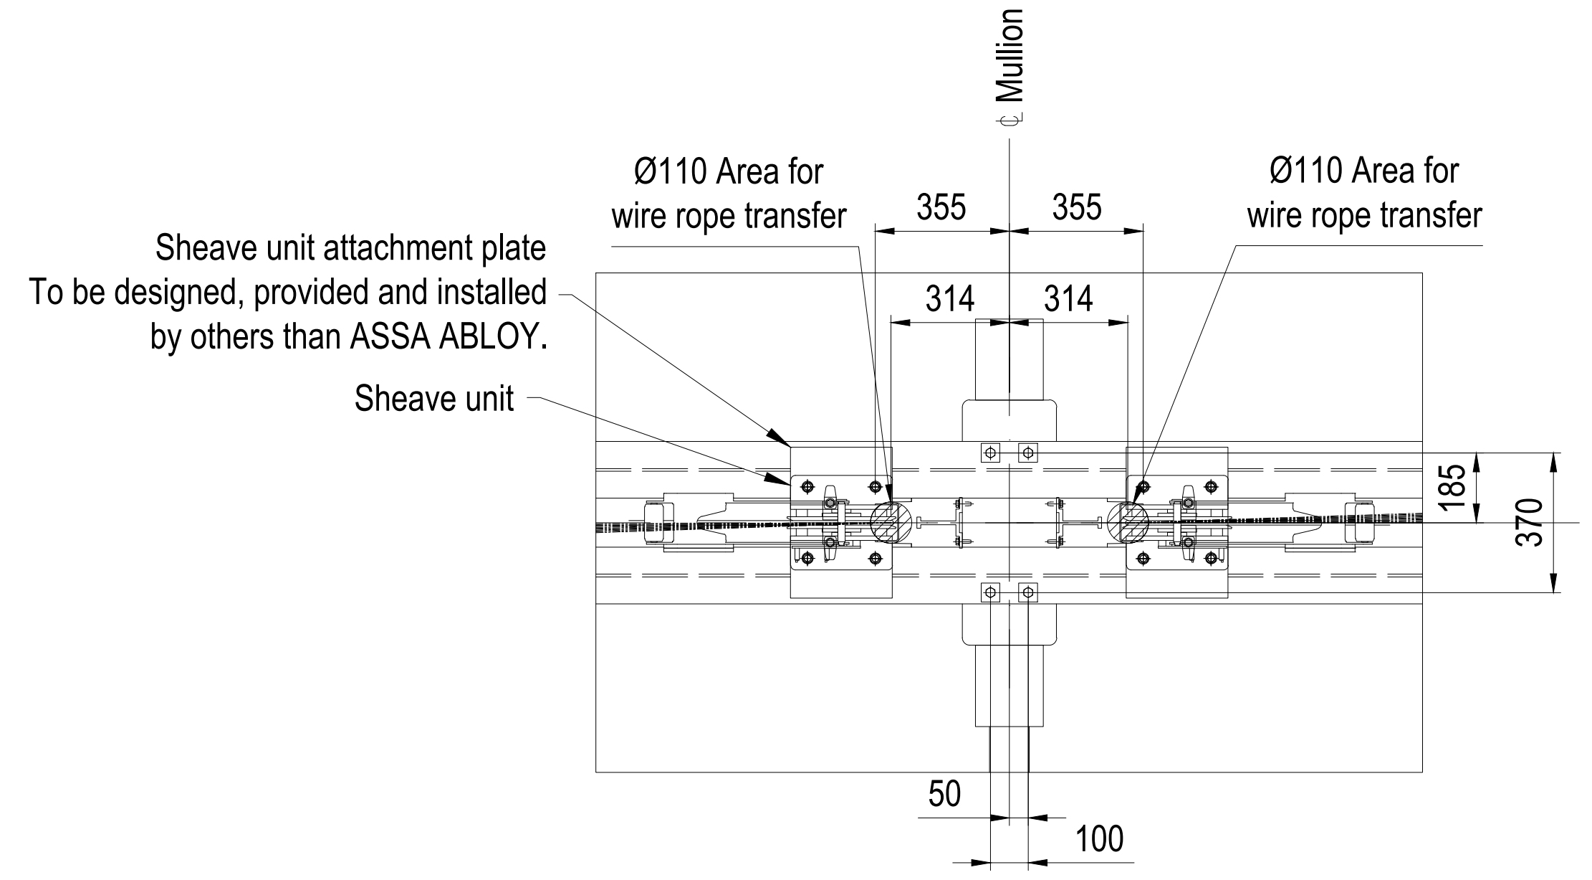

DETAIL C, SCALE (1:20)

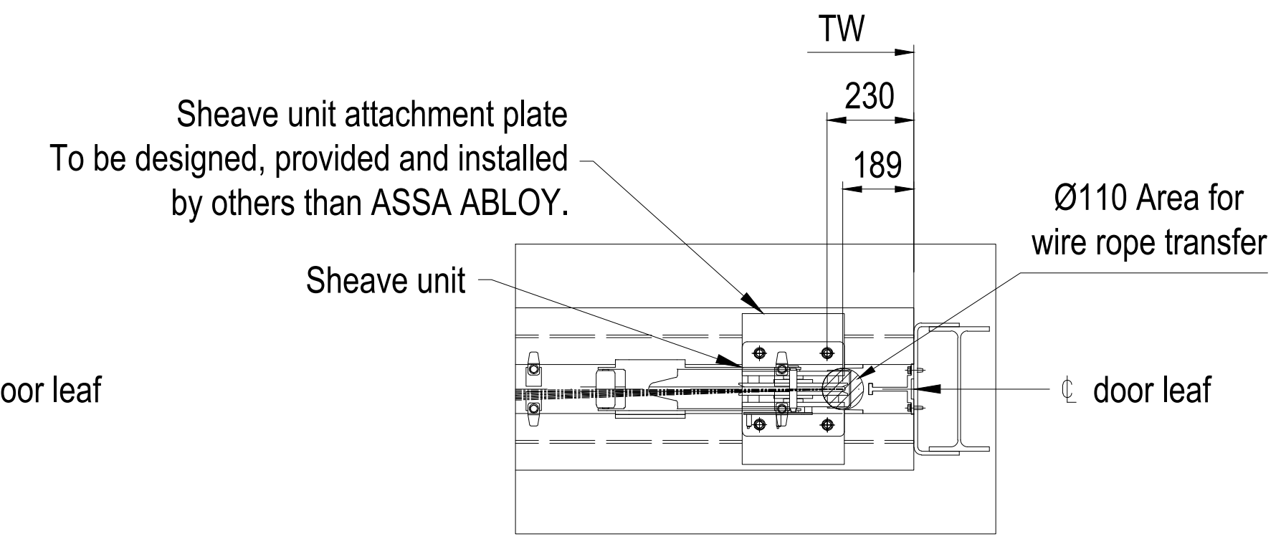
TW
230
189
Sheave unit attachment plate
To be designed, provided and installed
by others than ASSA ABLOY.
Ø110 Area for
wire rope transfer
Sheave unit
℄ door leaf

DETAIL D, SCALE (1:20)

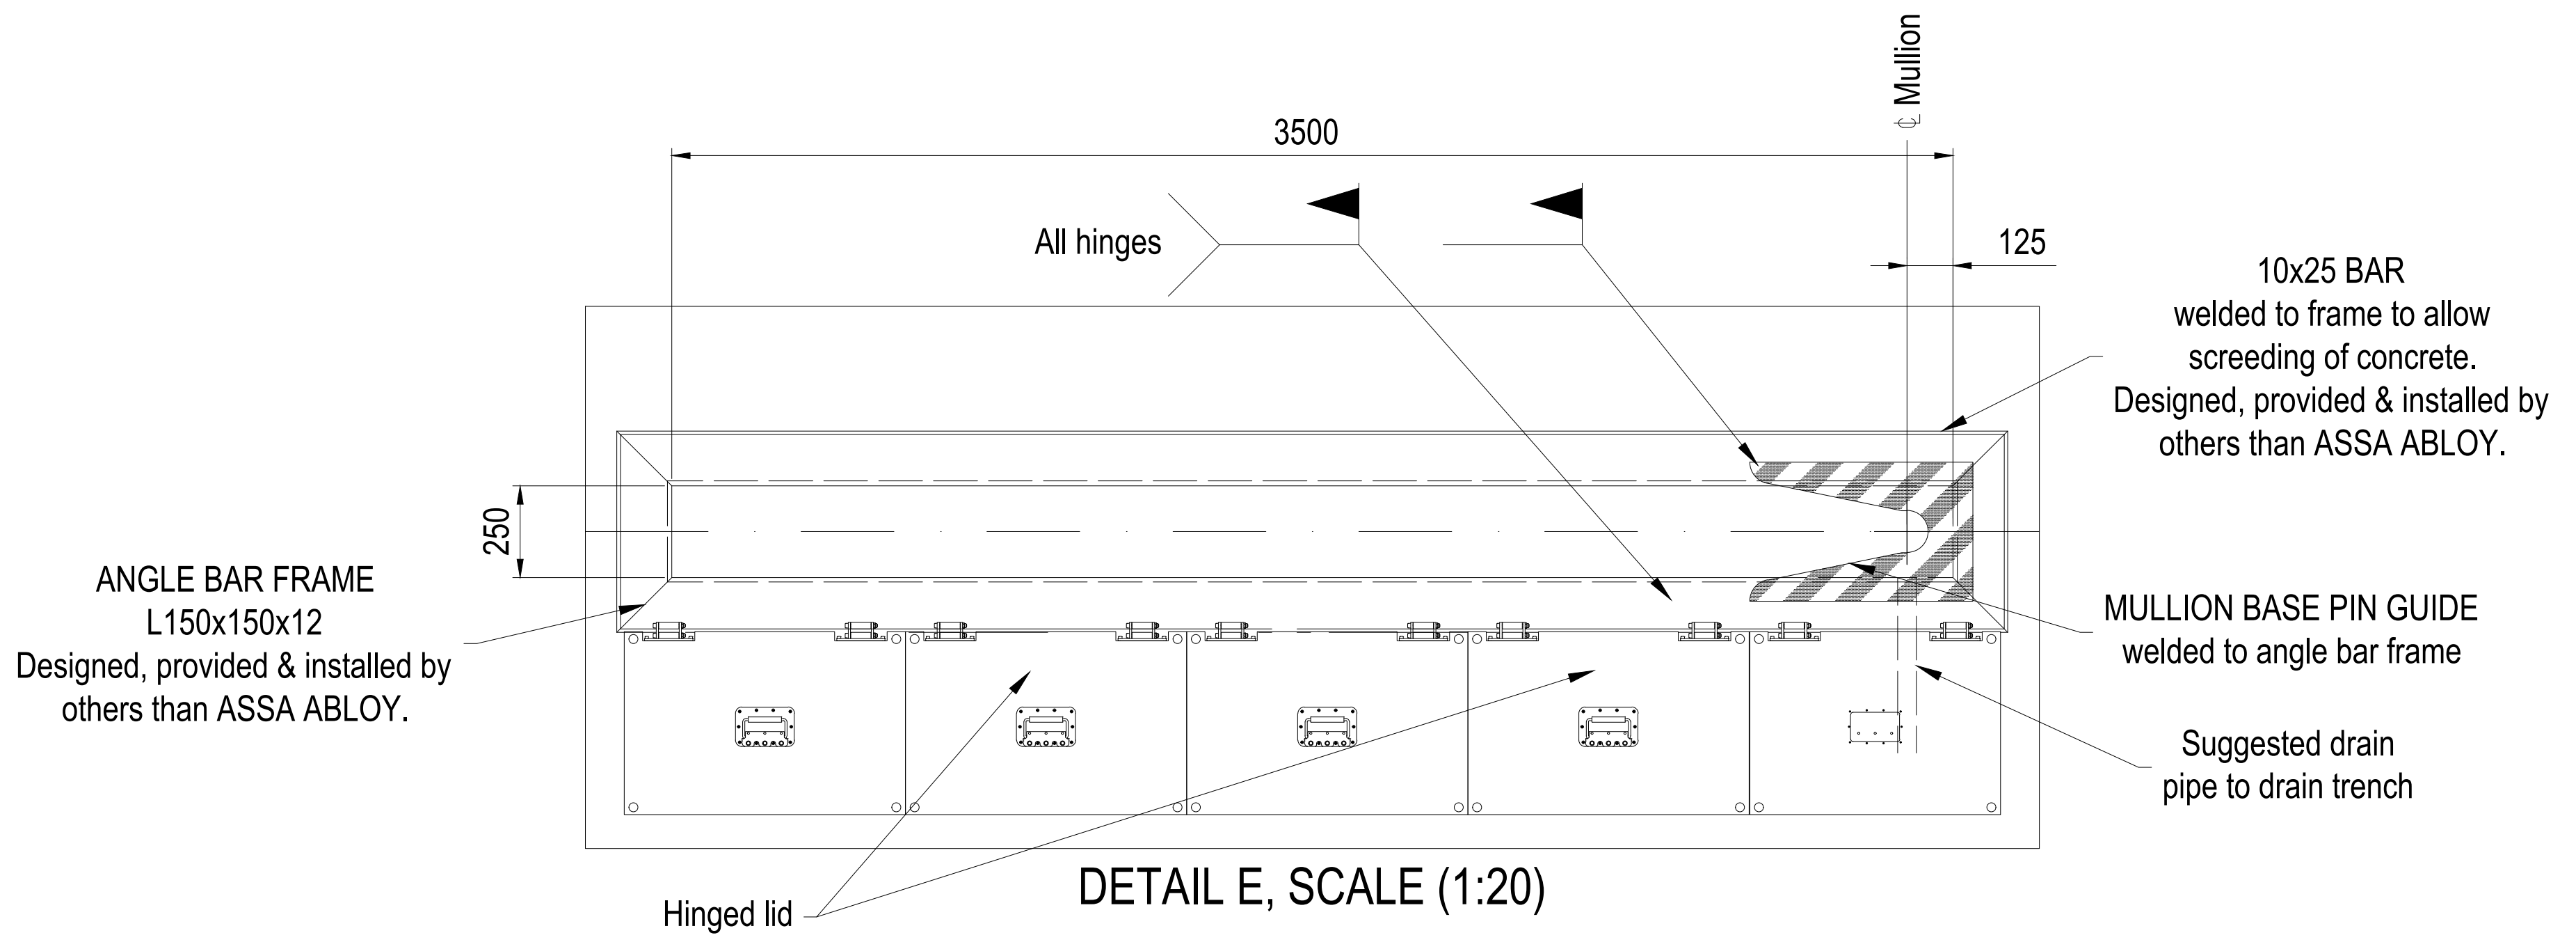

DETAIL E, SCALE (1:20)

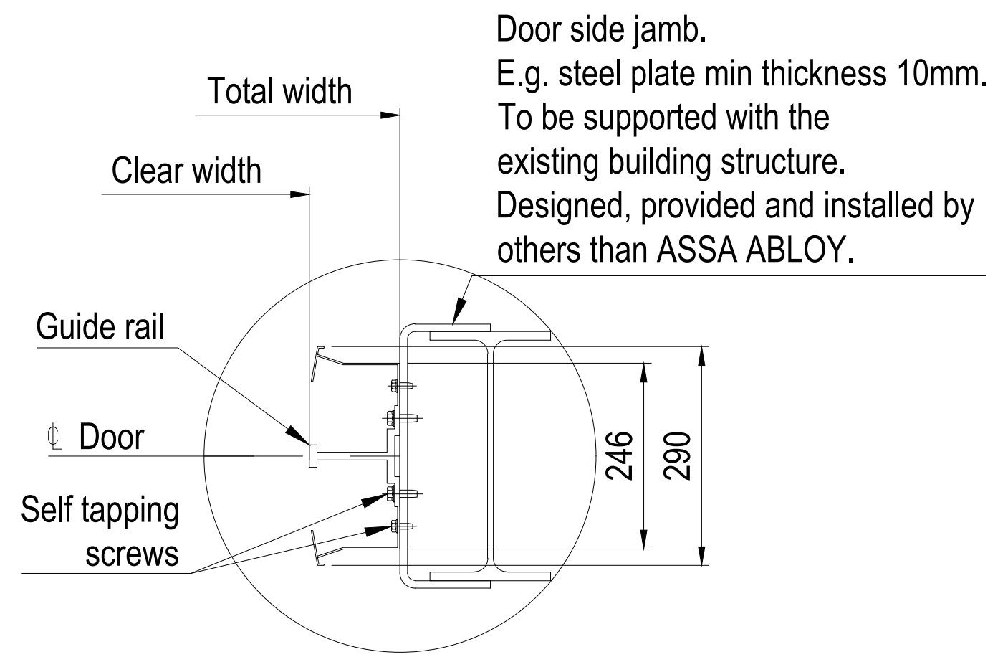

DETAIL F, SCALE (1:10)

DOOR IDENTITY NUMBER: 84801001

LOAD DIAGRAM & NOTES, ref. to drwng. no. 77450

INTERFACE, SECTIONS ref. to drwng. no. 77449

INTERFACE, ELEVATION ref. to drwng. no. 77447

DESIGNED EB		SIZE A1F	SCALE 1:100	GMR Aero Technic Hangar2 India Megadoor 99000x14700/14000 Interface, Plan views	PLOT DATE
CODE 84801		If not otherwise stated: Tolerances ISO 2768-m EN ISO 13920-B Cutting class ISO 9013-442 Weld class ISO 5817-C Surface finish Smooth raw surface			
ITEM NO					
DATE 2022-08-30					
ASSA ABLOY				DRAWING NO 77448	REVISION --

This document is the property of ASSA ABLOY Entrance Systems AB
and shall not without our written permission be copied, imparted to a
third party or used for any other unauthorized purpose.