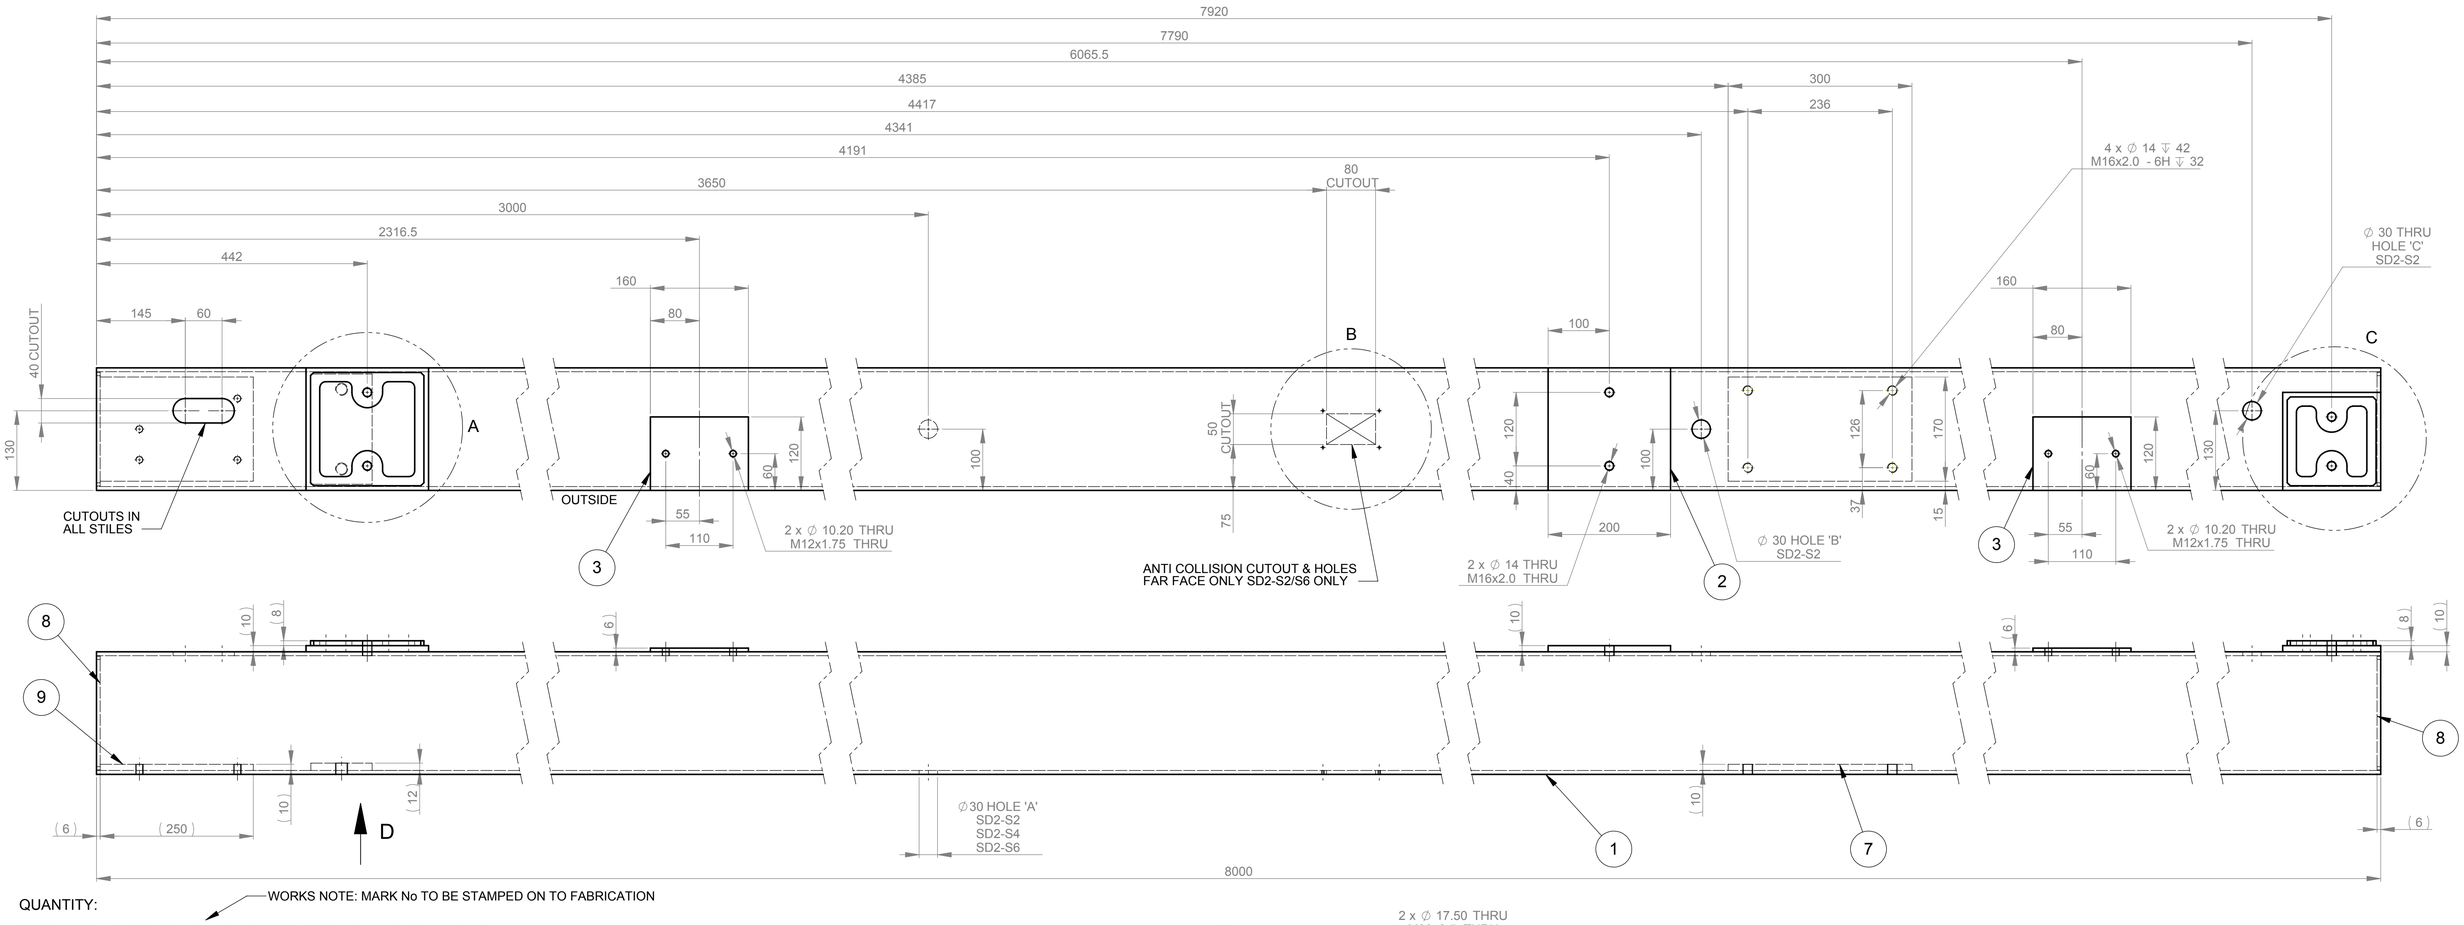


QUANTITY: (WORKS NOTE: MARK No TO BE STAMPED ON TO FABRICATION)

P4-SD2-S2 - 6-OFF REQD - AS DRAWN - WITH Ø30 HOLES 'A' 'B' 'C'. & ANTI COLLISION CUTOUT.
P4-SD2-S4 - 4-OFF REQD - AS DRAWN - WITH Ø30 HOLE 'A'. WITHOUT ANTI COLLISION CUTOUT
P4-SD2-S6 - 2-OFF REQD - AS DRAWN - WITH Ø30 HOLE 'A'. & ANTI COLLISION CUTOUT.

FINISH:

PRIOR TO FABRICATION


1. SHOTBLAST TO S.A. 2.5
2. APPLY 25u DFT K232 ZINC RICH EPOXY PRE-FAB PRIMER


AFTER FABRICATION

3. APPLY 75u DFT EPOXY ZINC RICH EPOXY PRIMER ("HEMPADUR ZINC 15360" BY HEMPEL)
4. APPLY 200u DFT TWIN PACK, HIGH BUILD EPOXY MIO COATING. ("HEMPADUR MASTIC 45881" BY HEMPEL)
5. APPLY 50u DFT TWIN PACK, ACRYLIC POLYURETHANE GLOSS COAT. ("HEMPATHANE 55210" BY HEMPEL) COLOUR - GENTIAN BLUE, RAL 5010.


SCALE 1:5 U.S.O.

ALL WELDS TO BE 6mm FILLET OR
FULL STRENGTH BUTT WELDS UNLESS STATED OTHERWISE

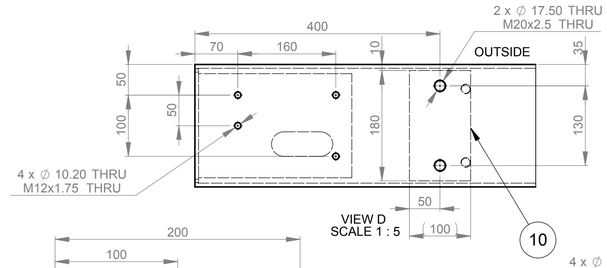


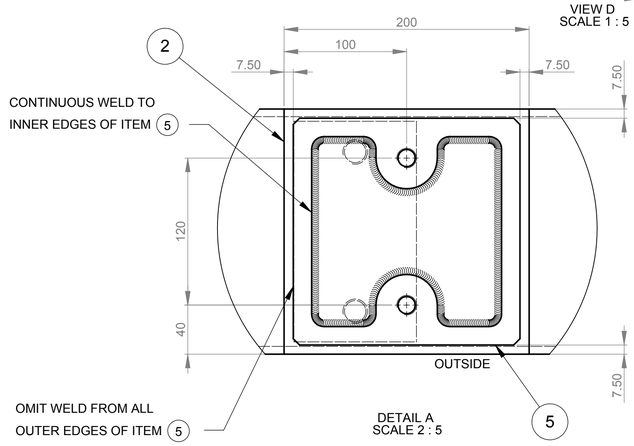

DETAIL A
SCALE 2 : 5

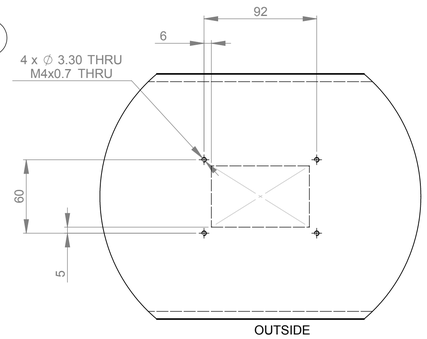

DETAIL B
SD2-S2
SD2-S6
SCALE 2 : 5

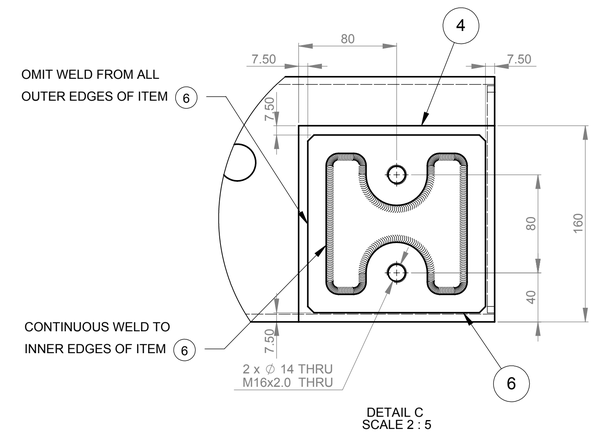

DETAIL C
SCALE 2 : 5

ITEM	MATERIAL	LENGTH	QTY	TOTAL QTY	PART #
10	FLAT 100x12	180	1	12	
9	FLAT 250x10	170	1	12	
8	6mm PROFILE PLATE - C6627-PR107		2	24	-
7	FLAT 300x10	170	1	12	
6	8mm PROFILE PLATE - C6627-PR105		1	12	-
5	8mm PROFILE PLATE - C6627-PR104		1	12	-
4	FLAT 160x10	160	1	12	
3	FLAT 120x6	160	2	24	
2	FLAT 200x10	200	2	24	
1	SHS 200x200x6.3 Gr355J2H-EN10210	8000	1	12	

DRAWING NUMBER C6627-122

TOTAL WEIGHT (kG) 320.43

GENERAL NOTES
1. ALL STEELWORK TO CONFORM TO BS EN 10025:2004
2. ALL WELDING TO CONFORM TO AWSD1.1/D1.1M 2006
3. ALL STEELWORK TO BE MIN GRADE S275JR UNLESS OTHERWISE STATED
4. TOLERANCE :- ±0.25 & ±0°30'
5. ALL DIMENSIONS IN mm UNLESS OTHERWISE STATED

INSPECTION CATEGORY	
DIMENSION	D
WELDING	D
FITTING	-
FINISH	D

DRAWN	CRA
DATE	05/01/2009

Esavian
Jewers Doors Limited
Stratton Business Park
Normandy Lane
Biggleswade
Beds SG18 8QB
United Kingdom
Tel: +44(0) 1767 317090
Fax: +44(0) 1767 312305
E-mail: postroom@jewersdoors.co.uk
Web Site: www.jewersdoors.co.uk

The Property of this Drawing Sheet and Design is vested in Jewers Doors Ltd. It must not be reproduced in any way or passed to third parties without their written consent.

DRAWING TITLE: STILE P4-SD2-S2/4/6

PROJECT REF: NAKILAT SHIP REPAIR YARD P4 - ASSEMBLY SHOP TYPE SD2

SHEET SIZE A1

ISSUE	DRAWN	CHECKED	DATE	MODIFICATION
A	CRA	SPB	28/1/09	FIRST ISSUE

DRAWING NUMBER C6627-122