



PRODUCED BY AN AUTODESK EDUCATIONAL PRODUCT

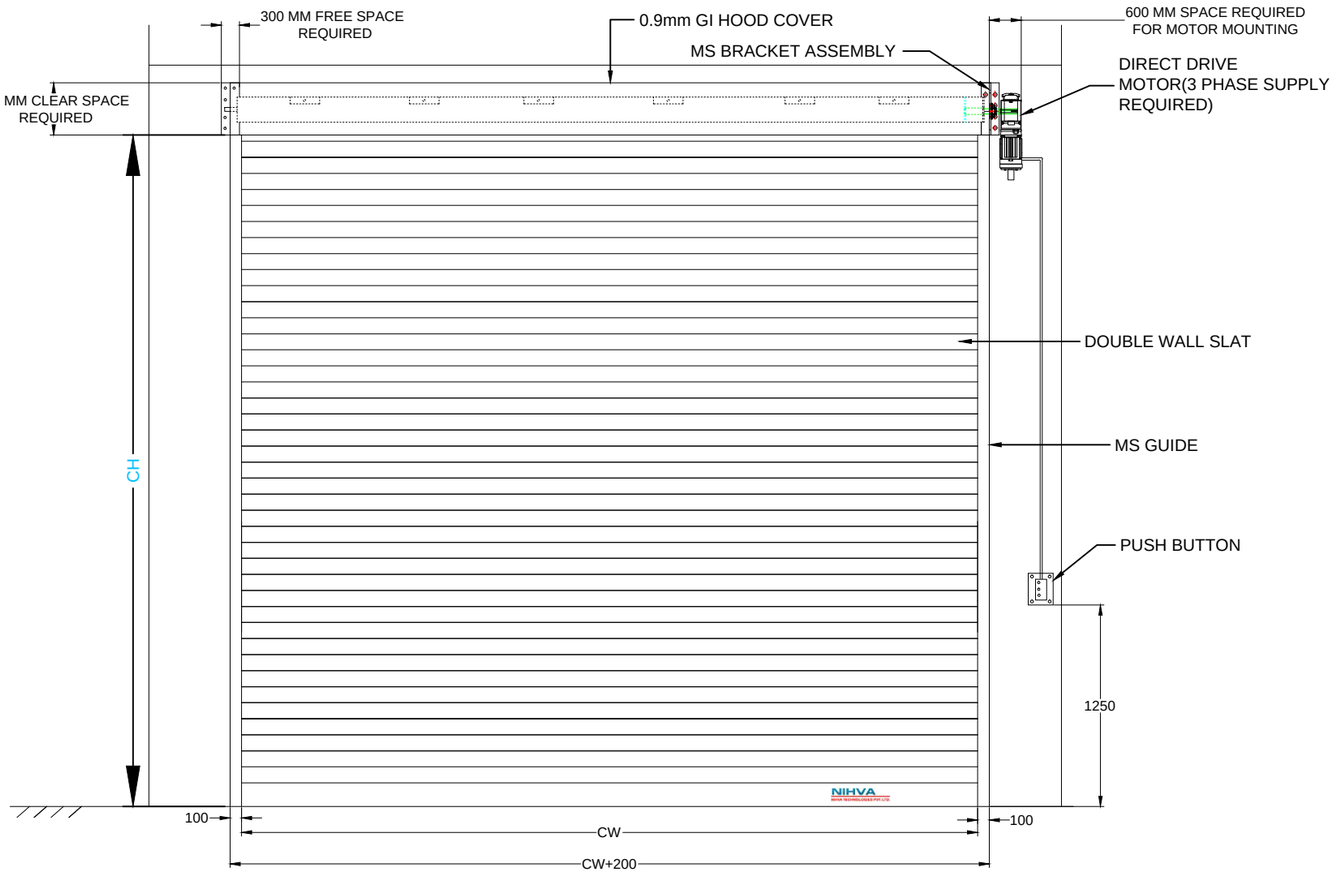

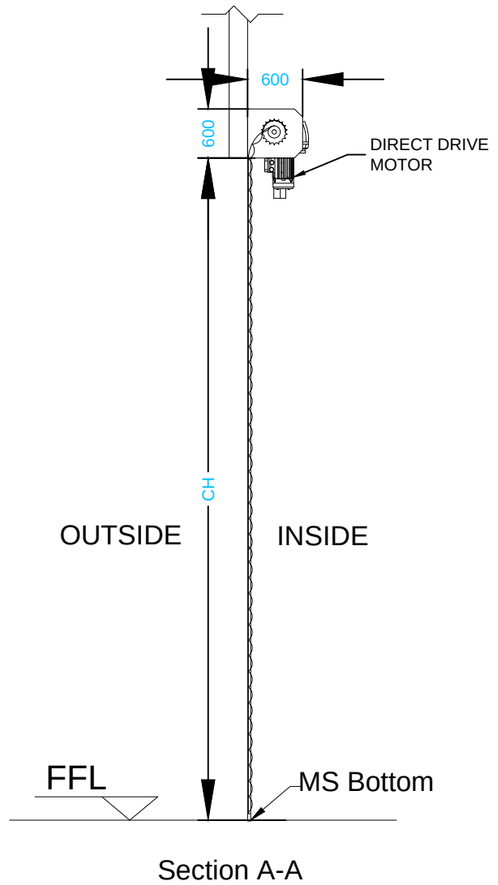


Section A-A

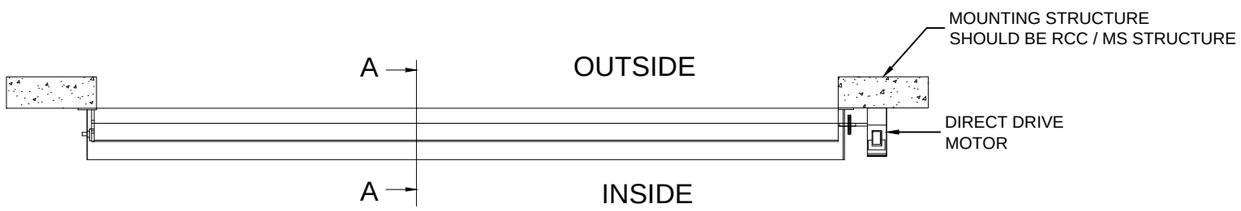

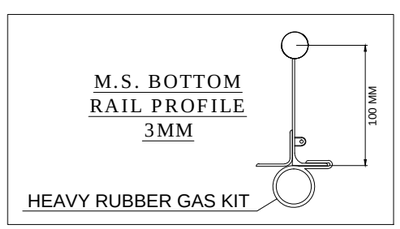

Main Slats
Double Wall Rolling Shutter

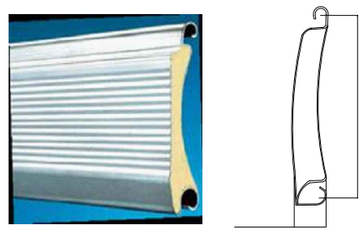

COLOR OF SLATS & SHUTTER -RAL9002 (GRAY WHITE)

DIMENSION :

CLEAR WIDTH	CLEAR HEIGHT	QUANTITY
4600 mm	3900 mm	2 NOS

NOTE:-

1.STRUCTURE FOR SHUTTER WILL BE IN CLIENT'S SCOPE.
2. 3 PHASE SUPPLY SHOULD BE PROVIDED.

NIHVA TECHNOLOGIES PVT. LTD.
NIHVA TECHNOLOGIES PVT. LTD. PUNE
Email:- info@nihva.com
Website:- www.nihva.com

TITLE:

DOUBLE WALL ROLLING SHUTTER
01. LGF south side
02. LGF south side

CLIENT'S APPROVAL :

CLIENT - AJAY KALE AND ASSOSIATE

PROJECT -

SITE LOCATION - PIRANGUT

DWG. NO. : NIHVA/21-22/CLT/280

SCALE: NTS	WT:	SHEET:01 OF 02

DRAWN BY: G.P.	DATE: 23-12-2021
CHECKED BY: A.K.	DATE: 23-12-2021
APPROVED BY :	

If any queries contact : design@nihva.com

NOTE: ALL DIMENSIONS ARE IN mm

THIS DRAWING & DESIGN IS THE PROPERTY OF NIHVA TECHNOLOGIES, NOT TO BE SOLD OR COPIED TO ANY OTHER CONCERN.
PRODUCED BY AN AUTODESK EDUCATIONAL PRODUCT
PRODUCED BY AN AUTODESK EDUCATIONAL PRODUCT