


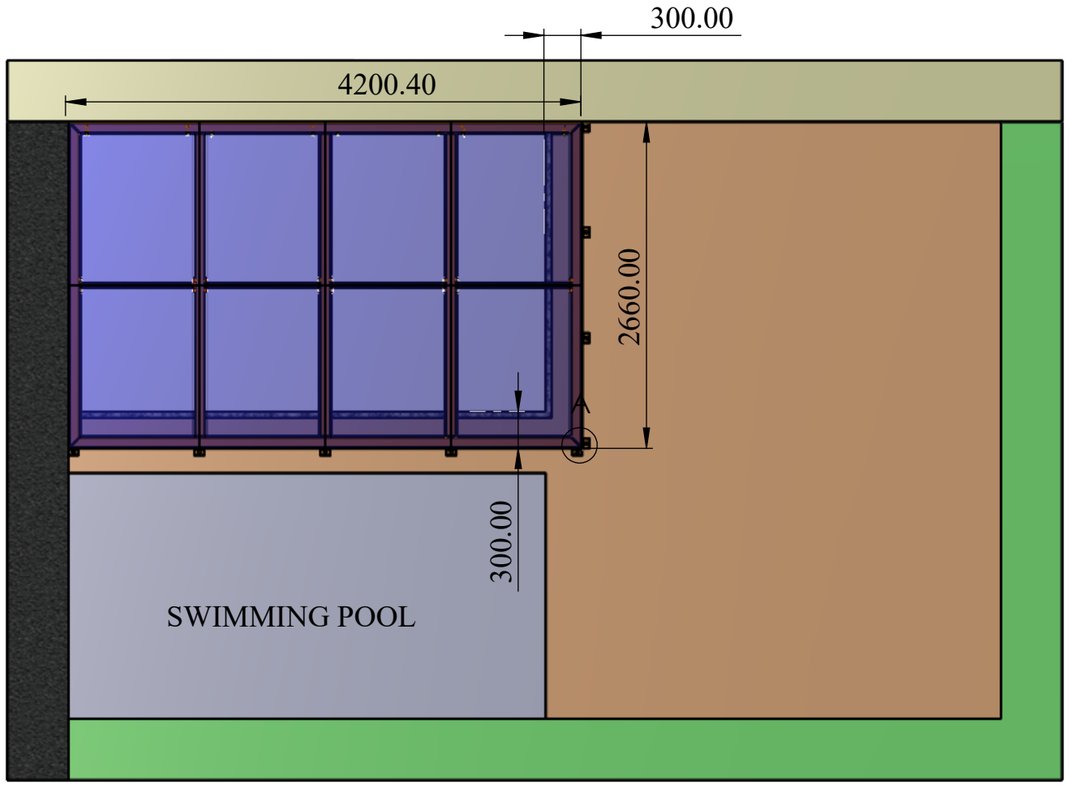


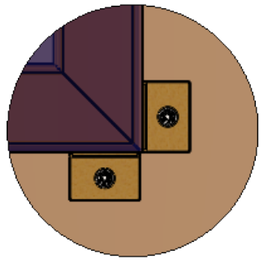

DETAIL A
SCALE 1 : 7

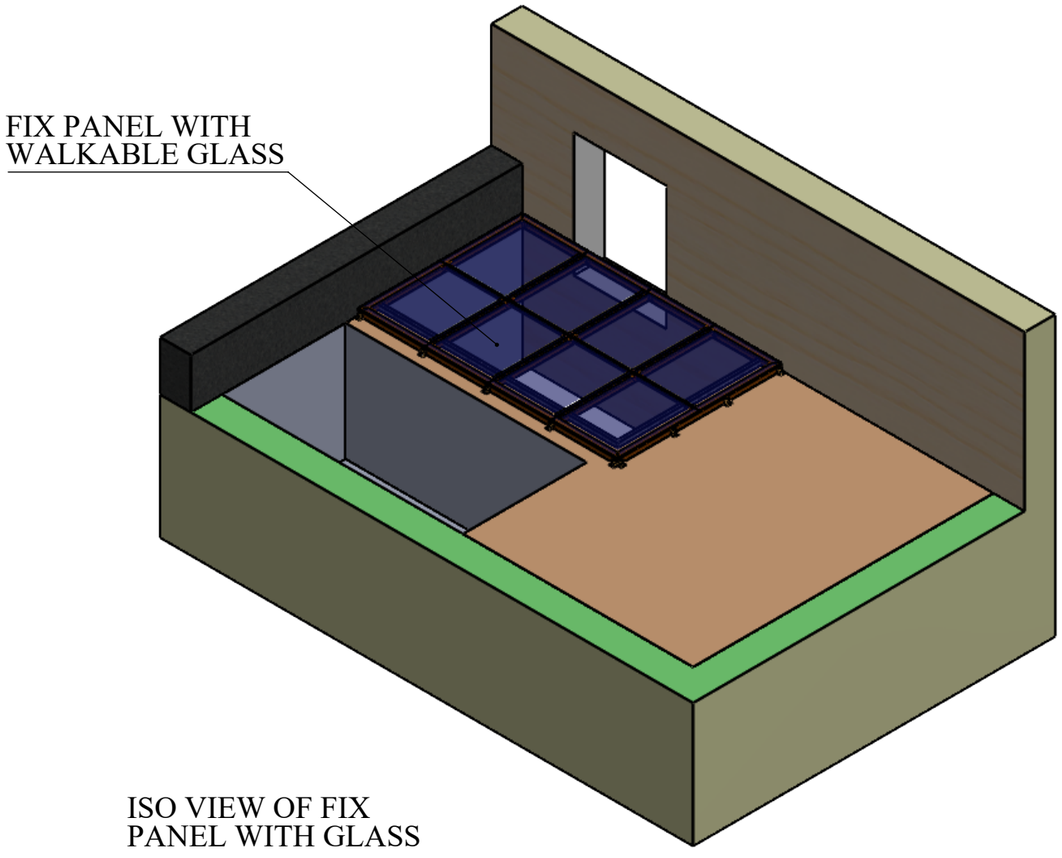



ISO VIEW OF FIX
PANEL WITH GLASS

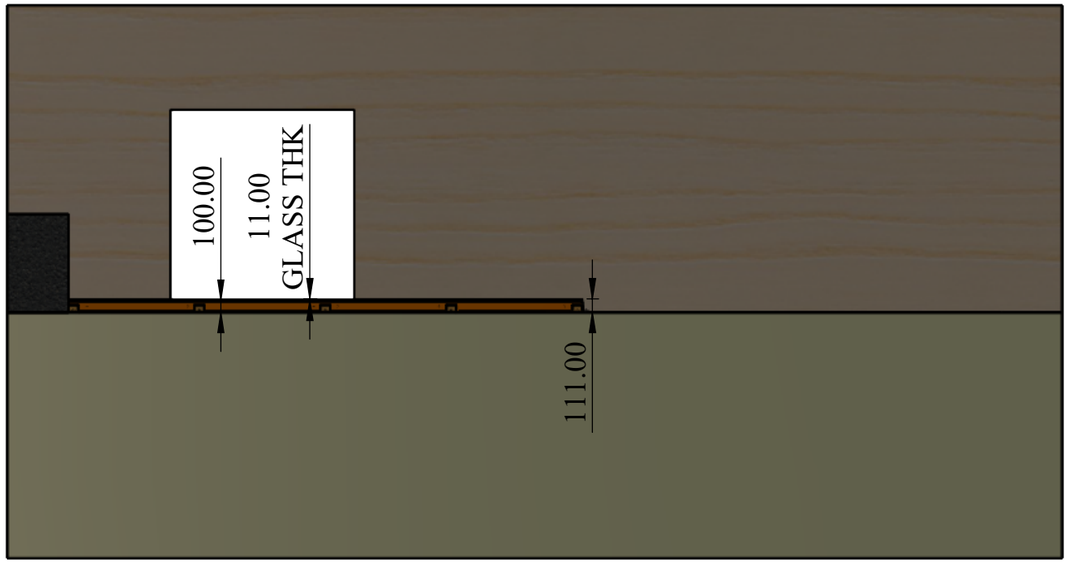


TITLE - ROOF AUTOMATION				NIHVA TECHNOLOGIES PVT.LTD.PUNE	
DWG NO - NTPL-283-PM-001-00-00-00				Website - www.nihva.com	
	NAME	SIGNATURE	DATE	PROJECT NO - NTPL-283-PM	
DRAWN	V.W		17-06-2025	PRODUCT - RETRACTABLE ROOF	WEIGHT -
CHK'D	S.W.		17-06-2025	SITE LOCATION - LUCKNOW	REVISION -
APPV'D	V.T.		17-06-2025	MATRIAL SPECIFICATION-	QTY - 1
if any queries contact - supportautomation@nihva.com				PROJECTION METHOD:	SCALE :
ALL DIMENSION ARE IN mm			A3		SHEET 1 OF 8

ITEM NO.	PART NUMBER	DESCRIPTION	QTY.
1	FIX PANEL	MS-100X100X5MM THK	1
2	INTERMEDIATE SUPPORT TUBE 40X40X3MM THK ASM	MS-40X40X3MM THK	4
3	GLASS 1330X1075X11MM THK	GLASS	4
4	GLASS 2 1330X1025X11 MM THK	GLASS	4
5	ANCHOR FASTENING PLATE	MS	9
6	RR_ Anchor Bolt M10x75	STD	17

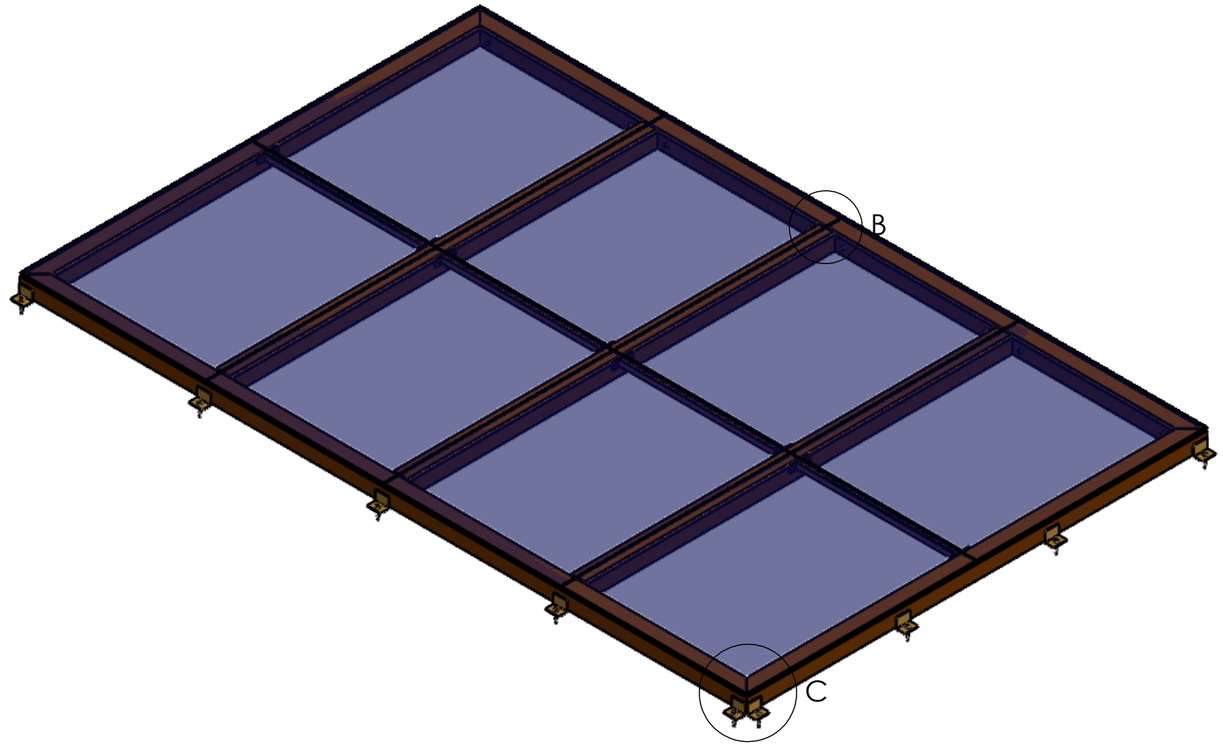


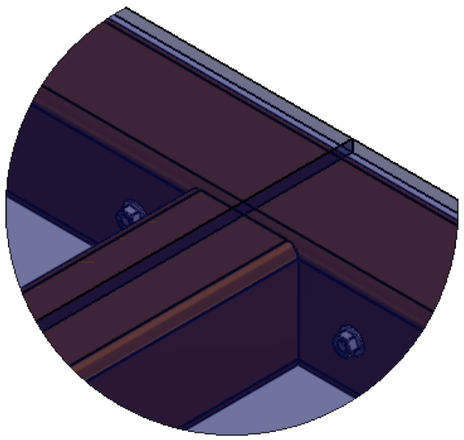

DETAIL B
SCALE 1 : 4

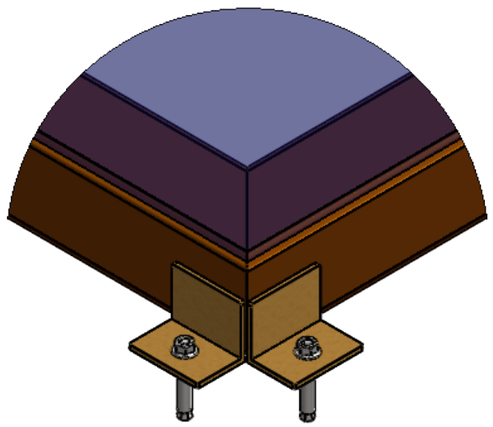



DETAIL C
SCALE 1 : 5

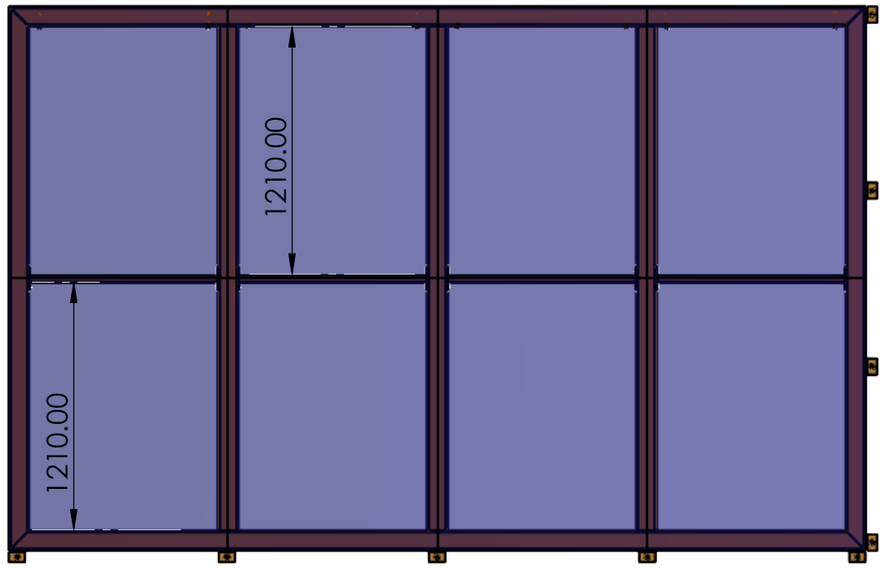


TITLE - ROOF AUTOMATION				NIHVA Technologies Pvt. Ltd. NIHVA TECHNOLOGIES PVT.LTD.PUNE Website - www.nihva.com	
DWG NO - NTPL-283-PM-001-00-00-00					
	NAME	SIGNATURE	DATE	PROJECT NO - NTPL-283-PM	
DRAWN	V.W		17-06-2025	PRODUCT - RETRACTABLE ROOF	WEIGHT -
CHK'D	S.W.		17-06-2025	SITE LOCATION - LUCKNOW	REVISION -
APPV'D	V.T.		17-06-2025	MATRIAL SPECIFICATION-	QTY - 1
if any queries contact - supportautomation@nihva.com				PROJECTION METHOD:	SCALE :
ALL DIMENSION ARE IN mm			A3		SHEET 2 OF 8

ITEM NO.	PART NUMBER	DESCRIPTION	QTY.
1	FIX PANEL	MS-100X100X5MM THK	1

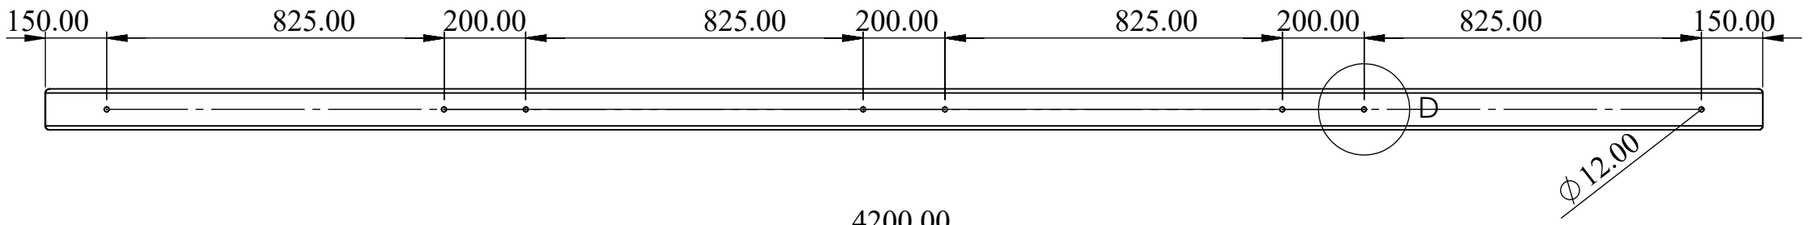

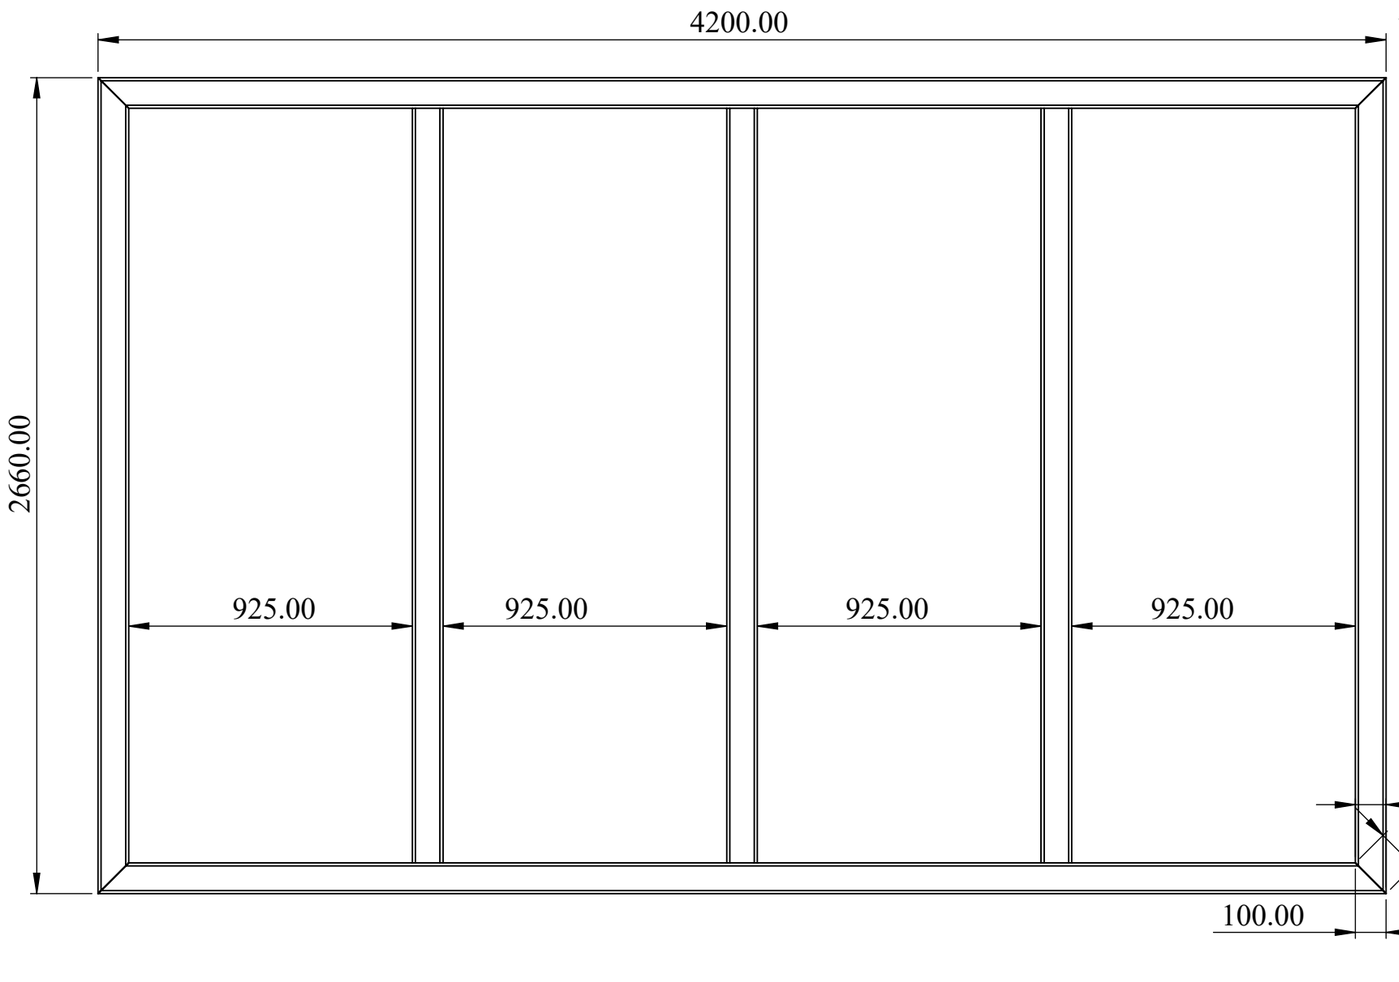

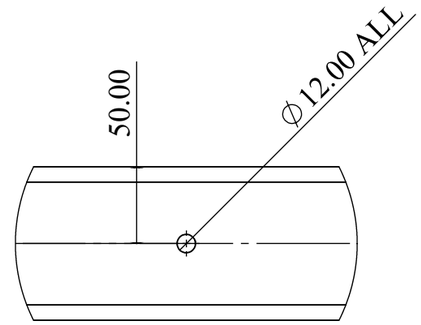



DETAIL D
SCALE 1 : 4

NOTE :
FIX PANEL
MTL - MS 100X100X5MM THK
QTY - 01 No's.

TITLE - ROOF AUTOMATION				NIHVA TECHNOLOGIES PVT.LTD.PUNE Website - www.nihva.com	
DWG NO - NTPL-283-PM-001-01-00-01					
	NAME	SIGNATURE	DATE	PROJECT NO - NTPL-283-PM	
DRAWN	V.W		17-06-2025	PRODUCT - RETRACTABLE ROOF	WEIGHT-298.210KG
CHK'D	S.W.		17-06-2025	SITE LOCATION - LUCKNOW	REVISION -
APPV'D	V.T.		17-06-2025	MATRIAL SPECIFICATION- MS	QTY - 1
if any queries contact - supportautomation@nihva.com				PROJECTION METHOD:	SCALE :
ALL DIMENSION ARE IN mm			A3		SHEET 3 OF 8

ITEM NO.	PART NUMBER	DESCRIPTION	QTY.
1	INTERMEDIATE SUPPORT TUBE 40X40X3MM THK	MS	4

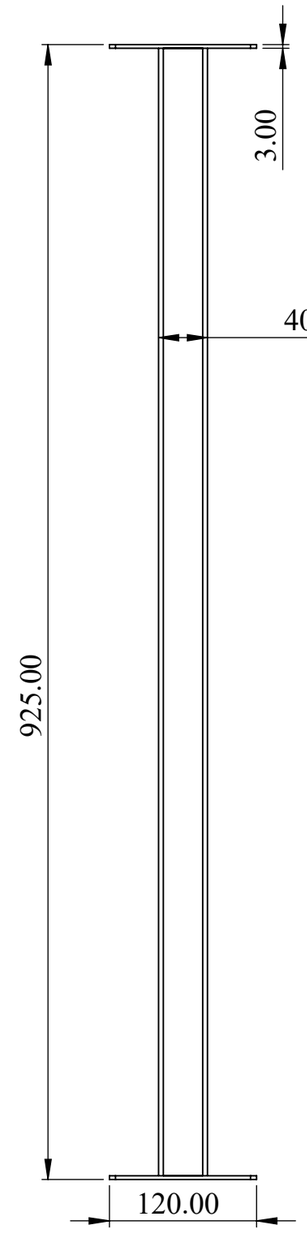


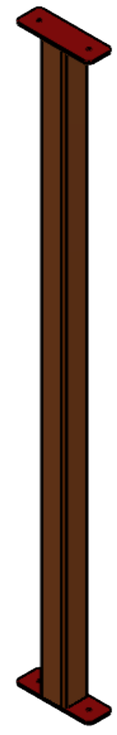


NOTE :
INTEMEDIAT SUPPORT TUBE
40 X40 X 3 MM THK
MTL - MS
QTY- 04 No's.


TITLE - ROOF AUTOMATION				NIHVA TECHNOLOGIES PVT.LTD.PUNE	
DWG NO - NTPL-283-PM-001-02-00-02				Website - www.nihva.com	
	NAME	SIGNATURE	DATE	PROJECT NO - NTPL-283-PM	
DRAWN	V.W		17-06-2025	PRODUCT - RETRACTABLE ROOF	WEIGHT - 3.304
CHK'D	S.W.		17-06-2025	SITE LOCATION - LUCKNOW	REVISION -
APPV'D	V.T.		17-06-2025	MATRIAL SPECIFICATION- MS	QTY - 1
if any queries contact - supportautomation@nihva.com				PROJECTION METHOD:	SCALE :
ALL DIMENSION ARE IN mm			A3		SHEET 4 OF 8

ITEM NO.	PART NUMBER	DESCRIPTION	QTY.
1	GLASS 1330X1075X11MM THK	GLASS	4

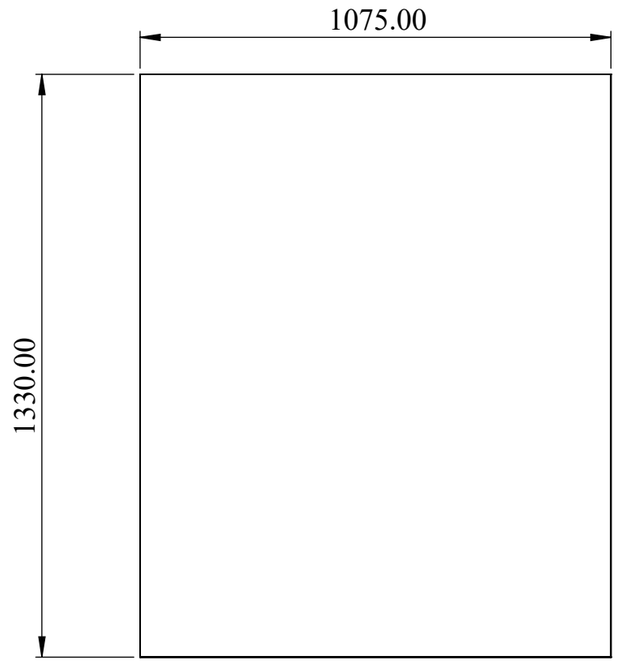

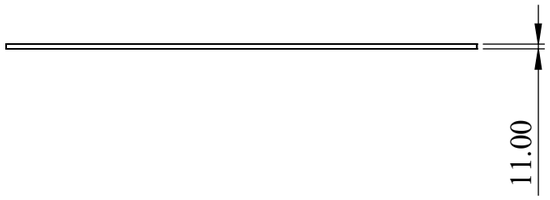



NOTE :
GLASS 1330 X 1075 11 THK
QTY - 4 No's.

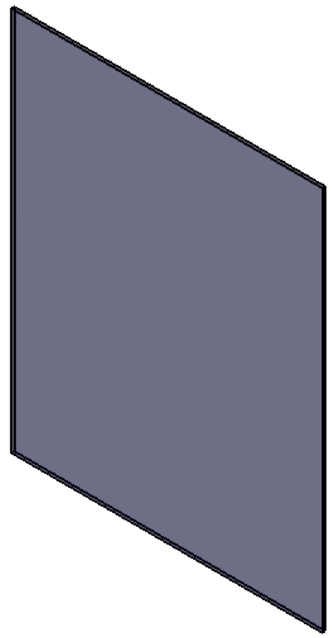


TITLE - ROOF AUTOMATION				NIHVA Technologies Pvt. Ltd.	NIHVA TECHNOLOGIES PVT.LTD.PUNE Website - www.nihva.com
DWG NO - NTPL-283-PM-001-03-00-03				PROJECT NO - NTPL-283-PM	
	NAME	SIGNATURE	DATE		
DRAWN	V.W		17-06-2025	PRODUCT - RETRACTABLE ROOF	WEIGHT -38.651KG
CHK'D	S.W.		17-06-2025	SITE LOCATION - LUCKNOW	REVISION -
APPV'D	V.T.		17-06-2025	MATRIAL SPECIFICATION- GLASS	QTY - 1
if any queries contact - supportautomation@nihva.com				PROJECTION METHOD:	SCALE :
ALL DIMENSION ARE IN mm			A3		SHEET 5 OF 8

ITEM NO.	PART NUMBER	DESCRIPTION	QTY.
1	GLASS 2 1330X1025X11 MM THK	GLASS	4

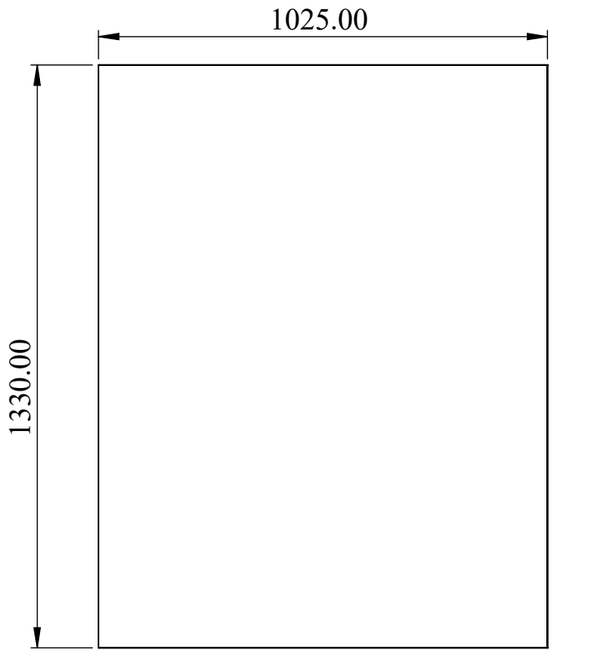


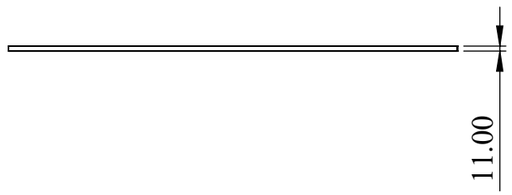


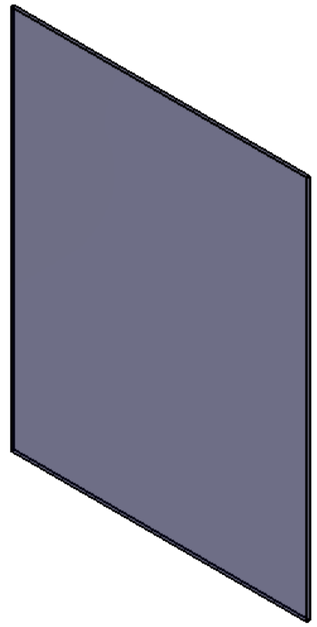


NOTE :
GLASS - 1330 X 1025 11 MM THK
QTY - 04 No'S.


TITLE - ROOF AUTOMATION				NIHVA TECHNOLOGIES PVT.LTD.PUNE Website - www.nihva.com	
DWG NO - NTPL-283-PM-001-04-00-04					
	NAME	SIGNATURE	DATE	PROJECT NO - NTPL-283-PM	
DRAWN	V.W		17-06-2025	PRODUCT - RETRACTABLE ROOF	WEIGHT - 36.657KG
CHK'D	S.W.		17-06-2025	SITE LOCATION - LUCKNOW	REVISION -
APPV'D	V.T.		17-06-2025	MATRIAL SPECIFICATION-	QTY - 1
if any queries contact - supportautomation@nihva.com				PROJECTION METHOD:	SCALE :
ALL DIMENSION ARE IN mm			A3		SHEET 6 OF 8

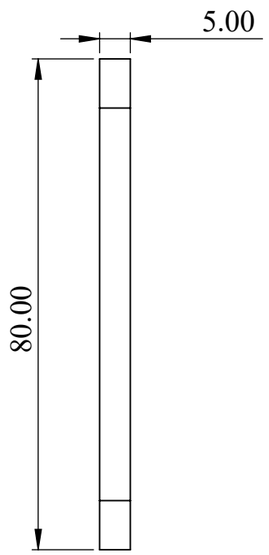

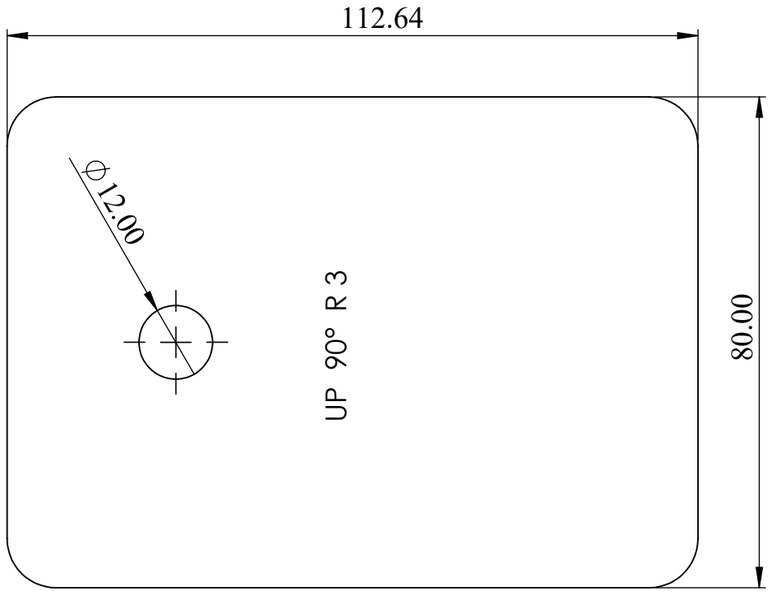

ITEM NO.	PART NUMBER	DESCRIPTION	QTY.
1	WELDING PLATE FOR ANCHOR FASTENING	MS PLATE -112.64 X 80 X 5 MM THK	1

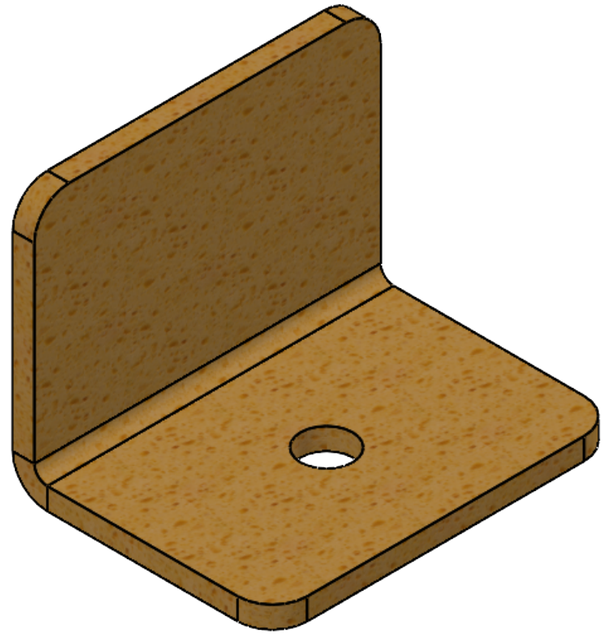


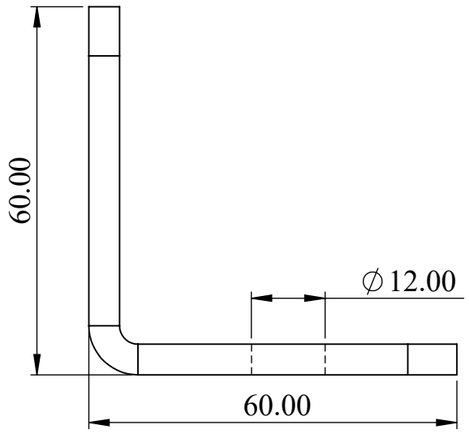


NOTE :
WELDING PLATE
MTL - MS
QTY - 09 No's
LASER CUTTING.

TITLE - ROOF AUTOMATION				NIHVA Technologies Pvt. Ltd.	NIHVA TECHNOLOGIES PVT.LTD.PUNE Website - www.nihva.com
DWG NO - NTPL-283-PM-001-05-00-05				PROJECT NO - NTPL-283-PM	
	NAME	SIGNATURE	DATE		
DRAWN	V.W		17-06-2025	PRODUCT - RETRACTABLE ROOF	WEIGHT - 0.442KG
CHK'D	S.W.		17-06-2025	SITE LOCATION - LUCKNOW	REVISION -
APPV'D	V.T.		17-06-2025	MATRIAL SPECIFICATION- MS	QTY - 1
if any queries contact - supportautomation@nihva.com				PROJECTION METHOD:	SCALE :
ALL DIMENSION ARE IN mm			A3		SHEET 7 OF 8

ITEM NO.	PART NUMBER	DESCRIPTION	QTY.
1	RR_ Anchor Bolt M10x75	STD	9

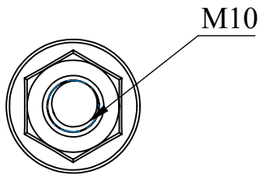

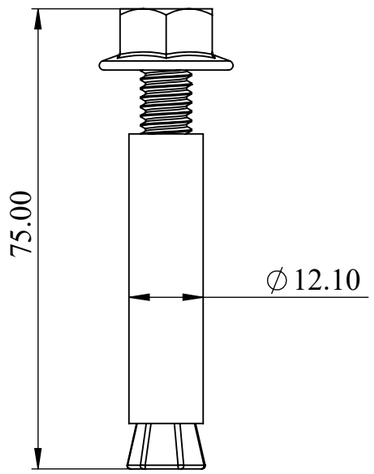



NOTE :
CHEMICAL ANCHOR BOLT M10 X 75 MM L
MTL - SS
QTY - 09 NO'S.

OR

CHEMICAL ANCHOR BOLT M10 X 200 MM L
QTY - 8 No's.

TITLE - ROOF AUTOMATION				NIHVA Technologies Pvt. Ltd.	NIHVA TECHNOLOGIES PVT.LTD.PUNE Website - www.nihva.com
DWG NO - NTPL-283-PM-001-06-00-06					
	NAME	SIGNATURE	DATE	PROJECT NO - NTPL-283-PM	
DRAWN	V.W		17-06-2025	PRODUCT - RETRACTABLE ROOF	WEIGHT -
CHK'D	S.W.		17-06-2025	SITE LOCATION - LUCKNOW	REVISION -
APPV'D	V.T.		17-06-2025	MATRIAL SPECIFICATION- MS	QTY - 1
if any queries contact - supportautomation@nihva.com				PROJECTION METHOD:	SCALE :
ALL DIMENSION ARE IN mm			A3		SHEET 8 OF 8