
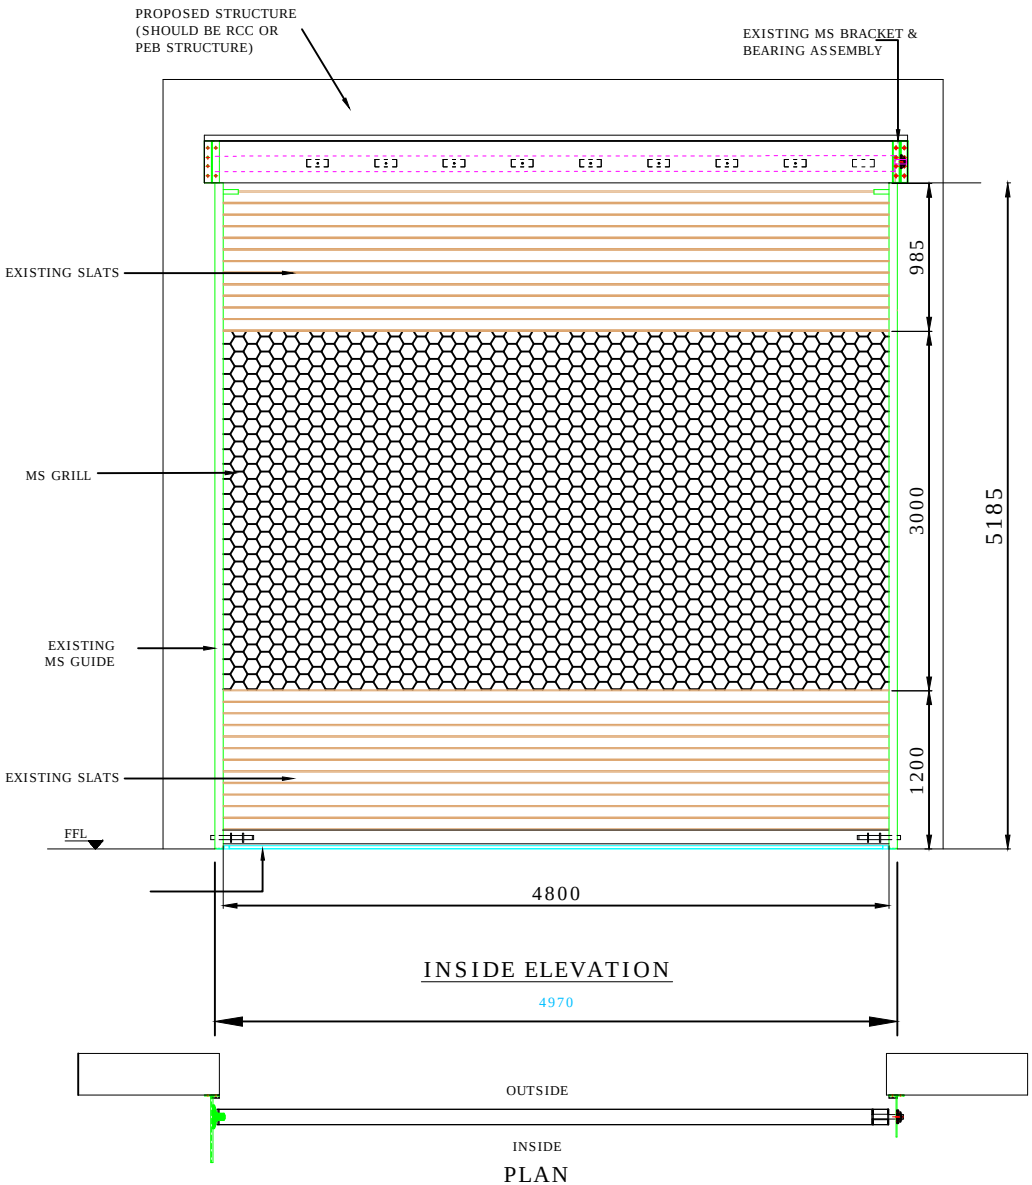


INSIDE ELEVATION


4970

PLAN

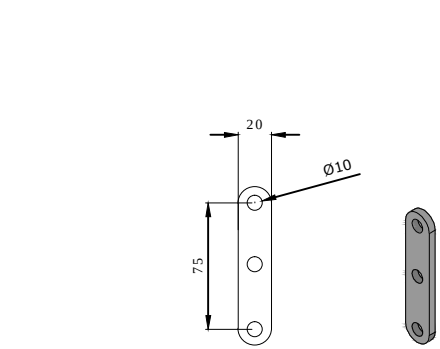

SIDE VIEW

5mm THK. LINK

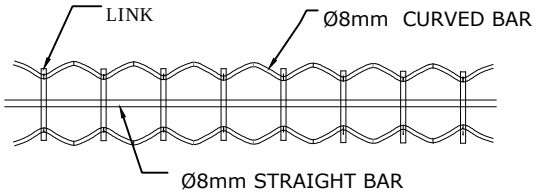

GRILL DETAILS

NOTE:-

1. ONLY M.S GRILL IS ADDED IN YOUR EXISTING ROLLING SHUTTER

REV. NO	REV DATE	DRAWN	REMARK
R01	21.06.19	P.V.A	GRILL & SLAT DIMENSION CHANGE

This drawing & designing is the property of NIHVA TECHNOLOGIES. Not to be sold or copied to any other concern.

TITLE: GRILLED ROLLING SHUTTER

	NAME	SIGN	DATE
DRAWN	P.V.A		19.06.2019
CHECK	V.M.T		19.06.2019
APPROVAL			
REV.			

If any queries contact : projects@nihva.com

ALL DIMENSION ARE IN mm

NIHVA TECHNOLOGIES PVT. LTD. PUNE
Tel : 020 66304033
Email:- info@nihva.com
Website:- www.nihva.com

CLIENT - BRIDGESTONE

PROJECT -

SITE -CHAKAN

DWG. NO. : NIHVA/19-20/0035/R01 | REV : R01

SCALE: NTS | WT: | SHEET: 01 OF 01