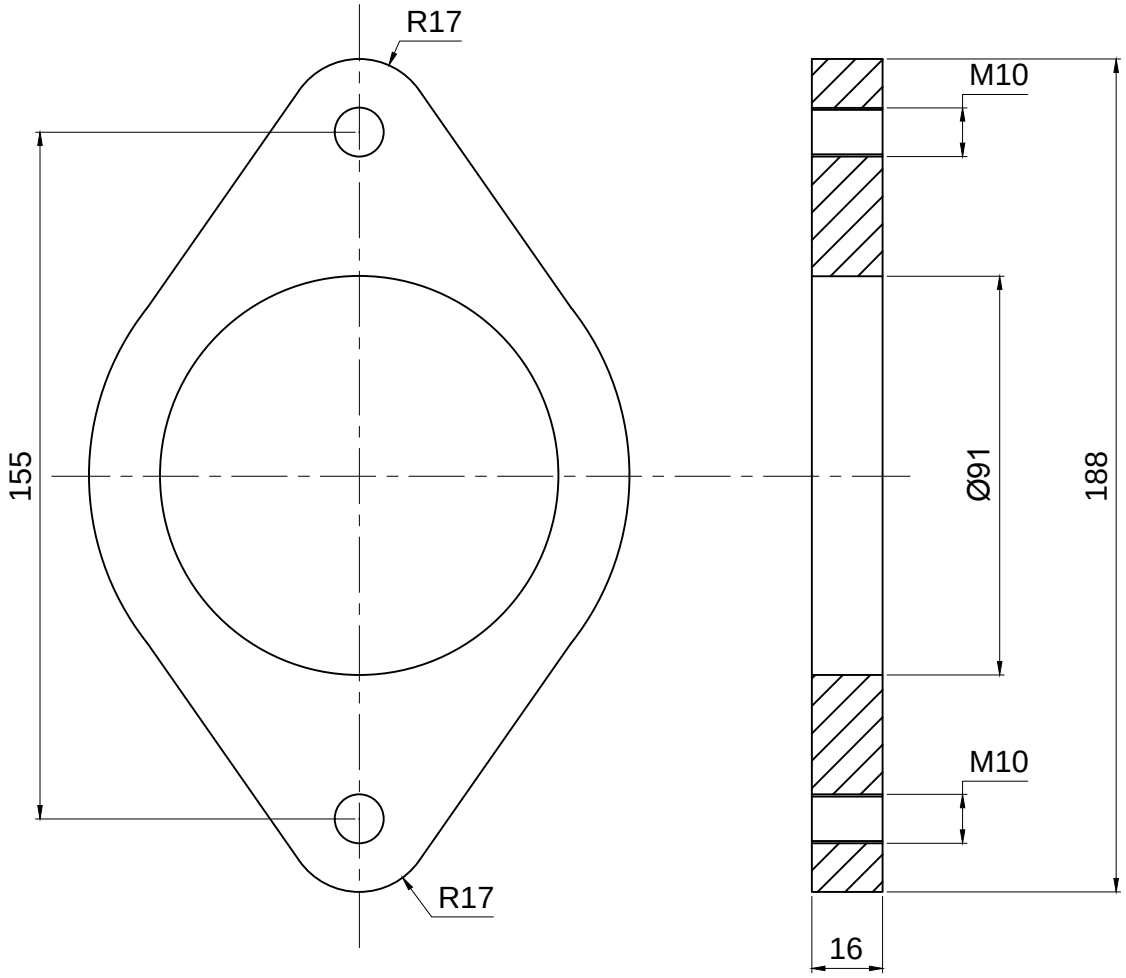


2. MS LOCK PLATE 188 X 18L = 04 NOS
M10 X 25L = 08 NOS

This drawing & design is the property of NIHVA TECHNOLOGIES. Not to be sold or copied to any other concern.

TITLE : -
LOCK PLATE 02

NIHVA TECHNOLOGIES PVT. LTD.

NIHVA TECHNOLOGIES PVT. LTD. PUNE
Tel : 020 66304033
Email:- info@nihva.com
Website:- www.nihva.com

	SIGN	DATE
DRAWN	P.A	10.01.19
CHECK	R.D	10.01.19
REV.		
APPROVAL		

CLIENT -
PROJECT -
SITE -
DWG. NO. : NIHVA/18-19/VDR/322
SCALE: NTS | WT: | SHEET: 01 OF 01

If any queries contact : projects@nihva.com
ALL DIMENSION ARE IN mm