



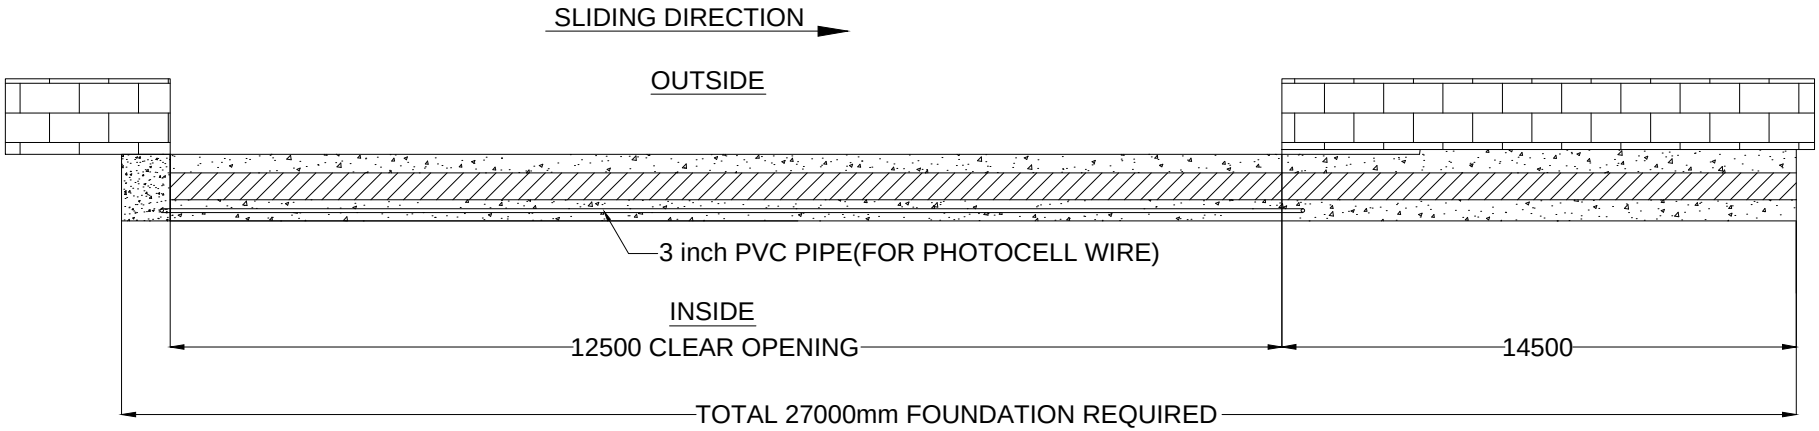

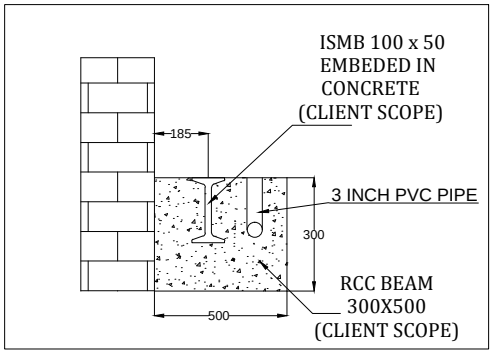

This drawing & designing is the property of NIHVA TECHNOLOGIES. Not to be sold or copied to any other concern.

TITLE: SLIDING GATE FOUNDATION DRAWING			NIHVA TECHNOLOGIES PVT. LTD. PUNE Tel : 020 66304033 Email:- info@nihva.com Website:- www.nihva.com
	Name	SIGN	DATE
DRAWN	SURAJ		13/11/18
CHECK	PRADEEP		13/11/18
APPROVAL	R.D		13/11/18
CLIENT - INOX AIR PRODUCTS			
PROJECT -			
SITE LOCATION -MODINAGR,UTTAR PRADESH			
If any queries contact : design@nihva.com	DWG. NO. : NIHVA/18-19/0176		REV.:- 0
ALL DIMENSION ARE IN mm	SCALE: NTS	WT:	SHEET: 01 OF 01