


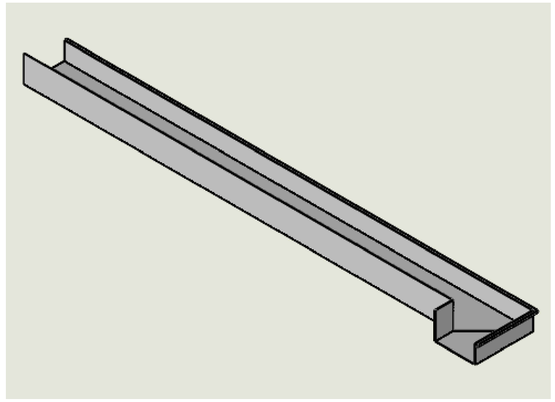


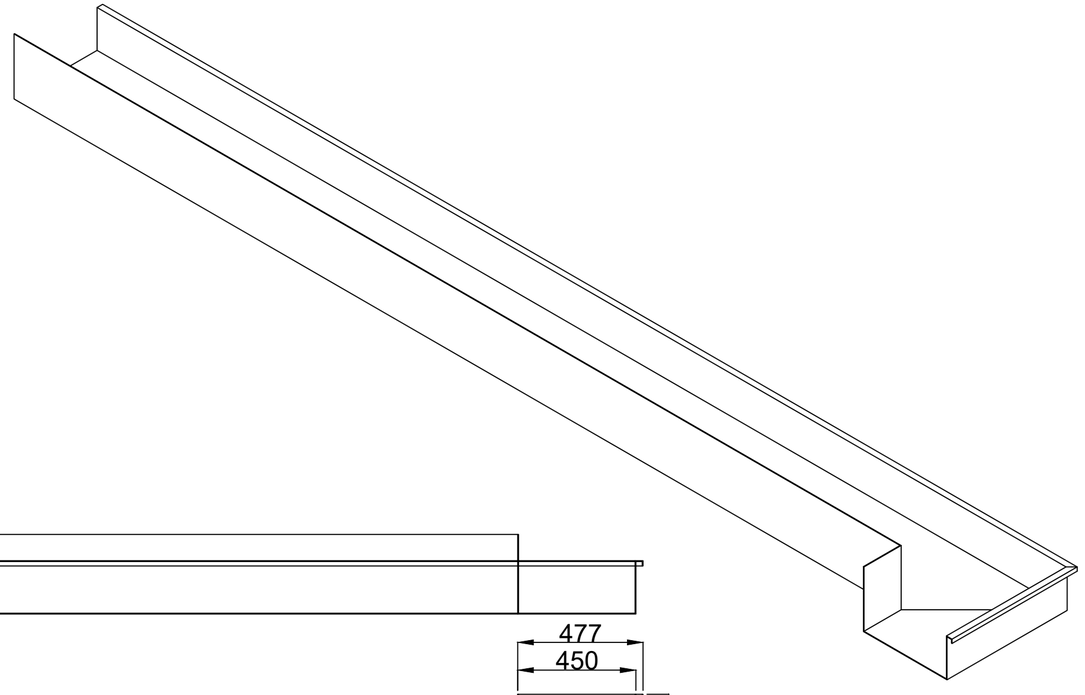

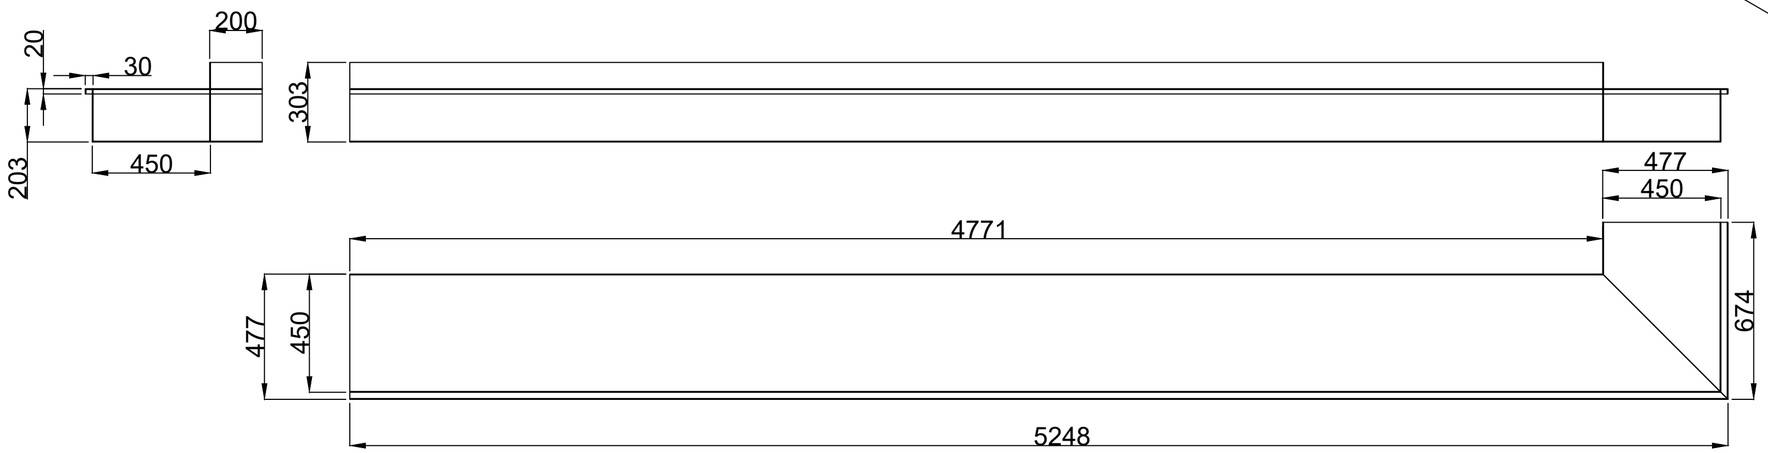

QTY. : 6 NOS.

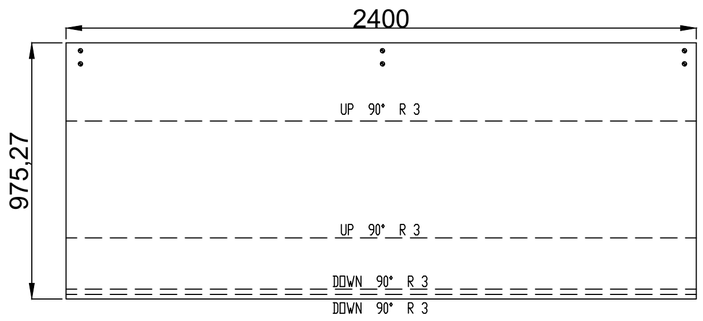

QTY. : 6 NOS.

REV NO.	DESCRIPTION	Date	Revised By

TITLE:- FRONT DRAIN TRAY				NIHVA TECHNOLOGIES PVT. LTD. PUNE Tel : 020 66304033 Email:- info@nihva.com Website:- www.nihva.com
	NAME	DATE	SIGN	
DRAWN	MAHESH S.	19/10/22		CLIENT - NIHVA TECHNOLOGIES PVT.LTD
CHECK	MAHESH S.	19/10/22		LOCATION -
APPRD.	VIJAY T.	19/10/22		PRODUCT: FIX & RETRACTABLE ROOF
If any queries contact : design@nihva.com				DWG NO:-NIHVA/22-23/MFG/0048 REV- 0
ALL DIMENSION ARE IN mm				SCALE: NTS SCALE:-- 1:1 SHEET: 01 OF 01