


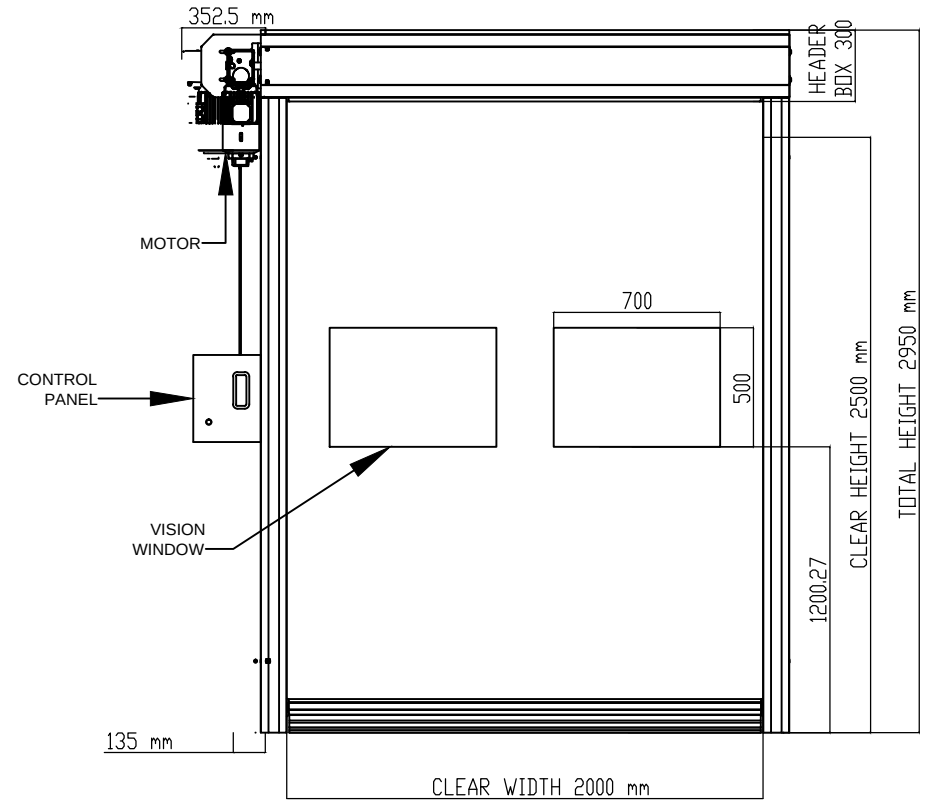


VIEW FROM OUTSIDE

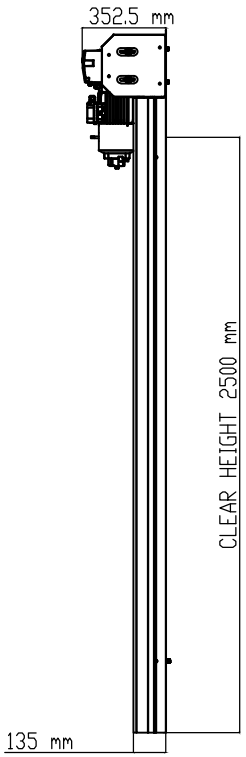

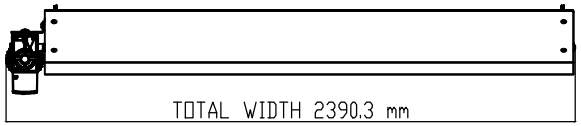

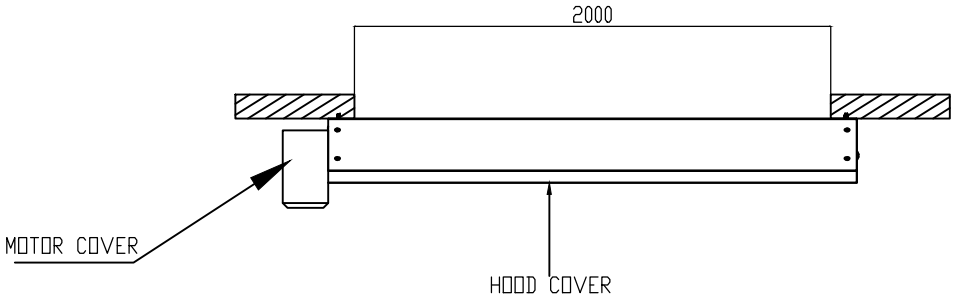

NOTE:
1. PVC CURTAIN 2 MM THICK IN BLUE (RAL 5002).
2. PUSH BUTTON WILL BE PROVIDED FROM BOTH THE SIDES.
3. DOOR WILL BE MOUNTED ON WALL.
4. ANY CIVIL WORK OR STRUCTURE REQUIRED FOR DOOR MOUNTING IS IN CLIENT SCOPE.
5. 500 MM HEIGHT REQUIRED ABOVE CLEAR OPENING FOR HEADER MOUNTING.
6. Required covers for Motor and Electrical panel is in TOLGA scope.

This drawing & design is the property of NIHVA TECHNOLOGIES. Not to be sold or copied to any other concern.

TITLE	HIGH SPEED DOOR			NIHVA TECHNOLOGIES PVT. LTD. PUNE
	NAME	SIGN	DATE	
DRAWN	G.P.		23.09.21	CLIENT :-
CHECK	A.K.		23.09.21	PROJECT :-
APPV'ED	V.T		23.09.21	LOCATION :-
If any queries contact : design@nihva.com				DWG. NO. :- NIHVA/21-22/VDR/0146 REV :- R00
ALL DIMENSION ARE IN mm				SCALE: NTS WT: SHEET: 01 OF 01

NIHVA TECHNOLOGIES PVT. LTD.
Tel : 020 66304033
Email:- info@nihva.com
Website:- www.nihva.com