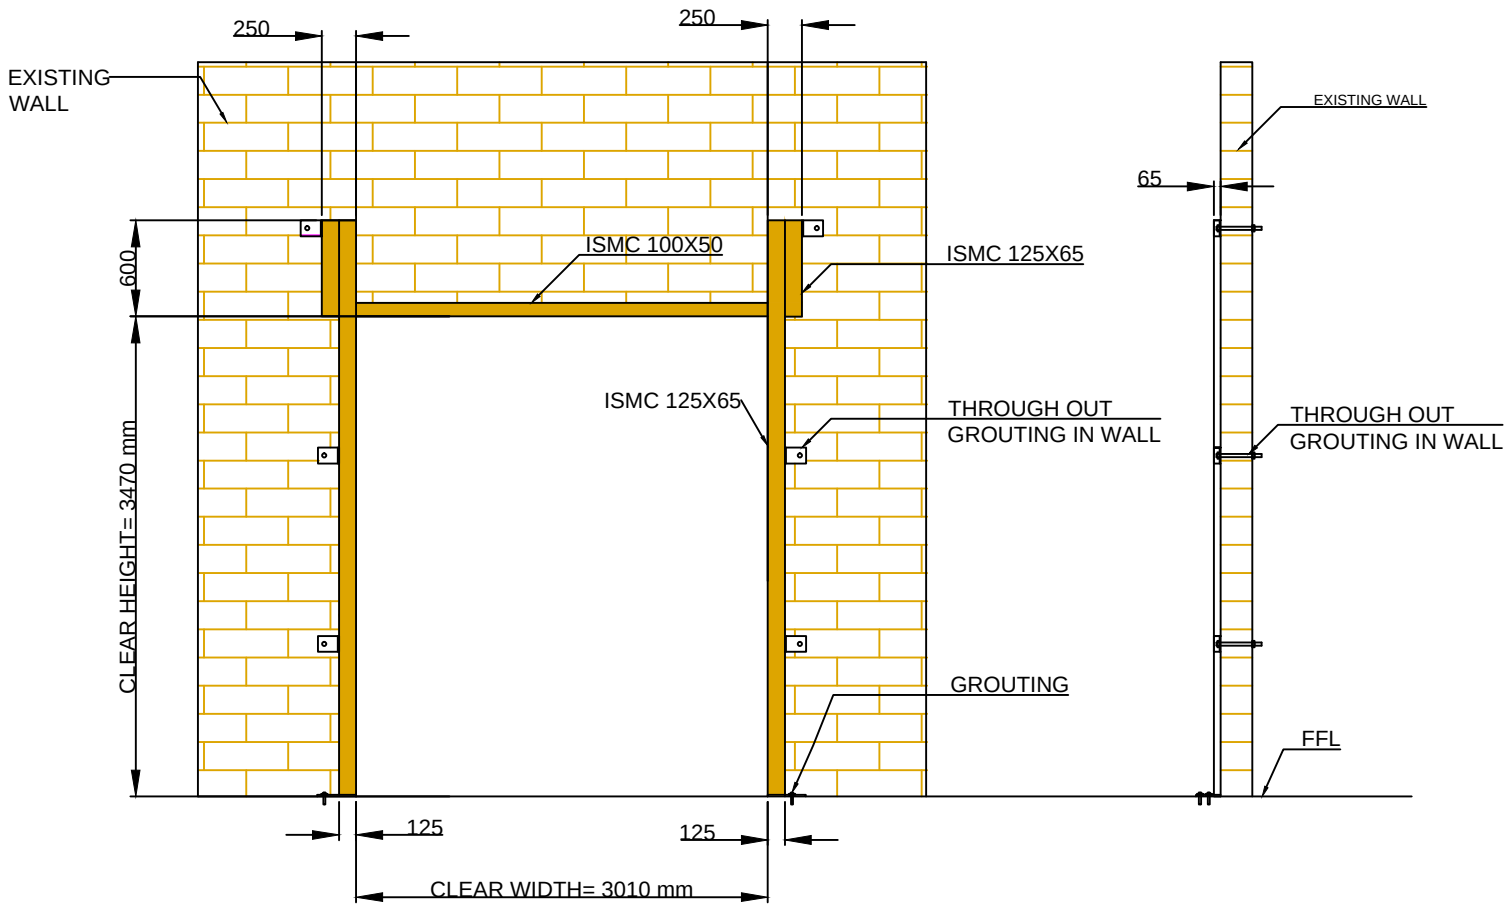

M.S. STRUCTURE DETAILS

NOTE: (1) REQUIRED M.S. TECHNICAL STRUCTURE & FITTING FOR HSD IS IN CLIENT SCOPE)
(2) ALL CIVIL WORK IN CLIENT SCOPE

3010	3470	1 NO
CLEAR WIDTH (CW)	CLEAR HEIGHT (CH)	QUANTITY

This drawing & design is the property of NIHVA TECHNOLOGIES. Not to be sold or copied to any other concern.

TITLE: HIGH SPEED DOOR STRUCTURE DRAWING

NIHVA TECHNOLOGIES PVT. LTD.
NIHVA TECHNOLOGIES PVT. LTD. PUNE
Tel : 020 66304033
Email:- info@nihva.com
Website:- www.nihva.com

	NAME	SIGN	DATE
DRAWN	S.M.S.		12.10.2020
CHECK	P.V.A.		12.10.2020
APPRD.			

CLIENT - SANDVIK ASIA PVT LTD
PROJECT - SANDVIK ASIA PVT LTD
SITE LOCATION - CHIPLUN
If any queries contact : projectsupport@nihva.com
DWG. NO. : NIHVA/20-21/0063 REV- R00
ALL DIMENSION ARE IN mm
SCALE: NTS WT: SHEET: