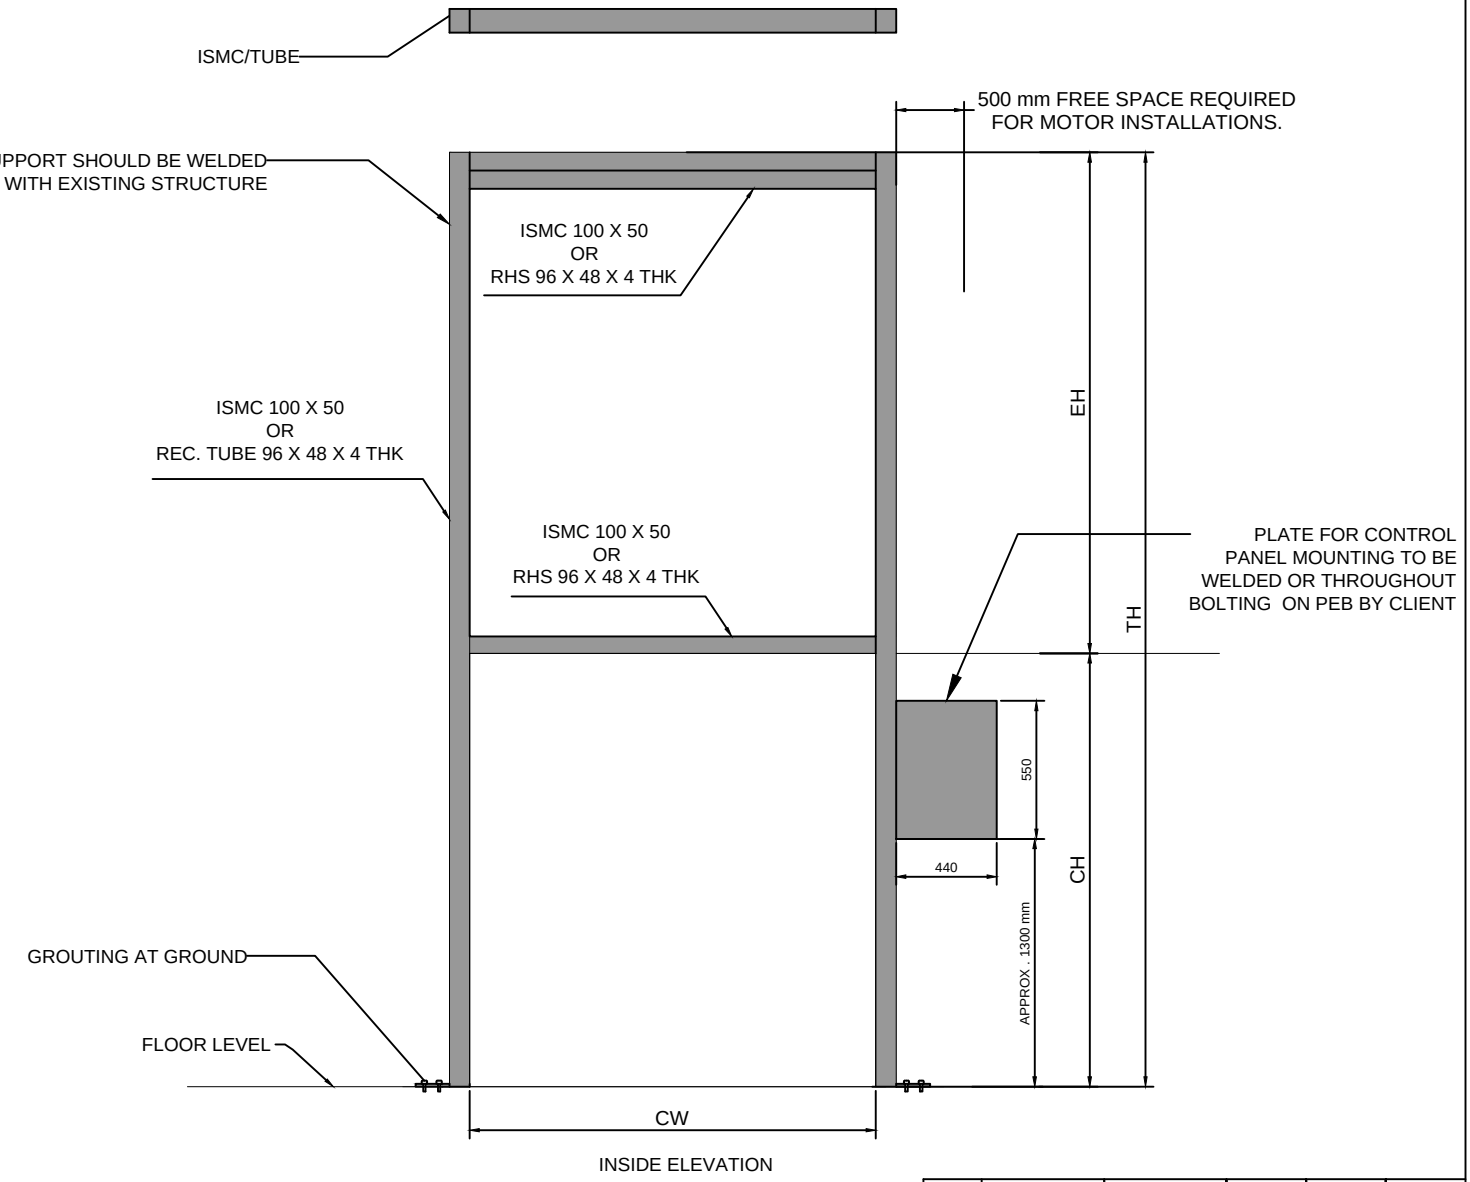

INSIDE ELEVATION

SR NO	CLEAR WIDTH CW	CLEAR HEIGHT CH	QTY	TH	EH
1	5000mm	4000mm	1	8300	4300

REV NO	DATE	DRAWN	REMARK
R01	30.11.20	S.M.S.	CONTROL PANEL MOUNTING ADDED.

NOTES-
(1) REQUIRED M.S. STRUCTURE , FITTING & ALL CIVIL WORK IN CLIENT SCOPE .
(2) PRODUCT WILL BE INSTALLED AFTER READINESS OF STRUCTURE AS PER DRAWING.

This drawing & design is the property of NIHVA TECHNOLOGIES. Not to be sold or copied to any other concern.

TITLE: STRUCTURE FOR SECTIONAL DOOR

NIHVA TECHNOLOGIES PVT. LTD. PUNE
Tel : 020 66304033
Email:- info@nihva.com
Website:- www.nihva.com

	NAME	SIGN	DATE
DRAWN	S.M.S.		20.11.2020
CHECK	ARJUN		20.11.2020
REV.			
APPROVAL			

If any queries contact : projectsupport@nihva.com

ALL DIMENSION ARE IN mm

CLIENT - SCON PROJECTS PVT LTD
PROJECT - INNOVATEC INDIA PVT. LTD.
SITE LOCATION - SANAND
DWG. NO. : NIHVA/19-20/0092/R01
SCALE: NTS | WT: | SHEET: 01 OF 01