




SIDE VIEW

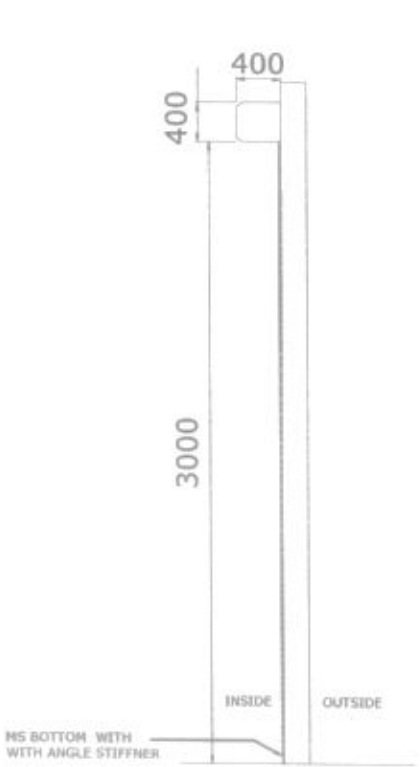


INSIDE ELEVATION

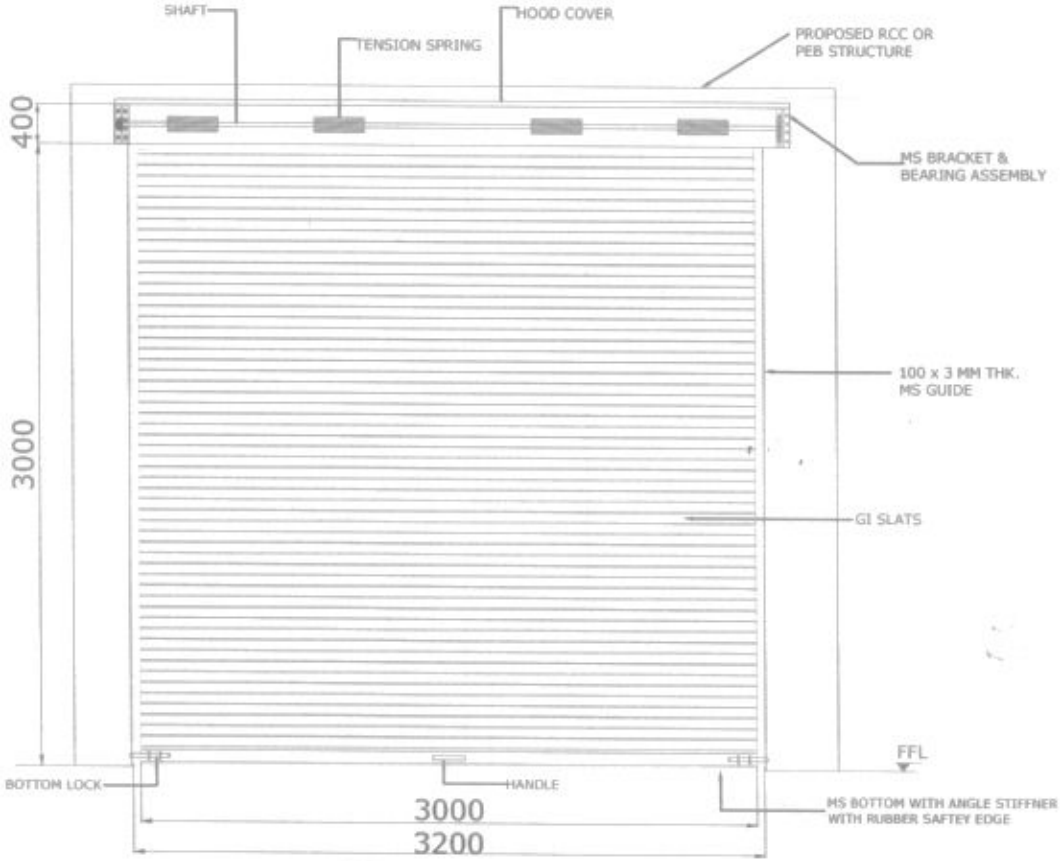

PLAN

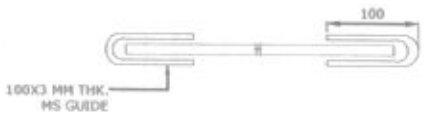

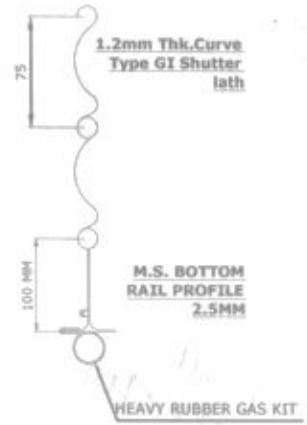

M.S. BOTTOM RAIL PROFILE 2.5MM

Shapoorji Pallonji & Co. Pvt. Ltd.
Mahindra Tower Project
SR Chauhan approved

CLEAR WIDTH (CW)	CLEAR HEIGHT (CH)	QUANTITY
3000	3000	01 NO

REV:-19-6-2018
I-SLAT THK. CHANGED 1mm TO 1.2mm

TOLERANCE:±10mm

This drawing & dadigning is the property of NIHVA TECHNOLOGIES. Not to be sold or copied to any other concern.

TITLE
MANUAL ROLLING SHUTTER

NIHVA
NIHVA TECHNOLOGIES PVT. LTD.

NIHVA TECHNOLOGIES
PVT. LTD. PUNE
Tel : 020 66304033
Email:- info@nihva.com
Website:- www.nihva.com

	SIGN	DATE
DRAWN	SURAJ	02.06.18
CHECK	PRADEEP	02.06.18
APPROVAL	PRADEEP	02.06.18
MFG.		

If any queries contact : design@nihva.com

ALL DIMENSION ARE IN mm

CLIENT - Shapoorji Pallonji and Co.Pvt Ltd
PROJECT -
SITE -
DWG. NO. : NIHVA/18-19/0051/R01 | REV-01
SCALE: NTS | WT: | SHEET: 01 OF 01