


VIEW A-A (TYP)

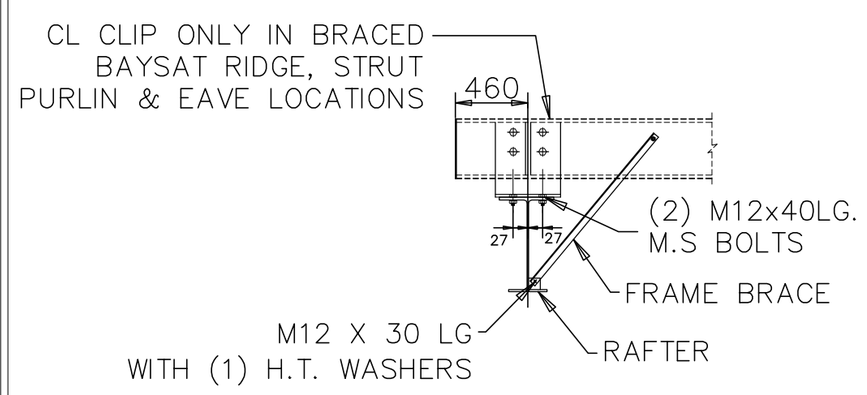


VIEW B-B (TYP)

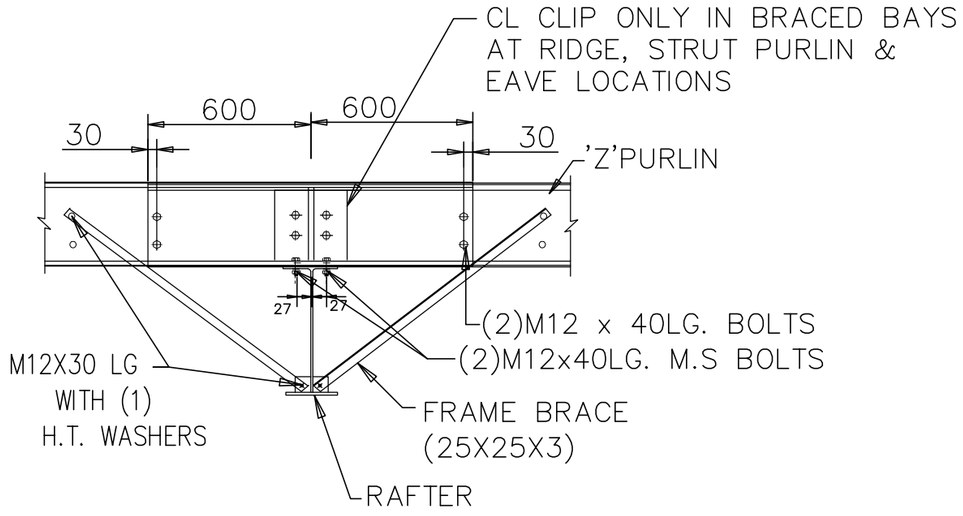


VIEW-CC (TYP)

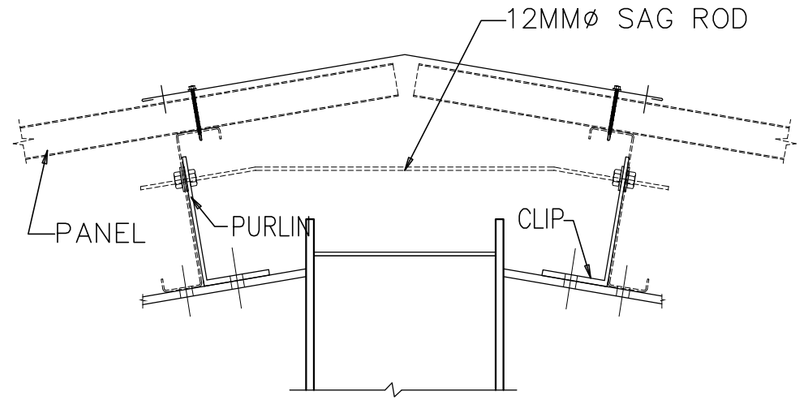


VIEW D-D (TYP)

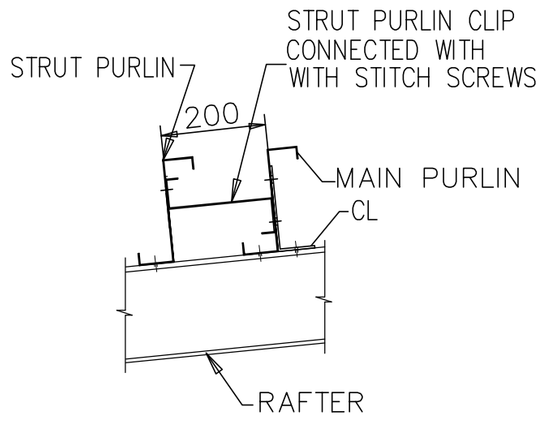


VIEW F-F (TYP)

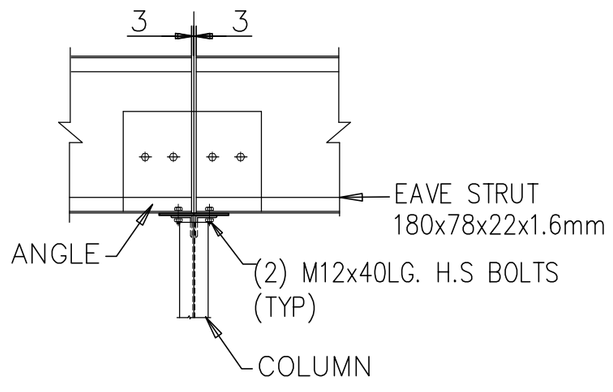

VIEW E-E (TYP)

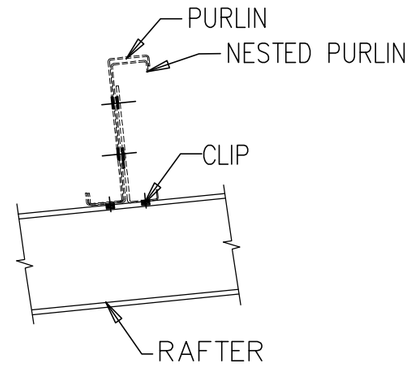

TYP.PURLIN & SAG ROD CONNECTION DETAIL

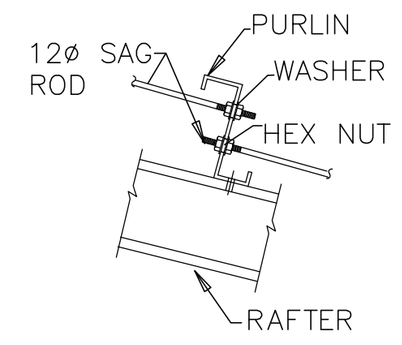

B.O.M FOR ROOF

ITEM NO.	SECTION	LENGTH	QTY REQD.	WEIGHT (Kg)
1	Z P1.200X60X20X2.3 THK	40280	18	4546.00
2	SR. 12MMø	1500	17X7	158.508
3	FB. 25X25X3	980	170	184.926
			TOTAL	4889.43 Kgs
			TOTAL	4890 Kgs

NOTES:-

1. ALL FILLET WELDS ARE EQUAL TO WEB THICKNESS U.N.O
2. FLANGE / WEB STIFFENERS ARE TO BE PROVIDED ON BOTH SIDES U.N.O..
3. BASE PLATE/CAP PLATE TO BE WELDED TO ALL-ROUND THE COLUMN.

KEY PLAN :-

LEGEND :-

REINFORCED CONCRETE

230MM THK BRICK WALL

STRUCTURAL GLAZING

N

GENERAL NOTES :

ALL DIMENSIONS ARE IN MILLIMETRES AND ARE UNFINISHED DIMENSIONS UNLESS OTHERWISE SPECIFIED.

ALL LEVELS ARE IN METRES AND ARE UNFINISHED LEVELS UNLESS OTHERWISE SPECIFIED.

DO NOT SCALE DRAWINGS. ONLY WRITTEN DIMENSIONS SHALL BE FOLLOWED. ANY DISCREPANCIES NOTED SHALL BE BROUGHT TO THE NOTICE OF THE ARCHITECT PRIOR TO EXECUTION.

SCHEDULE OF JOINERY

TYPE	DESCRIPTION	SIZE	NO.
RS	HANGER DOOR	24000 x 9000	01
W	WINDOW	1500 x 1200	20
D	DOOR	1200 x 2200	0

STRUCTURAL NOTES :

* ANCHOR BOLTS OF GRADE 4.6
* CONCRETE GRADE M30
* REBAR GRADE Fe 415

REV.	DESCRIPTION	DATE	BY	CHD.
R1	ISSUED FOR APPROVAL	20-07-17	CMF	SSF
R0	ISSUED FOR APPROVAL	20-07-17	CMF	SSF

AMENDMENT

GRAPHIC SCALE: 0 0.5M 2M 4M / 0.5M 0 1M 3M 5M

ARCHITECT

CLIENT:

HANGER AT PUNE

PROJECT LOCATION:

PUNE

DRAWING TITLE:

GENERAL ARRANGEMENT DRAWINGS

SCALE : NTS	DRAWN : SRK	R0
DATE : 02-08-2018	CHKD : SRK	
PROJECT ID: 1718-AI-052-PEB		DRAWING NO: PD: 01

Astre Infra
Private Limited
imagine and its done
691, Bemciel Indl. Estate,
Khanapur Rd,
Udyambag, Belgaum- 590008.
www.astreinfra.com

THESE DRAWINGS ARE UNDER COPYRIGHT AND ARE THE PROPERTY OF ASTRE INFRA PVT. LTD.. NONE OF THE DRAWINGS AND RELATED DOC-UMENTS CAN BE REPRODUCED, COPIED IN WHOLE OR IN PART WITHOUT PRIOR EXPRESSED WRITTEN CONSENT OF ASTRE INFRA PVT.LTD. THESE DRAWINGS AND RELATED DOCUMENTS ARE LOANED FOR THE PURPOSE OF ISSUE THE DRAWINGS SHALL BE RETURNED TO ASTRE INFRA PVT.LTD. WHICH IT HAS BEEN LOANED. AFTER FULFILLING THE PURPOSE OF ISSUE