
THIS PRINT IS THE PROPERTY OF NIHVA IT IS TO BE USED ONLY FOR THE PURPOSE FOR WHICH IT WAS LENT AND MUST NOT BE USED IN ANY WAY DERTIMENTAL TO THE INTEREST OF THIS COMPANY AND IS SUBJECT TO RETURN ON DEMAND.

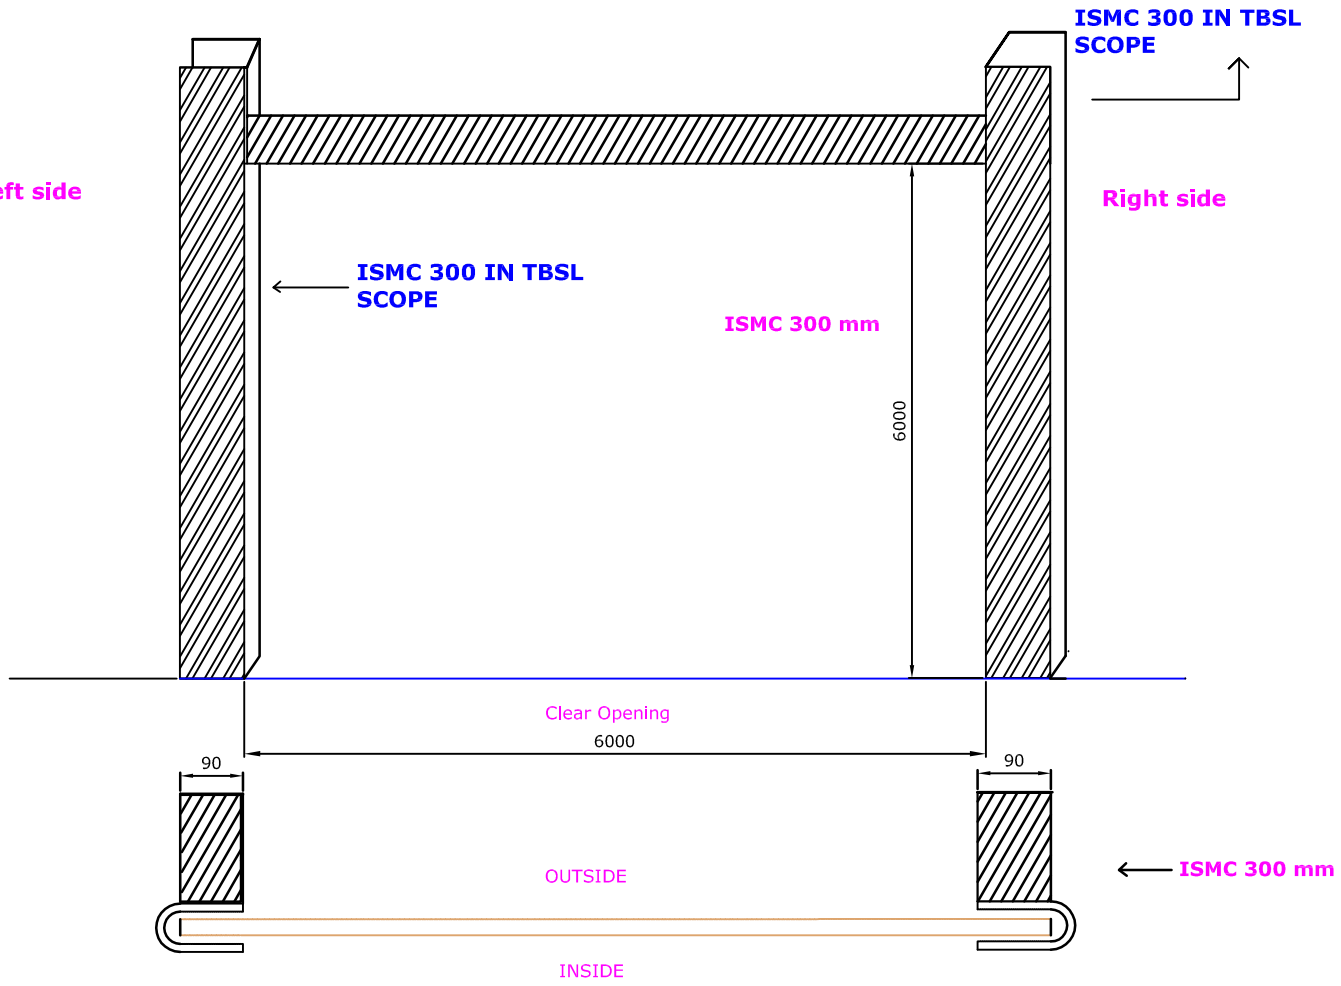

SIZE :- (W)6.0M X (H)6.0M

TITLE: MOUNTING STRUCTURE FOR MOTORISED ROLLING SHUTTER		NIHVA TECHNOLOGIES PVT. LTD. Pune-411044 Tel : 020 66304033 , Email:info@nihva.com	
CLIENTS APPROVEL:–	DRAWN A.K	CLIENT: SHAPOOR JI PALLON JI	
	CHECK V.T	PROJECT / SITE: GE / CHAKAN	
	ENG	PRODUCT NAME: MOTORISED DOUBLE WALL ROLLING SHUTTER	
	APPRD.		
ALL DIMENSION ARE IN M.M.	PROD		
If any querles CONTACT: projects@nihva.com	MFG	DWG. NO.:– NVA/SP-GE/636/3-3/R3	
	DATE :- 12/10/2013	SCALE: NTS	SHEET: 1 OF 1