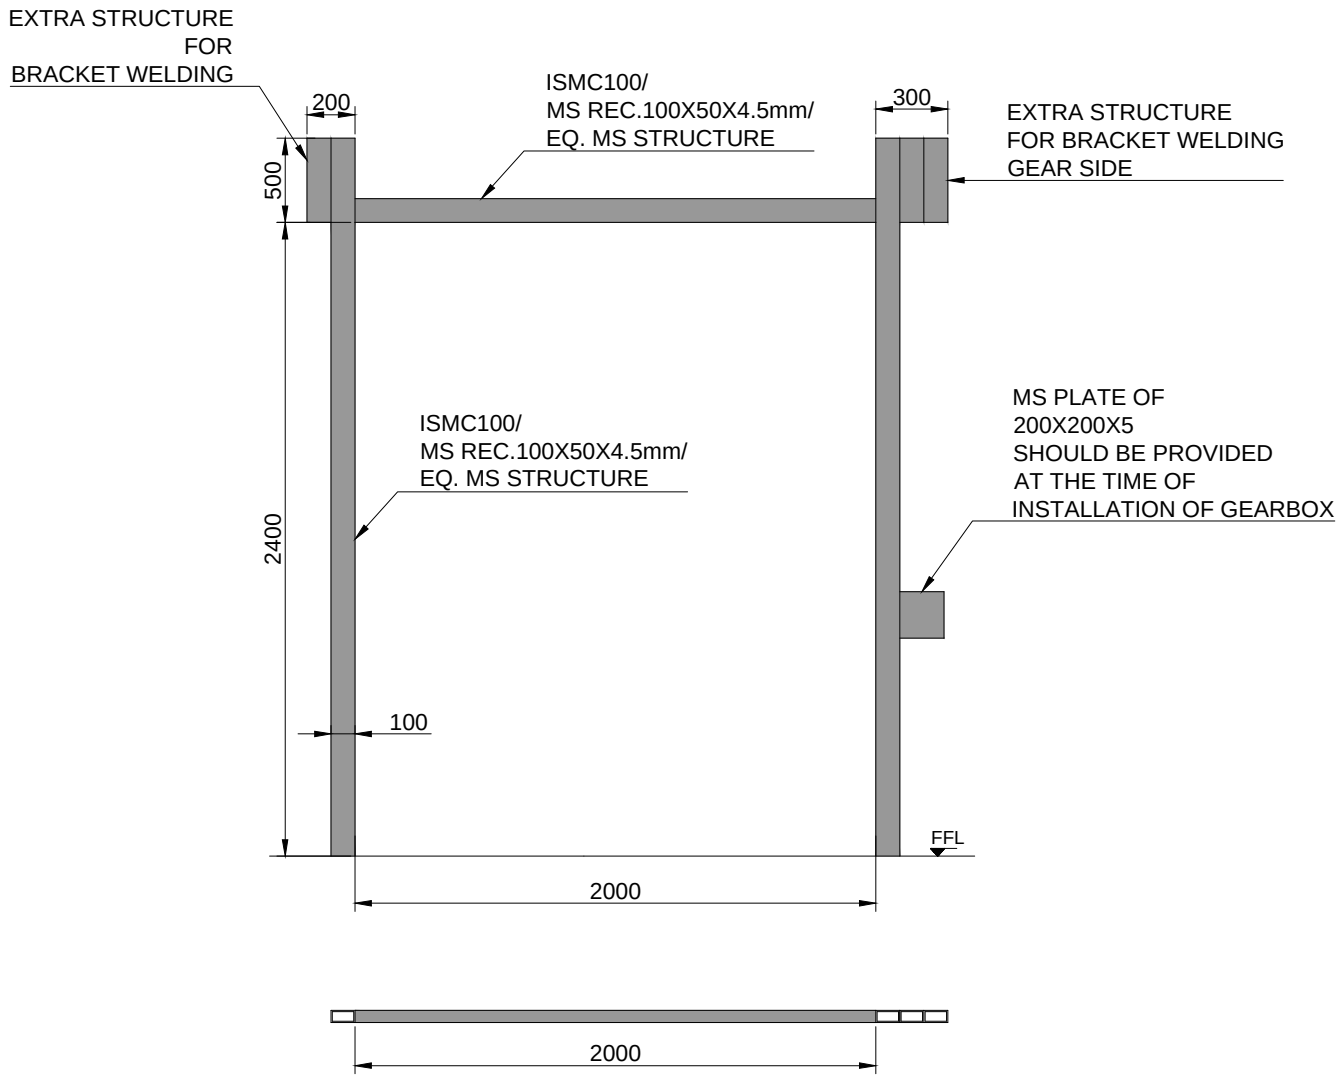


TOLERANCE - ±10mm

S.N.	LOCATION	SIZE	QUANTITY
1	B600	2000(W)X2400(H)	01

NOTE-
1. ALL CIVIL WORK WILL BE CLIENT'S SCOPE.
2.STRUCTURE REQUIRED FOR SHUTTER IS IN CLIENT'S SCOPE.

This drawing & design is the property of NIHVA TECHNOLOGIES. Not to be sold or copied to any other concern.

TITLE	STRUCTURE FOR GEAR OPERATED ROLLING SHUTTER 2mX2.4m WITH RIGHT SIDE GEARBOX			NIHVA TECHNOLOGIES PVT. LTD. PUNE Tel : 020 66304033 Email:- info@nihva.com Website:- www.nihva.com	
	NAME	SIGN	DATE		
DRAWN	SURAJ		14.12.2018	CLIENT - REWARD CONSTRUCTION	
CHECK	PRADEEP		14.12.2018	PROJECT -	
APPRD.	R.D		14.12.2018	SITE LOCATION - CHAKAN	
If any queries contact : design@nihva.com				DWG. NO. : NIHVA/18-19/0206	REV- 0
ALL DIMENSION ARE IN mm				SCALE: NTS	WT: SHEET: 01 OF 01