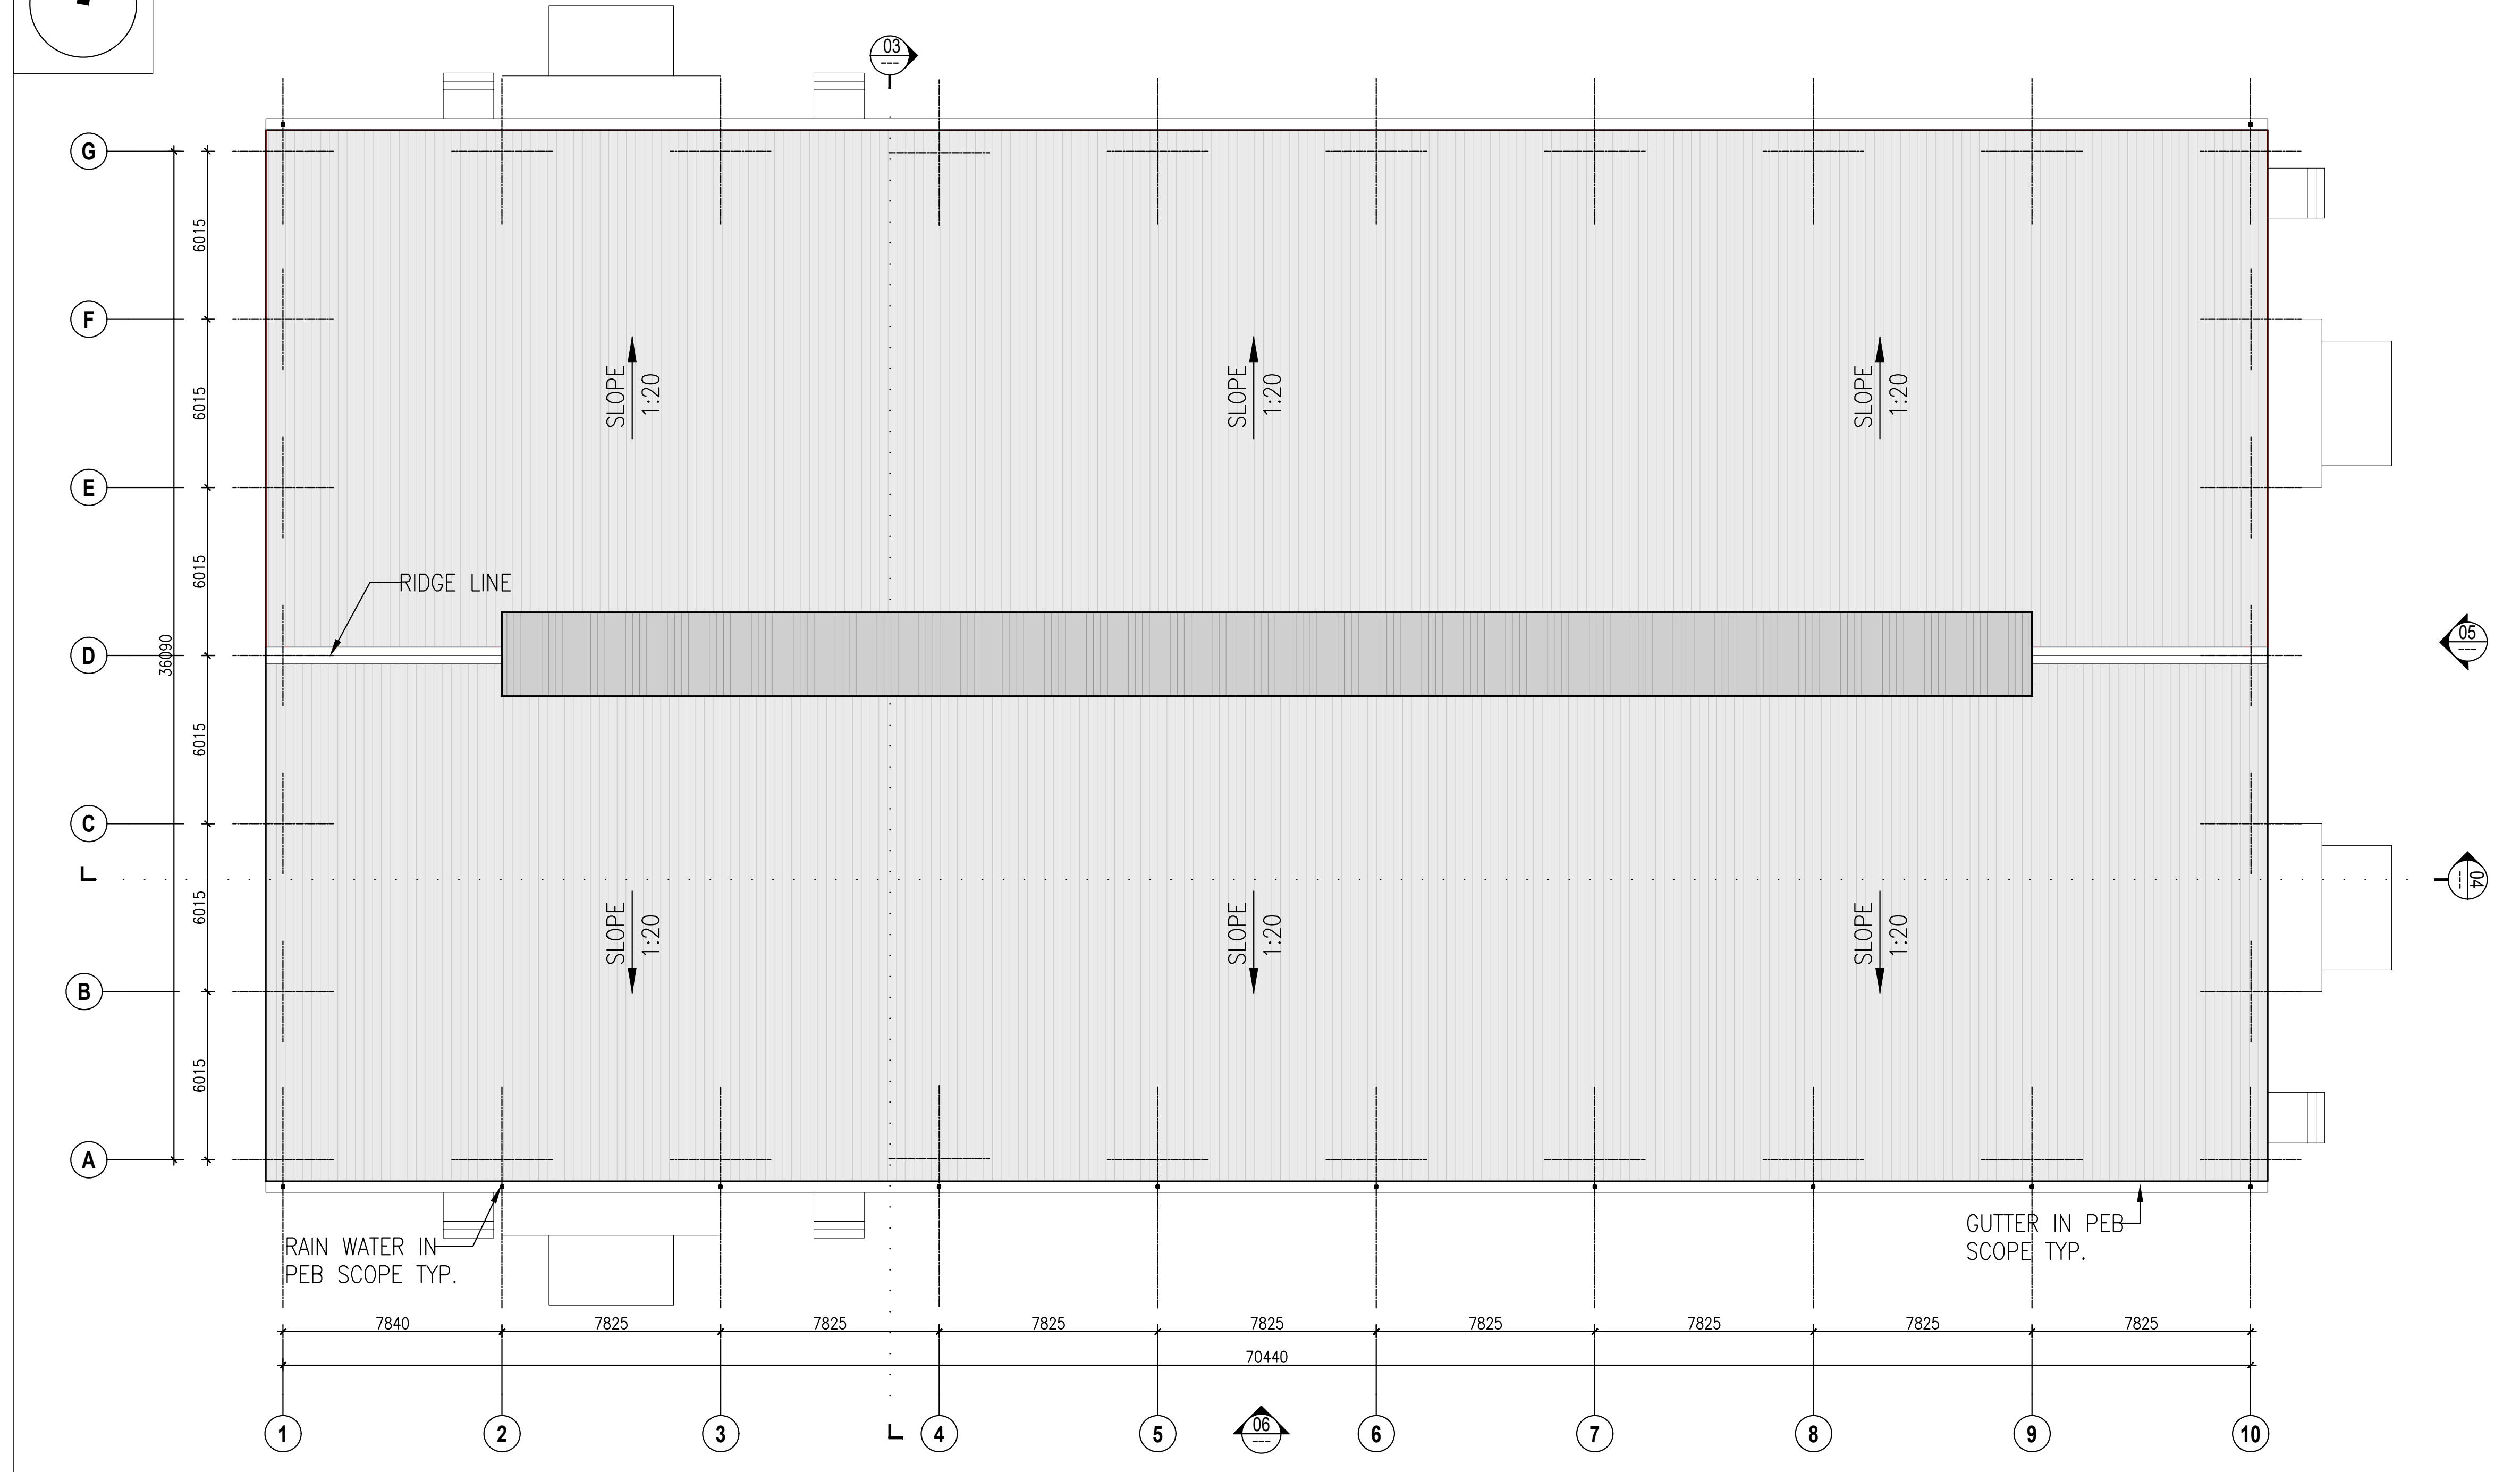
G
F
E
D
C
B
A
6015
6015
6015
6015
6015
6015
SLOPE 1:20
SLOPE 1:20
SLOPE 1:20
SLOPE 1:20
SLOPE 1:20
SLOPE 1:20
RIDGE LINE
RAIN WATER IN PEB SCOPE TYP.
GUTTER IN PEB SCOPE TYP.
7840
7825
7825
7825
7825
7825
7825
7825
7825
70440
1
2
3
4
5
6
7
8
9
10

02 ROOF PLAN
SCALE 1:200

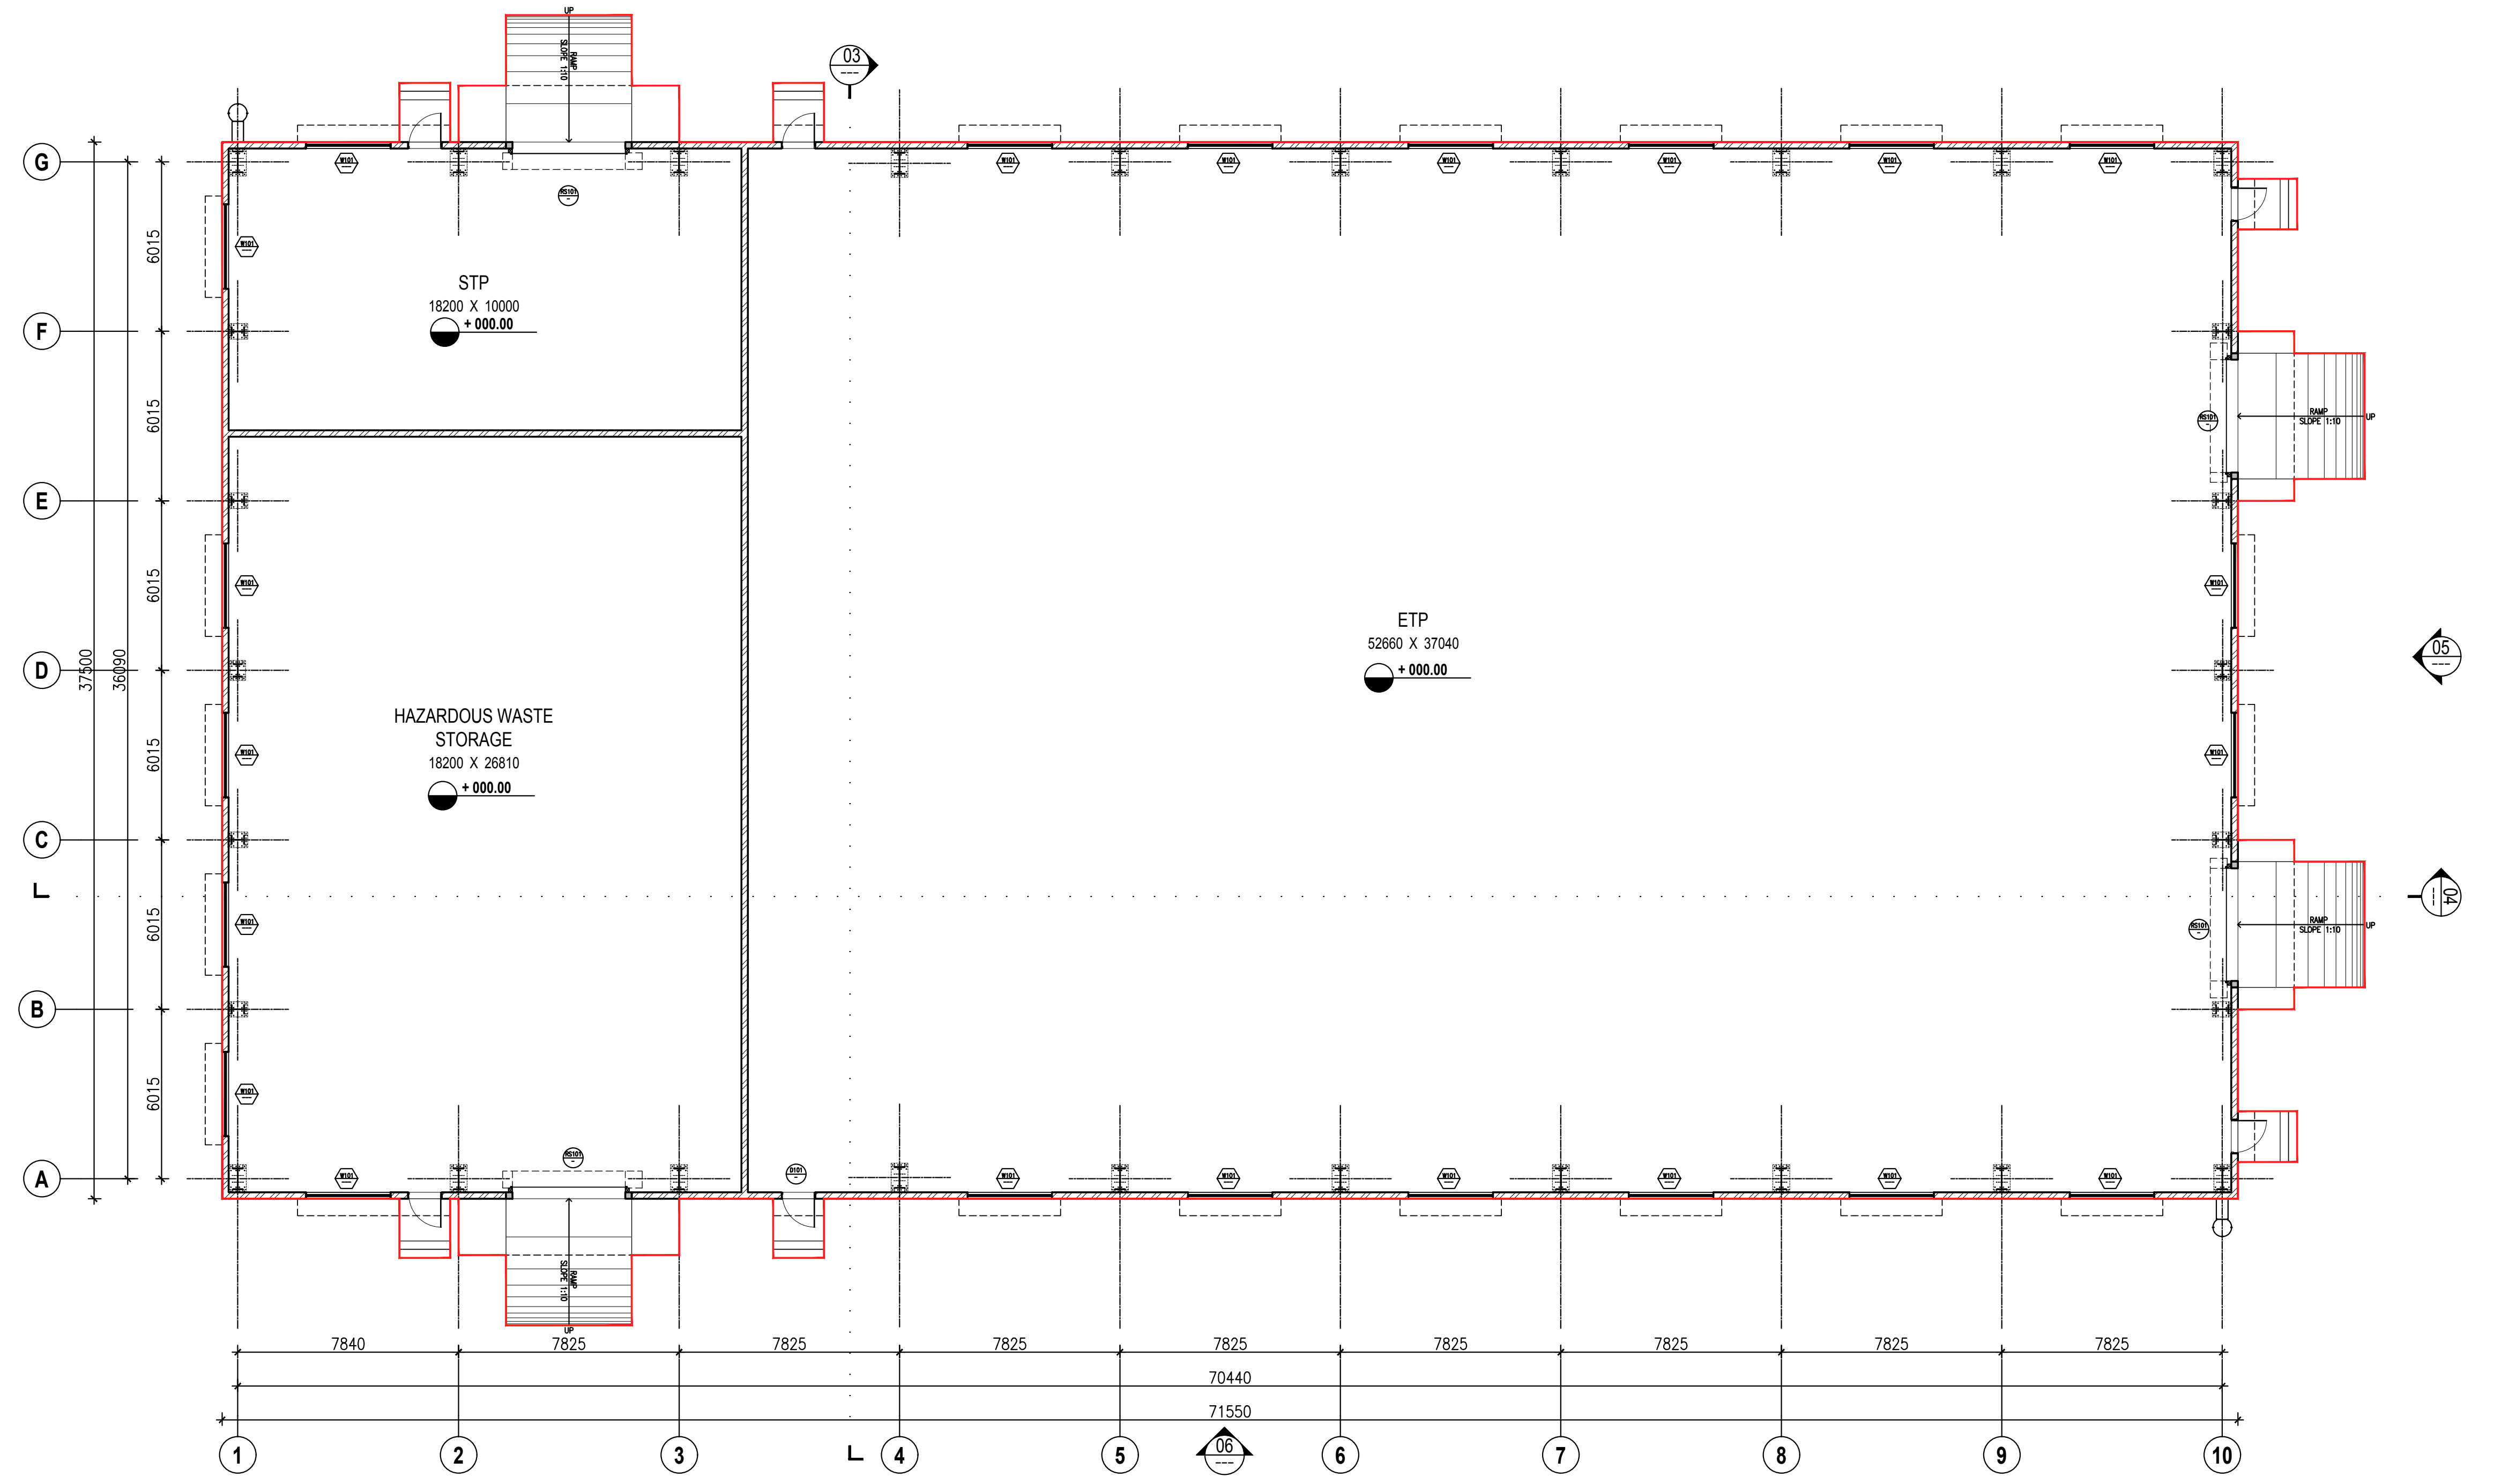
G
F
E
D
C
B
A
6015
STP
18200 X 10000
+ 000.00
HAZARDOUS WASTE STORAGE
18200 X 26810
+ 000.00
ETP
52660 X 37040
+ 000.00
W101
RS101
D101
7840
7825
70440
71550
1
2
3
4
5
6
7
8
9
10

01 GROUND FLOOR PLAN
SCALE 1:200

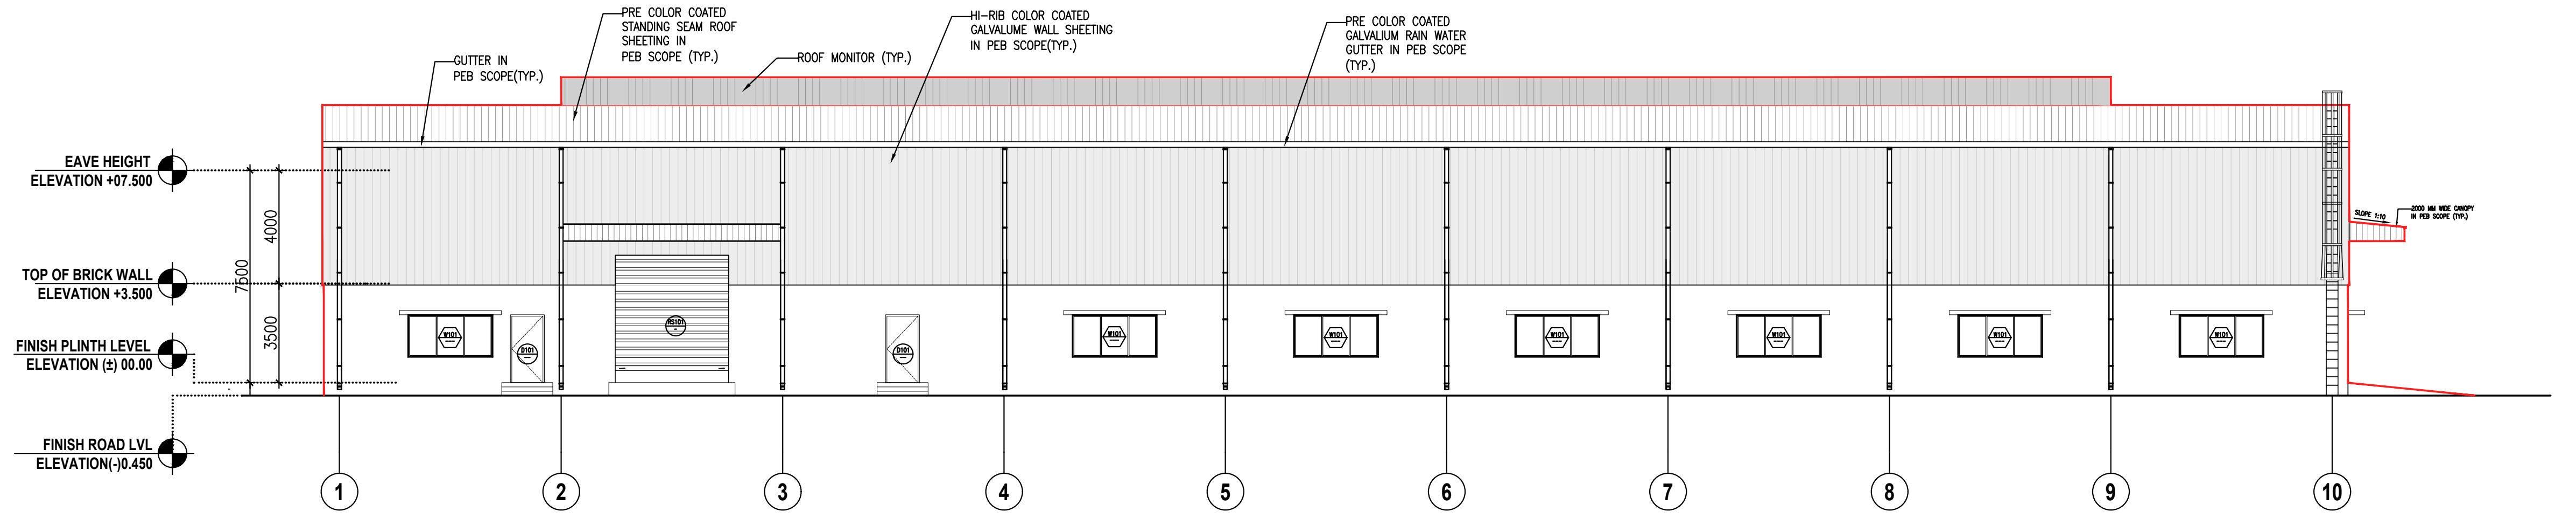
GUTTER IN PEB SCOPE(TYP.)
PRE COLOR COATED STANDING SEAM ROOF SHEETING IN PEB SCOPE (TYP.)
ROOF MONITOR (TYP.)
HI-RIB COLOR COATED GALVALUME WALL SHEETING IN PEB SCOPE(TYP.)
PRE COLOR COATED GALVALIUM RAIN WATER GUTTER IN PEB SCOPE (TYP.)
EAVE HEIGHT ELEVATION +07.500
TOP OF BRICK WALL ELEVATION +3.500
FINISH PLINTH LEVEL ELEVATION (±) 00.00
FINISH ROAD LVL ELEVATION(-)0.450
7500
4000
3500
W101
D101
RS101
1
2
3
4
5
6
7
8
9
10

06 ELEVATION
SCALE 1CM : 1.50M

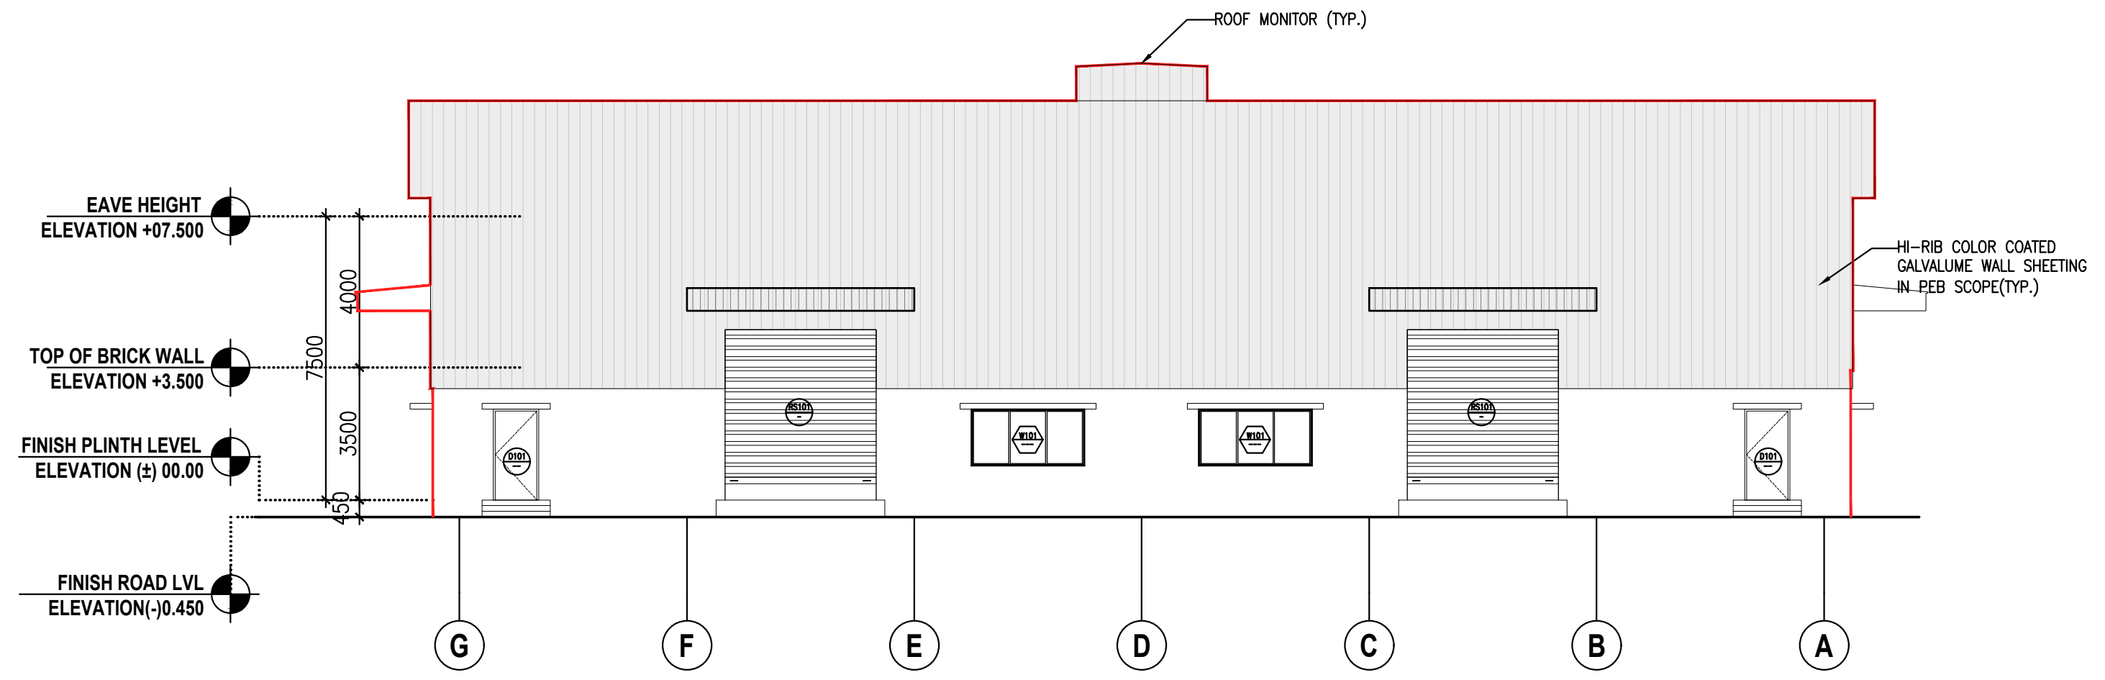
ROOF MONITOR (TYP.)
HI-RIB COLOR COATED GALVALUME WALL SHEETING IN PEB SCOPE(TYP.)
EAVE HEIGHT ELEVATION +07.500
TOP OF BRICK WALL ELEVATION +3.500
FINISH PLINTH LEVEL ELEVATION (±) 00.00
FINISH ROAD LVL ELEVATION(-)0.450
7500
4000
3500
450
D101
RS101
W101
G
F
E
D
C
B
A

05 ELEVATION
SCALE 1CM : 1.50M

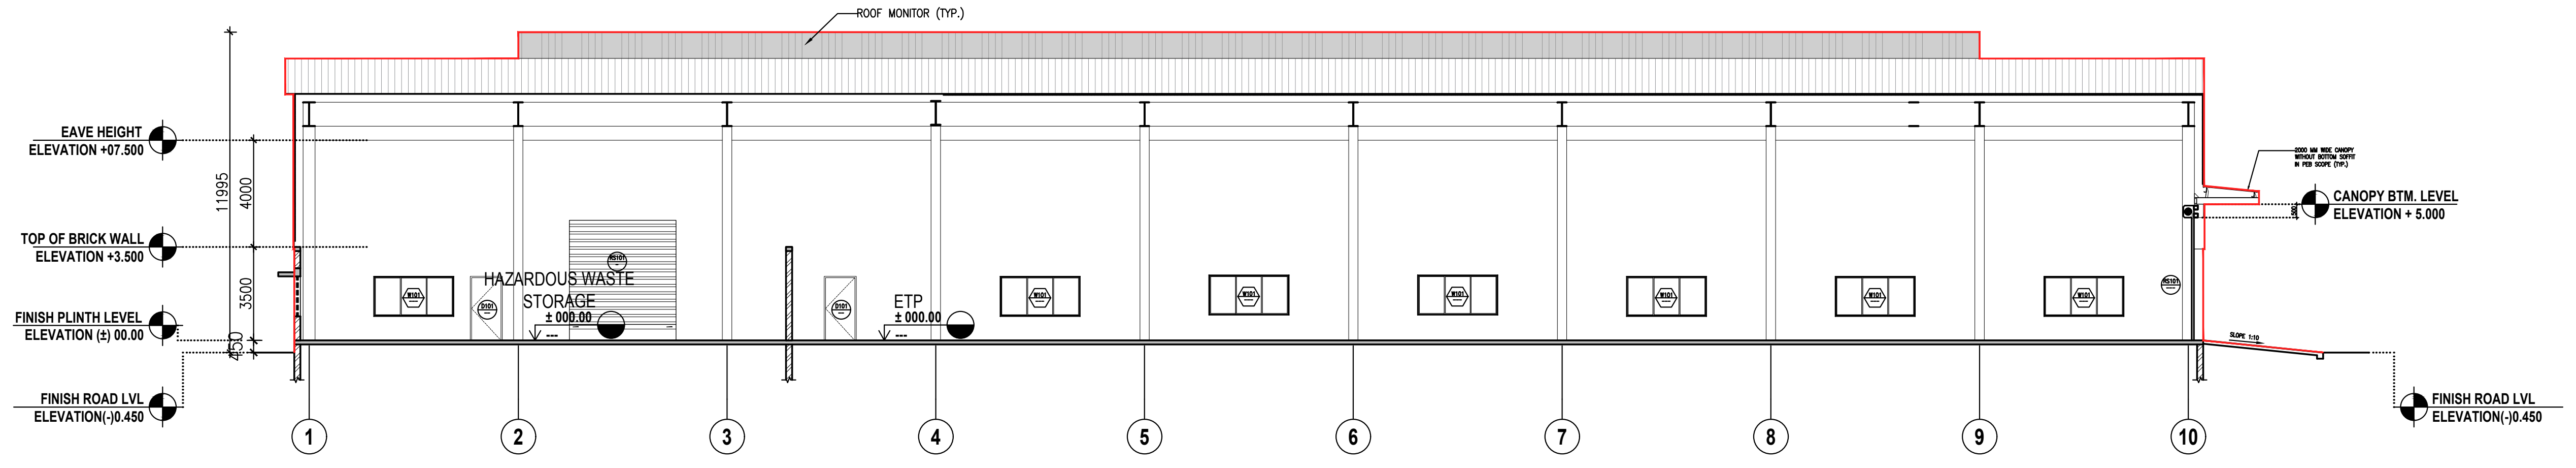
ROOF MONITOR (TYP.)
EAVE HEIGHT ELEVATION +07.500
TOP OF BRICK WALL ELEVATION +3.500
FINISH PLINTH LEVEL ELEVATION (±) 00.00
FINISH ROAD LVL ELEVATION(-)0.450
11995
4000
3500
450
HAZARDOUS WASTE STORAGE
± 000.00
ETP
± 000.00
CANOPY BTM. LEVEL ELEVATION + 5.000
SLOPE 1:10
FINISH ROAD LVL ELEVATION(-)0.450
1
2
3
4
5
6
7
8
9
10

04 SECTION
SCALE 1:200

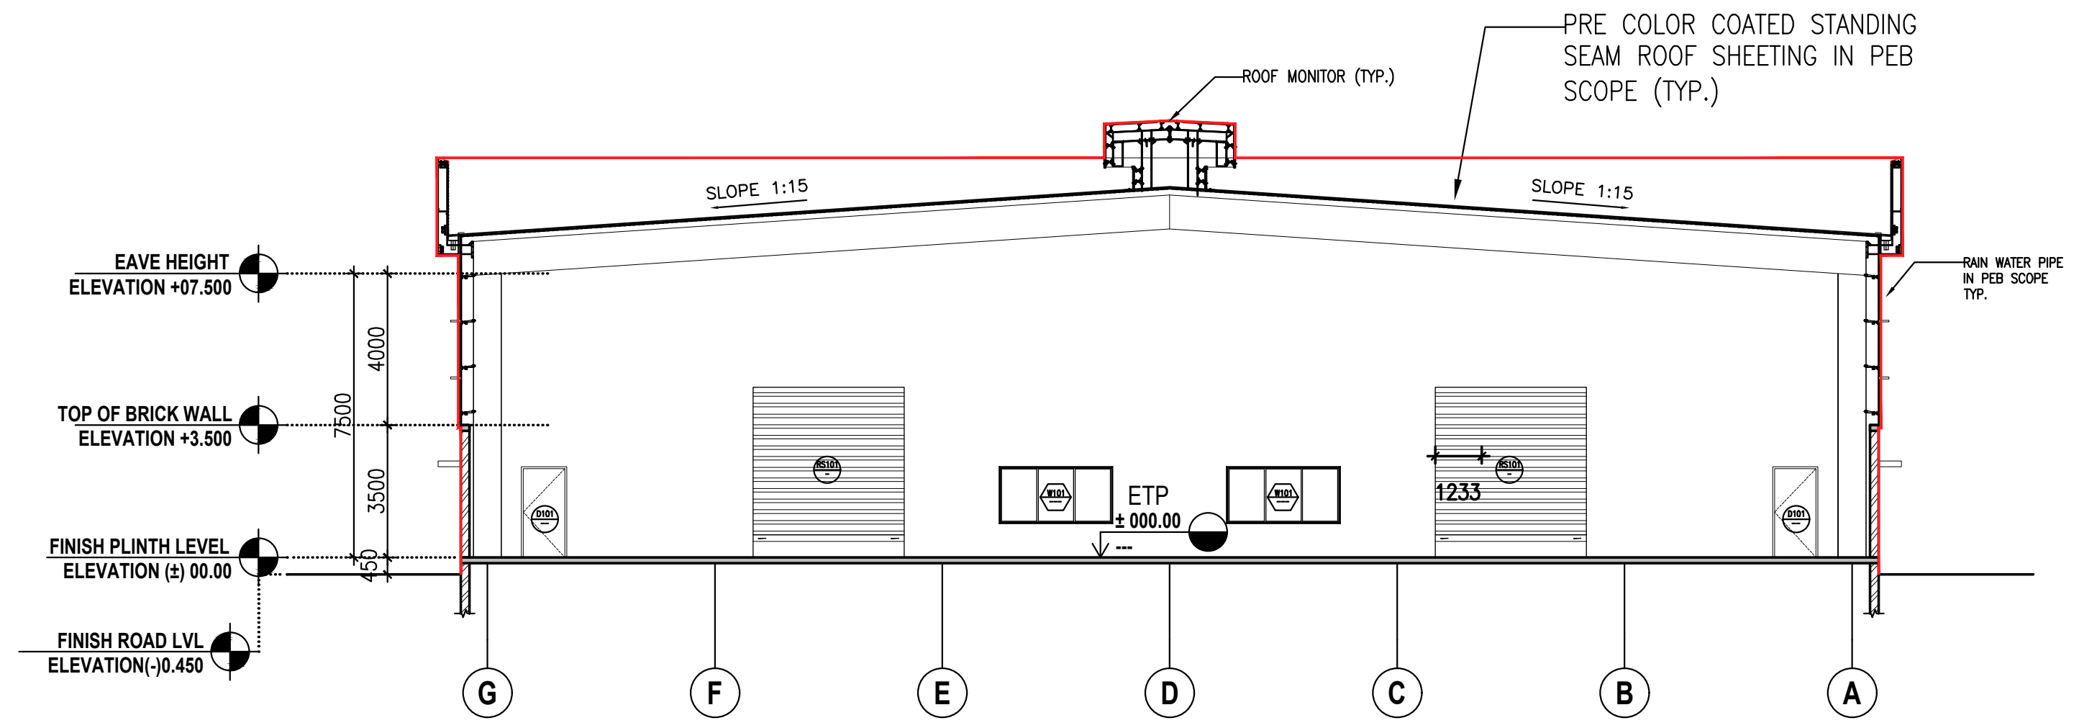
ROOF MONITOR (TYP.)
PRE COLOR COATED STANDING SEAM ROOF SHEETING IN PEB SCOPE (TYP.)
SLOPE 1:15
SLOPE 1:15
RAIN WATER PIPE IN PEB SCOPE TYP.
EAVE HEIGHT ELEVATION +07.500
TOP OF BRICK WALL ELEVATION +3.500
FINISH PLINTH LEVEL ELEVATION (±) 00.00
FINISH ROAD LVL ELEVATION(-)0.450
7500
4000
3500
450
ETP
± 000.00
1233
G
F
E
D
C
B
A

03 SECTION
SCALE 1:200

AREA CALCULATION		
NO.	FLOOR NAME	AREA (SQ. MT.)
1.	GROUND FLOOR	2805

THIS DRAWING & DESIGN IS THE SOLE PROPERTY OF VMS & SHALL NOT BE COPIED,
TRACED OR REPRODUCED BY ANY MEANS WITHOUT PRIOR WRITTEN CONSENT OF THE FIRM.

GENERAL NOTES :

1. ALL THE DIMENSIONS ARE UNFINISHED DIMENSIONS.
2. ALL DIMENSIONS ARE IN MM AND LEVELS ARE IN MT, UNLESS OTHERWISE MENTIONED.
3. ALL THE DIMENSIONS SHALL BE READ & NOT TO BE MEASURED.
4. IN CASE OF ANY DISCREPANCY, BRING IT TO THE NOTICE OF THE ARCHITECT IMMEDIATELY.
5. DETAIL DRAWING PRECEDES THE GENERAL DRAWING

SCHEDULE OF OPENINGS:

MKD.	SIZE	SILL HT.	LINTEL HT.	TOTAL NO.	REMARKS
D101	1200x2400	----	2400	6	FIRE DOOR
RS101	4000x4500	----	4500	4	ROLLING SHUTTER
W101	3000x1500	900	2400	21	ALU. FRAME WITH FIXED GLASS & LOUVERS WINDOW

FOR TENDER

NO.	DATE	DESCRIPTION	DRAWN BY	CHECKED BY
R0	-	-	-	-

REVISION HISTORY

KEY PLAN
SCALE : N.T.S.

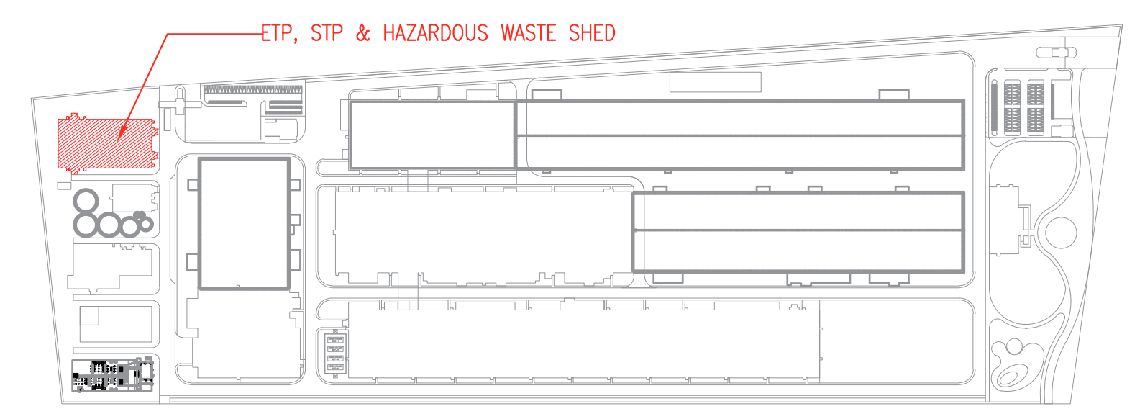
ETP, STP & HAZARDOUS WASTE SHED

REFERENCE DRAWINGS :
01. ARCHITECTURAL : -
02. STRUCTURAL : -
03. HVAC : -
04. ELECTRICAL : -
05. UTILITIES : -

GROUND FLOOR PLAN, SECTIONS & ELEVATIONS

ETP, STP & HAZARDOUS WASTE SHED

AGRAWAL METAL WORKS(P) LTD.

PROJECT NO. 3824	SCALE : AS SHOWN	DRAWN :	BHAKTI B.
		CHECKED:	BHAKTI B.
	DATE : 03-12-24	APPROVED:	DARSH D.
		COORDINATION CHECKED:	DARSH D.

ENGINEERING + ARCHITECTURE
VMS ENGINEERING & DESIGN SERVICES (P) LTD.
CHITRAKOOT FLATS, B/H TIMES OF INDIA, OFF ASHRAM ROAD,
AHMEDABAD-380 009. PHONE: +91 (079) 2658-8829, 4023-6236
WWW.VMSCONSULTANTS.COM

SHEET SIZE	DRAWING NO.	TENDER	REVISION:
600x 1200	T.A.9.101	T	R0