


DWG.NO: SALT_1714_STR_01_R0

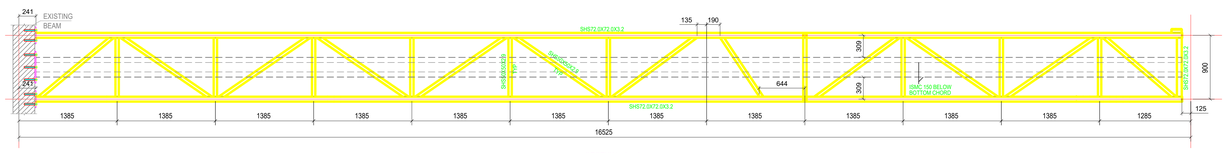


SECTION A - A
1:30

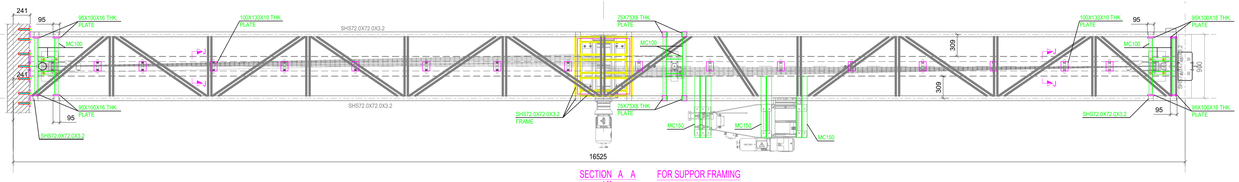


SECTION A A FOR SUPPOR FRAMING
1:30

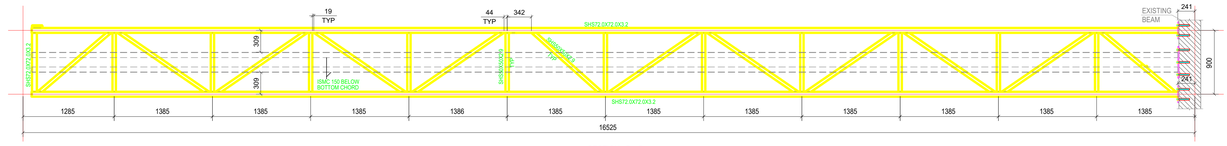


SECTION B - B
1:30

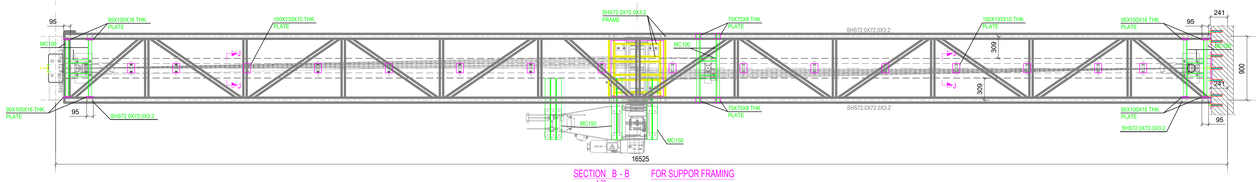


SECTION B - B FOR SUPPOR FRAMING
1:30

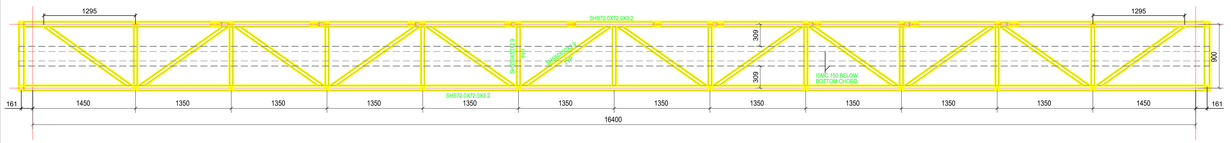


SECTION E - E
1:30

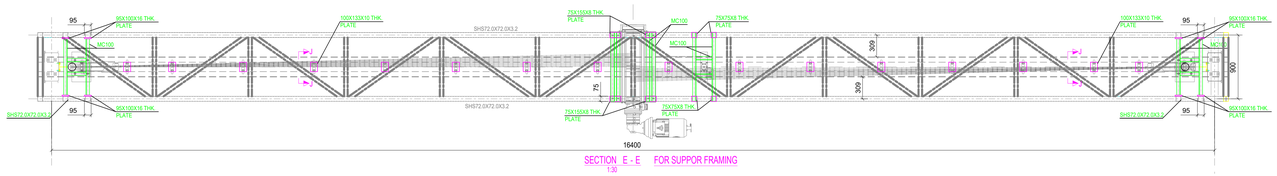


SECTION E - E FOR SUPPOR FRAMING
1:30

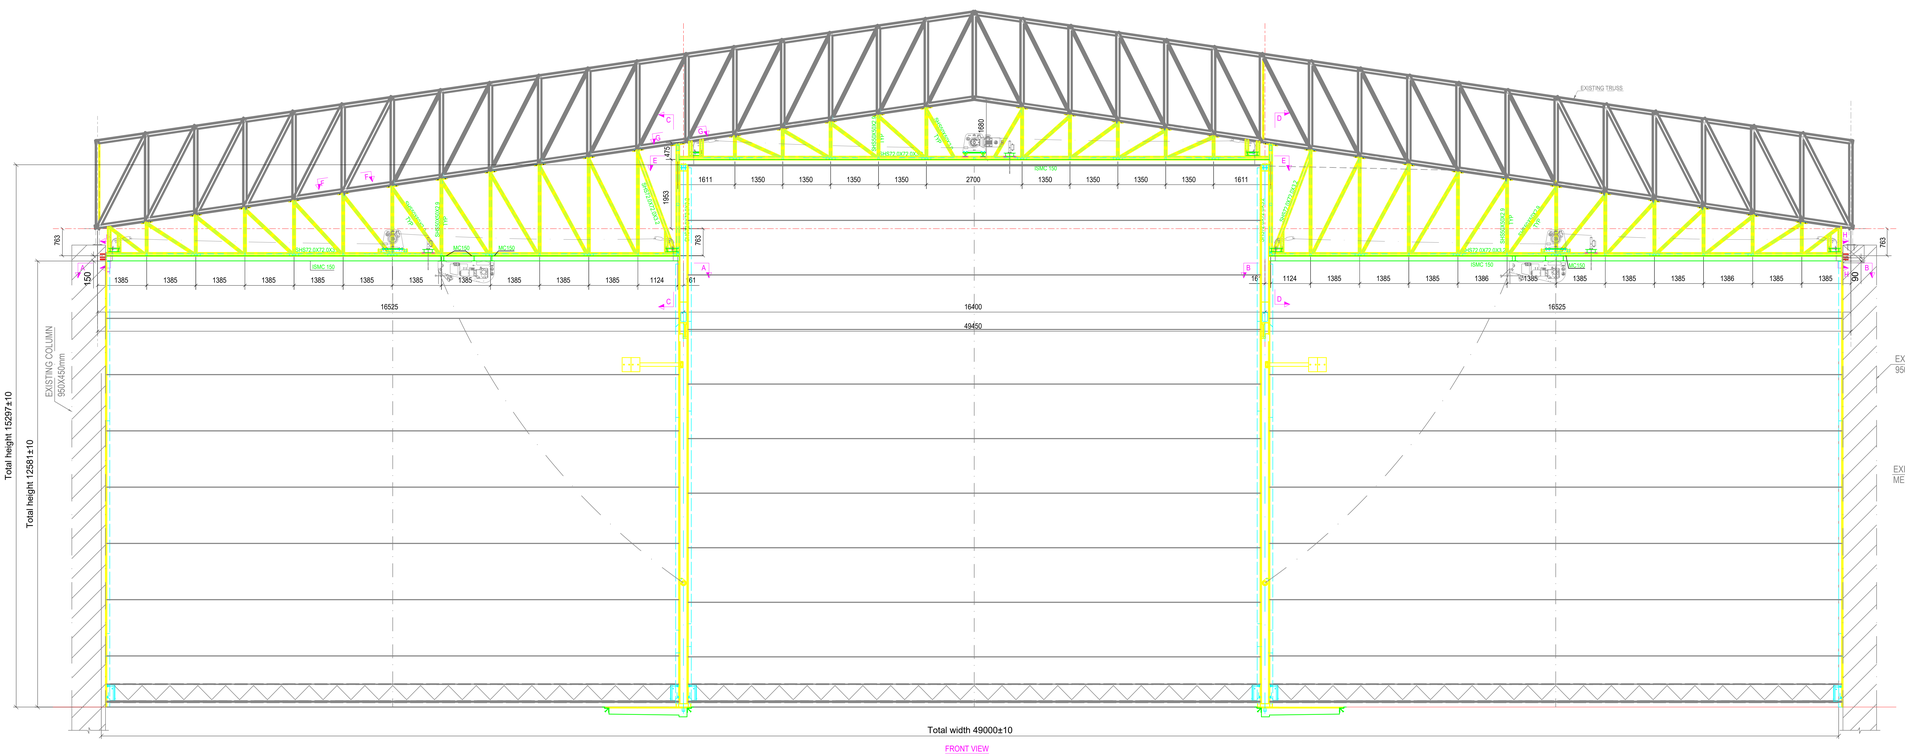


FRONT VIEW

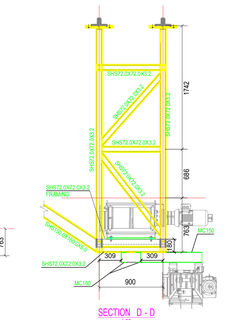

SECTION D - D
1:30

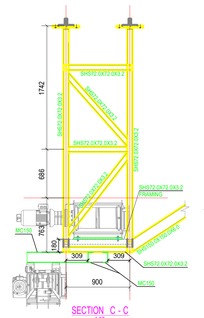


SECTION C - C
1:30

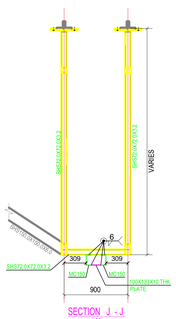


SECTION J - J
1:30


EXISTING COLUMN
950X450mm

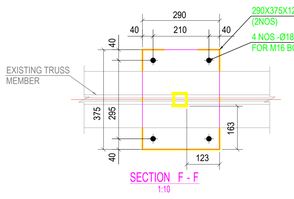

SECTION F - F
1:10

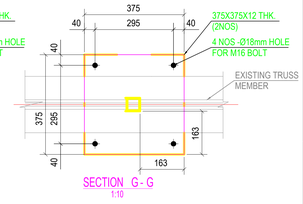

SECTION G - G
1:10

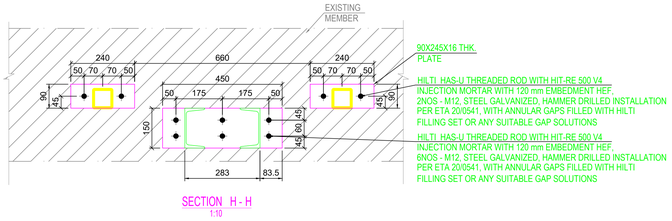


90X245X16 THK PLATE

HILTI HAS-U THREADED ROD WITH HIT-RE 500 V4 INJECTION MORTAR WITH 120 mm EMBEDMENT HEF. 2NOS - M12, STEEL GALVANIZED, HAMMER DRILLED INSTALLATION PER ETA 20/0541, WITH ANNULAR GAPS FILLED WITH HILTI FILLING SET OR ANY SUITABLE GAP SOLUTIONS

HILTI HAS-U THREADED ROD WITH HIT-RE 500 V4 INJECTION MORTAR WITH 120 mm EMBEDMENT HEF. 6NOS - M12, STEEL GALVANIZED, HAMMER DRILLED INSTALLATION PER ETA 20/0541, WITH ANNULAR GAPS FILLED WITH HILTI FILLING SET OR ANY SUITABLE GAP SOLUTIONS

SECTION H - H
1:10

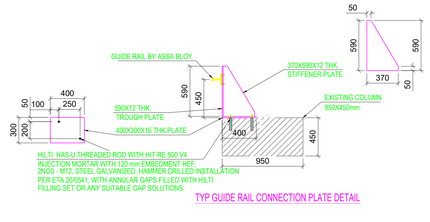

TYP GUIDE RAIL CONNECTION PLATE DETAIL

REV.NO.	DESCRIPTION.	REV.DATE	DRAWN.	CHKD.	APPD.
0					

DWG.TITLE :- STRUCTURAL DRAWING FOR DOOR FRAME

PROJECT	
CLIENT	Cochin International Airport

SALT Design Services

SALT DESIGN SERVICES
4-PUSHKAR NIRZAR, SBI COLONY,
NEAR ICICI BANK, KOTHRUD, PUNE-411038.

DRAWN :RRK	CHECKED : HAB	SCALE: 1:100
APPROVED : HAB	JOB CODE. : 1714	DATE: 14.07.2022
DWG.NO: SALT_1714_STR_01_R0	(SH-1OF1)	REV. - R0 SIZE. - A0