
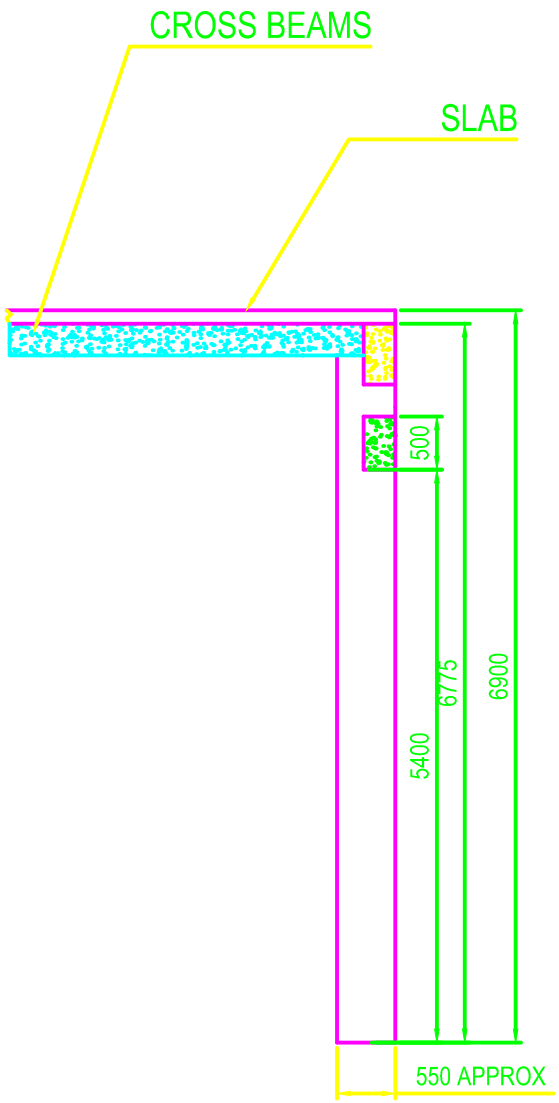


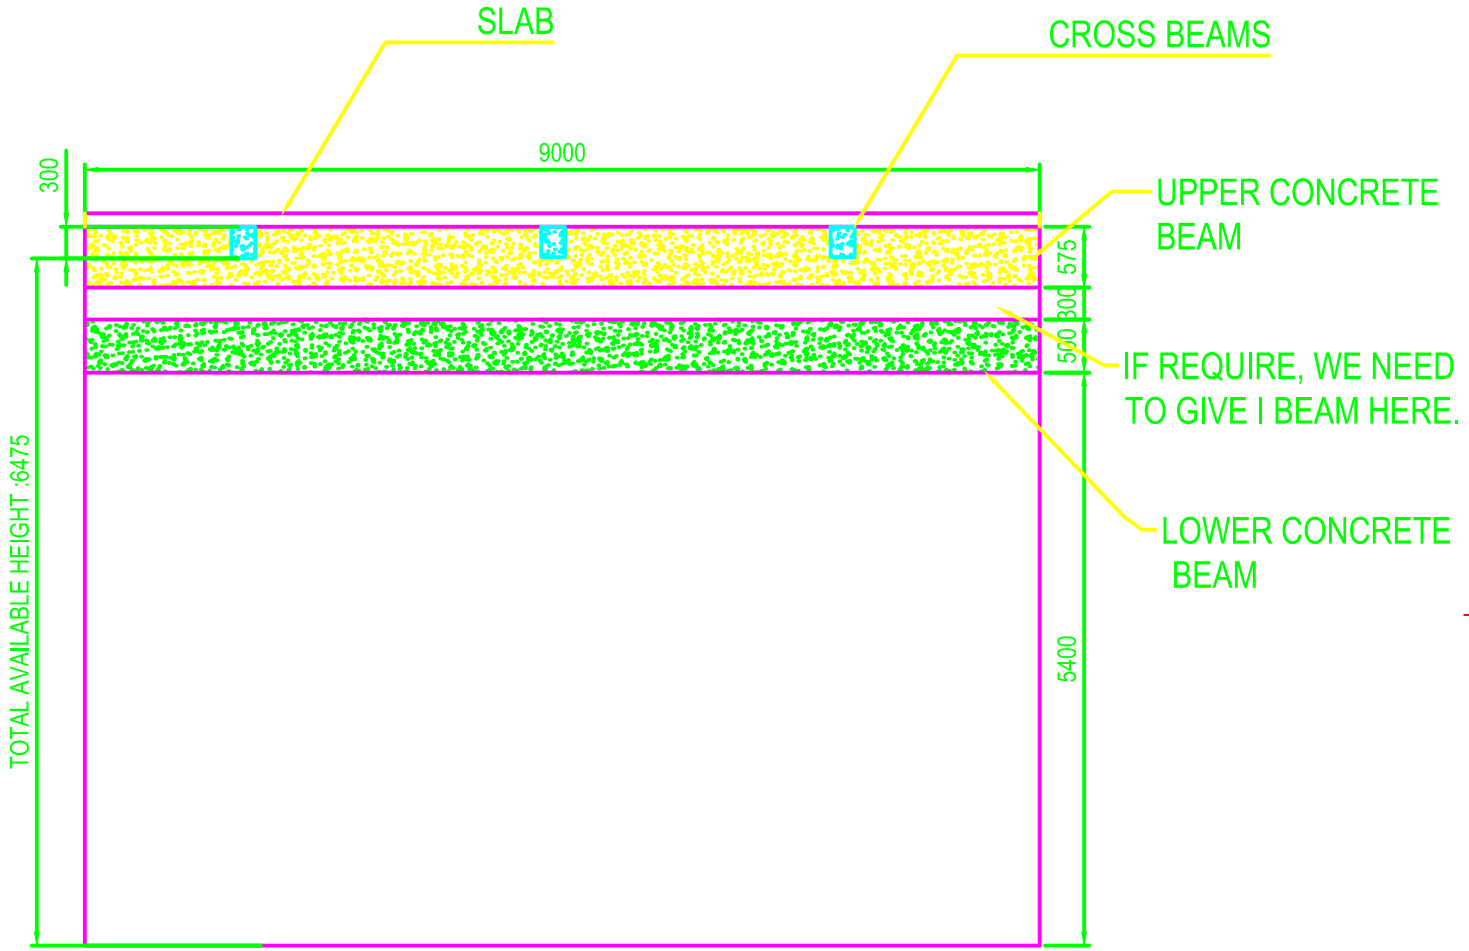

BEAM STRUCTURE AT SITE TERMINAL 5

NEW BUILDING : ARFF 5
CLEAR OPENING : 5400 X 9000
QTY : 2 NOS

This drawing & design is the property of NIHVA TEC-NOLOGIES. Not to be sold or copied to any other person

TITLE				
MEGA DOOR 5400 X 9000(ARFF5)				NIHVA TECHNOLOGIES PVT. LTD. PUNE Tel : 020 66304033 Email:- info@nihva.com Website:- www.nihva.com
	NAME	SIGN	DATE	
DRAWN	G.P.		21.08.2021	CLIENT -DIAL- L&T
CHECK	A.K.		21.08.2021	LOCATION - DELHI
APPRD.	V.T.		21.08.2021	PRODUCT - MEGA DOOR - 5400 X 9000
If any queries contact : design@nihva.com				NIHVA\20-21\0219 REV- 0
ALL DIMENSION ARE IN mm				SCALE: NTS SHEET: 02 OF 02

This document is the property of ASSA ABLOY Entrance Systems AB and shall not be reproduced or disclosed to any third party without the express written permission of ASSA ABLOY Entrance Systems AB. Infringement is subject to action and claims for damages.