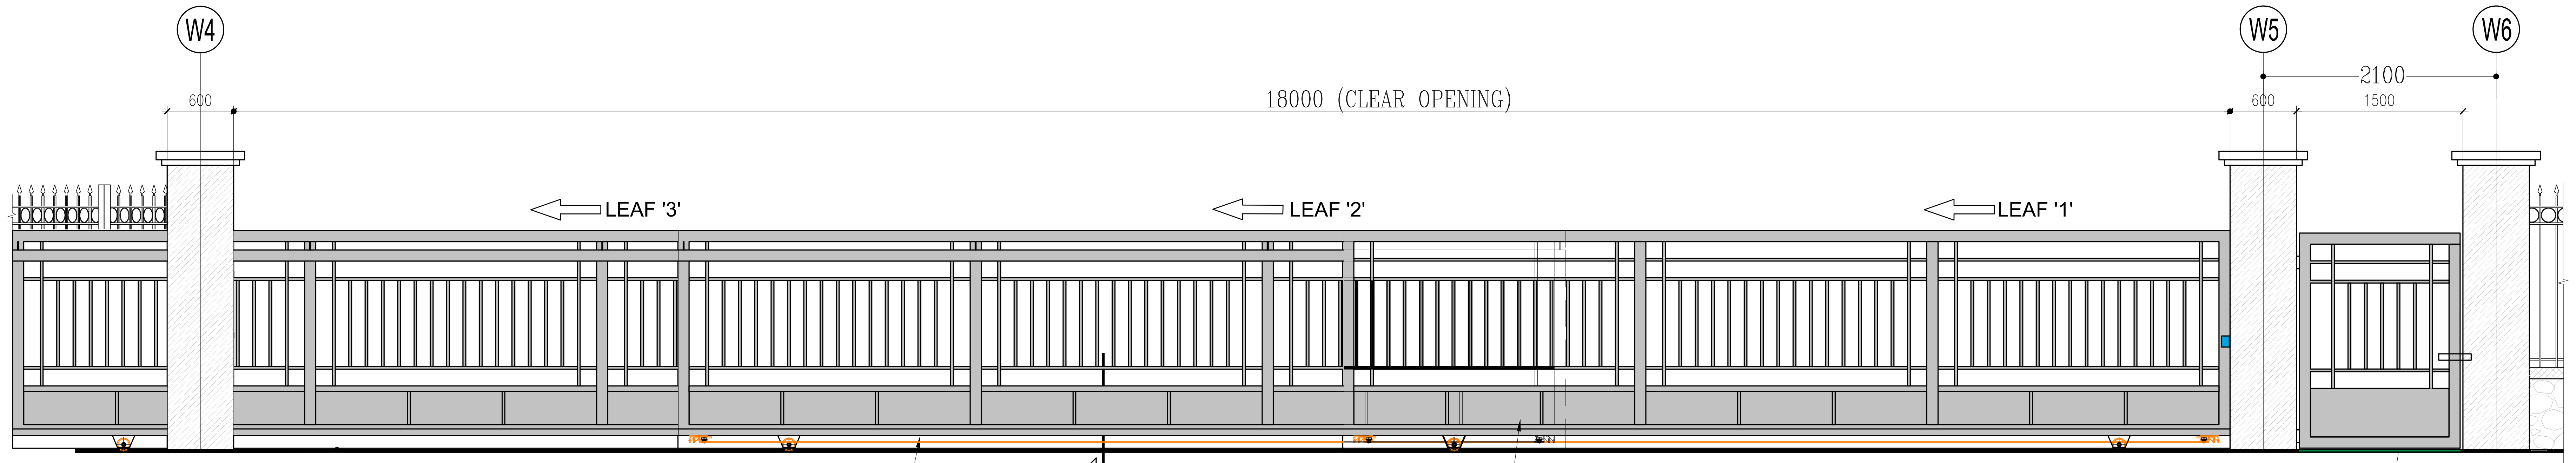

ELEVATION OF 18.0M WIDE GATE

SCALE 1:40

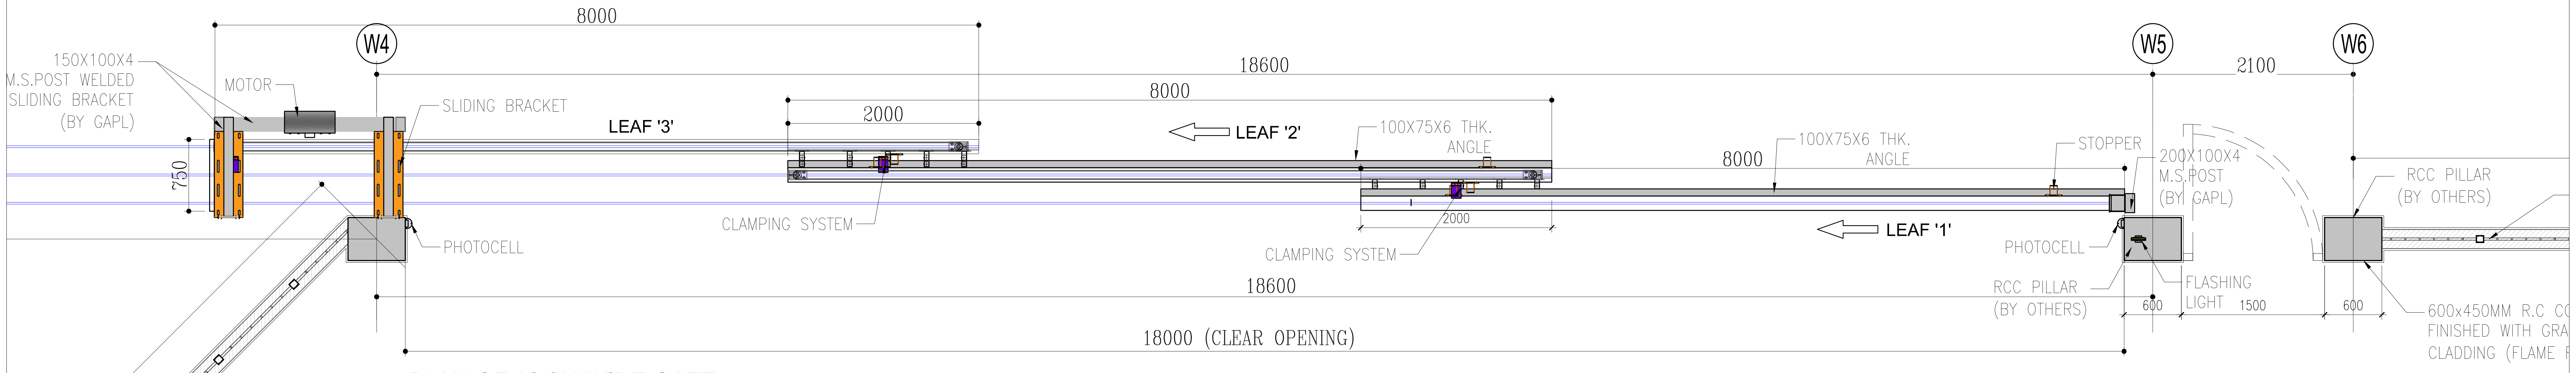

PLAN OF 18.0M WIDE GATE

SCALE 1:40

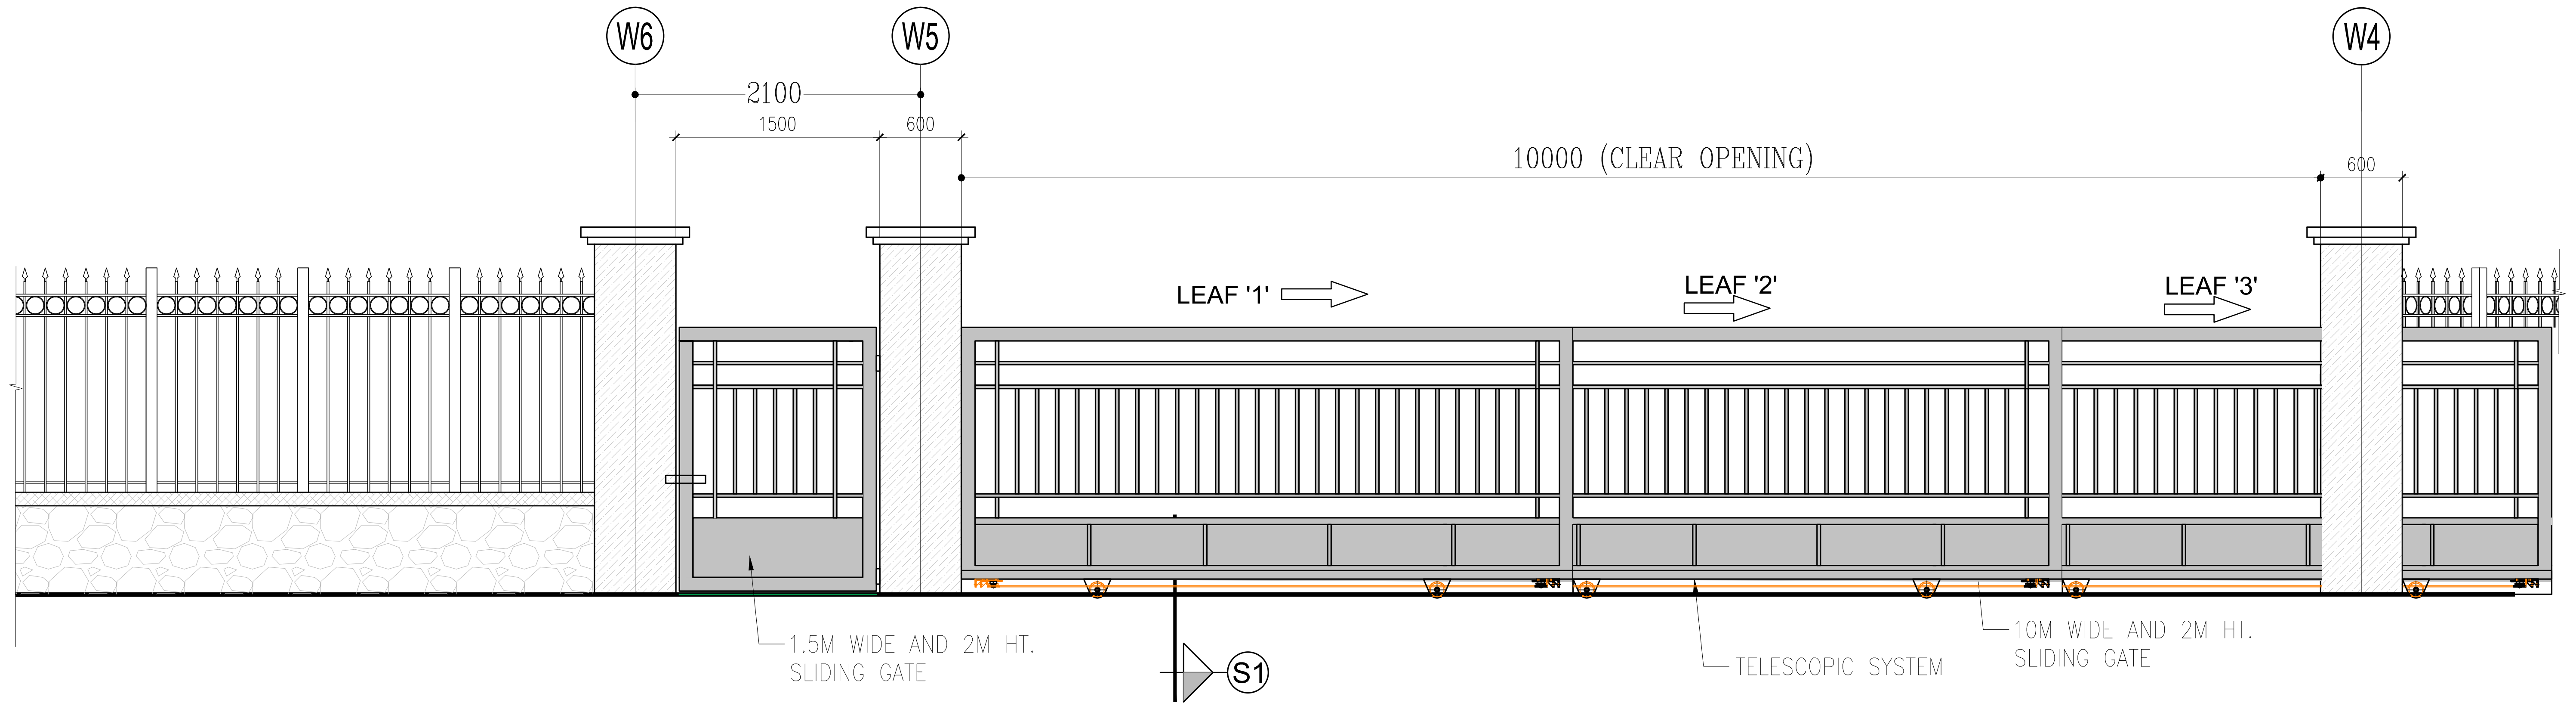

ELEVATION OF 10.0M WIDE GATE

SCALE 1:40

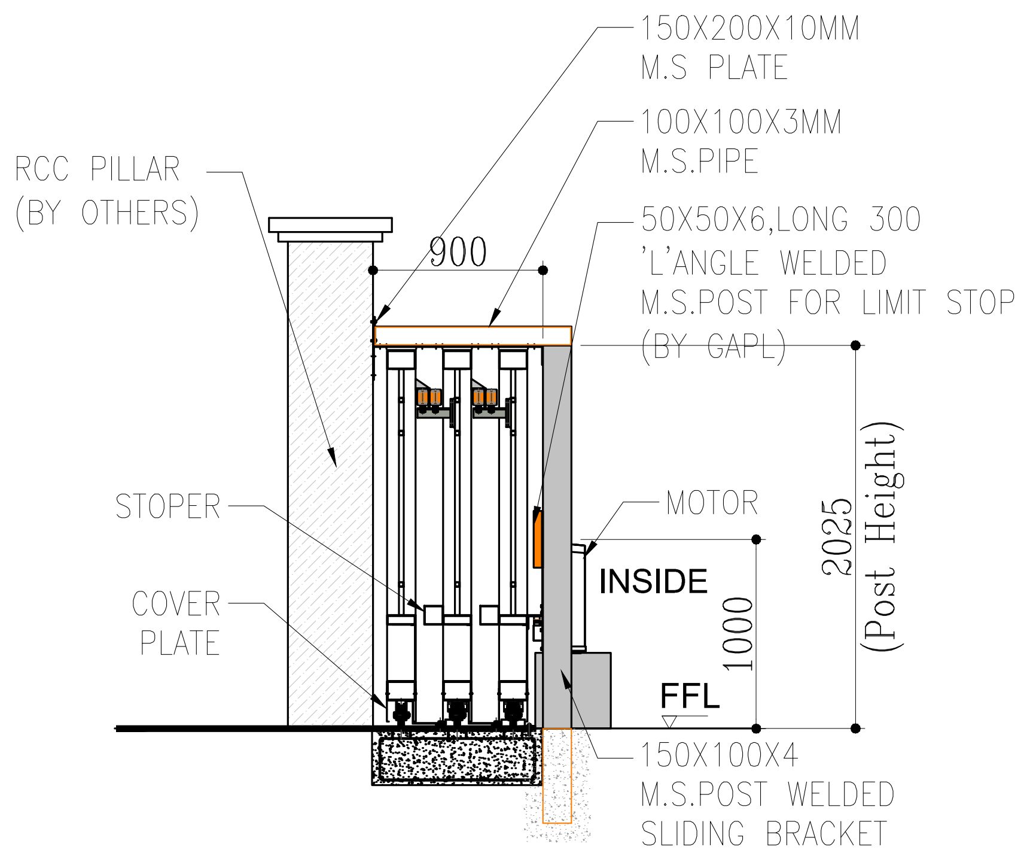

SECTION-S1

SCALE 1:50

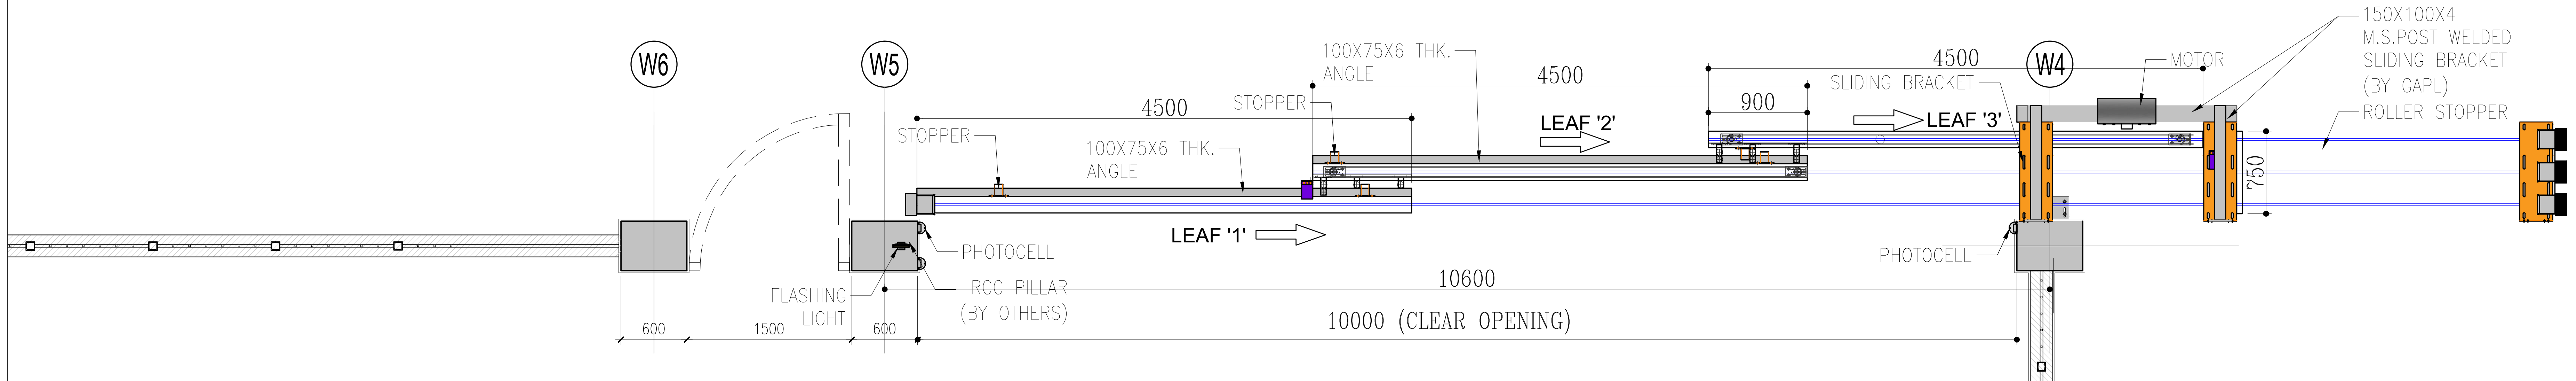

PLAN OF 10.0M WIDE GATE

SCALE 1:40

KEYPLAN :-

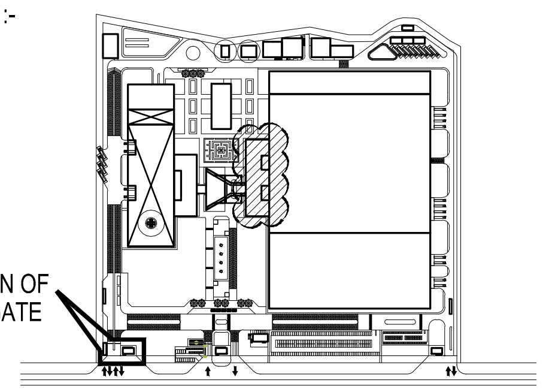

LEGEND :-

▨	R.C.C WALL
▨	150mm THICK SOLID BLOCK WALL
▨	200mm THICK SOLID BLOCK WALL

N

REV.	DESCRIPTION	DATE	BY	CHD.
R2	OPENABLE GATE DETAIL HAS BEEN REVISED INTO TELESCOPIC GATE	21.05.18	STA	GBK
R1	ISSUED FOR CONSTRUCTION	25.04.18	STA	GBK
S1	ISSUED FOR CLIENT APPROVAL	–	VP	GBK

AMENDMENT

GRAPHIC SCALE: 1M 0 1M 2M 4M 6M 8M 10M

CLIENT:

Emerson Process Management India private Limited, Pune

PROJECT:

Proposed Manufacturing facility for Emerson at Chakan, Pune

DRAWING TITLE:

SITE DEVELOPMENT WORK
18MTS.&10MTS WIDE - GATE DETAILS

(SHEET 1 OF 2)

SCALE : 1:40
DRAWN :PARVATHI.V
DATE : 19.09.17
CHKD : GBK
REV
DRAWING NO:
EPIPL-P-SITE-AR00-08-01-226223
R2

PROJECT MANAGEMENT:

CBRE South Asia Pvt. Ltd | Project Management Group - Pune
3rd Floor, East Wing | Nyati Unitree
Samrat Ashok Marg (Nagar Road)
Yerwada | Pune 411 006 - India
T (91 20) 40190 100 | F (91 20) 2605 5405

design | interiors | engineering | construction management

C.R.Narayana Rao (Consultants) Private Limited

C R NARAYANA RAO

No. 10, Karpagambal Nagar,
Mylapore, Chennai-600 004.
India.
www.crn.co.in

Construction work shall be executed only as per the latest revision drawing. Once a revision drawing is issued, the validity of the previous revision drawing stands cancelled and as such construction shall not be carried out as per superseded revisions. The Contractor is expected to:

1. Maintain a register of Drawing Receipts, listing drawing number & revision number, title, from whom received, date received, number of copies received, details of transmittal from the issuer & any other relevant details to be advised from time to time.
2. Archive all previous revision issues immediately upon receipt of a new revision and no superseded drawing shall remain in the site of works except in the Contractor's archives for record and reference purposes only.
3. While archiving superseded drawing, the Contractor is expected to stamp all previously issued drawings / prints appropriately, mentioning the date and revision number of the new revision on account of which the previous revision is archived.
4. The Contractor shall allow the representative of Client / PMC / Architect to inspect Contractor's archives for ensuring compliance.
5. Any work carried out by the Contractor using a superseded drawing after the issue of a new revision is liable for rejection and reinstatement as per new revision at Contractor's risk and cost without any entitlement to extension of time

THESE DRAWINGS ARE UNDER COPYRIGHT AND ARE THE PROPERTY OF CRN. NONE OF THE DRAWINGS AND RELATED DOCUMENTS CAN BE REPRODUCED, COPIED IN WHOLE OR IN PART WITHOUT PRIOR EXPRESSED WRITTEN CONSENT OF CRN. THESE DRAWINGS CANNOT BE HANDED OVER TO A THIRD PARTY OR USED FOR ANY PURPOSE, OTHER THAN THAT FOR WHICH IT HAS BEEN LOANED. AFTER FULFILLING THE PURPOSE OF ISSUE THE DRAWINGS SHALL BE RETURNED TO CRN.