

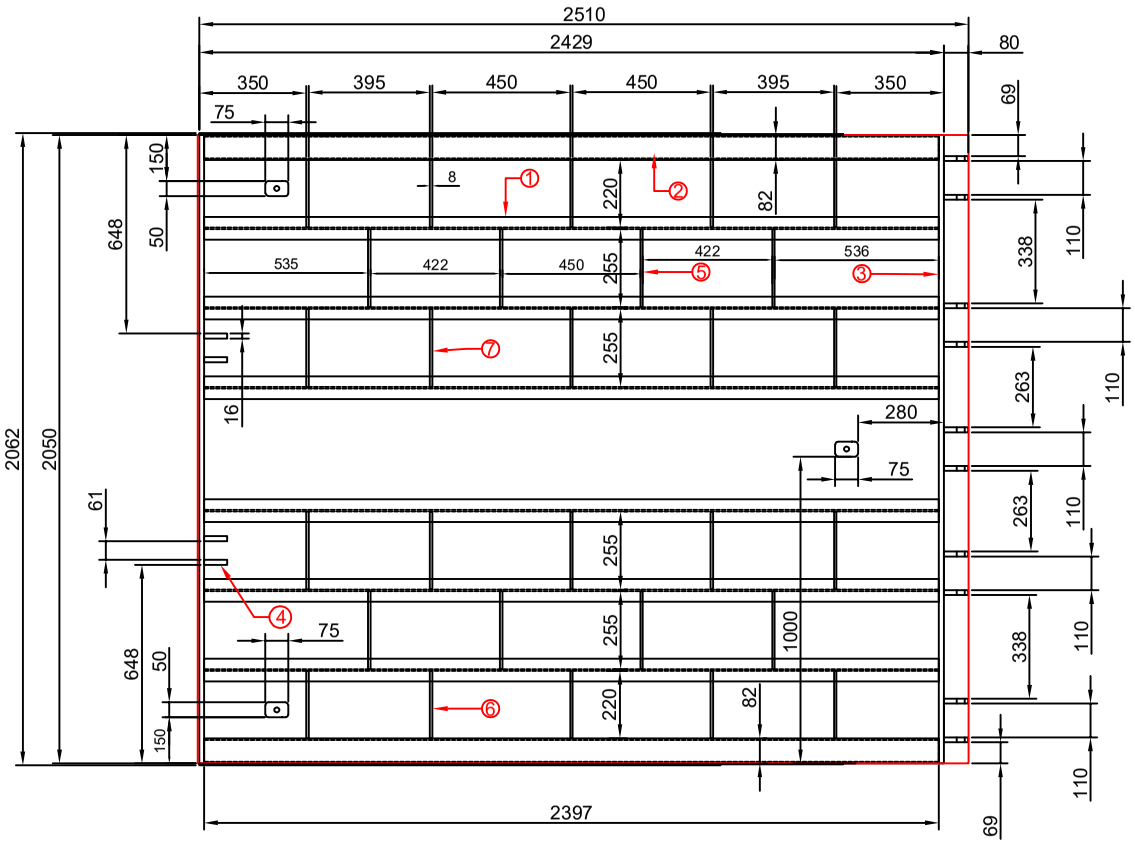


BOM			
SL NO.	DESCRIPTION	SPECIFICATION	QTY
1	ISMB	150X75X2397L	6NOS
2	MS RECT.TUBE	145X82X2397X5.4THK	2NOS
3	MS FLAT	150X16X2050L	2NOS
4	CYLINDER MTG BKT	75X75X16THK	4NOS
5	MS FLAT	100X8X255L	8NOS
6	MS FLAT	100X8X220L	10NOS
7	MS FLAT	100X8X255L	10NOS
8	L BEND	100X2100X3THK	2NOS
9	HOLDING BKT	100X80X16THK	10NOS
10	SIDE COVER	180X1700X3THK	2NOS
11	CHEQ.SHEET	2515X2050X8THK	1NO
12	EYE BOLT	M16XSTD WITH NUT	3NOS
13	EYE BOLT MTNG BKT	50X75X16	3NOS
14	MS FLAT	25X5X100	20NOS
15	MS BRACKET	50X106X16	2NOS
16	MS FLAT	75X10X115	1NO

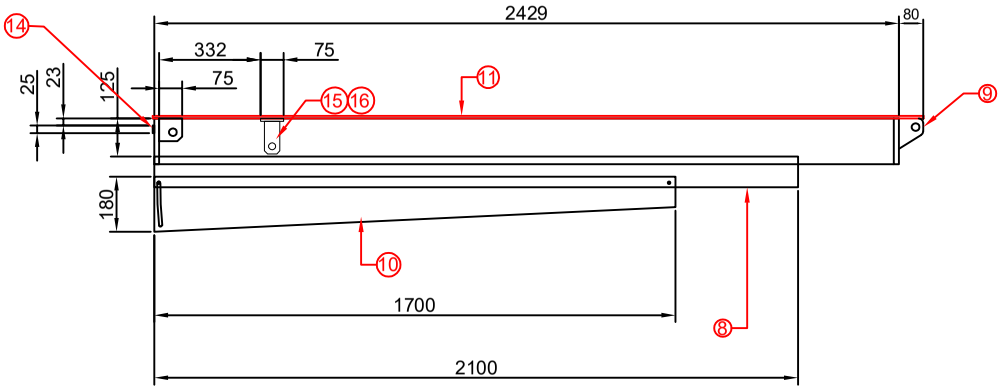

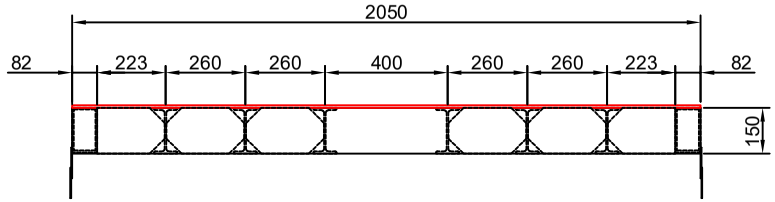

NOTE:-

1.All dimension are in MM

2.Above given quantity in the table is one for single dock

This drawing & design is the property of NIHVA TECHNOLOGIES. Not to be sold or copied to any other concern.

TITLE: DECK FRAME

NIHVA TECHNOLOGIES PVT. LTD.
NIHVA TECHNOLOGIES PVT. LTD. PUNE
Tel : 020 66304033
Email:- info@nihva.com
Website:- www.nihva.com

	NAME	DATE	SIGN
DRAWN	SUJATA	22/04/2022	
CHECK	M.SUTAR	22/04/2022	
APPRD.			

CLIENT - ABHI BUILDCON

LOCATION - PUNE

PRODUCT - DOCK LEVELER

If any queries contact : design@nihva.com

DWG NO:-NIHVA/22-23/MFG/0002 | REV- 0

ALL DIMENSION ARE IN mm | SCALE: NTS | SCALE:-- 1:1 | SHEET: 01 OF 01

Rev No.	Revision	Date	Revised By