A1

CROWN PORTAL TOP +89.90M


O.H.T SLAB BOTTOM LEVEL +88.10 M

TERRACE LEVEL +85.10 M


22ND FLOOR LEVEL +82.10 M

21ST FLOOR +79.10 M


OHT SLAB TOP LEVEL + 92.60 M

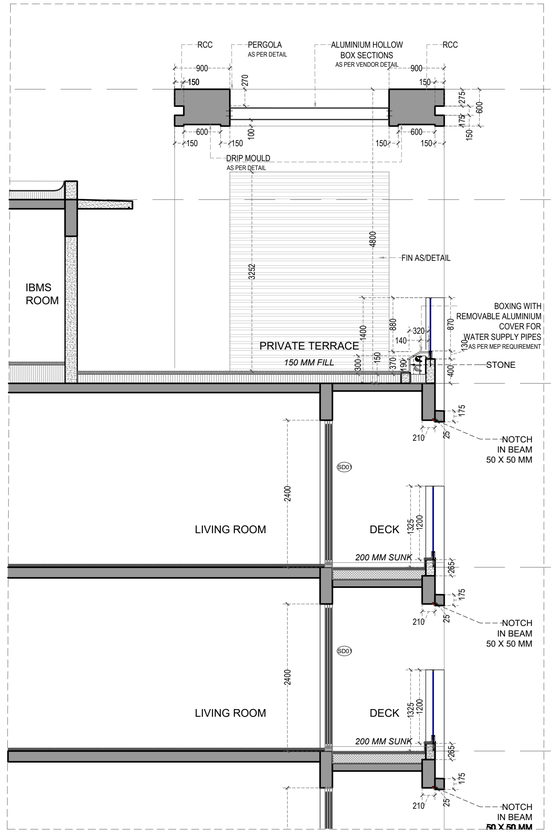



SECTION -1

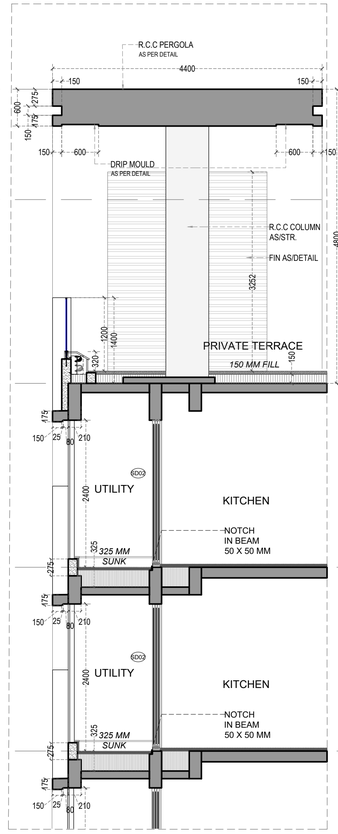



SECTION -2

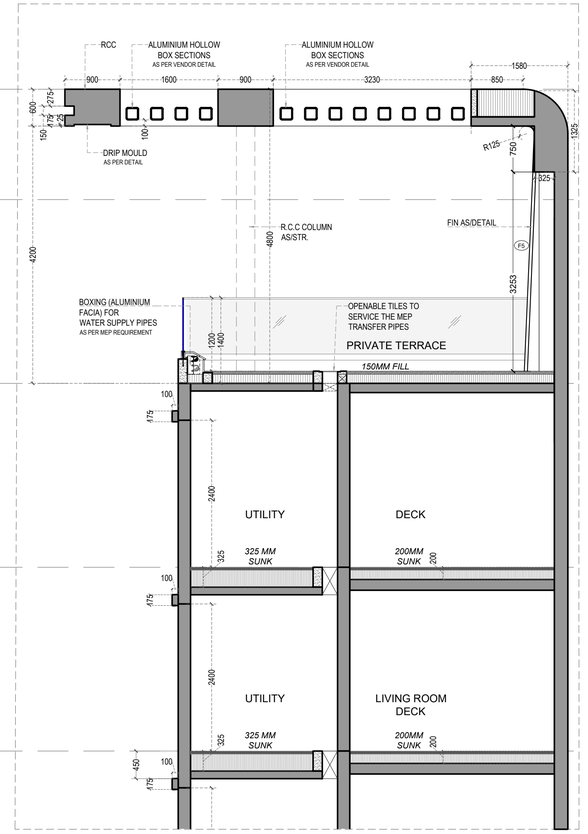


SECTION -2A

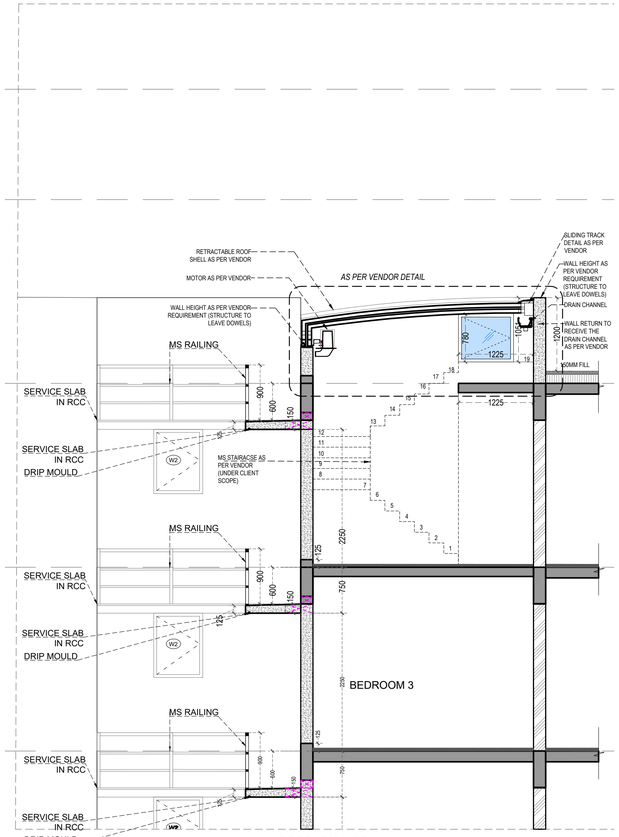


SECTION -3D

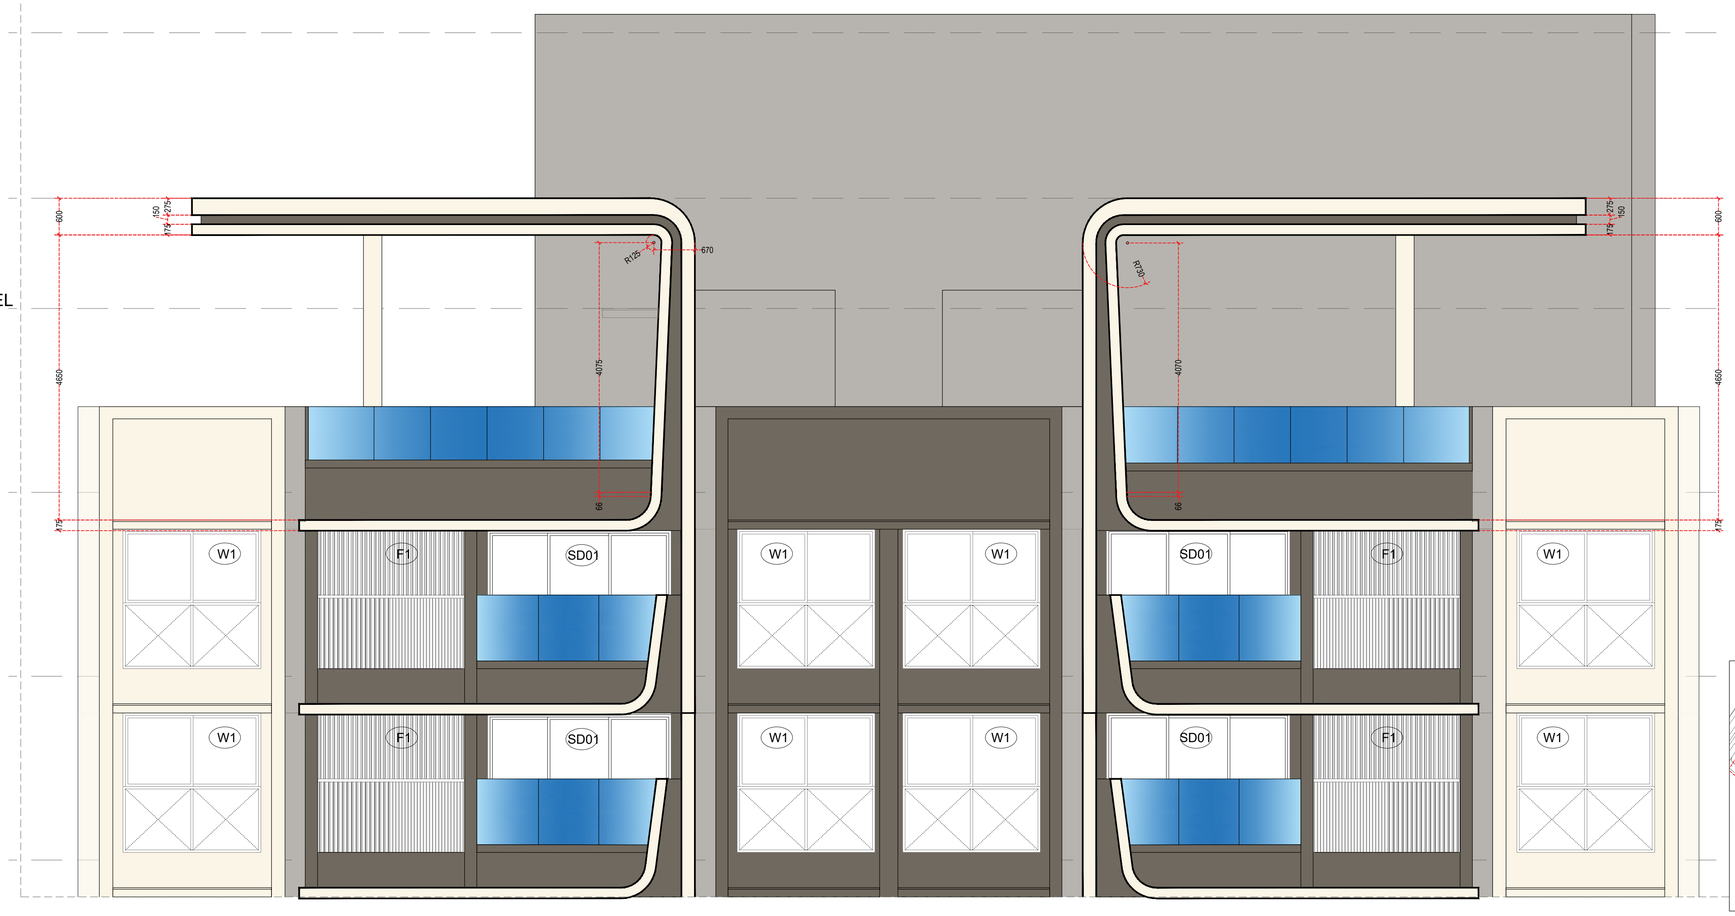


Jagadishponraj Nadar

Digitally signed by: Jagadishponraj Nadar
DN: CN = Jagadishponraj Nadar OU = Lodha Users
Date: 2026.07.01 16:12:40 +06'30'

Vaibhav Shimpi

Digitally signed by: Vaibhav Shimpi
DN: CN = Vaibhav Shimpi OU = Lodha Users
Date: 2026.07.01 15:40:54 +06'30'

Digitally signed by: SUPRIYA UKIDAVE
Date: 2026.07.01 11:59:12 +06'30'

KEYPLAN (NTS)

GENERAL NOTES

1 : All dimensions are in millimeters and levels in meters unless specified otherwise.
2 : Do not scale the drawing; follow written dimensions.
3 : All dimensions are unfinished dimensions unless specified otherwise.
4 : Any discrepancies should be brought to the notice of the Architect prior to execution of job / procuring materials at site.
5 : This drawing is the property of Kapadia Associates and should not be reproduced, copied, handed over to a third party or used for any purpose other than for which it has been issued.
6 : This drawing is to be read in conjunction with all relevant structural & services drawings.

NOTE:

1. PLEASE READ IN CONJUNCTION WITH KITCHEN DETAIL,TOILET DETAIL, FIN DETAIL & RAILING DETAIL, STARICASE DETAILS.
2. 10MM ADDITIONAL COVER HAS BEEN INCLUDED IN THE SHEAR WALL THICKNESS, WHEREVER REQUIRED FOR GROOVE.

REVISION INDEX

| REV. NO. | DATE | REMARKS |
|---|---|---|
| R00 | 24-04-2026 | VFC ISSUED |
| R01 | 30-06-2026 | SERVICE SHAFTS, RETRACTABLE ROOF,OHT LAYOUT REVISED |
| | | |
| | | |
| | | |
| | | |

CLIENT

**LODHA GROUP**

PROJECT TITLE

**LODHA RISERVO - A4**

VIKHROLI,MUMBAI

DRAWING TITLE & NO.

**AR-KA-A4-401.1_TERRACE WALL SECTIONS**

DRAWING STAGE

**WORKING DRAWING**

| SCALE | REV. NO. | REV. DATE |
|---|---|---|
| 1:50 | R01 | 30-06-2026 |

STAMP & SIGNATURE


KAPADIA ASSOCIATES
architecture • urban design
112-114, Peninsula Centre,Dr. S.S. Rao Road,Parel East, Mumbai 400012
Tel : 91-22-6660 2838 / 39 E-mail : kapl@kapl.in Website : www.kapl.in