

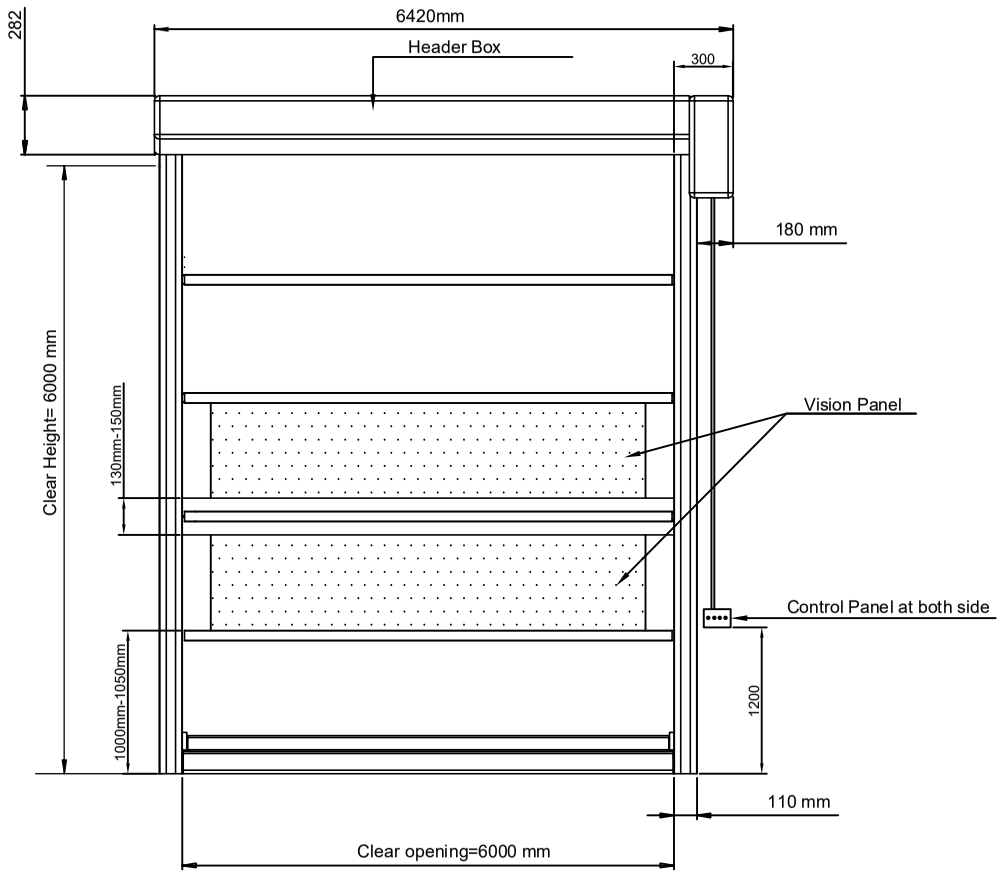


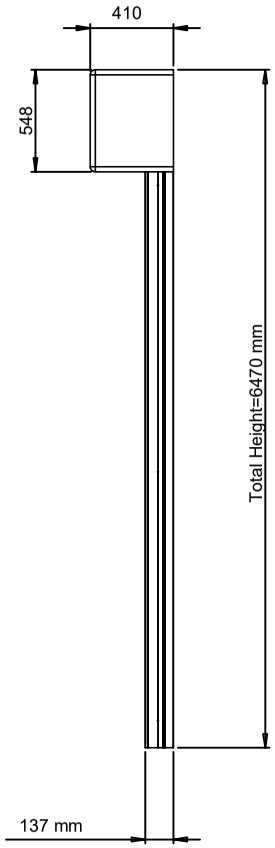

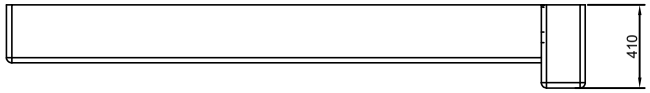

RAL CODE	SHADE
RAL 1018	
RAL 1019	
RAL 5010	
RAL 3020	
RAL 7035	
RAL 7016	
RAL 9006	

Note:--

1) All Dimension are in MM
2) Opening speed will be 0.5-1.5m/s
3) 1.5kw motor will be used
4) All curtain are closed vinyl(pvc)
5) Segment height can be change from the bars 50 to 100mm

Rev No.	Revision	Date	Revised By
1.	Total height of the door has been changed from 6020mm to 6470mm +150mm installation space	24/08/2022	Sujata
2.	Vision panel, control panel,Segment height tolerance has been added.	10/11/2022	Sujata
3.	Door qty has been changed	18/01/2023	Sujata

This drawing & design is the property of NIHVA TECHNOLOGIES. Not to be sold or copied to any other concern.

TITLE:- HIGH SPEED DOOR

NIHVA TECHNOLOGIES PVT. LTD.

NIHVA TECHNOLOGIES PVT. LTD. PUNE
Tel : 020 66304033
Email:- info@nihva.com
Website:- www.nihva.com

	NAME	DATE	SIGN
DRAWN	SUJATA.B	09/08/2022	
CHECK			
APPRD.	AMIT.K	09/08/2022	

CLIENT - RONAK BUILD.

LOCATION -Pune

PRODUCT - HSD

If any queries contact : design@nihva.com

DWG NO:-NIHVA/21-22/CLT/0104_1 REV- 03

ALL DIMENSION ARE IN mm

SCALE: NTS SCALE:-- 1:1 SHEET: 01 OF 01