




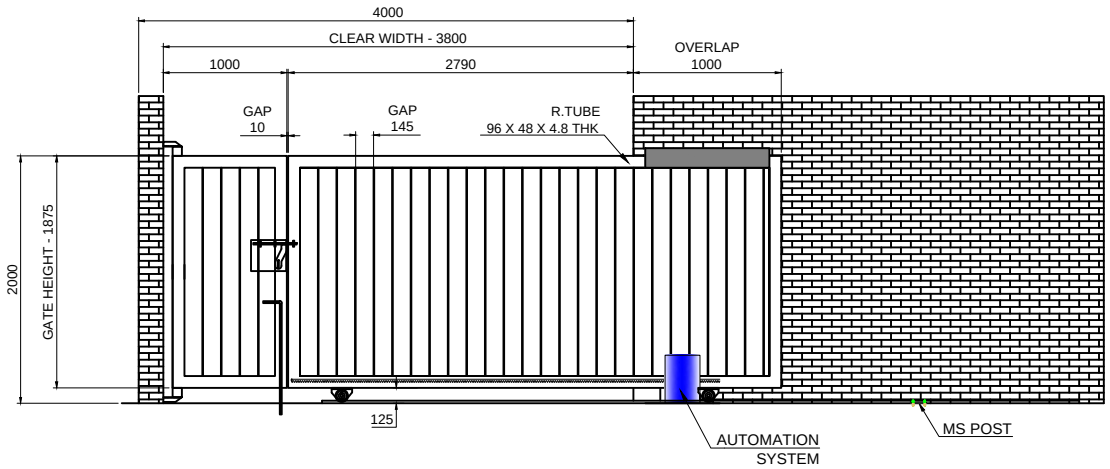

VIEW FROM INSIDE

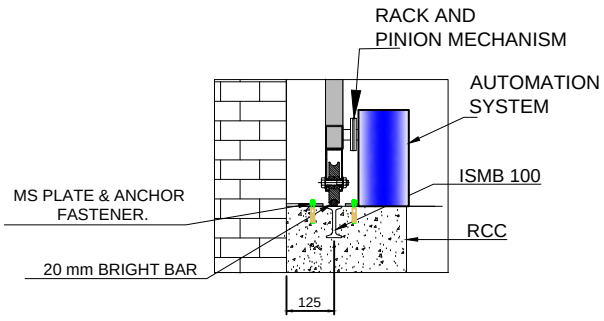

DETAIL VIEW OF A

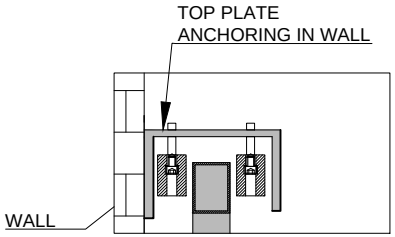

DETAIL VIEW OF B

SR.NO	RAL CODE	RAL COLOR
01	RAL 7015	LIGHT GRAY

DIMENSION :

CLEAR WIDTH	CLEAR HEIGHT	QUANTITY
2800 mm	1875mm	1 NO
1000 mm	1875mm	1 NO

MATERIAL: MS

THICKNESS :

NOTE-
1. ALL REQUIRED CIVIL WORK WILL BE IN CLIENTS SCOPE.

TOLERANCE:- ± 05mm

NIHVA TECHNOLOGIES PVT. LTD.
Website:- www.nihva.com
NIHVA TECHNOLOGIES PVT. LTD. PUNE
Email:- info@nihva.com
TEL :020 66304033

TITLE:
AUTOMATIC SINGLE LEAF SLIDING GATE & MANUAL WICKET GATE

CLIENT'S APPROVAL :

CLIENT -

PROJECT -

SITE LOCATION -

DWG. NO. : NIHVA/19-20/VDR/223 | REV. : R00

SCALE: NTS | WT: | SHEET:1 OF 1

DRAWN	P.A		18.11.2019
CHECK	G.J		18.11.2019
APPROVED			

IF ANY QUERIES CONTACT:- design@nihva.com

NOTE: ALL DIMENSIONS ARE IN mm

THIS DRAWING & DESIGN IS THE PROPERTY OF NIHVA TECHNOLOGIES. NOT TO BE SOLD OR COPIED TO ANY OTHER CONCERN.