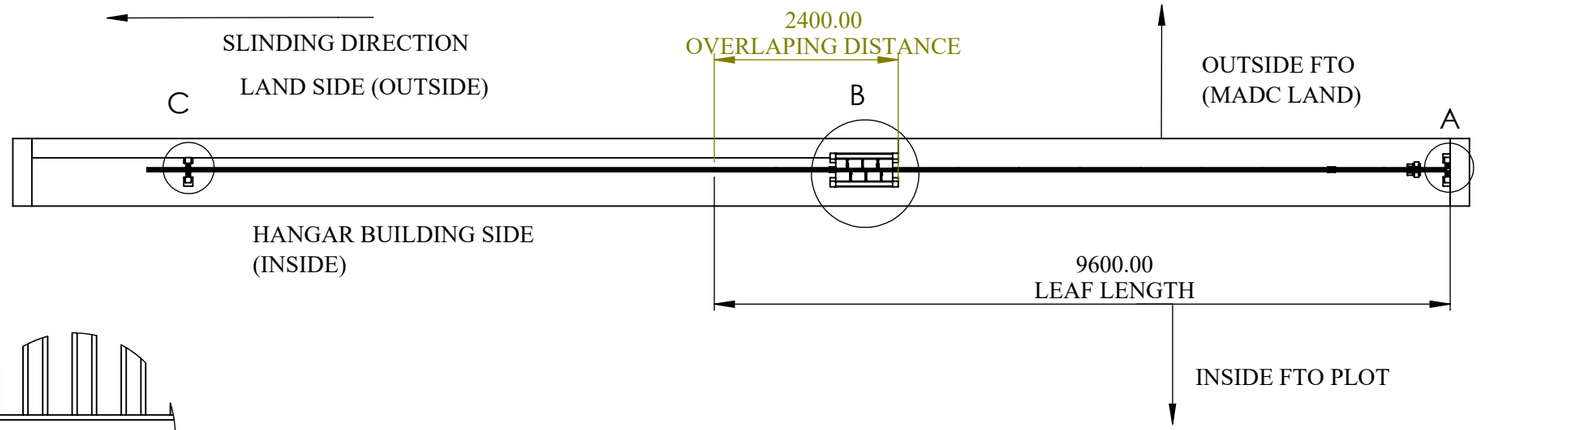
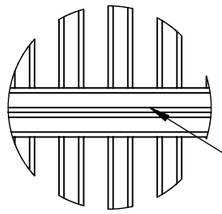
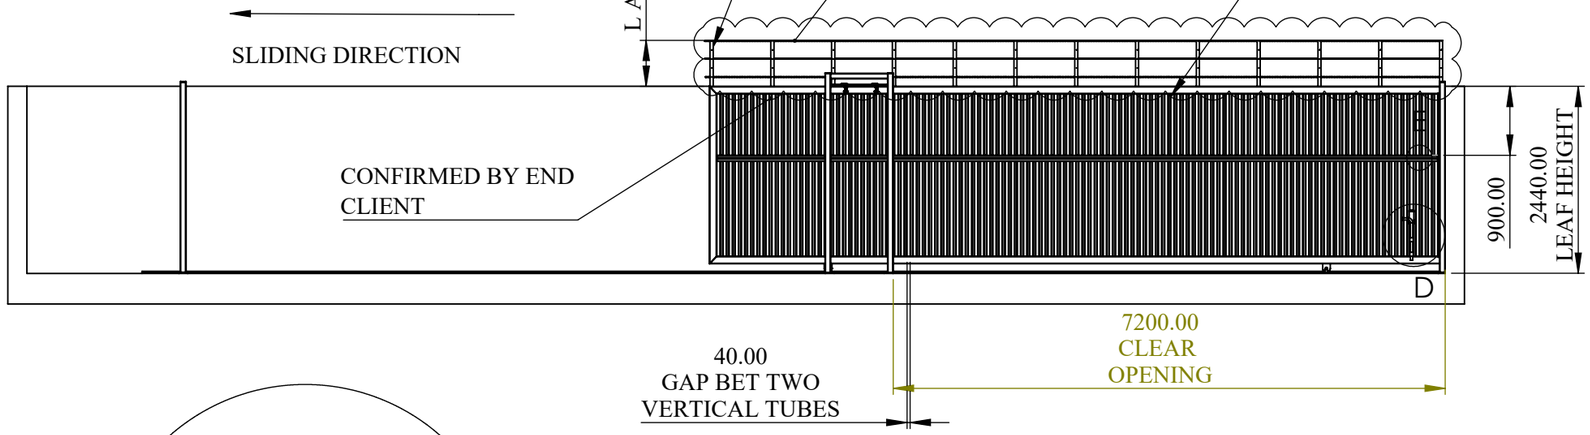
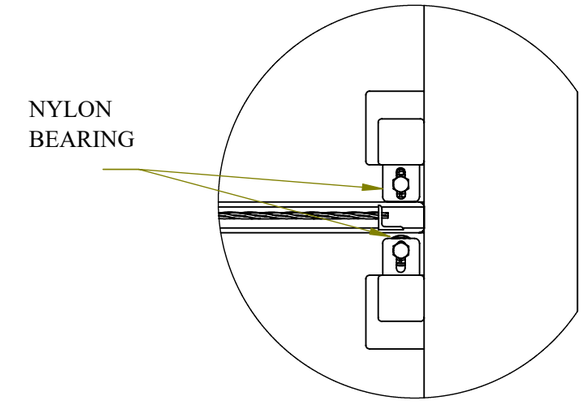


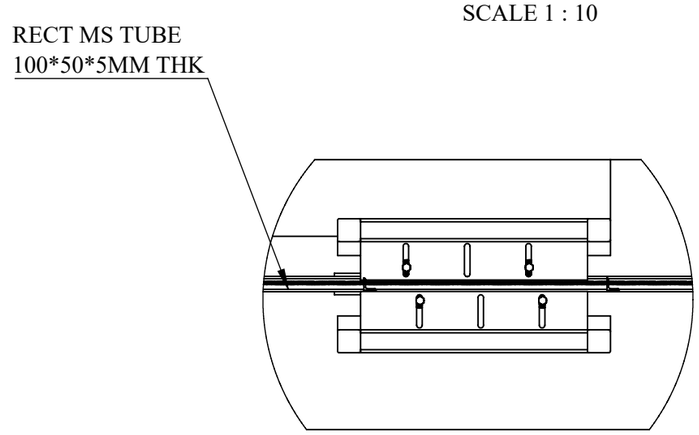

DETAIL E
SCALE 1 : 10



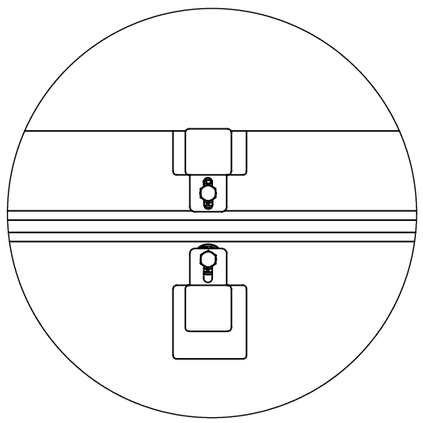

POST 1 AND NYLON
BEARING ASM

DETAIL A
SCALE 1 : 10



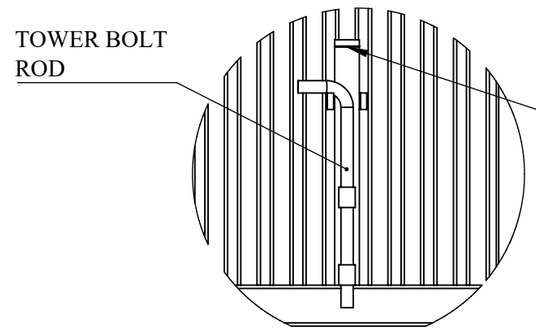

POST 2 AND NYLON
BEARING ASM

DETAIL B
SCALE 1 : 20



POST NO 3 &
NYLON ROLLER BERAING
ASM

DETAIL C
SCALE 1 : 10




TOWER BOLT LOCKING
ARRANGEMENT.

DETAIL D
SCALE 1 : 15

**NOTE :**
**GA DRAWING TYPE NO 01**

| | | | | |
|---|---|---|---|---|
| TITLE - GATE AUTOMATIOM | | | | NIHVA TECHNOLOGIES PVT.LTD.PUNE<br>Website - www.nihva.com |
| DWG NO - NTPL-000-PM-001-00-00-00 | | | | |
| | NAME | SIGNATURE | DATE | PROJECT NO - NTPL-000-PM |
| DRAWN | V.W | | 21-05-2025 | PRODUCT - SINGLE SLIDING GATE |
| CHK'D | S.W. | | 21-05-2025 | SITE LOCATION - |
| APPV'D | V.T. | | 21-05-2025 | |
| if any queries contact - supportautomation@nihva.com | | | | REVISION - 01 / QTY - 1 |
| ALL DIMENSION ARE IN mm | | A3 | | SCALE / SHEET 1 OF 1 |