


REV.	DESCRIPTION.	REVISED BY	SIGN	DATE
000	RELEASED GA DWG FOR APPROVAL	MAHESH S.		30.11.22
001	MODIFIED GA DWG PER SITE CHANGES	MAHESH S.		30.12.22

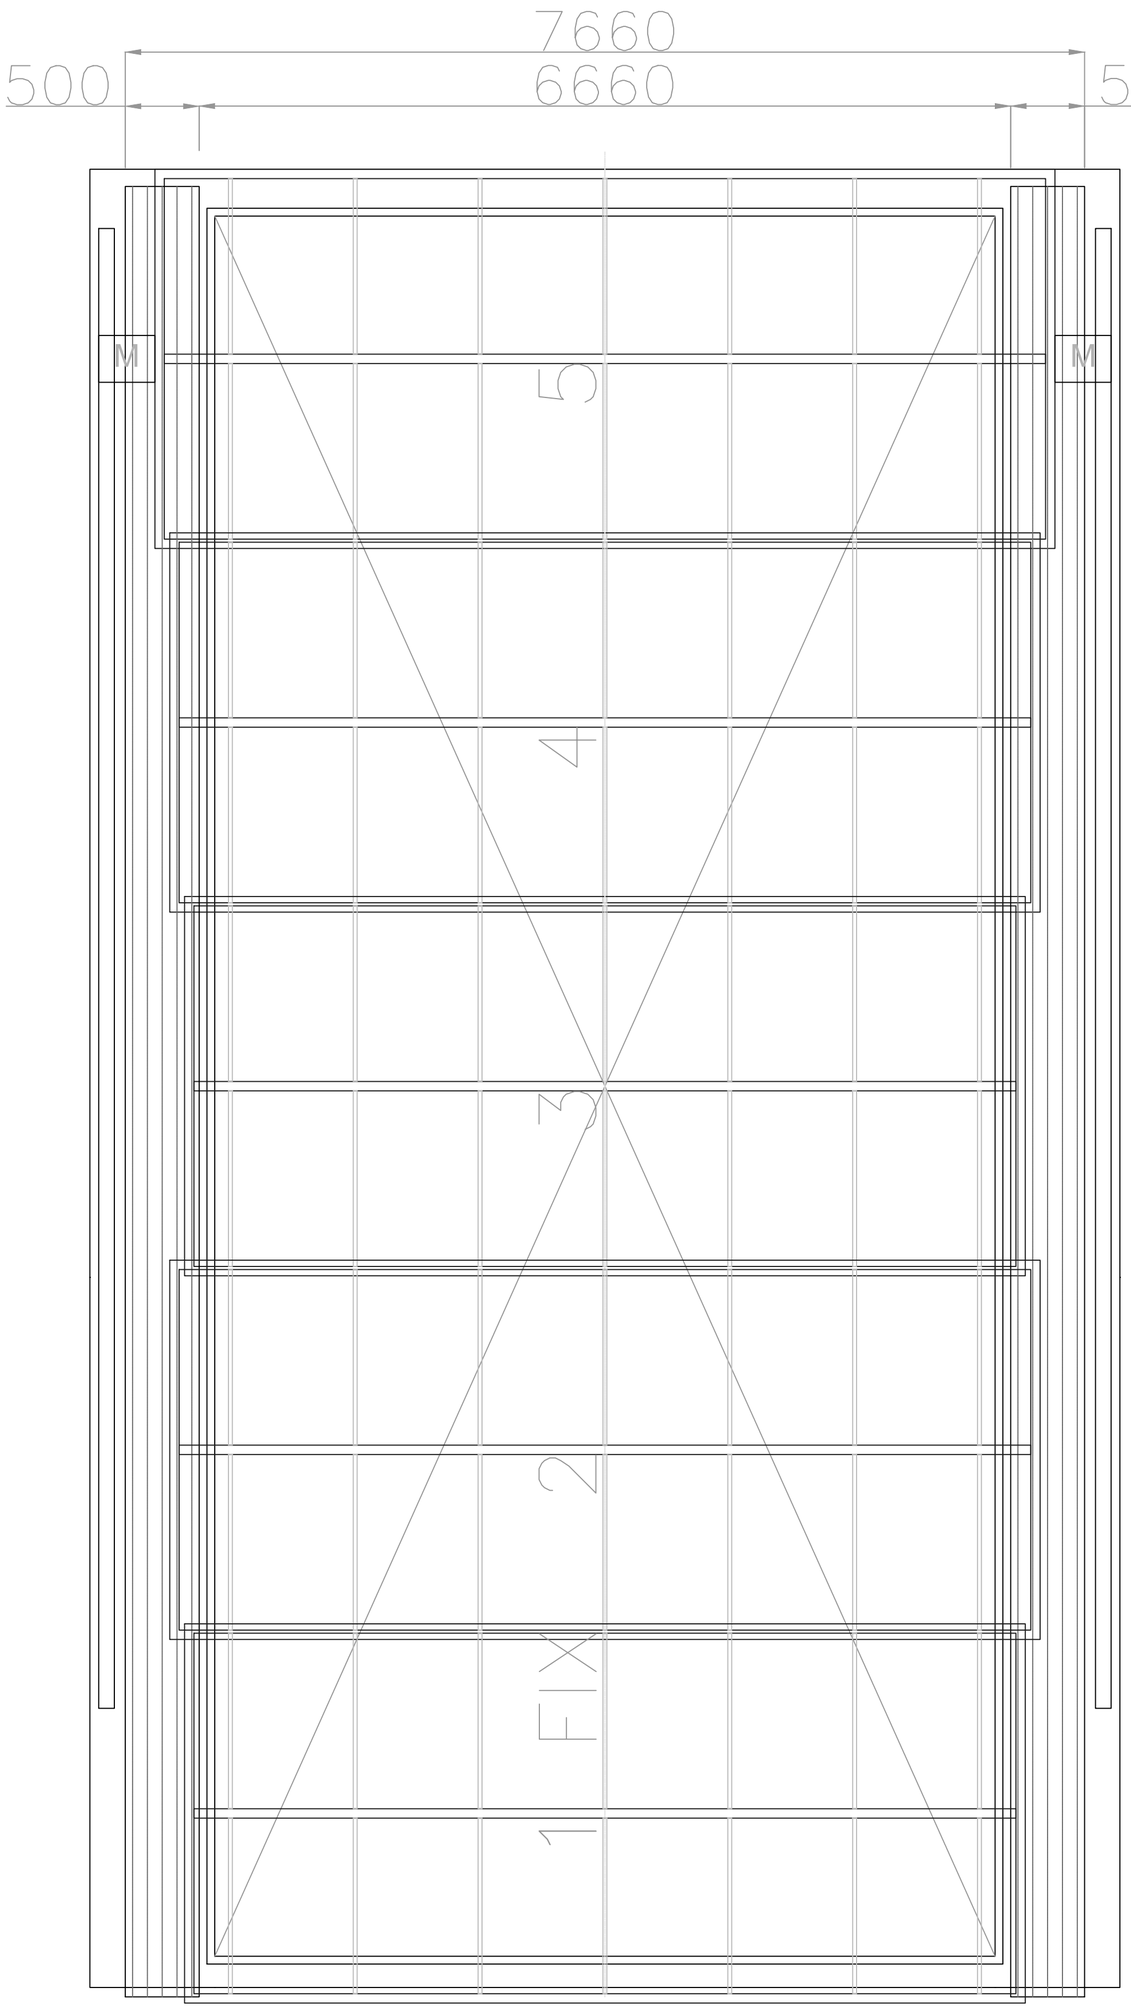

ENCLOSED PLAN

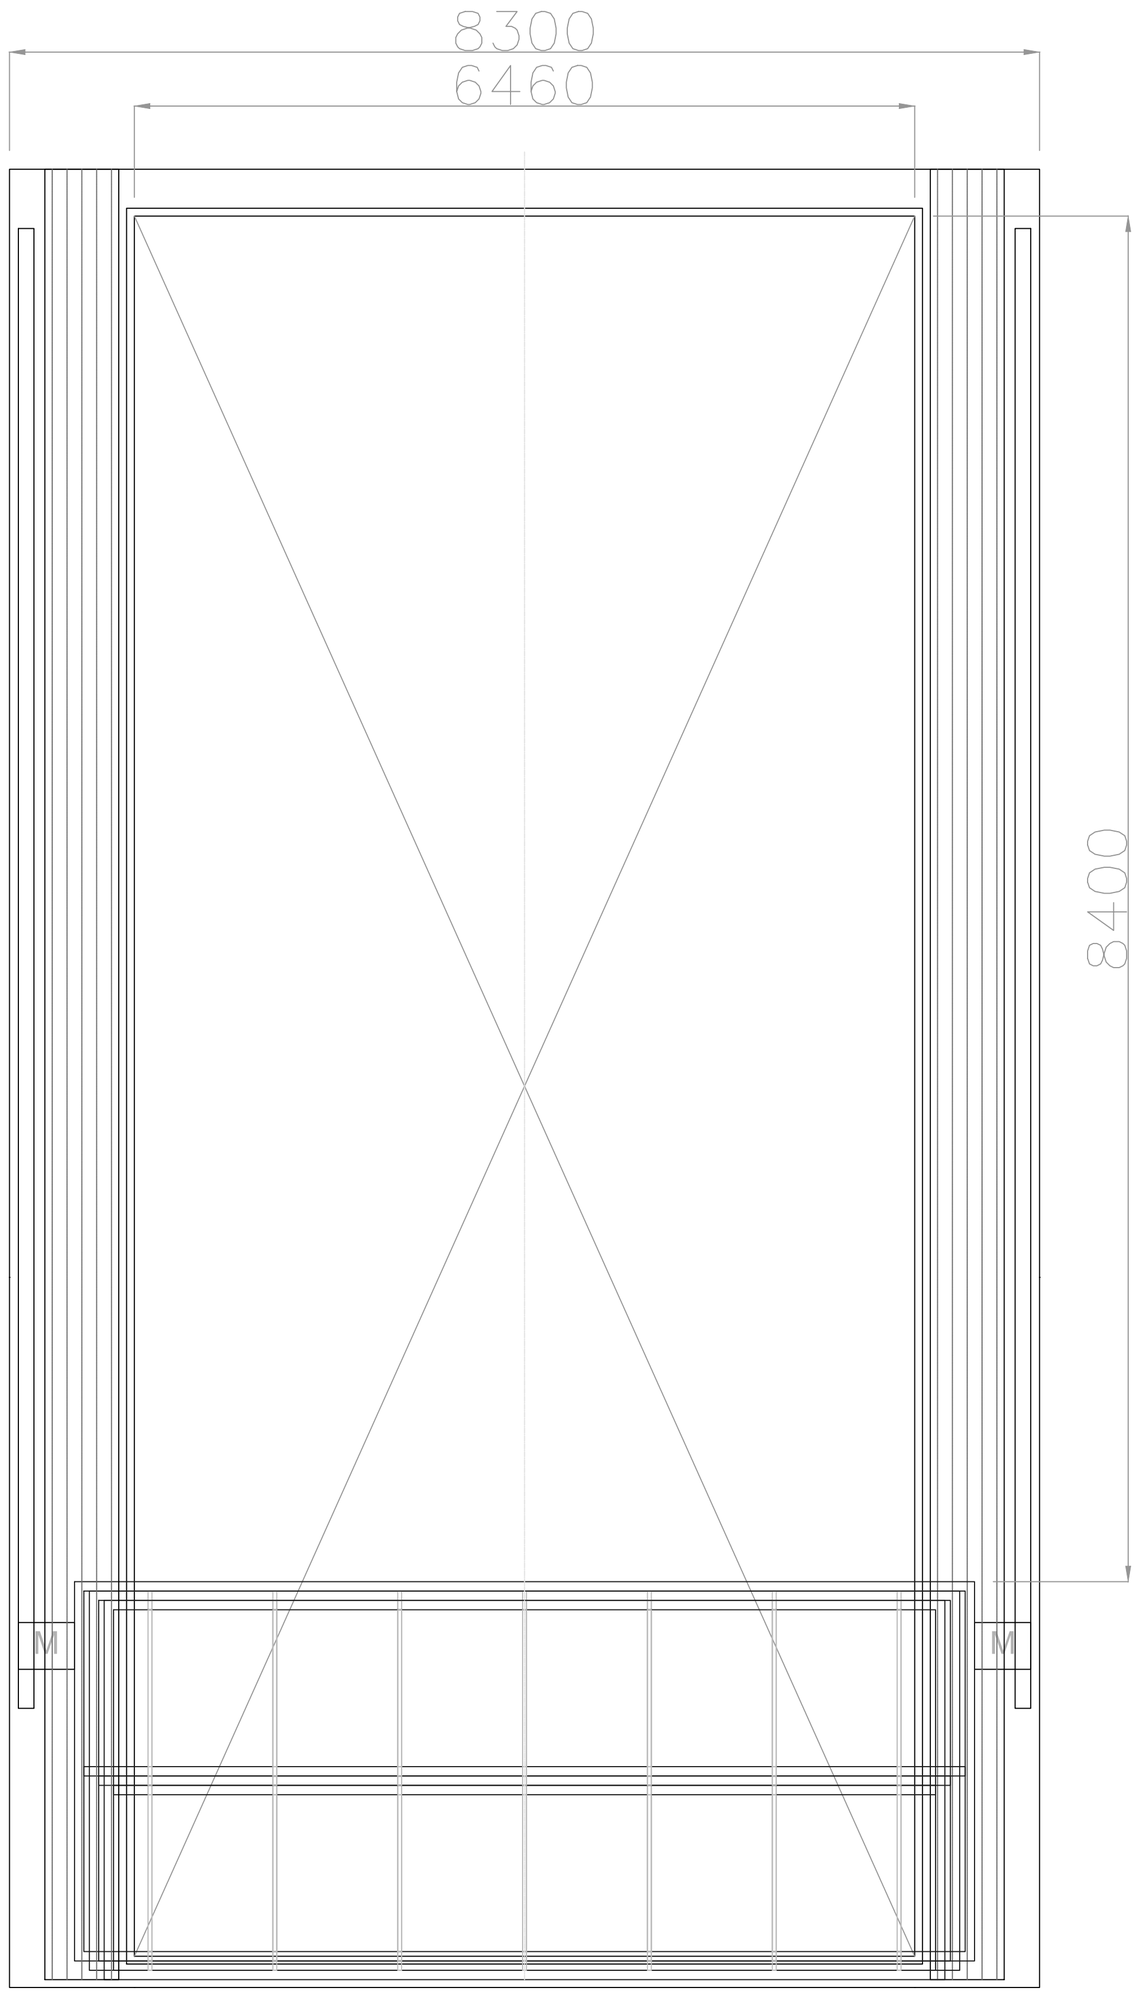

STACKED PLAN

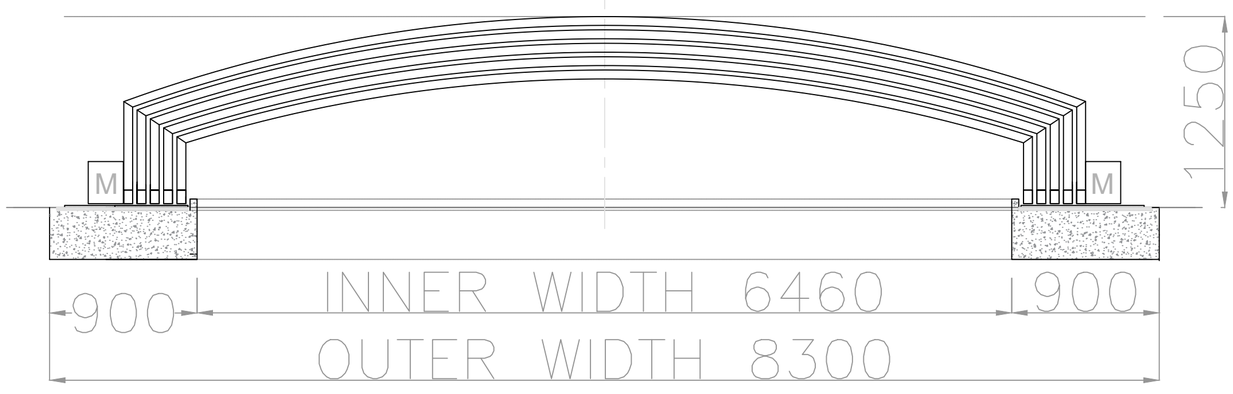

SECTION VIEW

This drawing & design is the property of NIHVA TECHNOLOGIES. Not to be sold or copied to any other concern.

TITLE
ROOF MOVEMENT LAYOUT

NIHVA
NIHVA TECHNOLOGIES PVT. LTD.

	NAME	SIGN	DATE
DRAWN	MAHESH S.		30.11.22
CHECK	MAHESH S.		30.11.22
APPRD.	VIJAY T.		30.11.22

CLIENT - MR. MANISH SHAHA
LOCATION - AHMEDABAD_IN
PRODUCT - RETRACTABLE ROOF
If any queries contact : projectsautomation@nihva.com
NIHVA\22-23\02XX
REV- 0
ALL DIMENSION ARE IN mm
SCALE: NTS
SHEET: 01 OF 01