

Abbrevation's:
WOW-Wall Opening Width
WOH-Wall Opening Height
CH- Clear Height
UC-Under Cut
FFL-Finished Floor Level

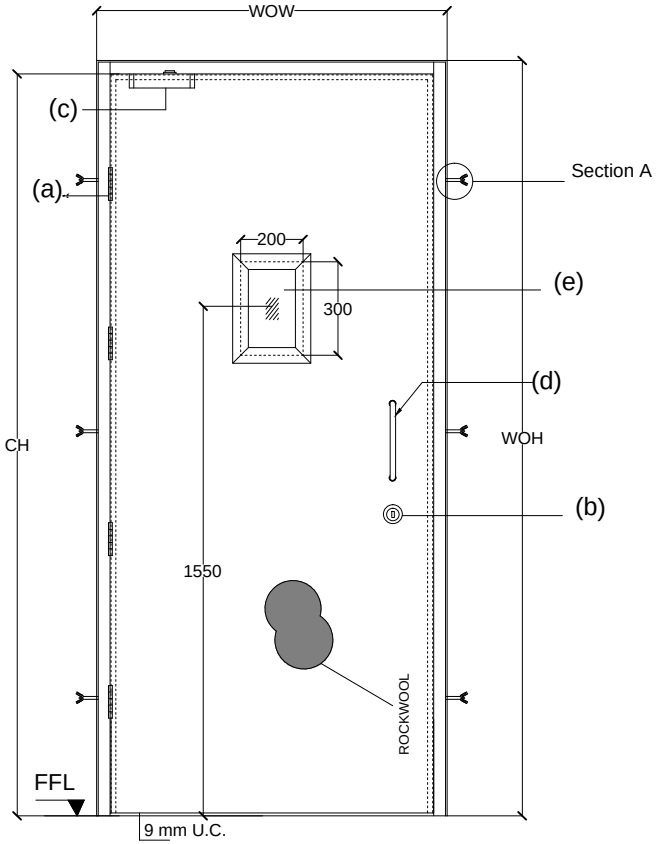

ELEVATION



TOP VIEW

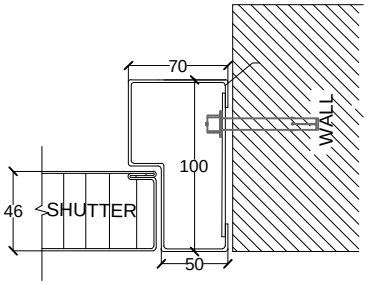

ASSESORIES DETALES

(a) HINGES: DORMA SS hinges 4"x3"x3mm

(b) LOCK : Mortise Dead Lock ML 112-Dorset with cylinder (One side key & other side turn bolt on Rose SSDORSET-CL 204) with escutcheon.

(c) DOOR CLOSER.

(d) HANDLE : D Handle (300x22) pair.

(e) VISION PANEL - 5mm THK. GLASS OF SIZE-200X300mm

Shutter thickness : 46 mm
Frame Sheet thick : 1.5mm
Shutter sheet thick : 1.2mm
Fixing : On Soliid Brick plasterd wall with Anchors

NOTE:- *All Dimensions are in mm.
*Tolerance:-All Linear Dimensions ±3mm,Others ±0.5mm.
*The Drawing Is For Location of Hardware only. Drawing Does Not Represent The Hardware For More Clarity, Please Go Through Hardware Broucher.

Fire door size

WOW	WOH	TYPE 1	TYPE 2	TYPE 3	TYPE 4	QUANTITY
1200	2100					14

COLOR:-
1.TRAFFIC WHITE:-RAL9016
2.LIGHT GREY:- RAL7035
3.Gentian Blue:- RAL5010
4.Signal Red:-RAL3001

NOTE- CLIENT SHOULD SELECT DOOR TYPE FROM DOOR HANDLING SHEET & COLOR OF DOOR.

This drawing & designing is the property of NIHVA TECHNOLOGIES. Not to be sold or copied to any other concern.

TITLE	2HRS FIRE RATED STEEL DOOR		NIHVA TECHNOLOGIES PVT. LTD. PUNE Tel : 020 66304033 Email:- info@nihva.com Website:- www.nihva.com
	SIGN	DATE	
DRAWN	SURAJ.	18/11/17	CLIENT- MITTTAL PRECISION HITECH STEEL PVT LTD
CHECK	OMKAR	18/11/17	PROJECT -
APPROVAL	SHEKHAR	18/11/17	SITE - KHED,PUNE.
MFG.			DWG. NO. : NIHVA/17-18/0282 REV. : 00
If any queries contact : projects@nihva.com			SCALE: NTS WT: SHEET: 01 OF 01
ALL DIMENSION ARE IN mm			