
DRAWING

REV DESCRIPTION	DATE	REV NO
	04-07-2025	REV 00
1. Xyz		

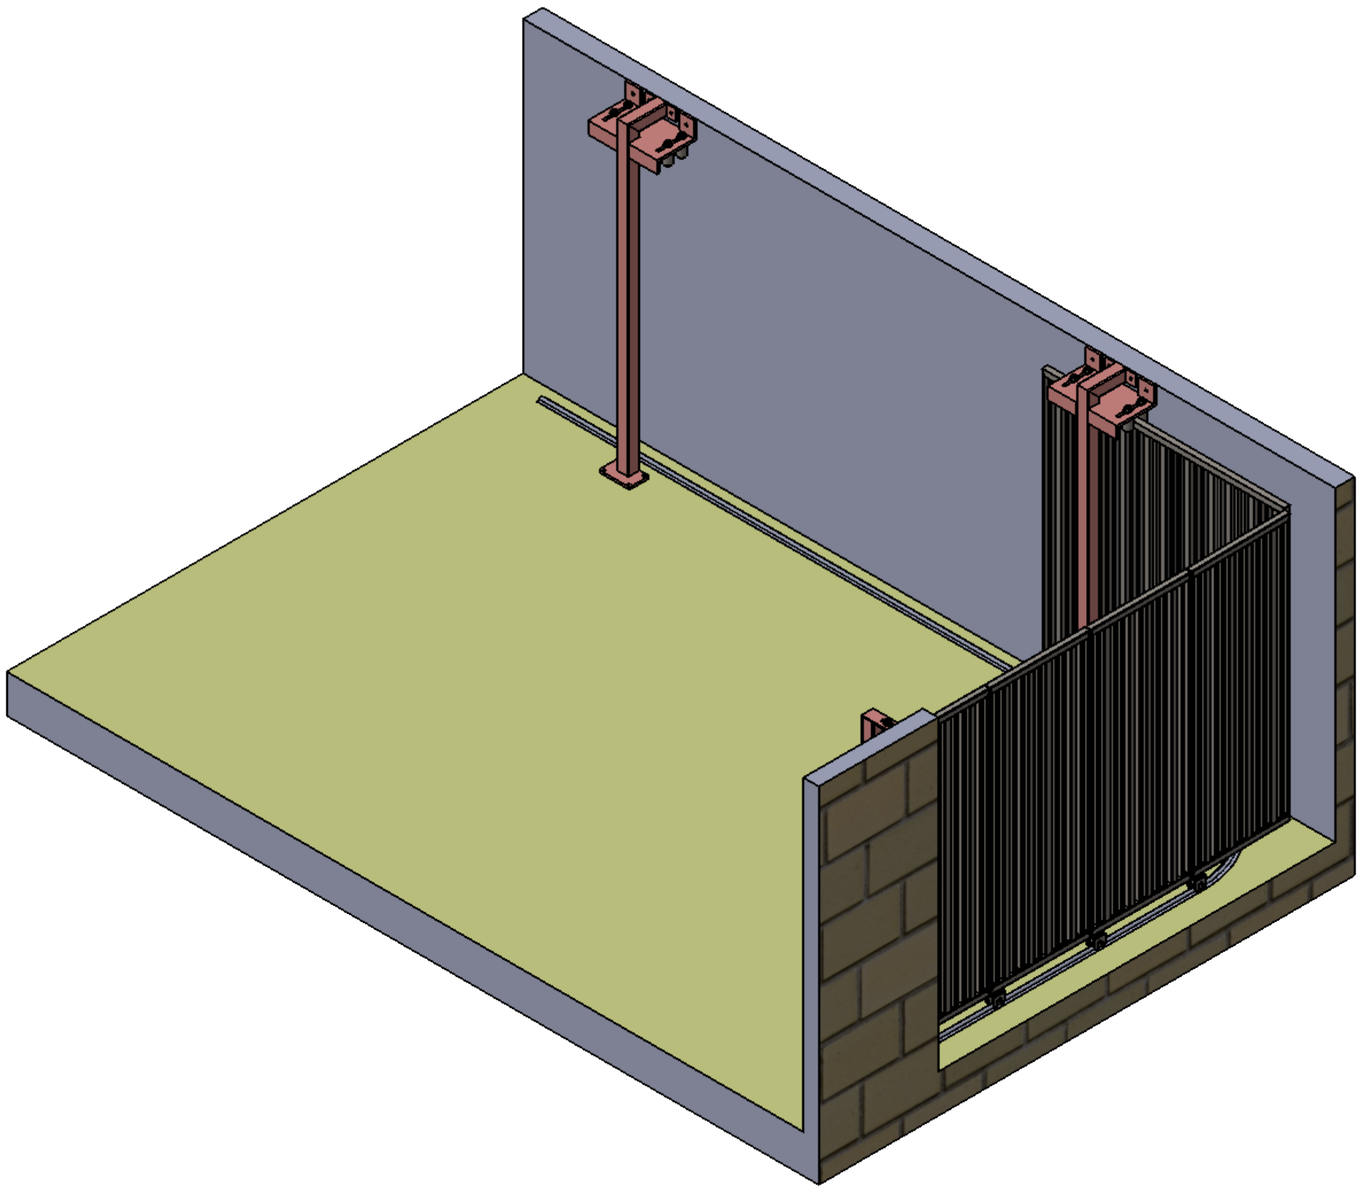

ISOMATRIC VIEW

NOTE :

SPECIAL INSTRUCTION'S :

TITLE - GATE AUTOMATION

DWG NO - NTPL-000-PM-001

NIHVA TECHNOLOGIES PVT.LTD.PUNE
Website - www.nihva.com

	NAME	SIGNATURE	DATE		
DRAWN	V.G.		04-09-2025	PROJECT NO - NTPL-000-PM	REVISION - 00
CHK'D	B.S.		05-09-2025	SITE LOCATION -LUCKNOW	WEIGHT -
APPV'D	V.T.		06-09-2025	MATRIAL - MS	QTY - 1

If any queries contact - design@nihva.com

ALL DIMENSION ARE IN mm | A2

PROJECTION METHOD:


SCALE :

SHEET 1 OF 29

DRAWING

REV DESCRIPTION	DATE	REV NO
	04-07-2025	REV 00
1. Xyz		

ITEM NO.	PART NUMBER	DESCRIPTION	QTY.
1	CIVIL BASE		1
2	TRACK 1		1
3	POST		2
4	POST - 6.3MTR		1
5	PLATE		2
6	END PANEL AND WHEEL ASM.		1
7	WHEEL ASM. NEW		6
8	LEAF ASM.		3
9	START LEAF ASM.		1
10	Assem2 roller and nut		10

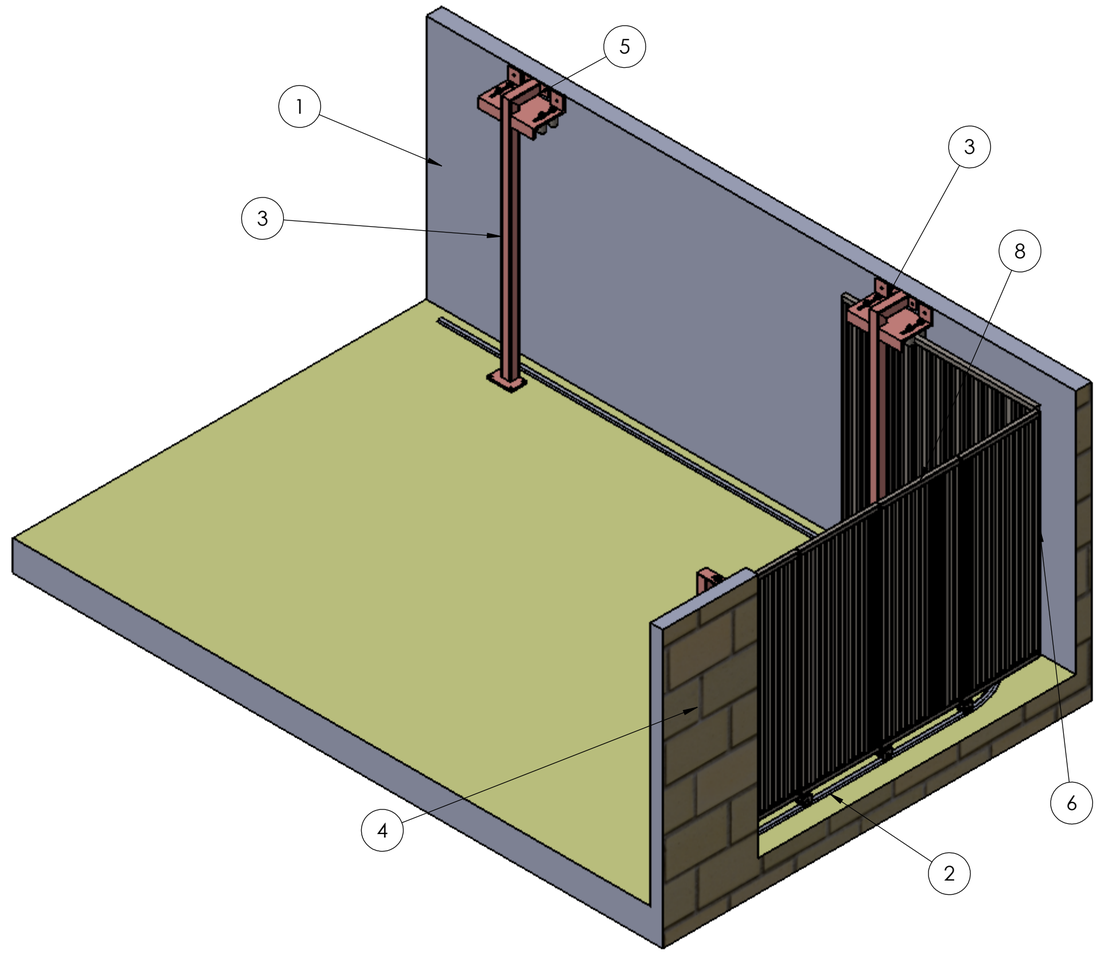

NOTE :

SPECIAL INSTRUCTION'S :

TITLE - GATE AUTOMATION

DWG NO - NTPL-000-PM-001

NIHVA Technologies Pvt. Ltd.

NIHVA TECHNOLOGIES PVT.LTD.PUNE
Website - www.nihva.com

	NAME	SIGNATURE	DATE		
DRAWN	V.G.		04-09-2025	PROJECT NO - NTPL-000-PM	REVISION - 00
CHK'D	B.S.		05-09-2025	SITE LOCATION -LUCKNOW	WEIGHT -
APPV'D	V.T.		06-09-2025	MATRIAL - MS	QTY - 1

If any queries contact - design@nihva.com


ALL DIMENSION ARE IN mm | A2


PROJECTION METHOD:

SCALE :


SHEET 2 OF 29

DRAWING

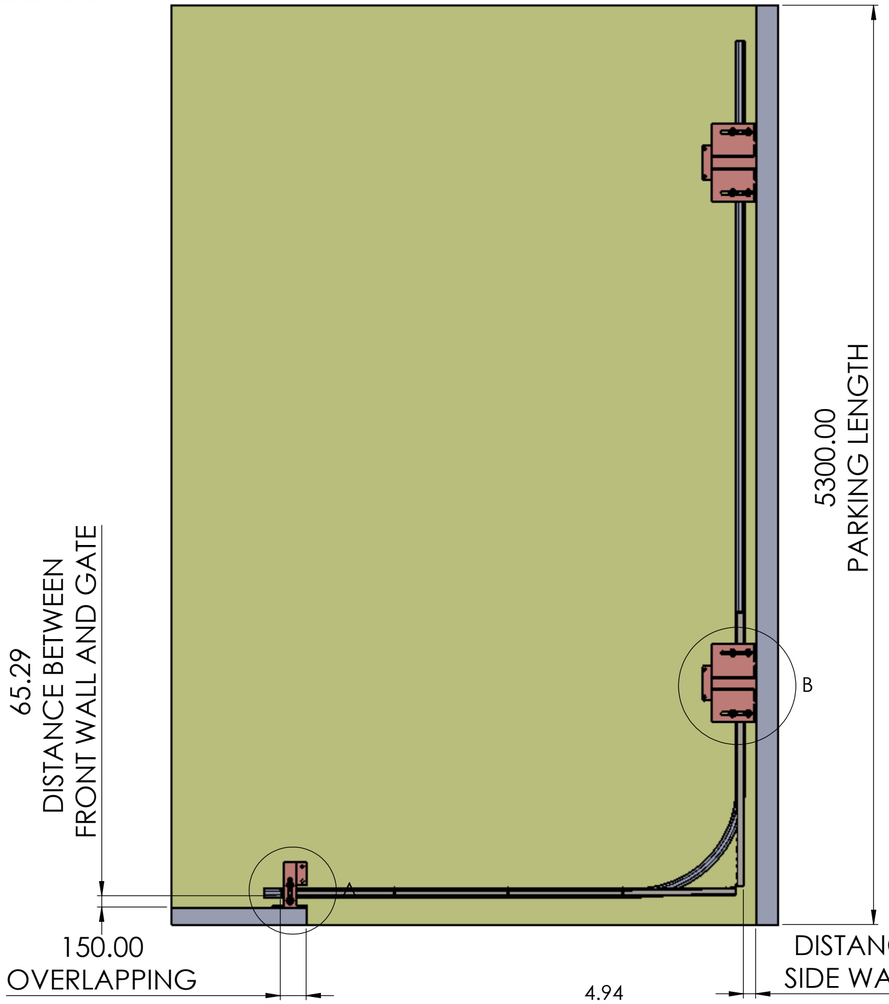


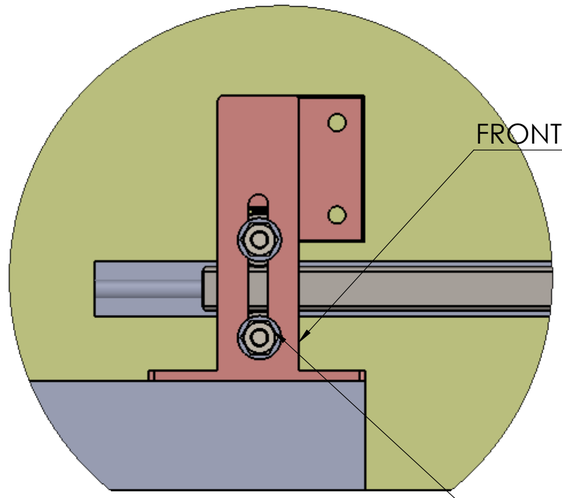

DETAIL A
SCALE 1 : 4

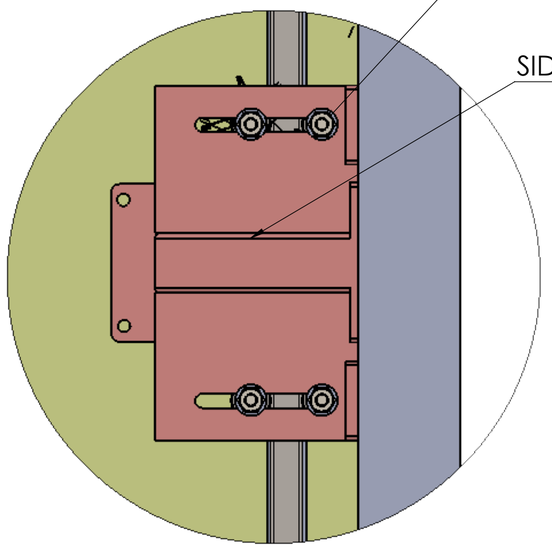

DETAIL B
SCALE 2 : 11

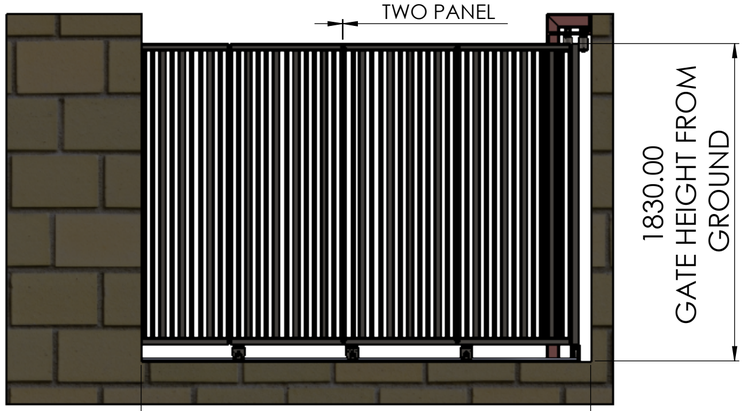

REV DESCRIPTION	DATE	REV NO
	04-07-2025	REV 00
1. Xyz		

NOTE :

SPECIAL INSTRUCTION'S :

TITLE - GATE AUTOMATION

DWG NO - NTPL-000-PM-001

NIHVA Technologies Pvt. Ltd.

NIHVA TECHNOLOGIES PVT.LTD.PUNE
Website - www.nihva.com

	NAME	SIGNATURE	DATE
DRAWN	V.G.		04-09-2025
CHK'D	B.S.		05-09-2025
APPV'D	V.T.		06-09-2025

PRODUCT - SLIDING FOLDING GATE

PROJECT NO - NTPL-000-PM | REVISION - 00

SITE LOCATION -LUCKNOW | WEIGHT -

MATRIAL - MS | QTY - 1

If any queries contact - design@nihva.com


ALL DIMENSION ARE IN mm | A2

PROJECTION METHOD:


SCALE :


DRAWING


REV DESCRIPTION	DATE	REV NO
	04-07-2025	REV 00
1. Xyz		

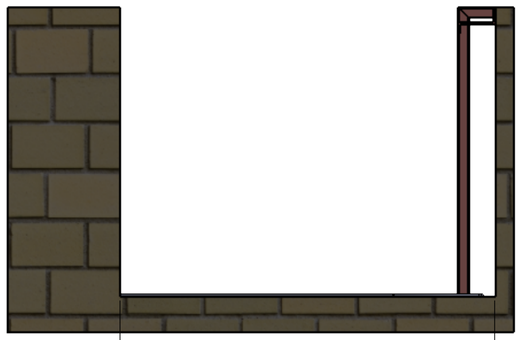


2591.00
CLEAR CUTOUT

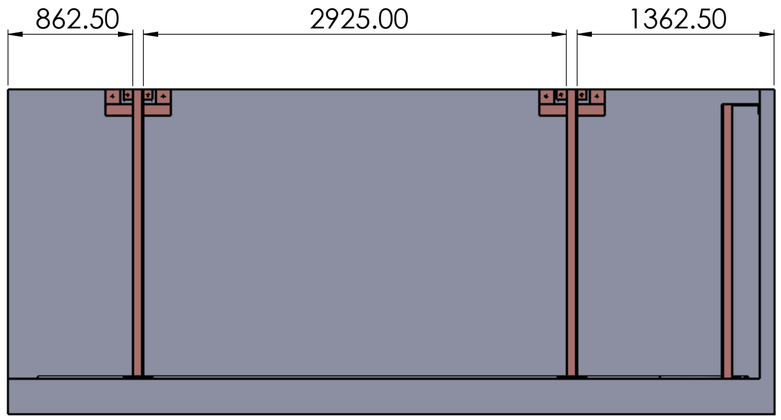

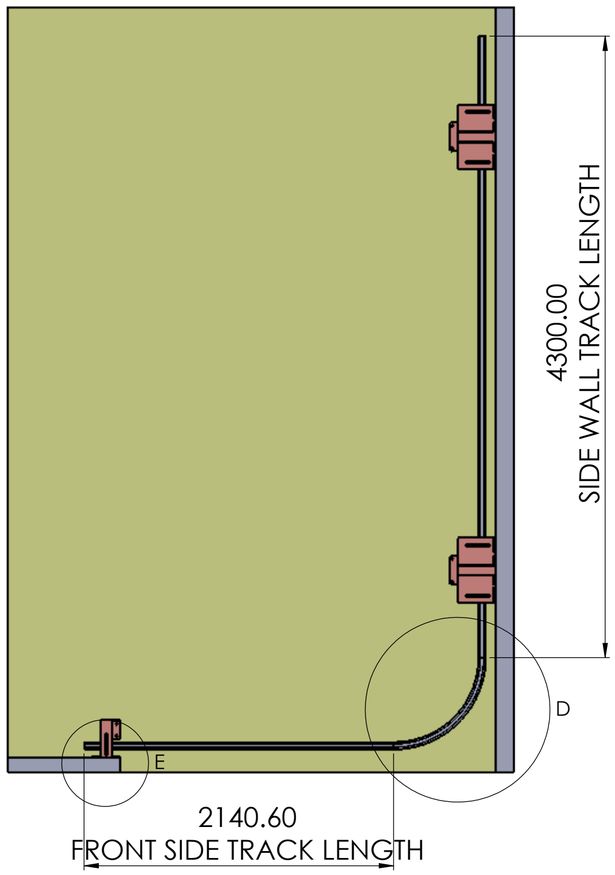

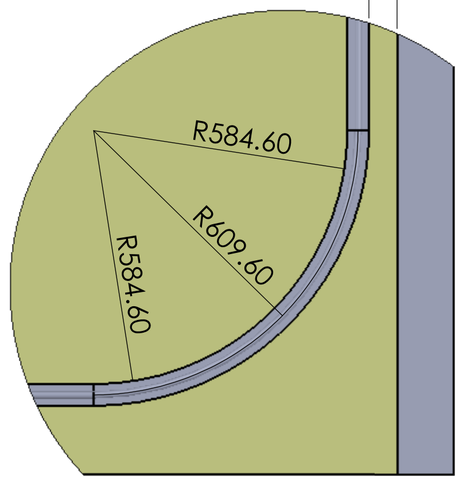

DETAIL D
SCALE 1 : 10

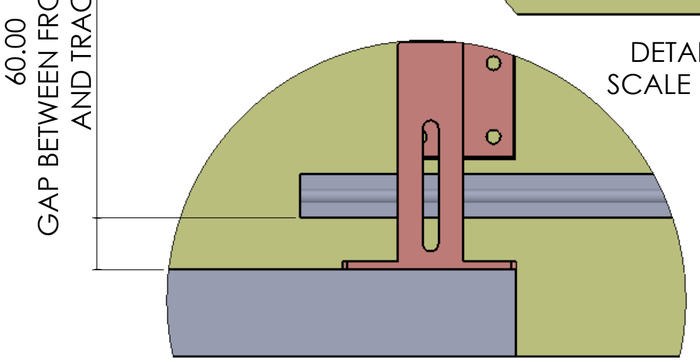

DETAIL E
SCALE 1 : 5

CIVIL STRUCTURE FOE TRACK

NOTE :

SPECIAL INSTRUCTION'S :

TITLE - GATE AUTOMATION			
DWG NO - NTPL-000-PM-001			
	NAME	SIGNATURE	DATE
DRAWN	V.G.		04-09-2025
CHK'D	B.S.		05-09-2025
APPV'D	V.T.		06-09-2025
If any queries contact - design@nihva.com			
ALL DIMENSION ARE IN mm			A2


NIHVA Technologies Pvt. Ltd.
NIHVA TECHNOLOGIES PVT.LTD.PUNE
Website - www.nihva.com


PRODUCT - SLIDING FOLDING GATE	
PROJECT NO - NTPL-000-PM	REVISION - 00
SITE LOCATION -LUCKNOW	WEIGHT -
MATRIAL - MS	QTY - 1
PROJECTION METHOD:	SCALE :
	SHEET 4 OF 29


DRAWING

ITEM NO.	PART NUMBER	DESCRIPTION	QTY.
1	FRONT TRACK	SB BEAM 100X50X8 MM	1
2	EN8 BAR	OD 20 MM	1

REV DESCRIPTION	DATE	REV NO
	04-07-2025	REV 00
1. Xyz		

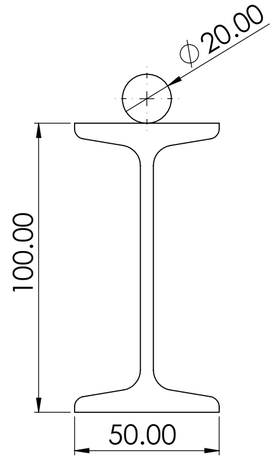

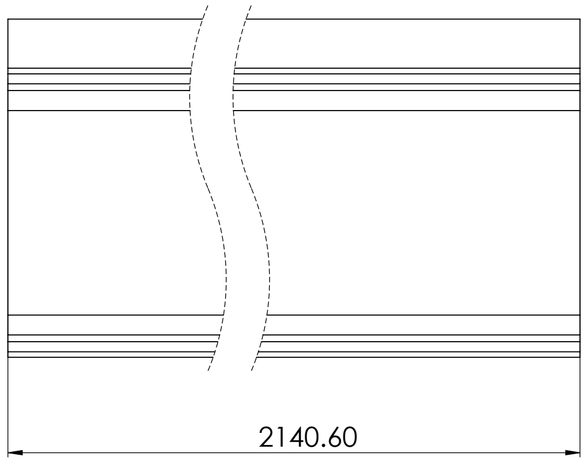

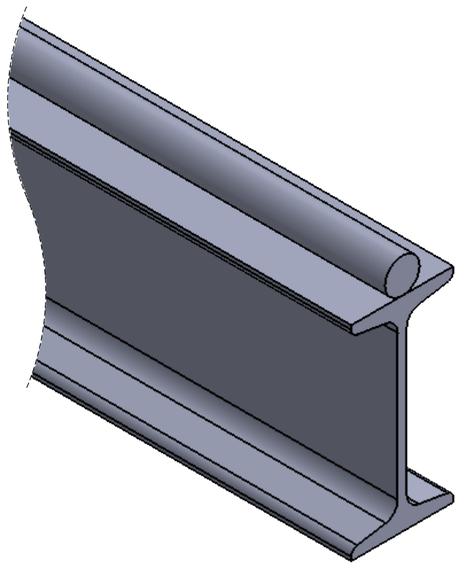

FRONT TRACK

NOTE :

SPECIAL INSTRUCTION'S :

TITLE - GATE AUTOMATION

DWG NO - NTPL-000-PM-001

NIHVA Technologies Pvt. Ltd.

NIHVA TECHNOLOGIES PVT.LTD.PUNE
Website - www.nihva.com

	NAME	SIGNATURE	DATE
DRAWN	V.G.		04-09-2025
CHK'D	B.S.		05-09-2025
APPV'D	V.T.		06-09-2025

PRODUCT - SLIDING FOLDING GATE

PROJECT NO - NTPL-000-PM | REVISION - 00

SITE LOCATION -LUCKNOW | WEIGHT -

MATRIAL - MS | QTY - 1

If any queries contact - design@nihva.com

ALL DIMENSION ARE IN mm | A2

PROJECTION METHOD:


SCALE :


SHEET 5 OF 29

DRAWING


ITEM NO.	PART NUMBER	DESCRIPTION	QTY.
1	CURVE TRACK	SB BEAM 100X50X8 MM	1
2	EN 8 BAR	OD 20 MM	1

REV DESCRIPTION	DATE	REV NO
	04-07-2025	REV 00
1. Xyz		

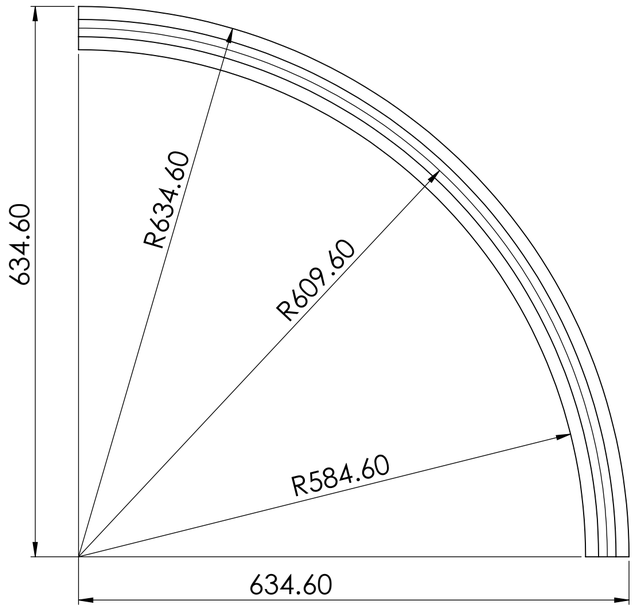

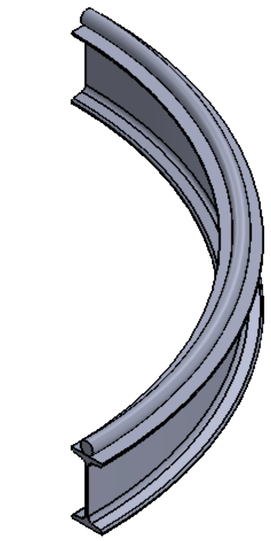

CURVE TRACK

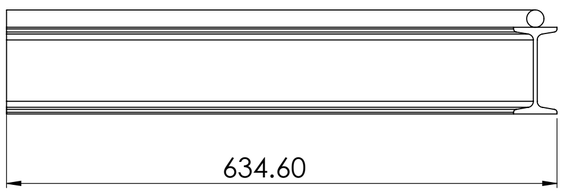

NOTE :

SPECIAL INSTRUCTION'S :

TITLE - GATE AUTOMATION

DWG NO - NTPL-000-PM-001-00-00-00

NIHVA TECHNOLOGIES PVT.LTD.PUNE
Website - www.nihva.com

	NAME	SIGNATURE	DATE		
DRAWN	V.G.		20-08-2025	PROJECT NO - NTPL-000-PM	REVISION - 00
CHK'D	B.S.		20-08-2025	SITE LOCATION -LUCKNOW	WEIGHT -
APPV'D	V.T.		20-08-2025	MATRIAL - MS	QTY - 1

PRODUCT - SLIDING FOLDING GATE

If any queries contact - design@nihva.com

ALL DIMENSION ARE IN mm | A2


PROJECTION METHOD:


SCALE :


SHEET 6 OF 29

DRAWING

ITEM NO.	PART NUMBER	DESCRIPTION	QTY.
1	SIDE WALL TRACK	SB BEAM 100X50X8 MM	1
2	EN 8 BAR	OD 20 MM	1

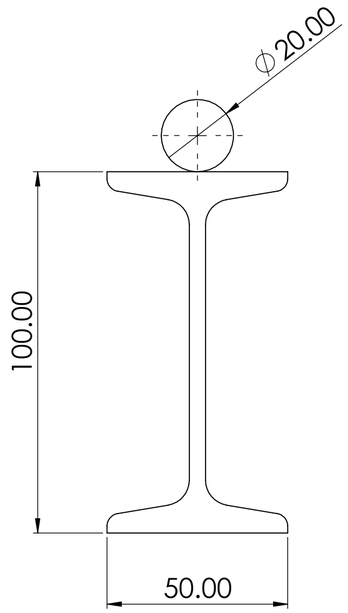

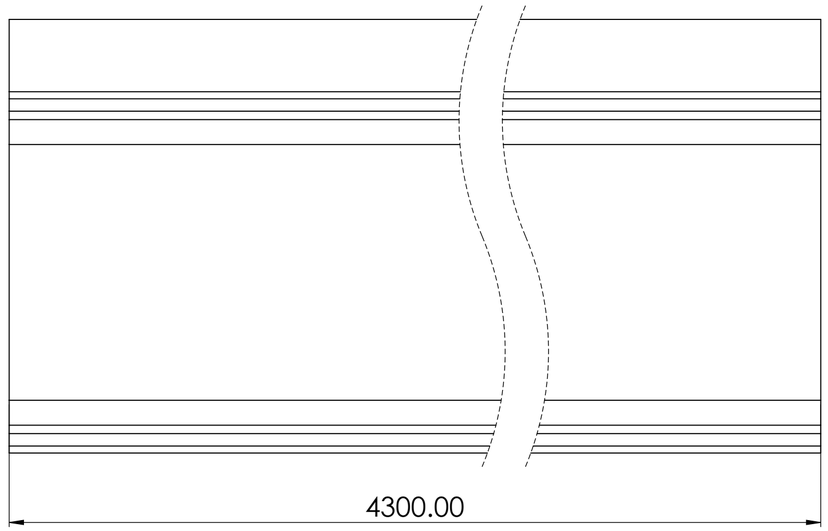

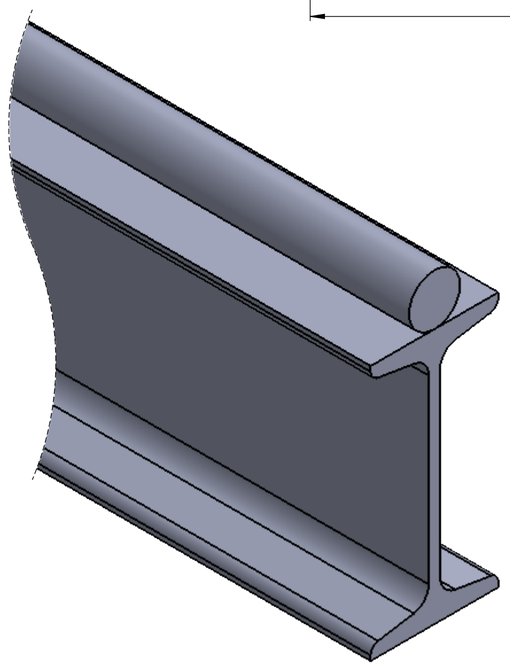

SIDE WALL TRACK

REV DESCRIPTION	DATE	REV NO
	04-07-2025	REV 00
1. Xyz		

NOTE :

SPECIAL INSTRUCTION'S :

TITLE - GATE AUTOMATION

DWG NO - NTPL-000-PM-001-00-00-00

NIHVA TECHNOLOGIES PVT.LTD.PUNE
Website - www.nihva.com

	NAME	SIGNATURE	DATE		
DRAWN	V.G.		20-08-2025	PROJECT NO - NTPL-000-PM	REVISION - 00
CHK'D	B.S.		20-08-2025	SITE LOCATION -LUCKNOW	WEIGHT -
APPV'D	V.T.		20-08-2025	MATRIAL - MS	QTY - 1


If any queries contact - design@nihva.com


ALL DIMENSION ARE IN mm | A2 | PROJECTION METHOD: | SCALE : | SHEET 7 OF 29

DRAWING

REV DESCRIPTION	DATE	REV NO
	04-07-2025	REV 00
1. Xyz		

ITEM NO.	PART NUMBER	DESCRIPTION	QTY.
1	M14 ANCHOR ASSY_1.STEP		25

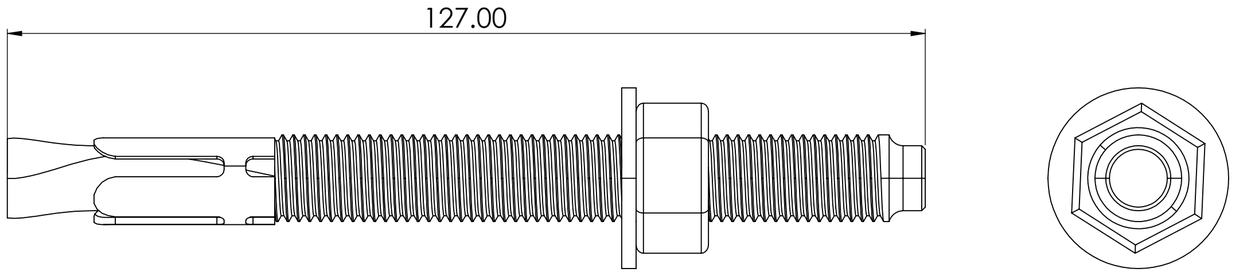

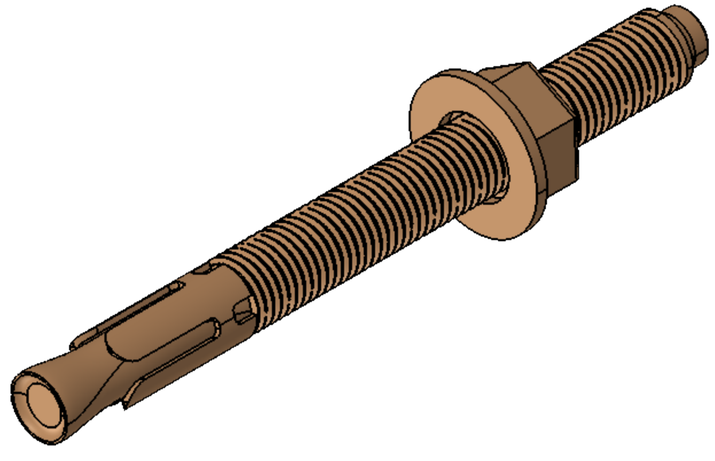

NOTE :

SPECIAL INSTRUCTION'S :

TITLE - GATE AUTOMATION

DWG NO - NTPL-000-PM-001-00-00-00

NIHVA Technologies Pvt. Ltd.

NIHVA TECHNOLOGIES PVT.LTD.PUNE
Website - www.nihva.com

	NAME	SIGNATURE	DATE		
DRAWN	V.G.		20-08-2025	PROJECT NO - NTPL-000-PM	REVISION - 00
CHK'D	B.S.		20-08-2025	SITE LOCATION -LUCKNOW	WEIGHT -
APPV'D	V.T.		20-08-2025	MATRIAL - MS	QTY - 1

If any queries contact - design@nihva.com

PROJECTION METHOD:


SCALE :


ALL DIMENSION ARE IN mm

A2

DRAWING

ITEM NO.	PART NUMBER	DESCRIPTION	QTY.
1	LEAF 01	1736X652X40 MM	4

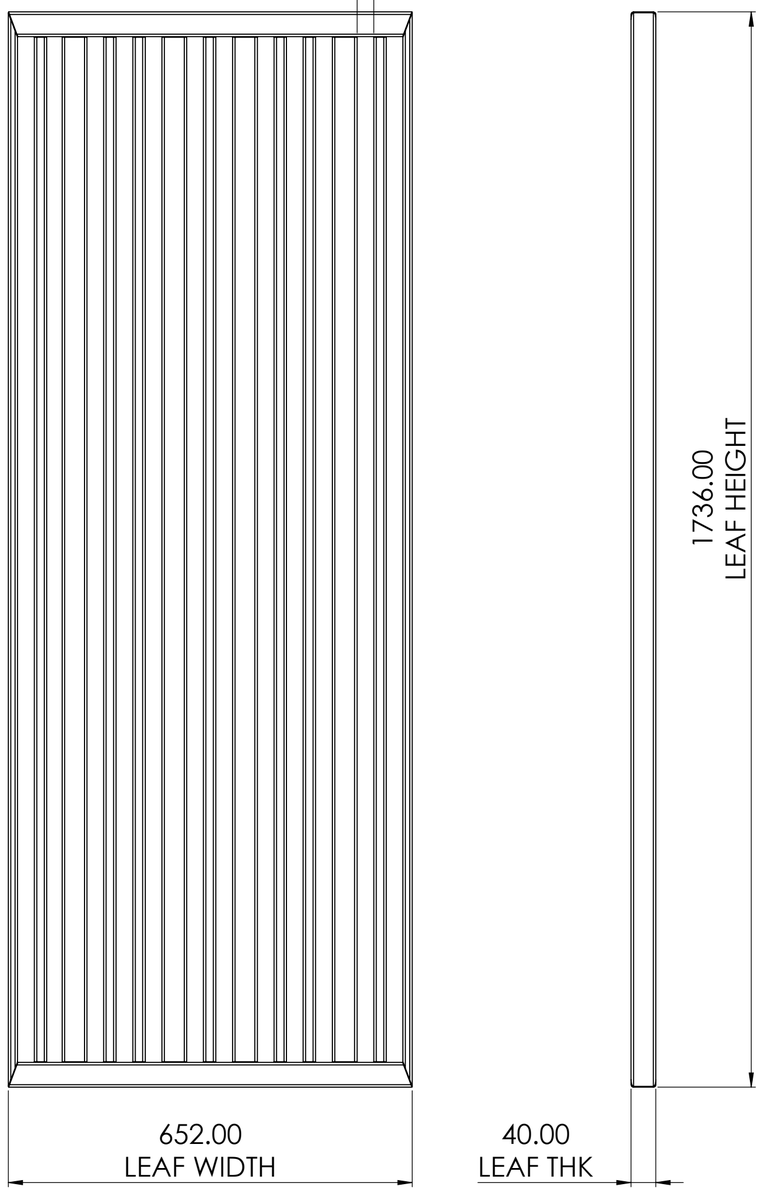

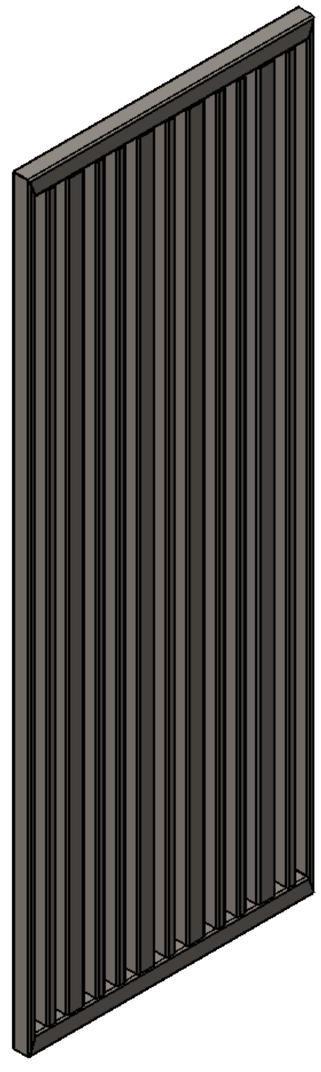

LEAF 01 :- QTY 4 NOS

REV DESCRIPTION	DATE	REV NO
	04-07-2025	REV 00
1. Xyz		

NOTE :

SPECIAL INSTRUCTION'S :

TITLE - GATE AUTOMATION

DWG NO - NTPL-000-PM-001-00-00-00

NIHVA Technologies Pvt. Ltd.

NIHVA TECHNOLOGIES PVT.LTD.PUNE
Website - www.nihva.com

	NAME	SIGNATURE	DATE	PRODUCT - SLIDING FOLDING GATE	
DRAWN	V.G.		20-08-2025	PROJECT NO - NTPL-000-PM	REVISION - 00
CHK'D	B.S.		20-08-2025	SITE LOCATION -LUCKNOW	WEIGHT -
APPV'D	V.T.		20-08-2025	MATRIAL - MS	QTY - 1


If any queries contact - design@nihva.com

ALL DIMENSION ARE IN mm | A2


PROJECTION METHOD:

SCALE :

DRAWING

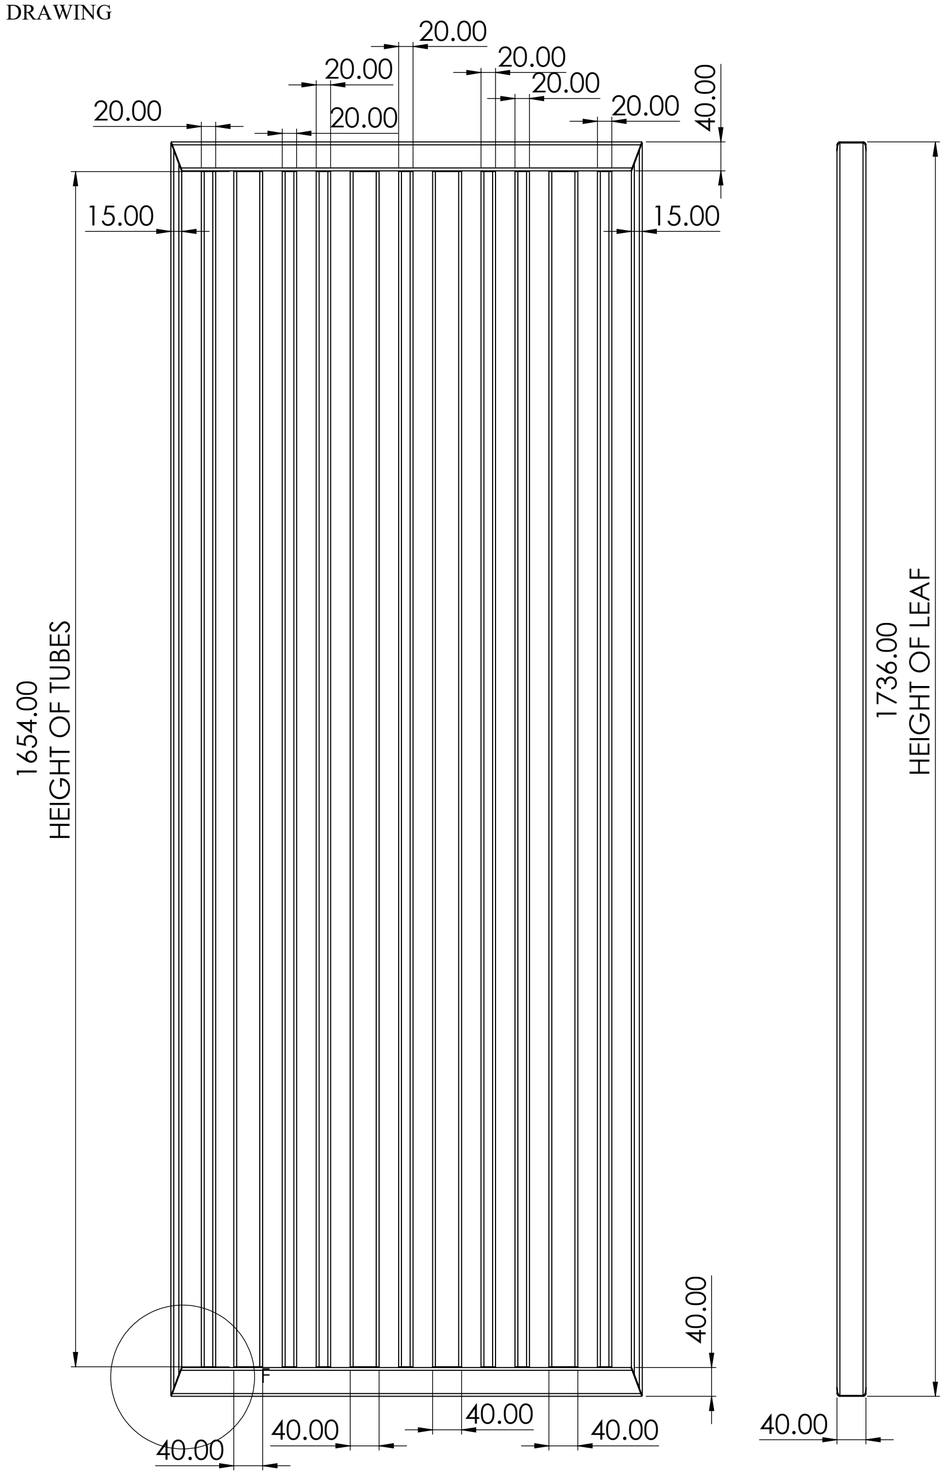

ITEM NO.	PART NUMBER	DESCRIPTION	QTY.
1	LEAF 01	1736X652X40 MM	1
2	MIDDILE TUBES	TUBE, RECTANGULAR 40.000000 X 40.000000 X 3.00	4
3	MIDDLE TUBES	TUBE, RECTANGULAR 40.000000 X 20.000000 X 3.00	7
4	TOP AND BOTTOM OUTER FRAME TUBES	TUBE, RECTANGULAR 40.000000 X 40.000000 X 3.00	2
5	LEFT AND RIGHT OUTER FRAME TUBES	TUBE, RECTANGULAR 40.000000 X 15.000000 X 3.00	2

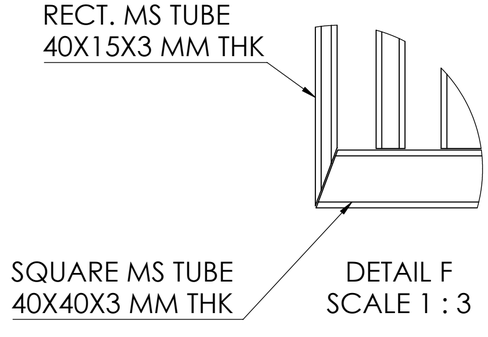

DETAIL F
SCALE 1 : 3

REV DESCRIPTION	DATE	REV NO
	04-07-2025	REV 00
1. Xyz		

NOTE :

TOP AND BOTTOM SQUARE TUBE 40X40X3 MM:-TOTAL 8 QTY REQ.
LEFT AND RIGHT RECT. TUBE 40X15X3 MM:-TOTAL 8 QTY REQ.
MIDDLE SQUARE TUBE 40X40X3 MM:-TOTAL QTY 16 REQ.
MIDDLE RECT. TUBE 40X20X3 MM:-TOTAL QTY 28 REQ.

SPECIAL INSTRUCTION'S :

NO OF PANEL :- 04

TITLE - GATE AUTOMATION

DWG NO - NTPL-000-PM-001-00-00-00

NIHVA TECHNOLOGIES PVT.LTD.PUNE
Website - www.nihva.com

	NAME	SIGNATURE	DATE	PRODUCT - SLIDING FOLDING GATE	
DRAWN	V.G.		20-08-2025	PROJECT NO - NTPL-000-PM	REVISION - 00
CHK'D	B.S.		20-08-2025	SITE LOCATION -LUCKNOW	WEIGHT -
APPV'D	V.T.		20-08-2025	MATRIAL - MS	QTY - 1

If any queries contact - design@nihva.com

ALL DIMENSION ARE IN mm | A2

PROJECTION METHOD:


SCALE :


SHEET 10 OF 29


DRAWING

ITEM NO.	PART NUMBER	DESCRIPTION	QTY.
1	END PANEL	1580X1736X40 MM	1

REV DESCRIPTION	DATE	REV NO
	04-07-2025	REV 00
1. Xyz		

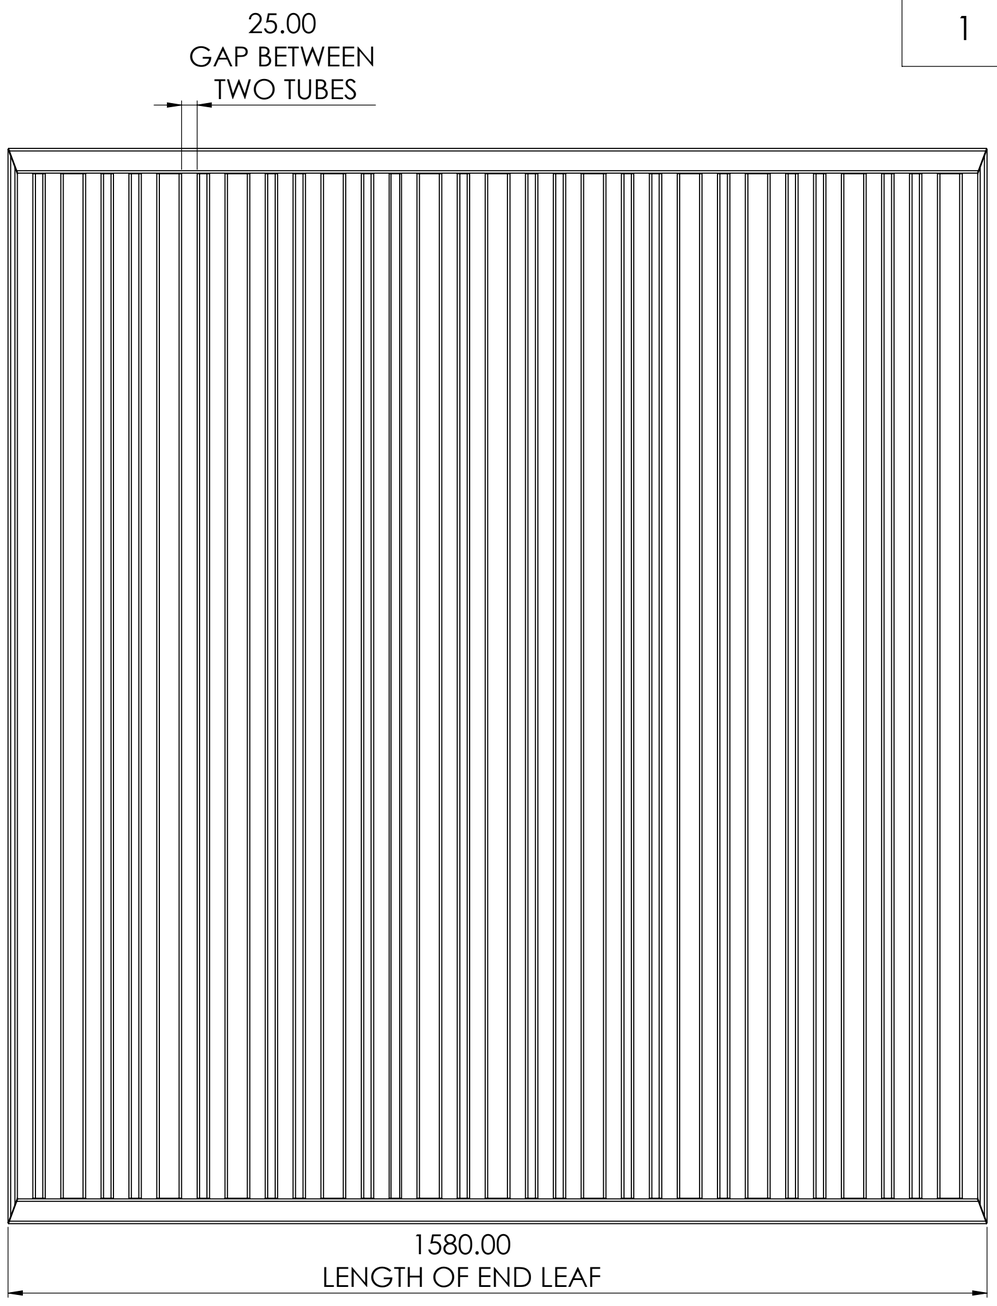

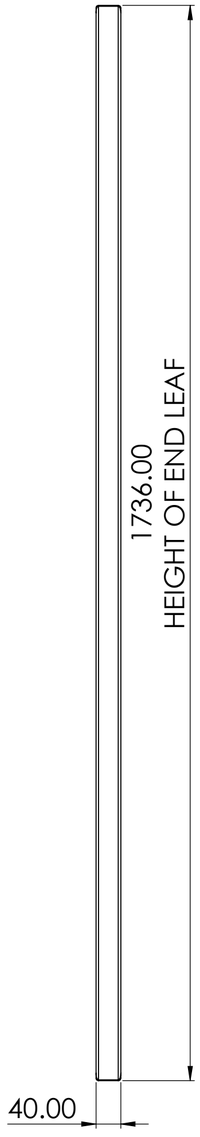

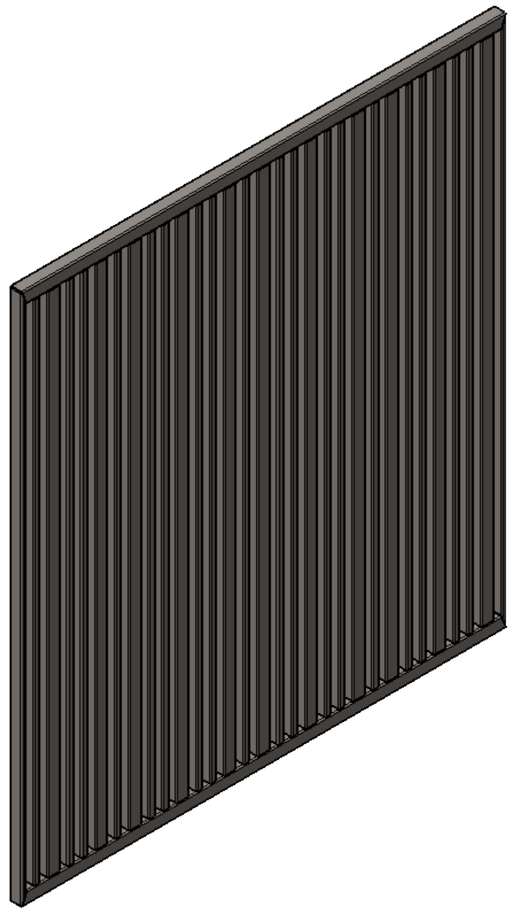

END LEAF :- QTY 1 NOS

NOTE :

SPECIAL INSTRUCTION'S :

TITLE - GATE AUTOMATION


DWG NO - NTPL-000-PM-001-00-00-00

NIHVA TECHNOLOGIES PVT.LTD.PUNE
Website - www.nihva.com

	NAME	SIGNATURE	DATE
DRAWN	V.G.		20-08-2025
CHK'D	B.S.		20-08-2025
APPV'D	V.T.		20-08-2025


PRODUCT - SLIDING FOLDING GATE
PROJECT NO - NTPL-000-PM
REVISION - 00
SITE LOCATION -LUCKNOW
WEIGHT -
MATRIAL - MS
QTY - 1
SCALE :
If any queries contact - design@nihva.com
ALL DIMENSION ARE IN mm
A2
PROJECTION METHOD:

DRAWING

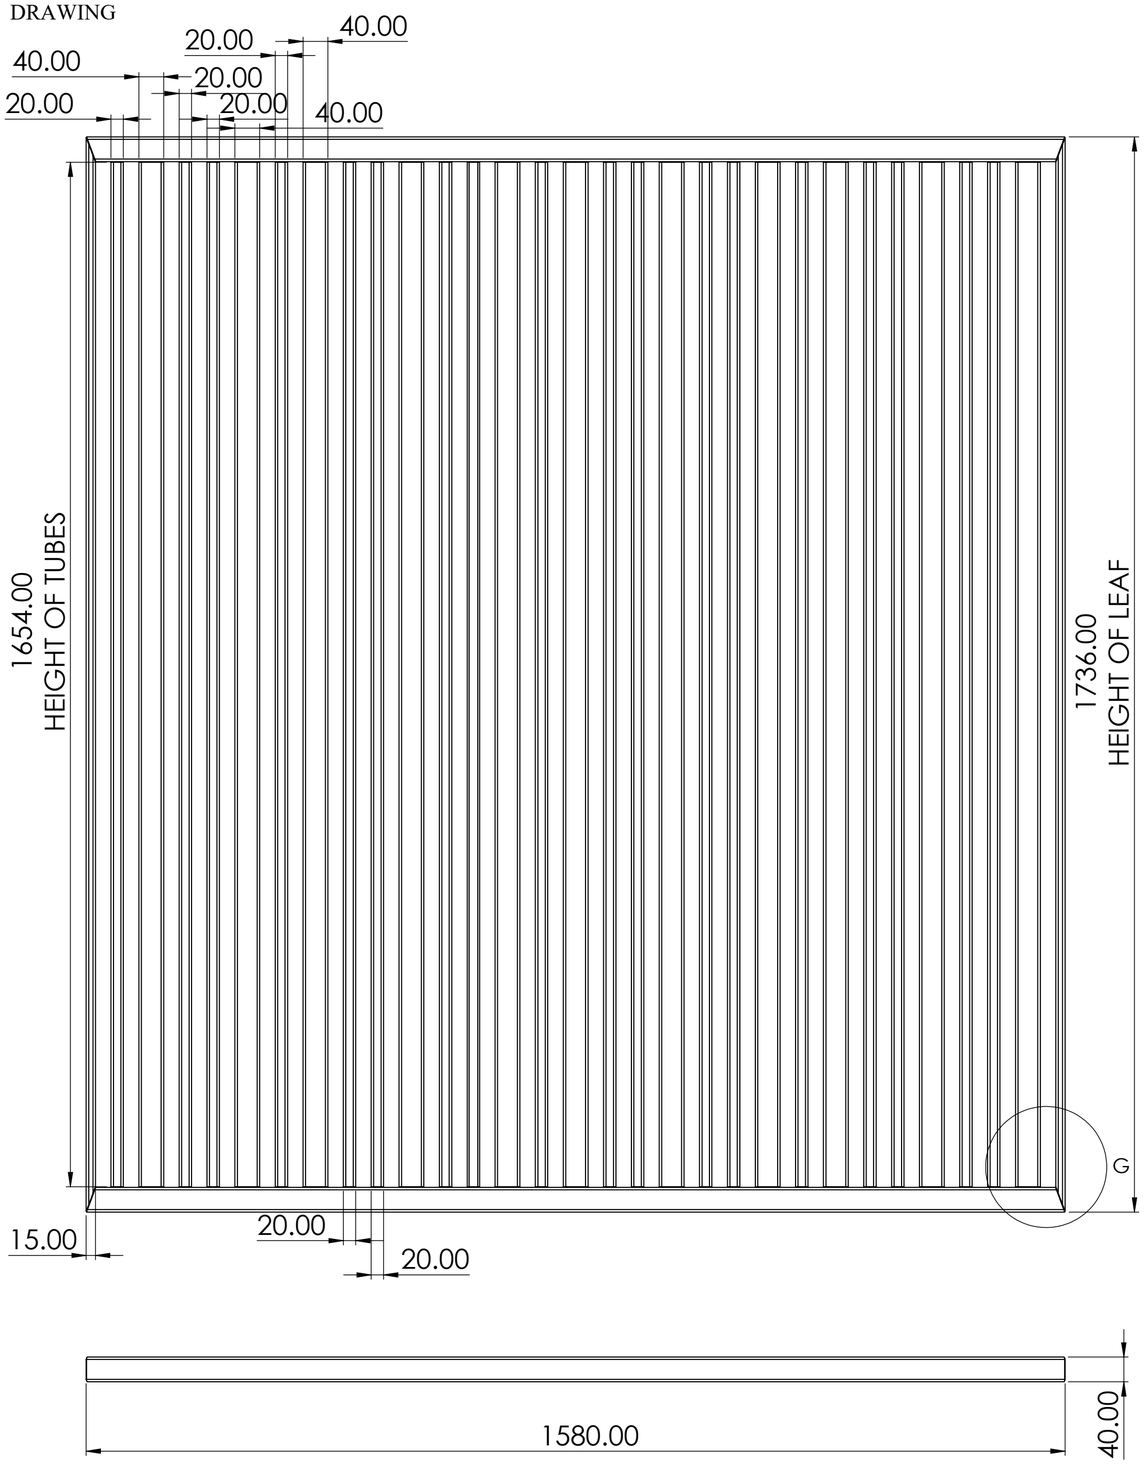

ITEM NO.	PART NUMBER	DESCRIPTION	QTY.
1	END PANEL		1
2	MIDDLE TUBES	TUBE, RECTANGULAR 40.000000 X 20.000000 X 3.00	18
3	MIDDLE TUBES	TUBE, RECTANGULAR 40.000000 X 40.000000 X 3.00	11
4	TOP AND BOT-TOM OUTER FRAME TUBES	TUBE, RECTANGULAR 40.000000 X 40.000000 X 3.00	2
5	LEFT AND RI-GHT OUTER FRAME TUBES	TUBE, RECTANGULAR 40.000000 X 15.000000 X 3.00	2

REV DESCRIPTION	DATE	REV NO
	04-07-2025	REV 00
1. Xyz		

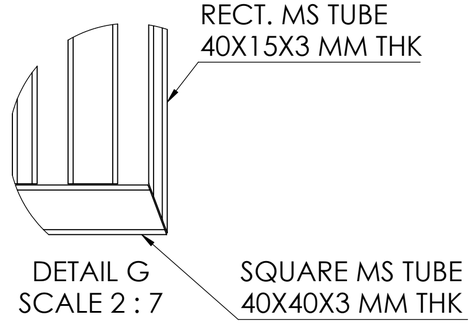

DETAIL G
SCALE 2 : 7

NOTE :

TOP AND BOTTOM SQUARE TUBE 40X40X3 MM:-TOTAL 2 QTY REQ.
LEFT AND RIGHT RECT. TUBE 40X15X3 MM:-TOTAL 2 QTY REQ.
MIDDLE SQUARE TUBE 40X40X3 MM:-TOTAL QTY 11 REQ.
MIDDLE RECT. TUBE 40X20X3 MM:-TOTAL QTY 18 REQ.

SPECIAL INSTRUCTION'S :

NO OF PANEL :- 01

TITLE - GATE AUTOMATION

DWG NO - NTPL-000-PM-001-00-00-00

NIHVA Technologies Pvt. Ltd.

NIHVA TECHNOLOGIES PVT.LTD.PUNE
Website - www.nihva.com

	NAME	SIGNATURE	DATE		
DRAWN	V.G.		20-08-2025	PROJECT NO - NTPL-000-PM	REVISION - 00
CHK'D	B.S.		20-08-2025	SITE LOCATION -LUCKNOW	WEIGHT -
APPV'D	V.T.		20-08-2025	MATRIAL - MS	QTY - 1

If any queries contact - design@nihva.com

ALL DIMENSION ARE IN mm | A2


PROJECTION METHOD:


SCALE :

SHEET 12 OF 29

DRAWING

REV DESCRIPTION	DATE	REV NO
	04-07-2025	REV 00
1. Xyz		

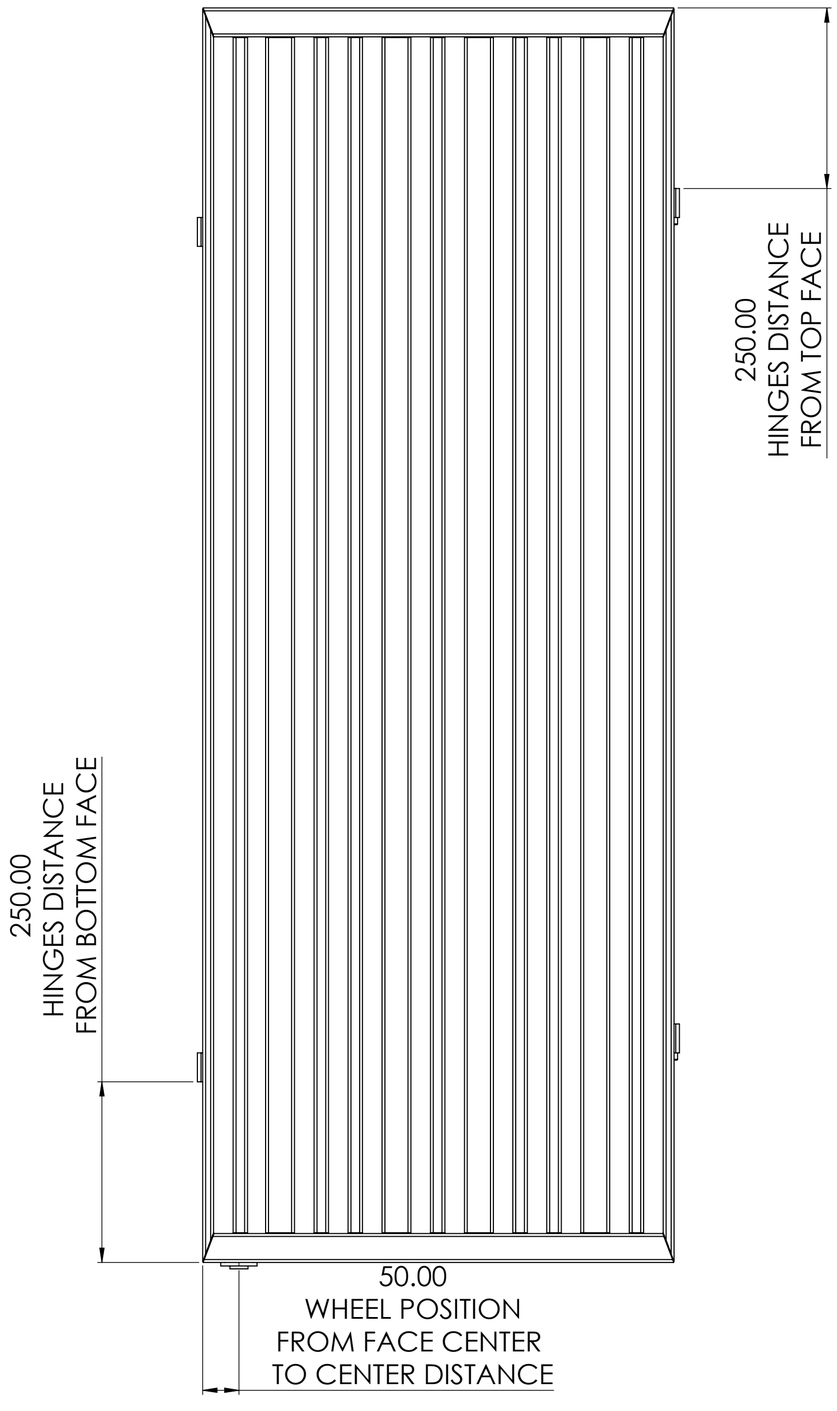

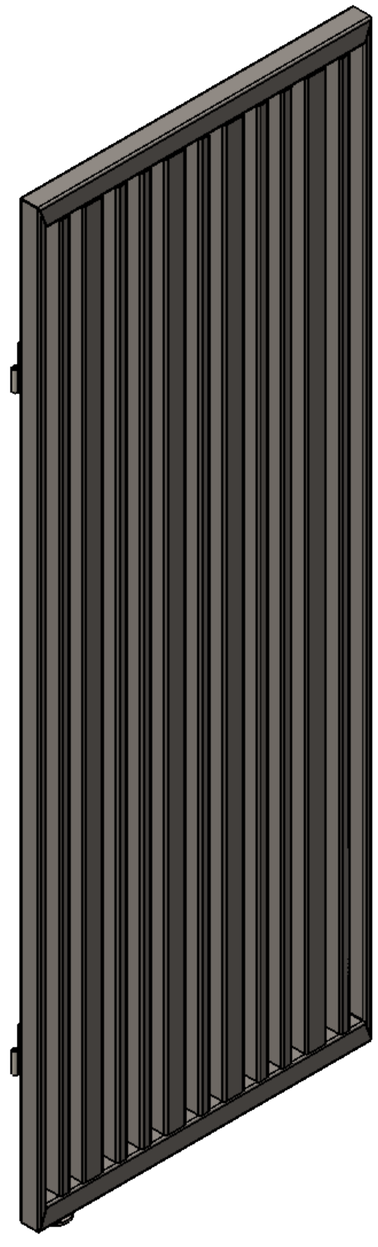

NOTE :

NOTE :- ONE LEAF 2 HINGES REQUIRED

TOTAL HONGES REQ 12

SPECIAL INSTRUCTION'S :

TITLE - GATE AUTOMATION


DWG NO - NTPL-000-PM-001-00-00-00


NIHVA TECHNOLOGIES PVT.LTD.PUNE
Website - www.nihva.com

	NAME	SIGNATURE	DATE	PRODUCT - SLIDING FOLDING GATE	
DRAWN	V.G.		20-08-2025	PROJECT NO - NTPL-000-PM	REVISION - 00
CHK'D	B.S.		20-08-2025	SITE LOCATION -LUCKNOW	WEIGHT -
APPV'D	V.T.		20-08-2025	MATRIAL - MS	QTY - 1
If any queries contact - design@nihva.com				PROJECTION METHOD:	SCALE :
ALL DIMENSION ARE IN mm		A2			SHEET 13 OF 29

DRAWING

REV DESCRIPTION	DATE	REV NO
	04-07-2025	REV 00
1. Xyz		

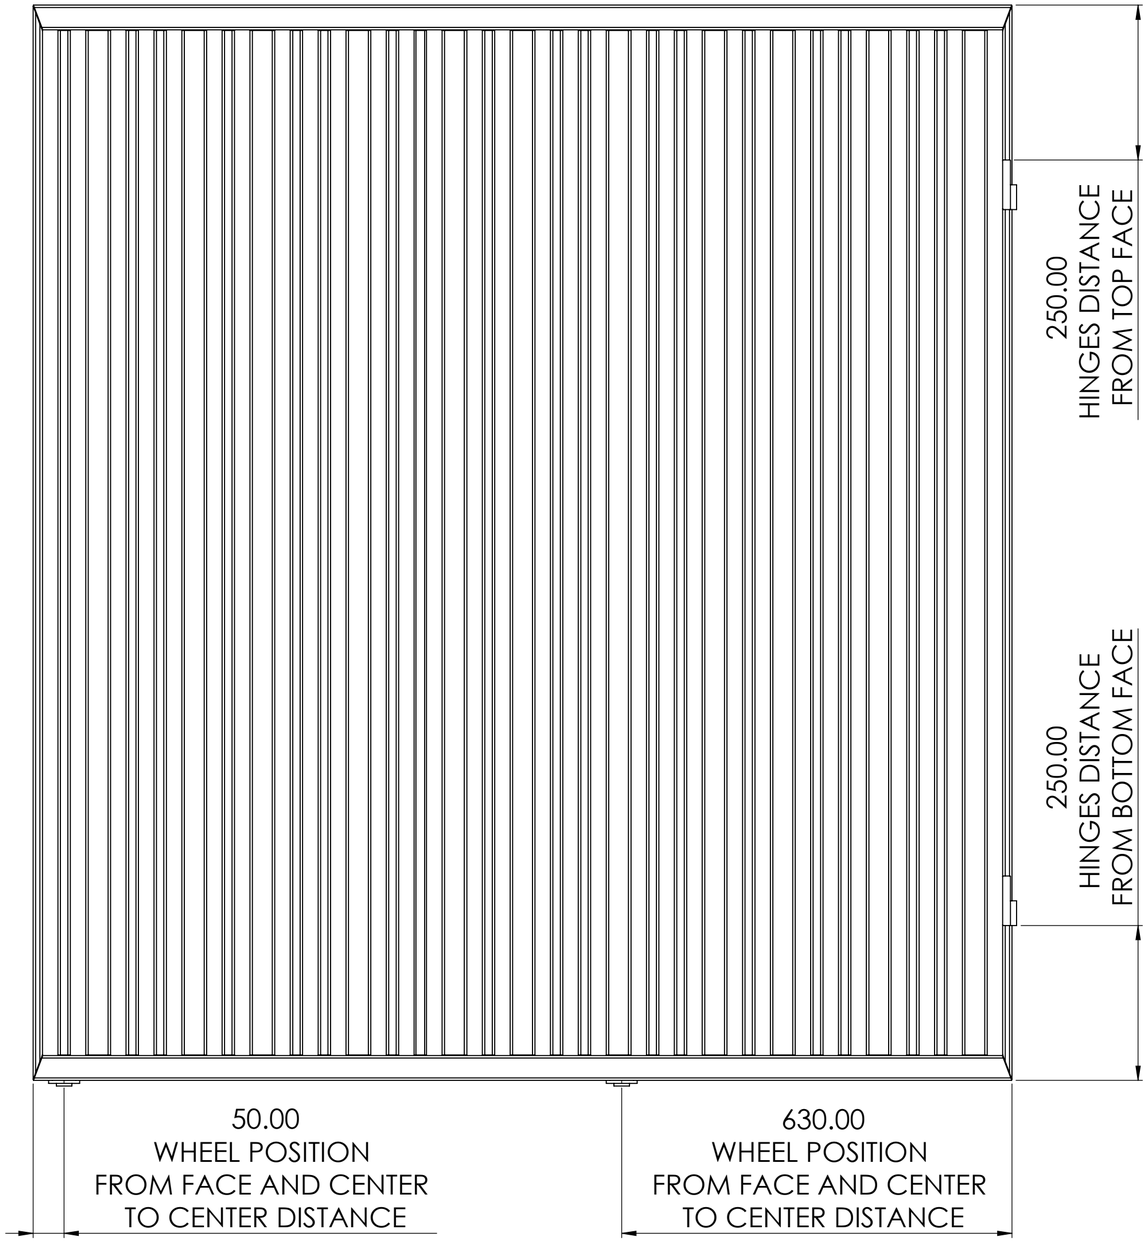

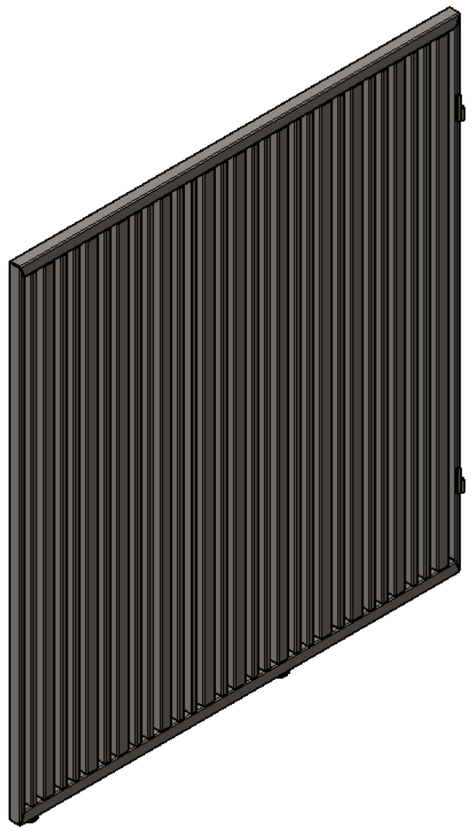

NOTE :

NOTE :- ONE LEAF 2 HINGES REQUIRED

SPECIAL INSTRUCTION'S :

TITLE - GATE AUTOMATION

DWG NO - NTPL-000-PM-001-00-00-00

NIHVA Technologies Pvt. Ltd.

NIHVA TECHNOLOGIES PVT.LTD.PUNE
Website - www.nihva.com

	NAME	SIGNATURE	DATE		
DRAWN	V.G.		20-08-2025	PROJECT NO - NTPL-000-PM	REVISION - 00
CHK'D	B.S.		20-08-2025	SITE LOCATION -LUCKNOW	WEIGHT -
APPV'D	V.T.		20-08-2025	MATRIAL - MS	QTY - 1

If any queries contact - design@nihva.com


ALL DIMENSION ARE IN mm | A2


PROJECTION METHOD:


SCALE :

SHEET 14 OF 29


DRAWING

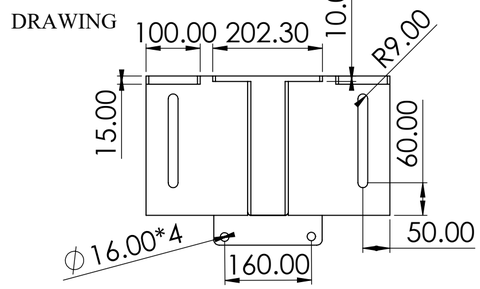

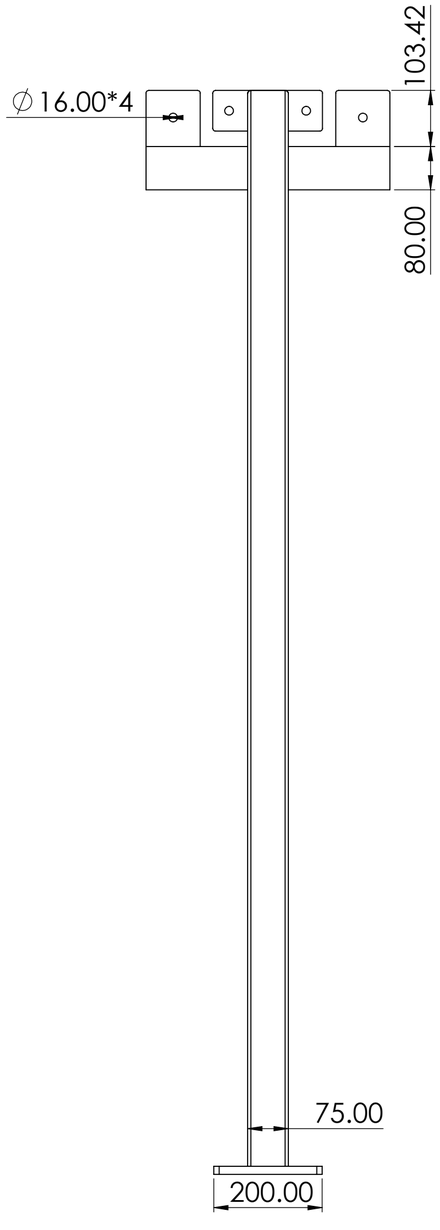

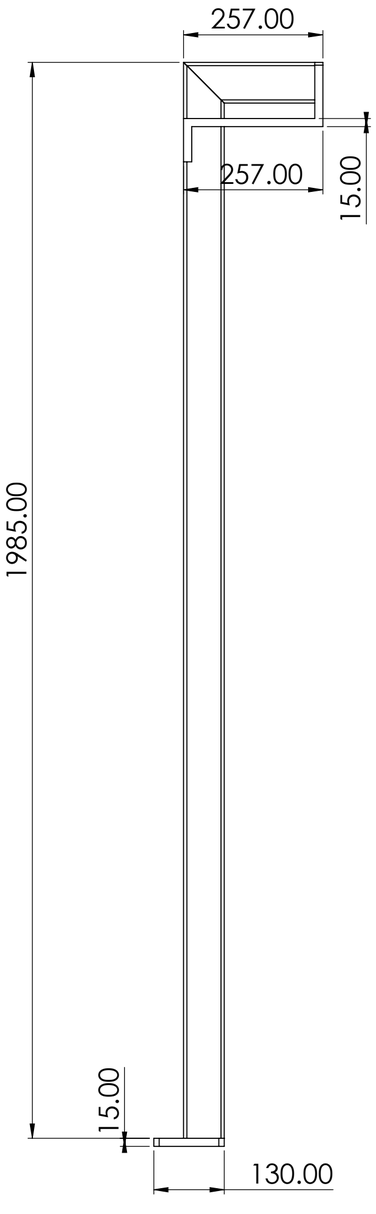

ITEM NO.	PART NUMBER	DESCRIPTION	QTY.
1	POST	2000X257 MM	2
2	PLATE	450X257X15 MM	2

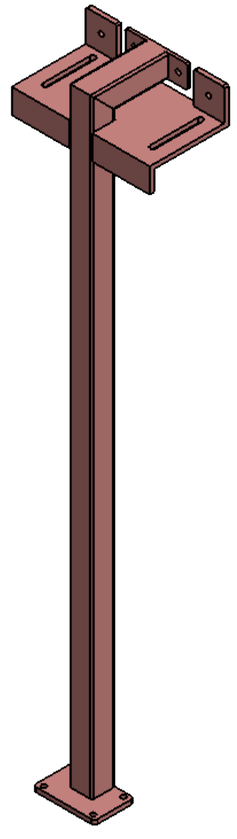

NO. OF QTY REQUIRED 2

REV DESCRIPTION	DATE	REV NO
	04-07-2025	REV 00
1. Xyz		


NOTE :


SPECIAL INSTRUCTION'S :

TITLE - GATE AUTOMATION				NIHVA Technologies Pvt. Ltd.	NIHVA TECHNOLOGIES PVT.LTD.PUNE Website - www.nihva.com
DWG NO - NTPL-000-PM-001-00-00-00					
	NAME	SIGNATURE	DATE	PRODUCT - SLIDING FOLDING GATE	
DRAWN	V.G.		20-08-2025	PROJECT NO - NTPL-000-PM	REVISION - 00
CHK'D	B.S.		20-08-2025	SITE LOCATION -LUCKNOW	WEIGHT -
APPV'D	V.T.		20-08-2025	MATRIAL - MS	QTY - 1
If any queries contact - design@nihva.com				PROJECTION METHOD:	SCALE :
ALL DIMENSION ARE IN mm		A2			SHEET 15 OF 29

DRAWING

ITEM NO.	PART NUMBER	DESCRIPTION	QTY.
1	POST	75X75X3MM THK	2

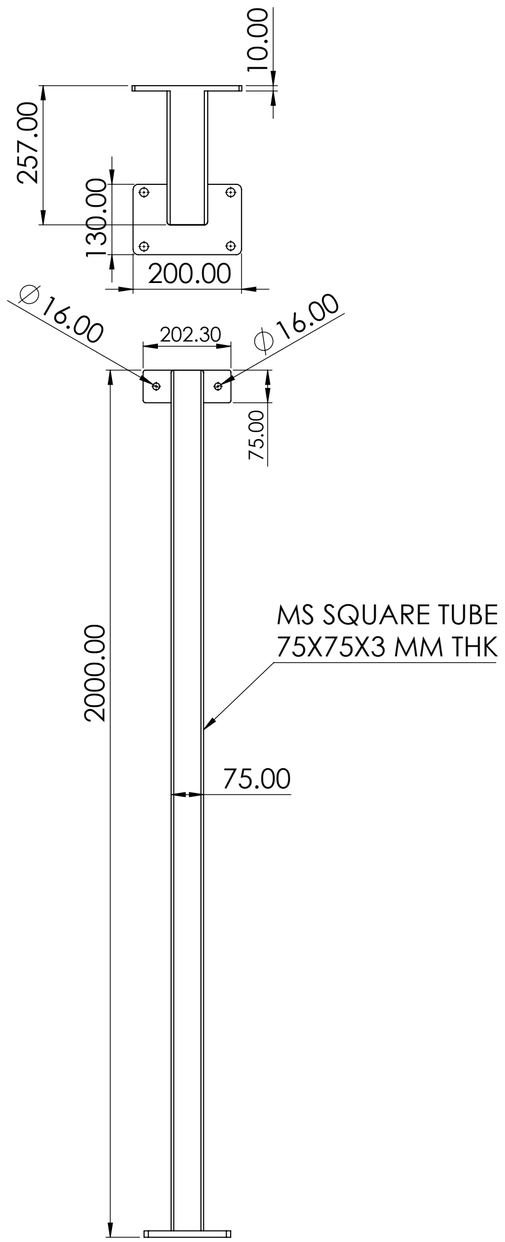

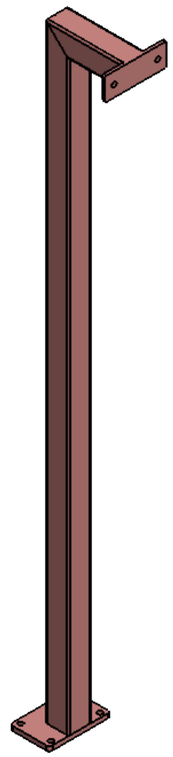

REV DESCRIPTION	DATE	REV NO
	04-07-2025	REV 00
1. Xyz		

NOTE :

SPECIAL INSTRUCTION'S :

TITLE - GATE AUTOMATION

DWG NO - NTPL-000-PM-001-00-00-00

NIHVA Technologies Pvt. Ltd.

NIHVA TECHNOLOGIES PVT.LTD.PUNE
Website - www.nihva.com

	NAME	SIGNATURE	DATE		
DRAWN	V.G.		20-08-2025	PROJECT NO - NTPL-000-PM	REVISION - 00
CHK'D	B.S.		20-08-2025	SITE LOCATION -LUCKNOW	WEIGHT -
APPV'D	V.T.		20-08-2025	MATRIAL - MS	QTY - 1

PRODUCT - SLIDING FOLDING GATE

If any queries contact - design@nihva.com

ALL DIMENSION ARE IN mm | A2


PROJECTION METHOD:


SCALE :


DRAWING

REV DESCRIPTION	DATE	REV NO
	04-07-2025	REV 00
1. Xyz		

ITEM NO.	PART NUMBER	DESCRIPTION	QTY.
1	BOTTOM PLATE	200X130X15 MM THK	2

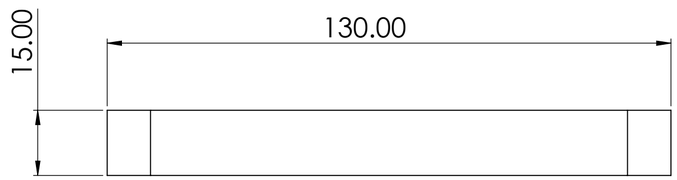

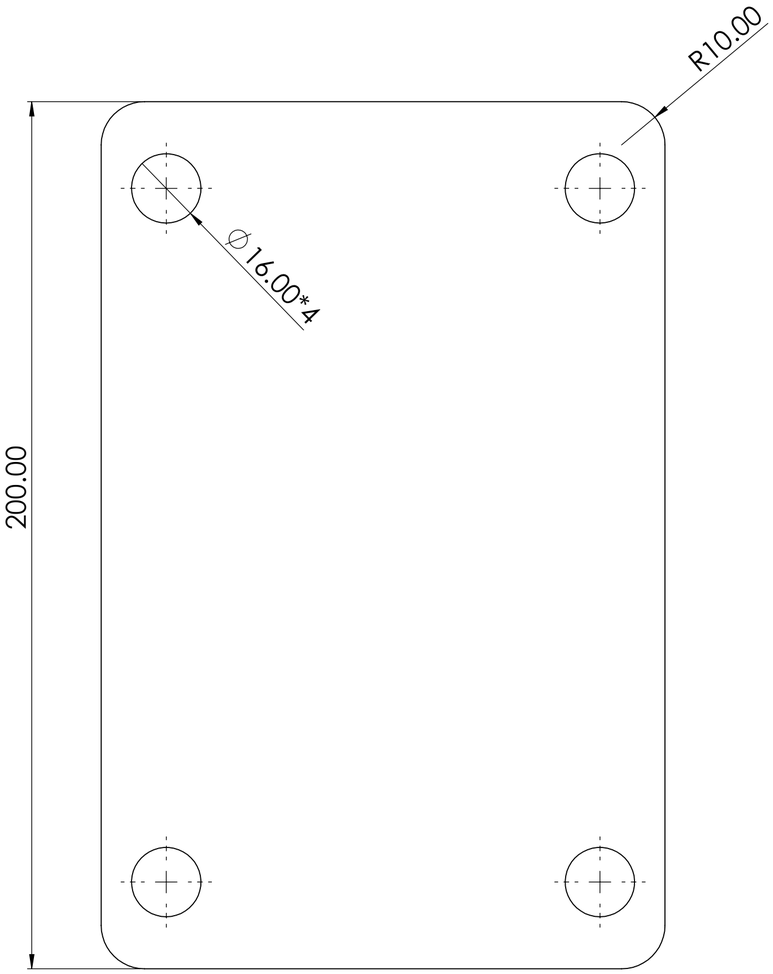

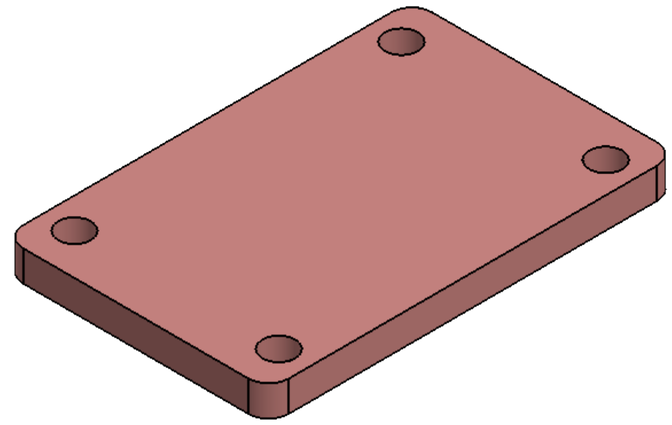

BOTTOM PLATE OF POST

NOTE :

SPECIAL INSTRUCTION'S :

TITLE - GATE AUTOMATION

DWG NO - NTPL-000-PM-001-00-00-00

NIHVA TECHNOLOGIES PVT.LTD.PUNE
Website - www.nihva.com

	NAME	SIGNATURE	DATE		
DRAWN	V.G.		20-08-2025	PROJECT NO - NTPL-000-PM	REVISION - 00
CHK'D	B.S.		20-08-2025	SITE LOCATION -LUCKNOW	WEIGHT -
APPV'D	V.T.		20-08-2025	MATRIAL - MS	QTY - 1

If any queries contact - design@nihva.com

ALL DIMENSION ARE IN mm | A2


PROJECTION METHOD:


SCALE :

DRAWING

ITEM NO.	PART NUMBER	DESCRIPTION	QTY.
1	WALL MOUNTED PLATE	200x75x10 MM THK	2

REV DESCRIPTION	DATE	REV NO
	04-07-2025	REV 00
1. Xyz		

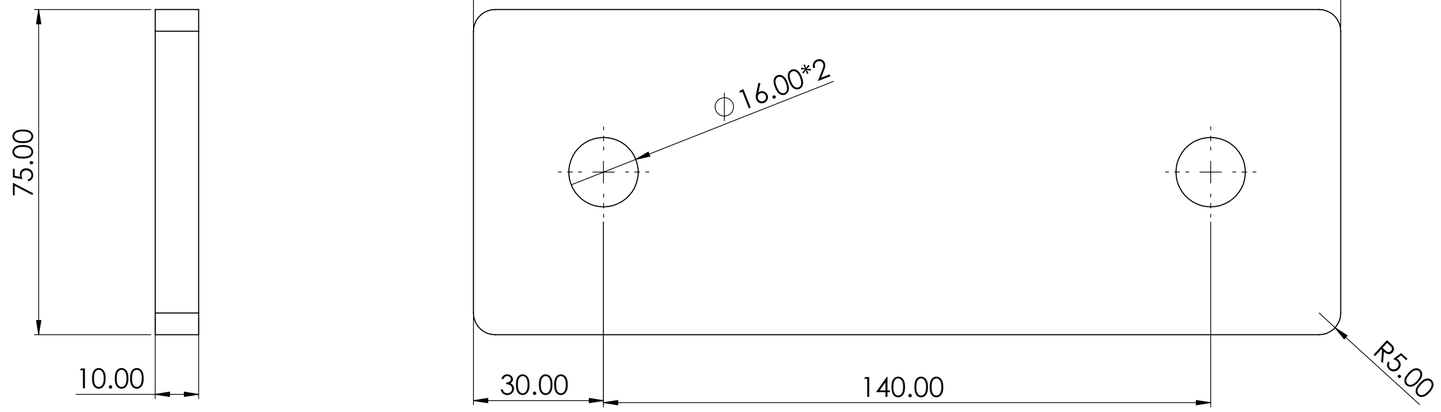

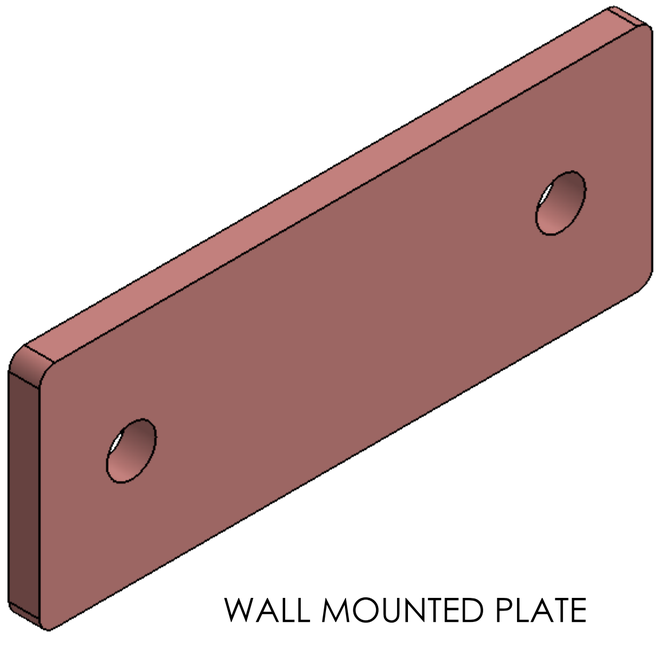

WALL MOUNTED PLATE

NOTE :


SPECIAL INSTRUCTION'S :


TITLE - GATE AUTOMATION				NIHVA TECHNOLOGIES PVT.LTD.PUNE Website - www.nihva.com	
DWG NO - NTPL-000-PM-001-00-00-00					
	NAME	SIGNATURE	DATE	PRODUCT - SLIDING FOLDING GATE	
DRAWN	V.G.		20-08-2025	PROJECT NO - NTPL-000-PM	REVISION - 00
CHK'D	B.S.		20-08-2025	SITE LOCATION -LUCKNOW	WEIGHT -
APPV'D	V.T.		20-08-2025	MATRIAL - MS	QTY - 1
If any queries contact - design@nihva.com				PROJECTION METHOD:	SCALE :
ALL DIMENSION ARE IN mm		A2			SHEET 18 OF 29

DRAWING

ITEM NO.	PART NUMBER	DESCRIPTION	QTY.
1	SIDE POST TUBE	1985X247 MM	2

REV DESCRIPTION	DATE	REV NO
	04-07-2025	REV 00
1. Xyz		

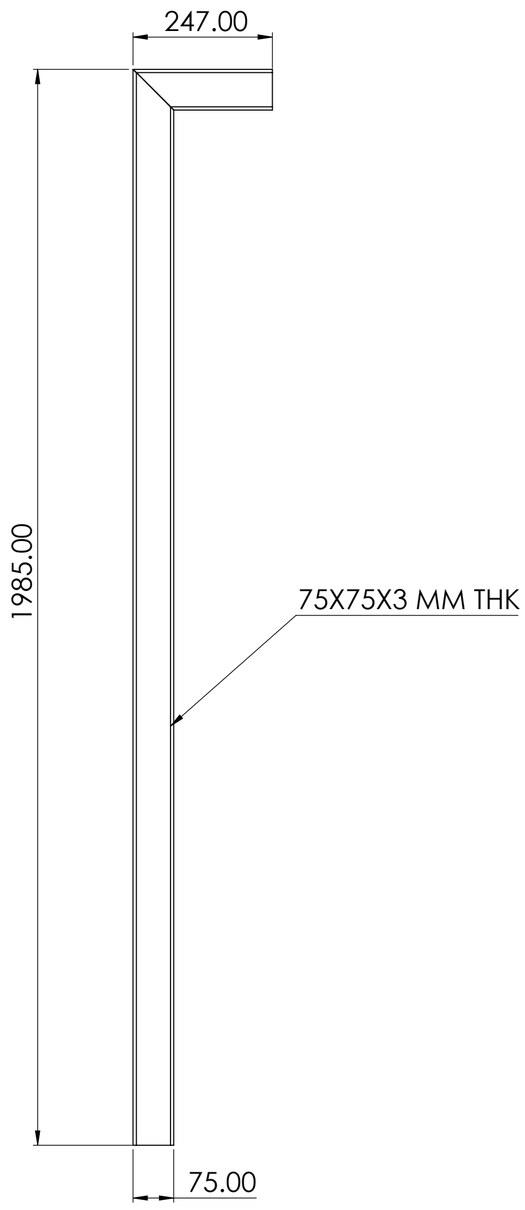

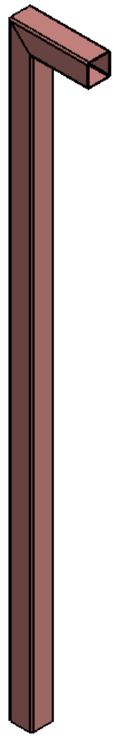

SIDE POST TUBE

NOTE :


SPECIAL INSTRUCTION'S :


TITLE - GATE AUTOMATION				NIHVA Technologies Pvt. Ltd.	NIHVA TECHNOLOGIES PVT.LTD.PUNE Website - www.nihva.com
DWG NO - NTPL-000-PM-001-00-00-00					
	NAME	SIGNATURE	DATE	PRODUCT - SLIDING FOLDING GATE	
DRAWN	V.G.		20-08-2025	PROJECT NO - NTPL-000-PM	REVISION - 00
CHK'D	B.S.		20-08-2025	SITE LOCATION -LUCKNOW	WEIGHT -
APPV'D	V.T.		20-08-2025	MATRIAL - MS	QTY - 1
If any queries contact - design@nihva.com				PROJECTION METHOD:	SCALE :
ALL DIMENSION ARE IN mm		A2			SHEET 19 OF 29


DRAWING


ITEM NO.	PART NUMBER	DESCRIPTION	QTY.
1	PLATE ASSEMBLY		2

REV DESCRIPTION	DATE	REV NO
	04-07-2025	REV 00
1. Xyz		

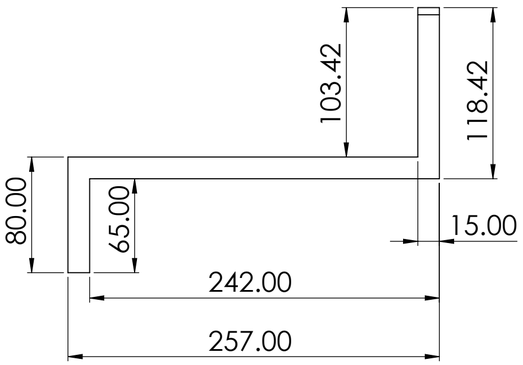

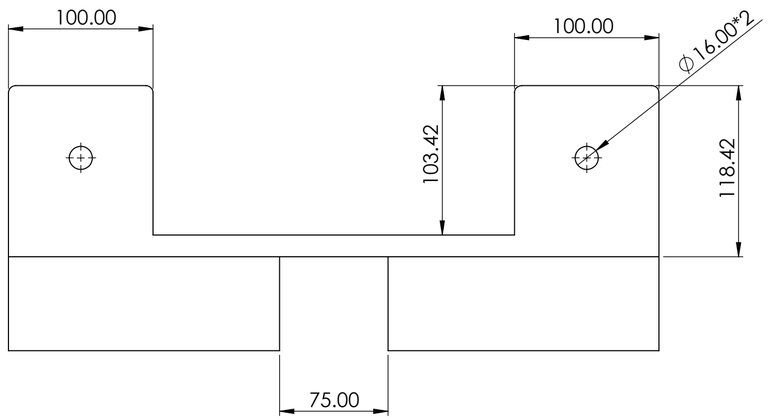

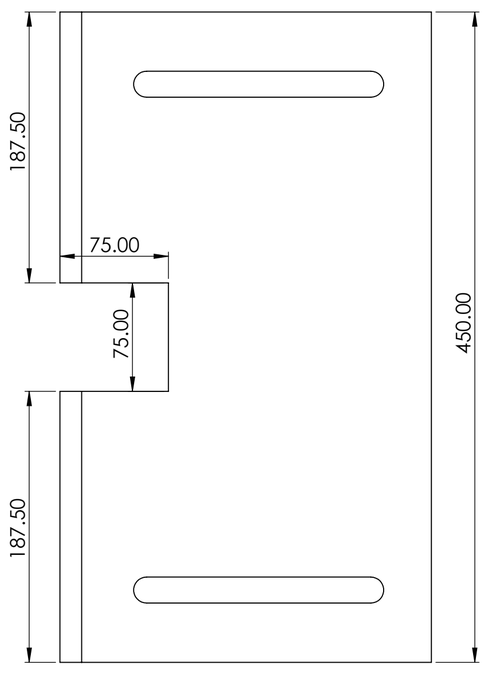

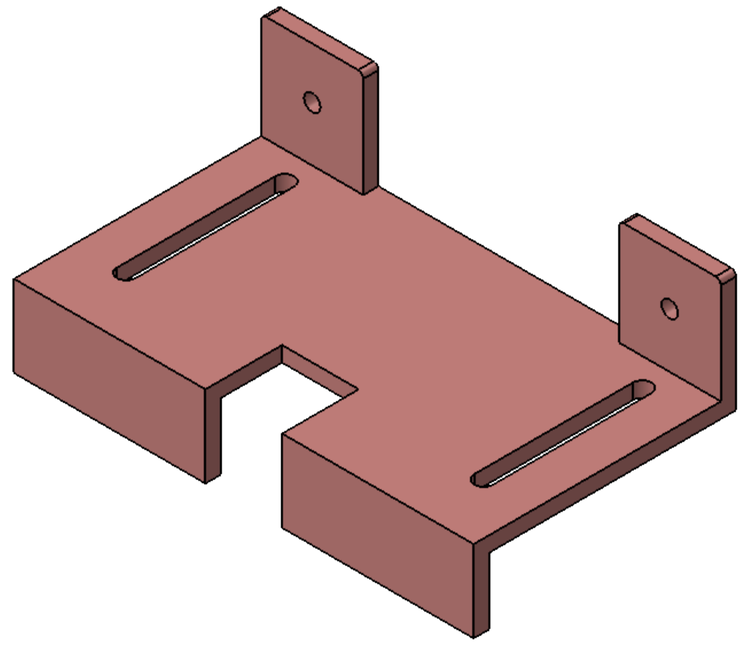

NOTE :

SPECIAL INSTRUCTION'S :

TITLE - GATE AUTOMATION

DWG NO - NTPL-000-PM-001-00-00-00


NIHVA Technologies Pvt. Ltd.


NIHVA TECHNOLOGIES PVT.LTD.PUNE
Website - www.nihva.com

	NAME	SIGNATURE	DATE		
DRAWN	V.G.		20-08-2025	PROJECT NO - NTPL-000-PM	REVISION - 00
CHK'D	B.S.		20-08-2025	SITE LOCATION -LUCKNOW	WEIGHT -
APPV'D	V.T.		20-08-2025	MATRIAL - MS	QTY - 1
If any queries contact - design@nihva.com				PROJECTION METHOD:	SCALE :
ALL DIMENSION ARE IN mm			A2		SHEET 20 OF 29

DRAWING

ITEM NO.	PART NUMBER	DESCRIPTION	QTY.
1	NYLON ROLLER PLATE	450X257X150MM	2

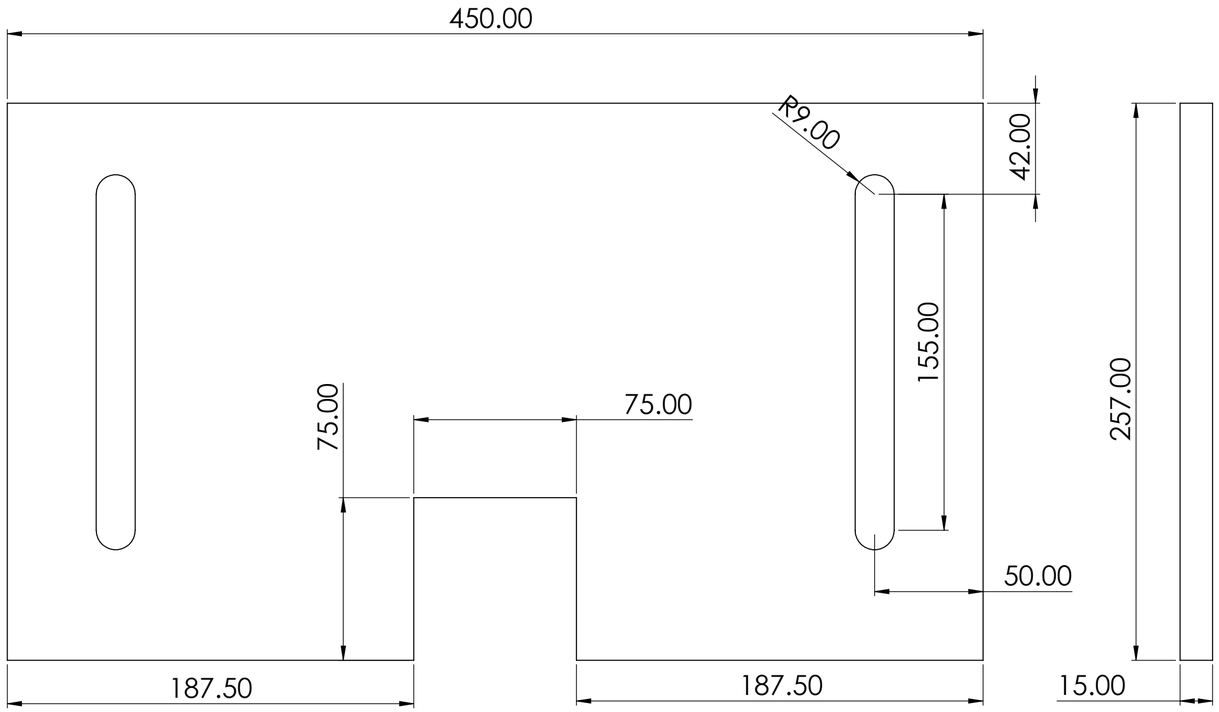

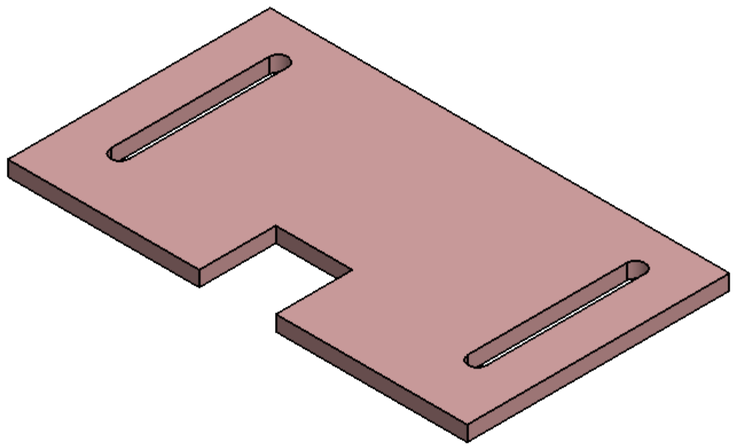

REV DESCRIPTION	DATE	REV NO
	04-07-2025	REV 00
1. Xyz		

NOTE :

SPECIAL INSTRUCTION'S :

TITLE - GATE AUTOMATION

DWG NO - NTPL-000-PM-001-00-00-00

NIHVA TECHNOLOGIES PVT.LTD.PUNE
Website - www.nihva.com

	NAME	SIGNATURE	DATE
DRAWN	V.G.		20-08-2025
CHK'D	B.S.		20-08-2025
APPV'D	V.T.		20-08-2025

PRODUCT - SLIDING FOLDING GATE

PROJECT NO - NTPL-000-PM | REVISION - 00

SITE LOCATION -LUCKNOW | WEIGHT -

MATRIAL - MS | QTY - 1

If any queries contact - design@nihva.com

ALL DIMENSION ARE IN mm | A2


PROJECTION METHOD:


SCALE :


DRAWING

ITEM NO.	PART NUMBER	DESCRIPTION	QTY.
1	TOP PLT	100X103.42X15 MM	4

REV DESCRIPTION	DATE	REV NO
	04-07-2025	REV 00
1. Xyz		

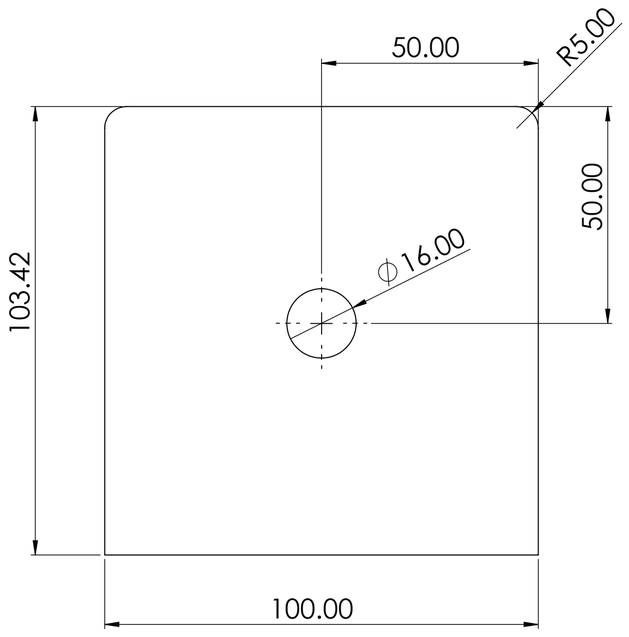

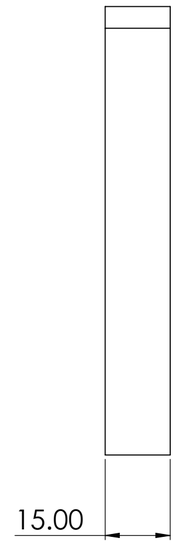

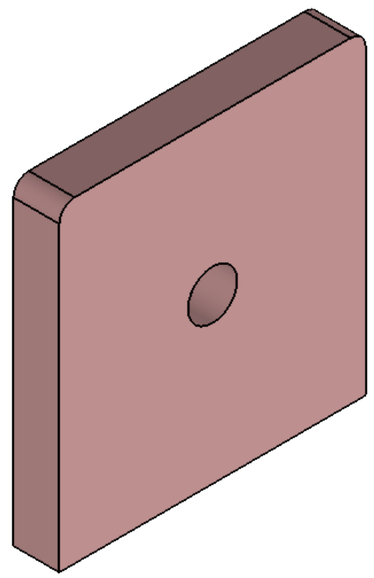

NOTE :

SPECIAL INSTRUCTION'S :

TITLE - GATE AUTOMATION

DWG NO - NTPL-000-PM-001-00-00-00

NIHVA Technologies Pvt. Ltd.

NIHVA TECHNOLOGIES PVT.LTD.PUNE
Website - www.nihva.com

	NAME	SIGNATURE	DATE	PRODUCT - SLIDING FOLDING GATE	
DRAWN	V.G.		20-08-2025	PROJECT NO - NTPL-000-PM	REVISION - 00
CHK'D	B.S.		20-08-2025	SITE LOCATION -LUCKNOW	WEIGHT -
APPV'D	V.T.		20-08-2025	MATRIAL - MS	QTY - 1

If any queries contact - design@nihva.com

ALL DIMENSION ARE IN mm | A2

PROJECTION METHOD:


SCALE :


DRAWING

REV DESCRIPTION	DATE	REV NO
	04-07-2025	REV 00
1. Xyz		

ITEM NO.	PART NUMBER	DESCRIPTION	QTY.
1	BOTTOM PLT	187.5X65X15 MM	1



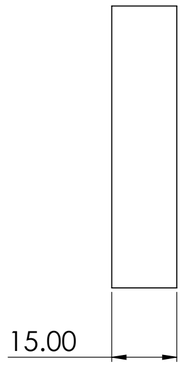

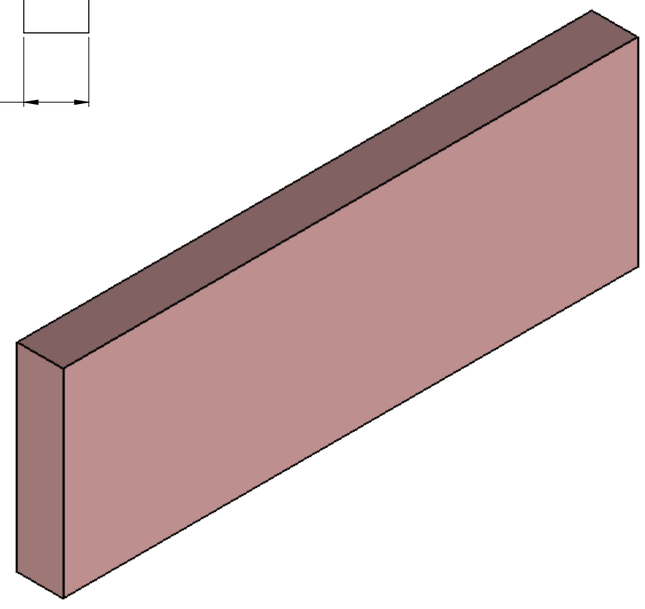

NOTE :

SPECIAL INSTRUCTION'S :

TITLE - GATE AUTOMATION

DWG NO - NTPL-000-PM-001-00-00-00

NIHVA Technologies Pvt. Ltd.

NIHVA TECHNOLOGIES PVT.LTD.PUNE
Website - www.nihva.com

	NAME	SIGNATURE	DATE		
DRAWN	V.G.		20-08-2025	PRODUCT - SLIDING FOLDING GATE	
CHK'D	B.S.		20-08-2025	PROJECT NO - NTPL-000-PM	REVISION - 00
APPV'D	V.T.		20-08-2025	SITE LOCATION -LUCKNOW	WEIGHT -
				MATRIAL - MS	QTY - 1

If any queries contact - design@nihva.com

ALL DIMENSION ARE IN mm | A2


PROJECTION METHOD:


SCALE :


DRAWING

REV DESCRIPTION	DATE	REV NO
	04-07-2025	REV 00
1. Xyz		

ITEM NO.	PART NUMBER	DESCRIPTION	QTY.
1	POST - 6.3MTR		1

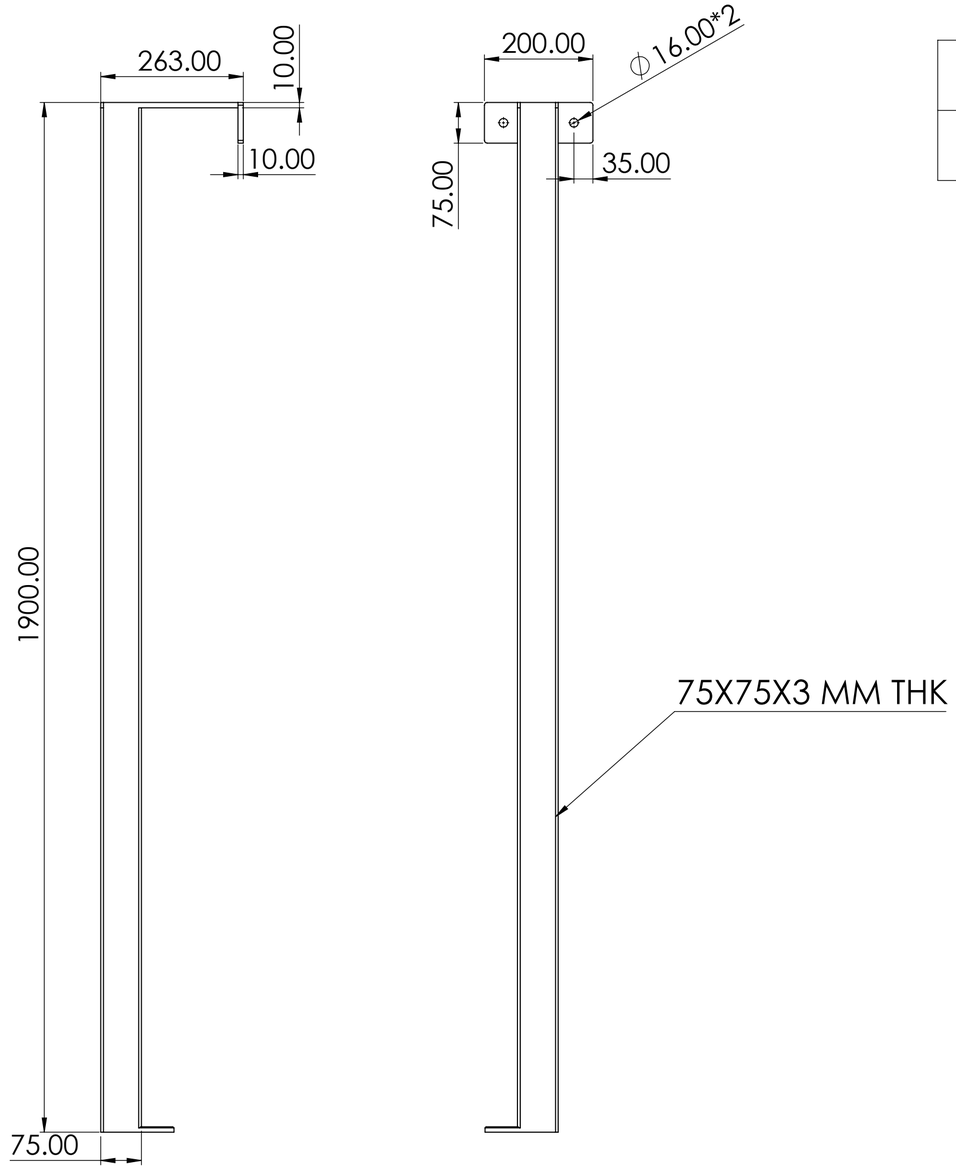

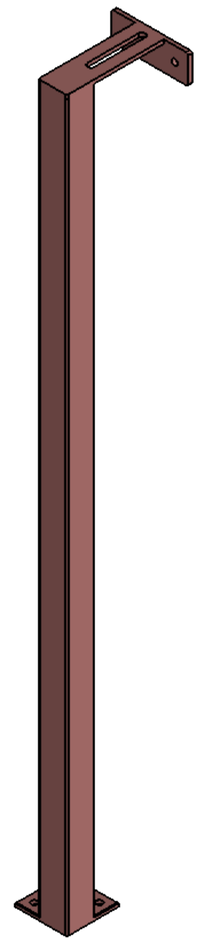

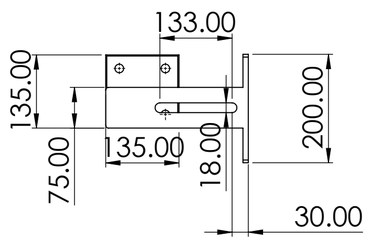

NOTE :

SPECIAL INSTRUCTION'S :

TITLE - GATE AUTOMATION

DWG NO - NTPL-000-PM-001-00-00-00

NIHVA Technologies Pvt. Ltd.


NIHVA TECHNOLOGIES PVT.LTD.PUNE
Website - www.nihva.com


	NAME	SIGNATURE	DATE	PRODUCT - SLIDING FOLDING GATE	
DRAWN	V.G.		20-08-2025	PROJECT NO - NTPL-000-PM	REVISION - 00
CHK'D	B.S.		20-08-2025	SITE LOCATION -LUCKNOW	WEIGHT -
APPV'D	V.T.		20-08-2025	MATRIAL - MS	QTY - 1
If any queries contact - design@nihva.com				PROJECTION METHOD:	SCALE :
ALL DIMENSION ARE IN mm		A2			SHEET 24 OF 29

DRAWING

REV DESCRIPTION	DATE	REV NO
	04-07-2025	REV 00
1. Xyz		

ITEM NO.	PART NUMBER	DESCRIPTION	QTY.
1	POST - 6.3MTR TUBE	75X75X3 MM	1

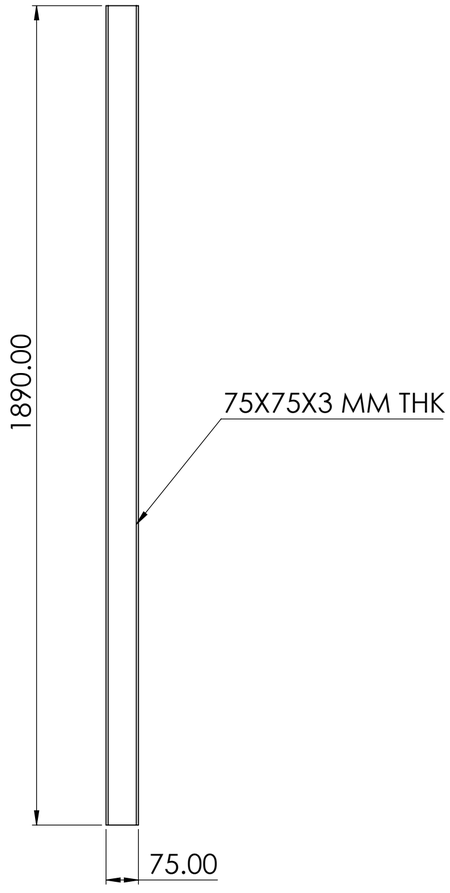

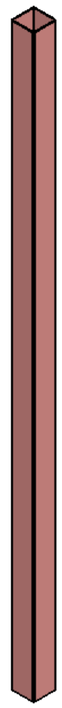

NOTE :

SPECIAL INSTRUCTION'S :

TITLE - GATE AUTOMATION

DWG NO - NTPL-000-PM-001-00-00-00

NIHVA Technologies Pvt. Ltd.

NIHVA TECHNOLOGIES PVT.LTD.PUNE
Website - www.nihva.com

	NAME	SIGNATURE	DATE
DRAWN	V.G.		20-08-2025
CHK'D	B.S.		20-08-2025
APPV'D	V.T.		20-08-2025

PRODUCT - SLIDING FOLDING GATE

PROJECT NO - NTPL-000-PM | REVISION - 00

SITE LOCATION -LUCKNOW | WEIGHT -

MATRIAL - MS | QTY - 1

If any queries contact - design@nihva.com

ALL DIMENSION ARE IN mm | A2


PROJECTION METHOD:


SCALE :

DRAWING

ITEM NO.	PART NUMBER	DESCRIPTION	QTY.
1	POST - 6.3MTR BOTTOM PLATE	132X132X10 MM THK	1

REV DESCRIPTION	DATE	REV NO
	04-07-2025	REV 00
1. Xyz		

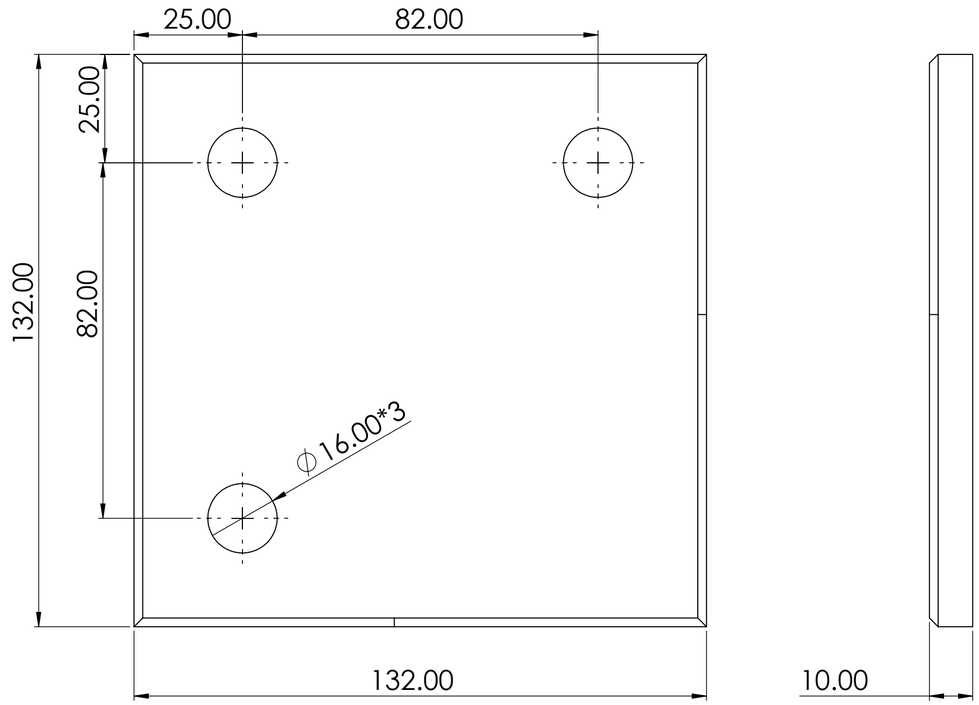

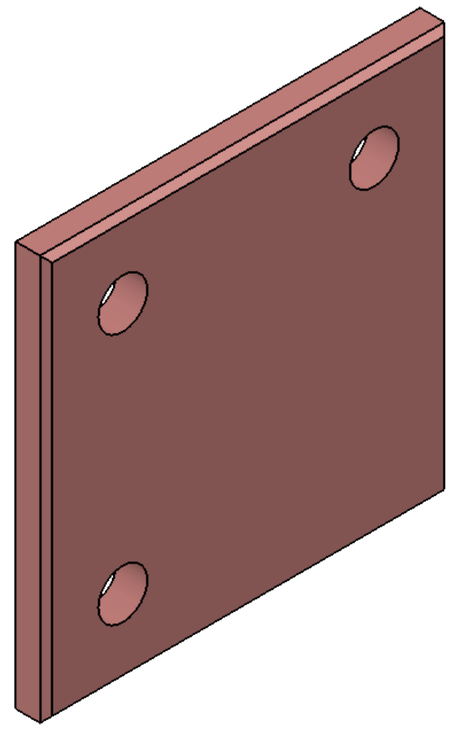

NOTE :

SPECIAL INSTRUCTION'S :

TITLE - GATE AUTOMATION

DWG NO - NTPL-000-PM-001-00-00-00

NIHVA Technologies Pvt. Ltd.

NIHVA TECHNOLOGIES PVT.LTD.PUNE
Website - www.nihva.com

	NAME	SIGNATURE	DATE
DRAWN	V.G.		20-08-2025
CHK'D	B.S.		20-08-2025
APPV'D	V.T.		20-08-2025

PRODUCT - SLIDING FOLDING GATE

PROJECT NO - NTPL-000-PM | REVISION - 00

SITE LOCATION -LUCKNOW | WEIGHT -

MATRIAL - MS | QTY - 1

If any queries contact - design@nihva.com


ALL DIMENSION ARE IN mm | A2


PROJECTION METHOD:

SCALE :

DRAWING

ITEM NO.	PART NUMBER	DESCRIPTION	QTY.
1	TOP PLATE SINGLE POST	263X75X10 MM THK	1

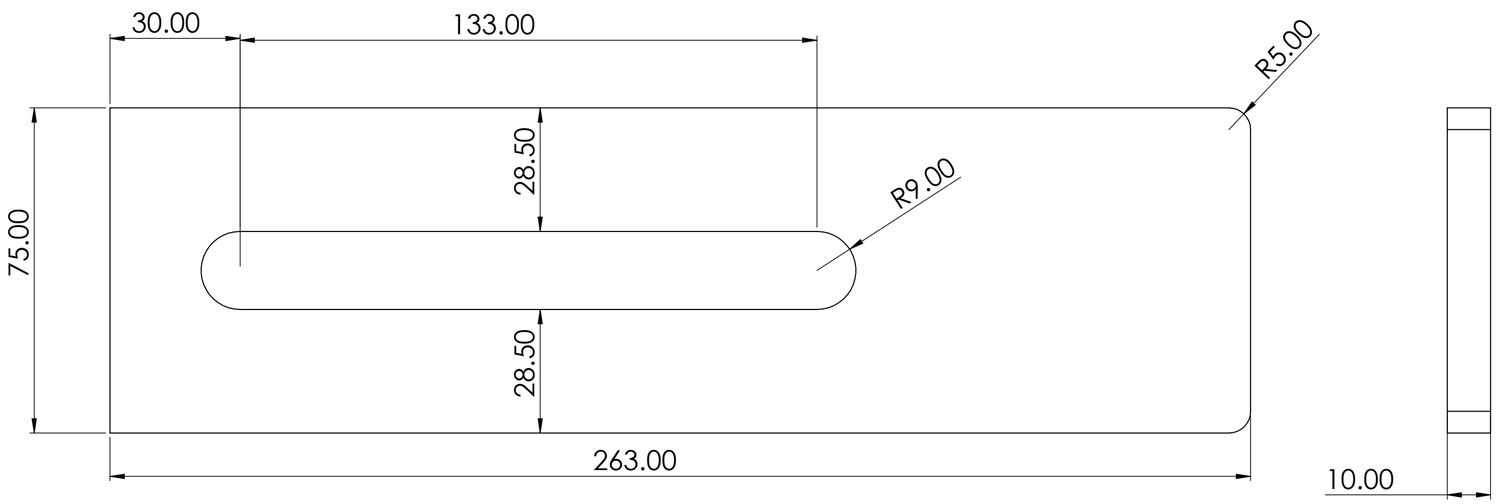

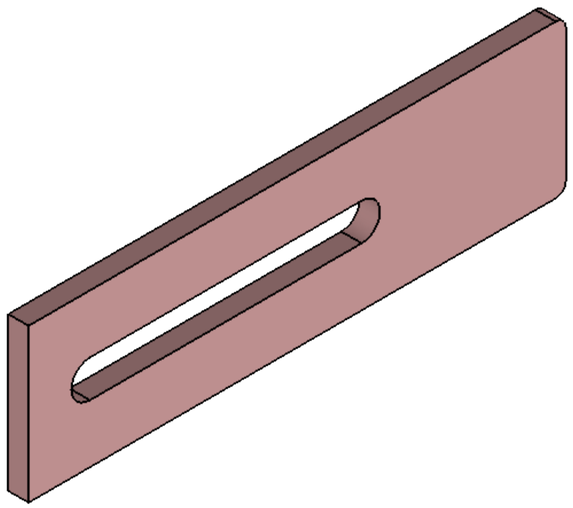

REV DESCRIPTION	DATE	REV NO
	04-07-2025	REV 00
1. Xyz		

NOTE :

SPECIAL INSTRUCTION'S :

TITLE - GATE AUTOMATION

DWG NO - NTPL-000-PM-001-00-00-00

NIHVA TECHNOLOGIES PVT.LTD.PUNE
Website - www.nihva.com

	NAME	SIGNATURE	DATE		
DRAWN	V.G.		20-08-2025	PROJECT NO - NTPL-000-PM	REVISION - 00
CHK'D	B.S.		20-08-2025	SITE LOCATION -LUCKNOW	WEIGHT -
APPV'D	V.T.		20-08-2025	MATRIAL - MS	QTY - 1

PRODUCT - SLIDING FOLDING GATE

If any queries contact - design@nihva.com


ALL DIMENSION ARE IN mm | A2


PROJECTION METHOD:


SCALE :

DRAWING

ITEM NO.	PART NUMBER	DESCRIPTION	QTY.
1	POST - 6.3MTR WALL MOUNTED PLATE	200X75X10 MM THK	1

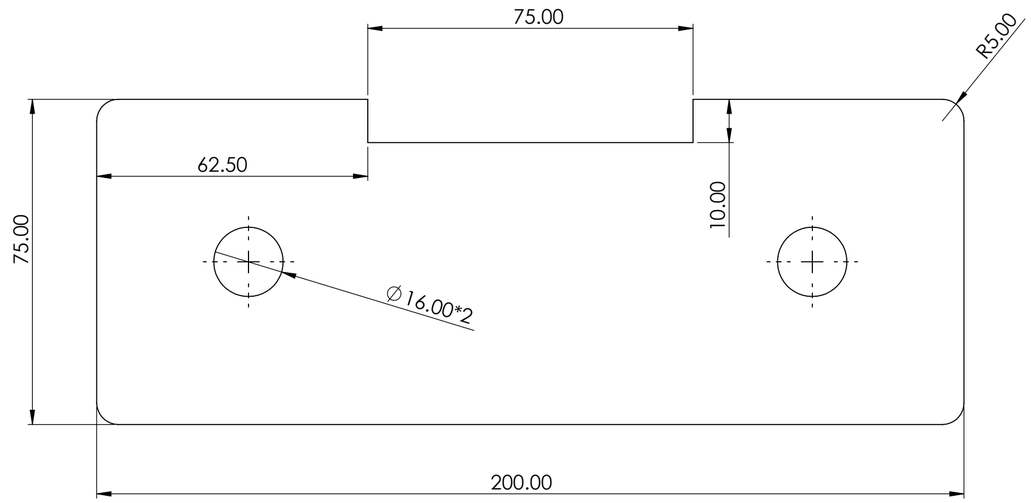

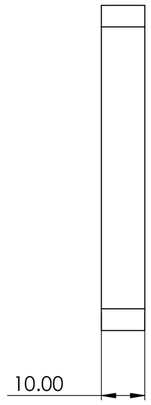

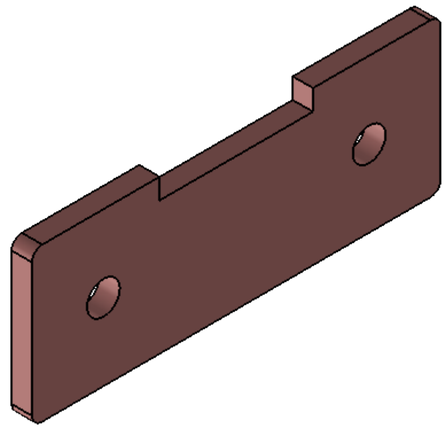

REV DESCRIPTION	DATE	REV NO
	04-07-2025	REV 00
1. Xyz		

NOTE :

SPECIAL INSTRUCTION'S :

TITLE - GATE AUTOMATION

DWG NO - NTPL-000-PM-001-00-00-00

NIHVA TECHNOLOGIES PVT.LTD.PUNE
Website - www.nihva.com

	NAME	SIGNATURE	DATE
DRAWN	V.G.		20-08-2025
CHK'D	B.S.		20-08-2025
APPV'D	V.T.		20-08-2025

PRODUCT - SLIDING FOLDING GATE

PROJECT NO - NTPL-000-PM | REVISION - 00

SITE LOCATION -LUCKNOW | WEIGHT -

MATRIAL - MS | QTY - 1

If any queries contact - design@nihva.com

ALL DIMENSION ARE IN mm | A2


PROJECTION METHOD:


SCALE :


DRAWING

ITEM NO.	PART NUMBER	DESCRIPTION	QTY.
1	AWheel.		6

REV DESCRIPTION	DATE	REV NO
	04-07-2025	REV 00
1. Xyz		

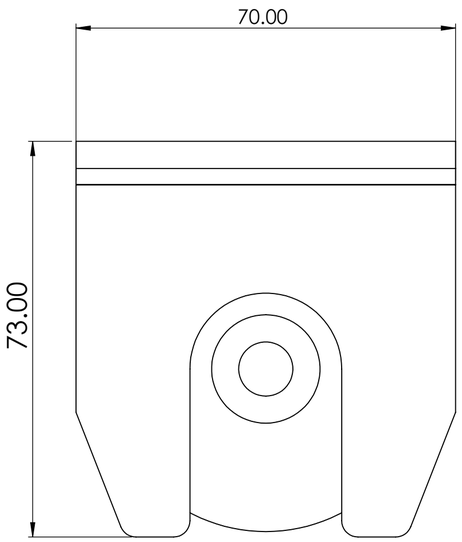

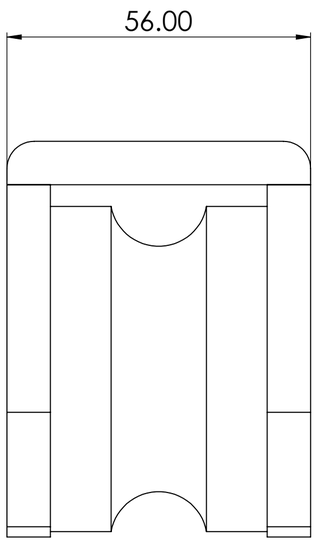

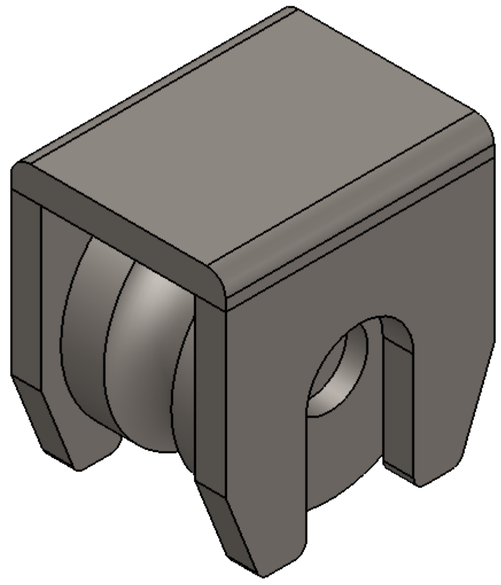

NOTE :

SPECIAL INSTRUCTION'S :

TITLE - GATE AUTOMATION

DWG NO - NTPL-000-PM-001-00-00-00

NIHVA Technologies Pvt. Ltd.

NIHVA TECHNOLOGIES PVT.LTD.PUNE
Website - www.nihva.com

	NAME	SIGNATURE	DATE	PRODUCT - SLIDING FOLDING GATE	
DRAWN	V.G.		20-08-2025	PROJECT NO - NTPL-000-PM	REVISION - 00
CHK'D	B.S.		20-08-2025	SITE LOCATION -LUCKNOW	WEIGHT -
APPV'D	V.T.		20-08-2025	MATRIAL - MS	QTY - 1

If any queries contact - design@nihva.com

ALL DIMENSION ARE IN mm | A2

PROJECTION METHOD:

SCALE :

SHEET 29 OF 29