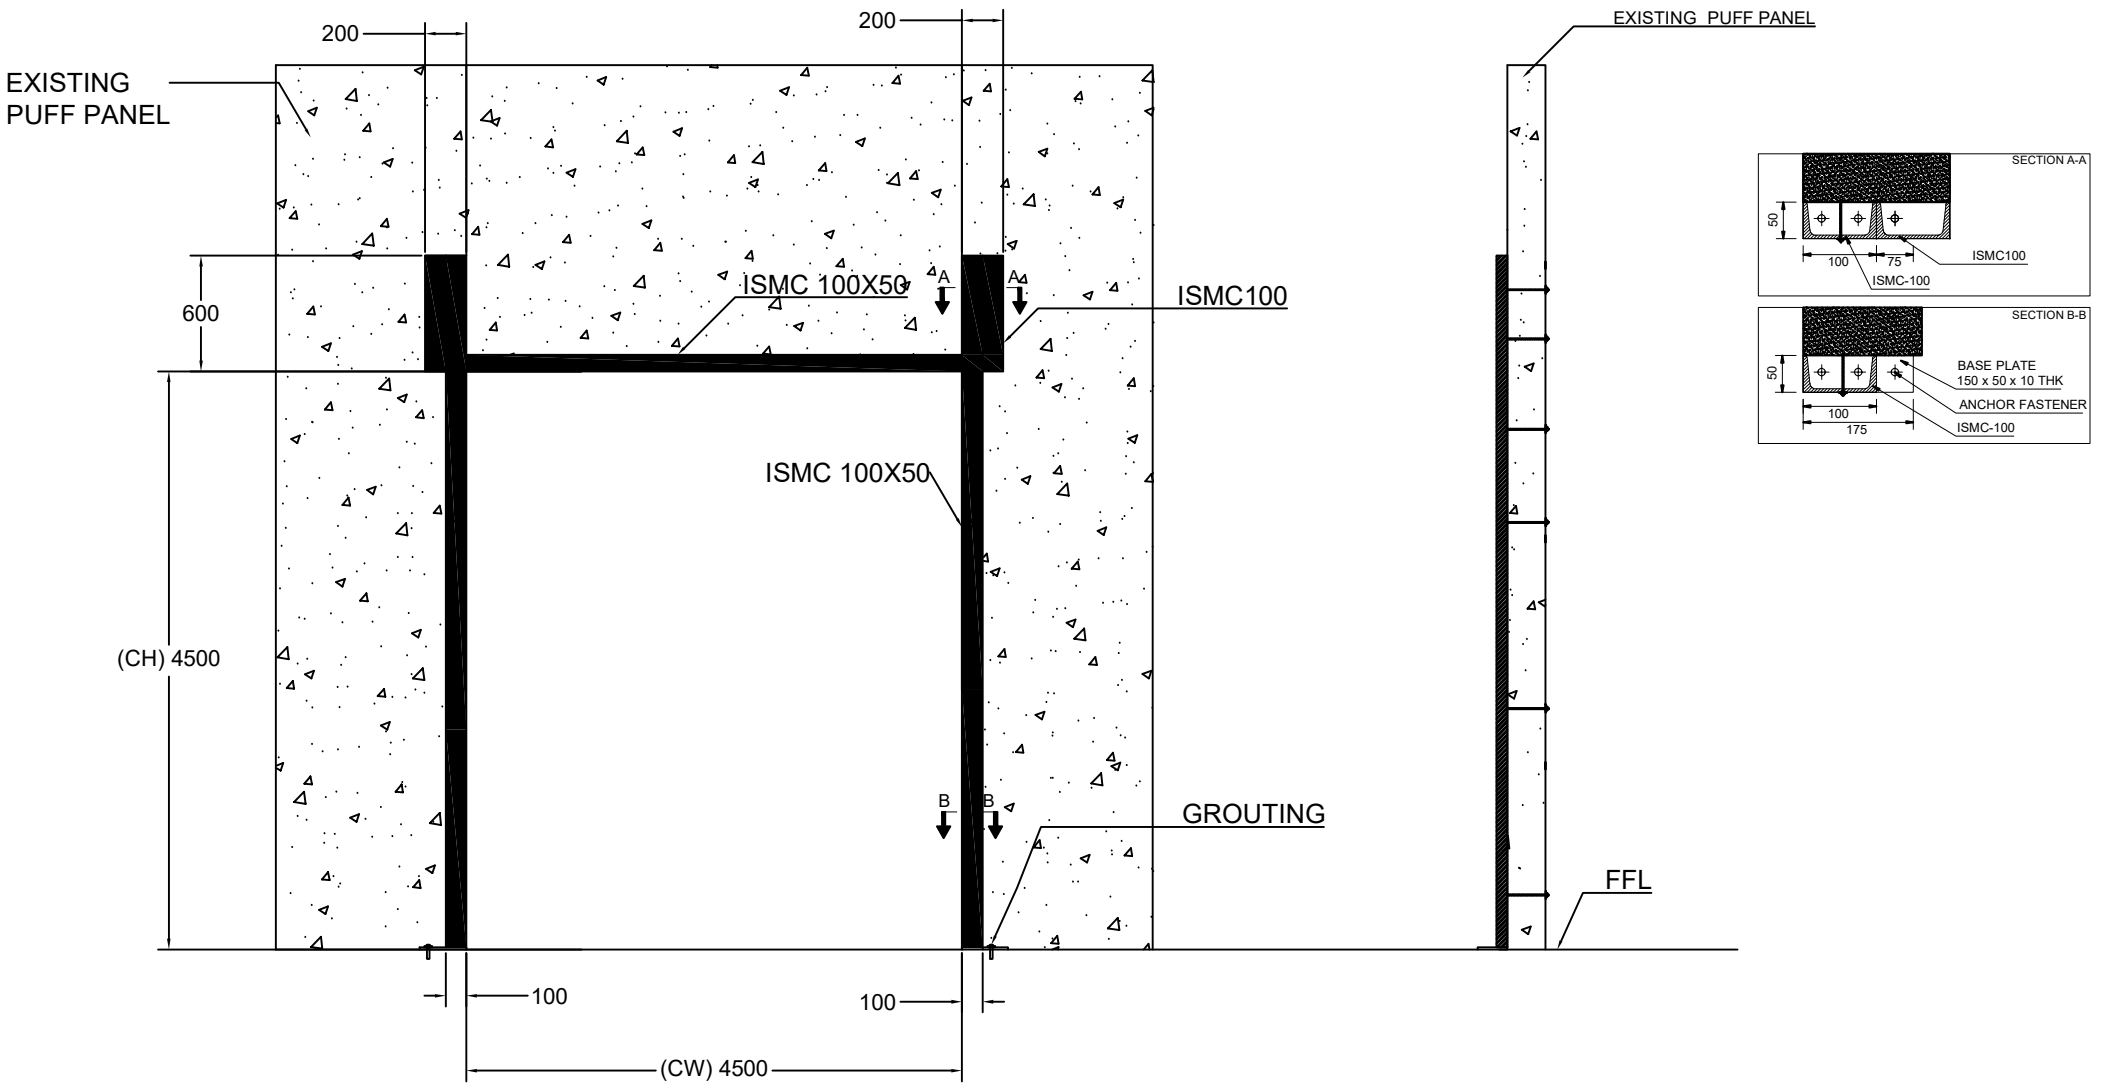



M.S. STRUCTURE DETAILS

SR.	CLEAR WIDTH	CLEAR HEIGHT	QTY.
01	4500	4500	07


This drawing & design is the property of NIHVA TECHNOLOGIES. Not to be sold or copied to any other concern.

TITLE	ROLLING SHUTTER ST.			
	NAME	SIGN	DATE	
DRAWN	J.S		19.01.2024	CLIENT - RINAC
CHECK	A.K		19.01.2024	PROJECT - ROLLING SHUTTER ST.
APPRD.	V.T		19.01.2024	FORMAT NO - NIHVA-DD-F-03
If any queries contact : projectsupport@nihva.com				DWG. NO. : NIHVA/23-24/106 / REV- R00
ALL DIMENSION ARE IN mm				SCALE: NTS / WT: / SHEET:


NIHVA TECHNOLOGIES PVT. LTD. PUNE
Tel : 020 66304033
Email:- info@nihva.com
Website:- www.nihva.com

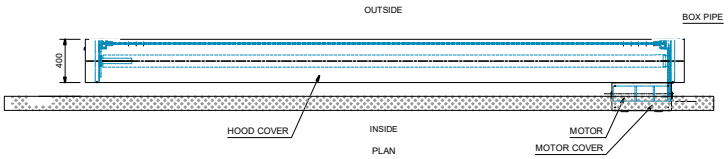


PLAN

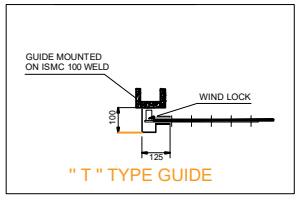

" T " TYPE GUIDE

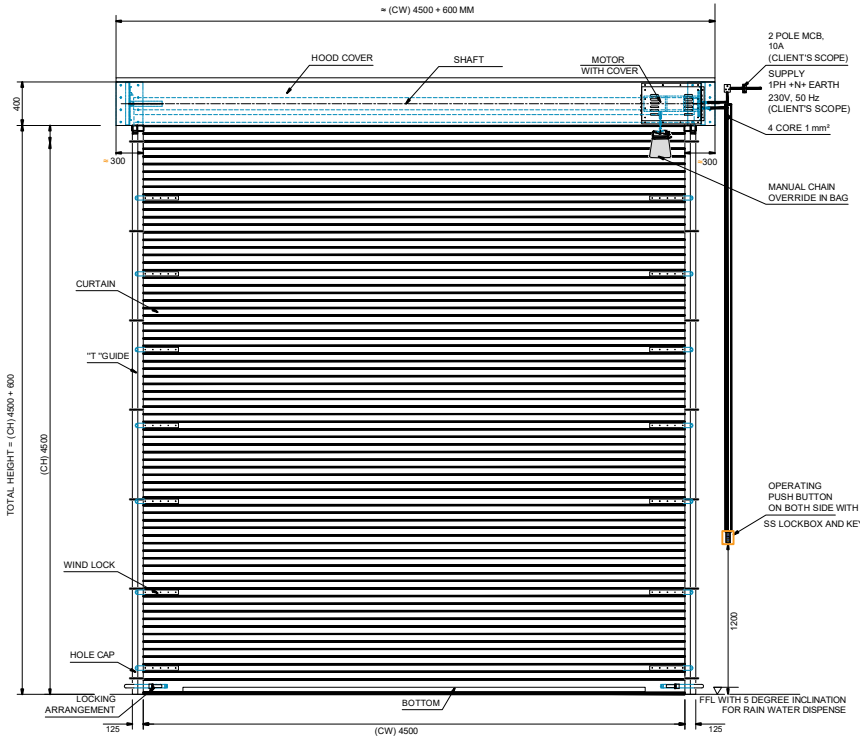

INSIDE ELEVATION

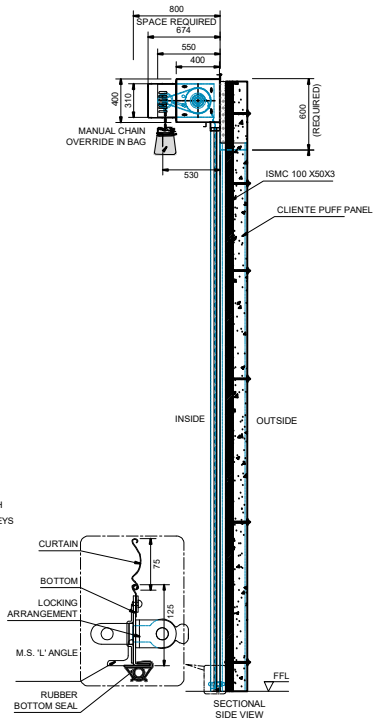

SECTIONAL
SIDE VIEW

TECHNICAL SPECIFICATION:-

SR.	SPECIFICATION	DETAILS
1.	Description & Drive	Motorised Rolling Shutter (Indirect Drive) with Manual Chain Arrangment
2.	Location Area	Inside / Outside
3.	Mounting Surface	Side Brackets: Optional / Structure
4.	Slat	Curved 75 mm PPGI Sheet - 1.0 mm Thk. & Windlock Considered
5.	Bottom Profile	MS Plate 125 x 2.5 mm thick with Angle Stiffner
6.	Guide Profile	M.S." T " Shape profile 125 x 3.15 mm Thk.
7.	Hood Cover & Motor Cover	Made of GI Sheet Thickness 0.9 mm
8.	Accessories	Push Button On Both Side

SHUTTER SIZES :-

SR.	CLEAR WIDTH	CLEAR HEIGHT	QTY.
01	4500	4500	07

This drawing & designing is the property of NIHVA TECHNOLOGIES. Not to be sold or copied to any other concern

TITLE :-
MOTORISED ROLLING
SHUTTER

NIHVA TECHNOLOGIES
PVT. LTD. PUNE
Tel : 020 66304033
Email:- info@nihva.com
Website:- www.nihva.com

	NAME	DATE
DRAWN	J.S.	19/01/2024
CHECK	A.K.	19/01/2024
APPROVAL	V.T.	19/01/2024

CLIENT - RINAC
PROJECT -ROLLING SHUTTER
FORMAT NO - NIHVA-DD-F-03
DWG. NO. : NIHVA/23-24/105 REV-01
SCALE: NTS WT: SHEET: 01 OF 01
ALL DIMENSION ARE IN mm
If any queries contact : design@nihva.com